
SKETCH

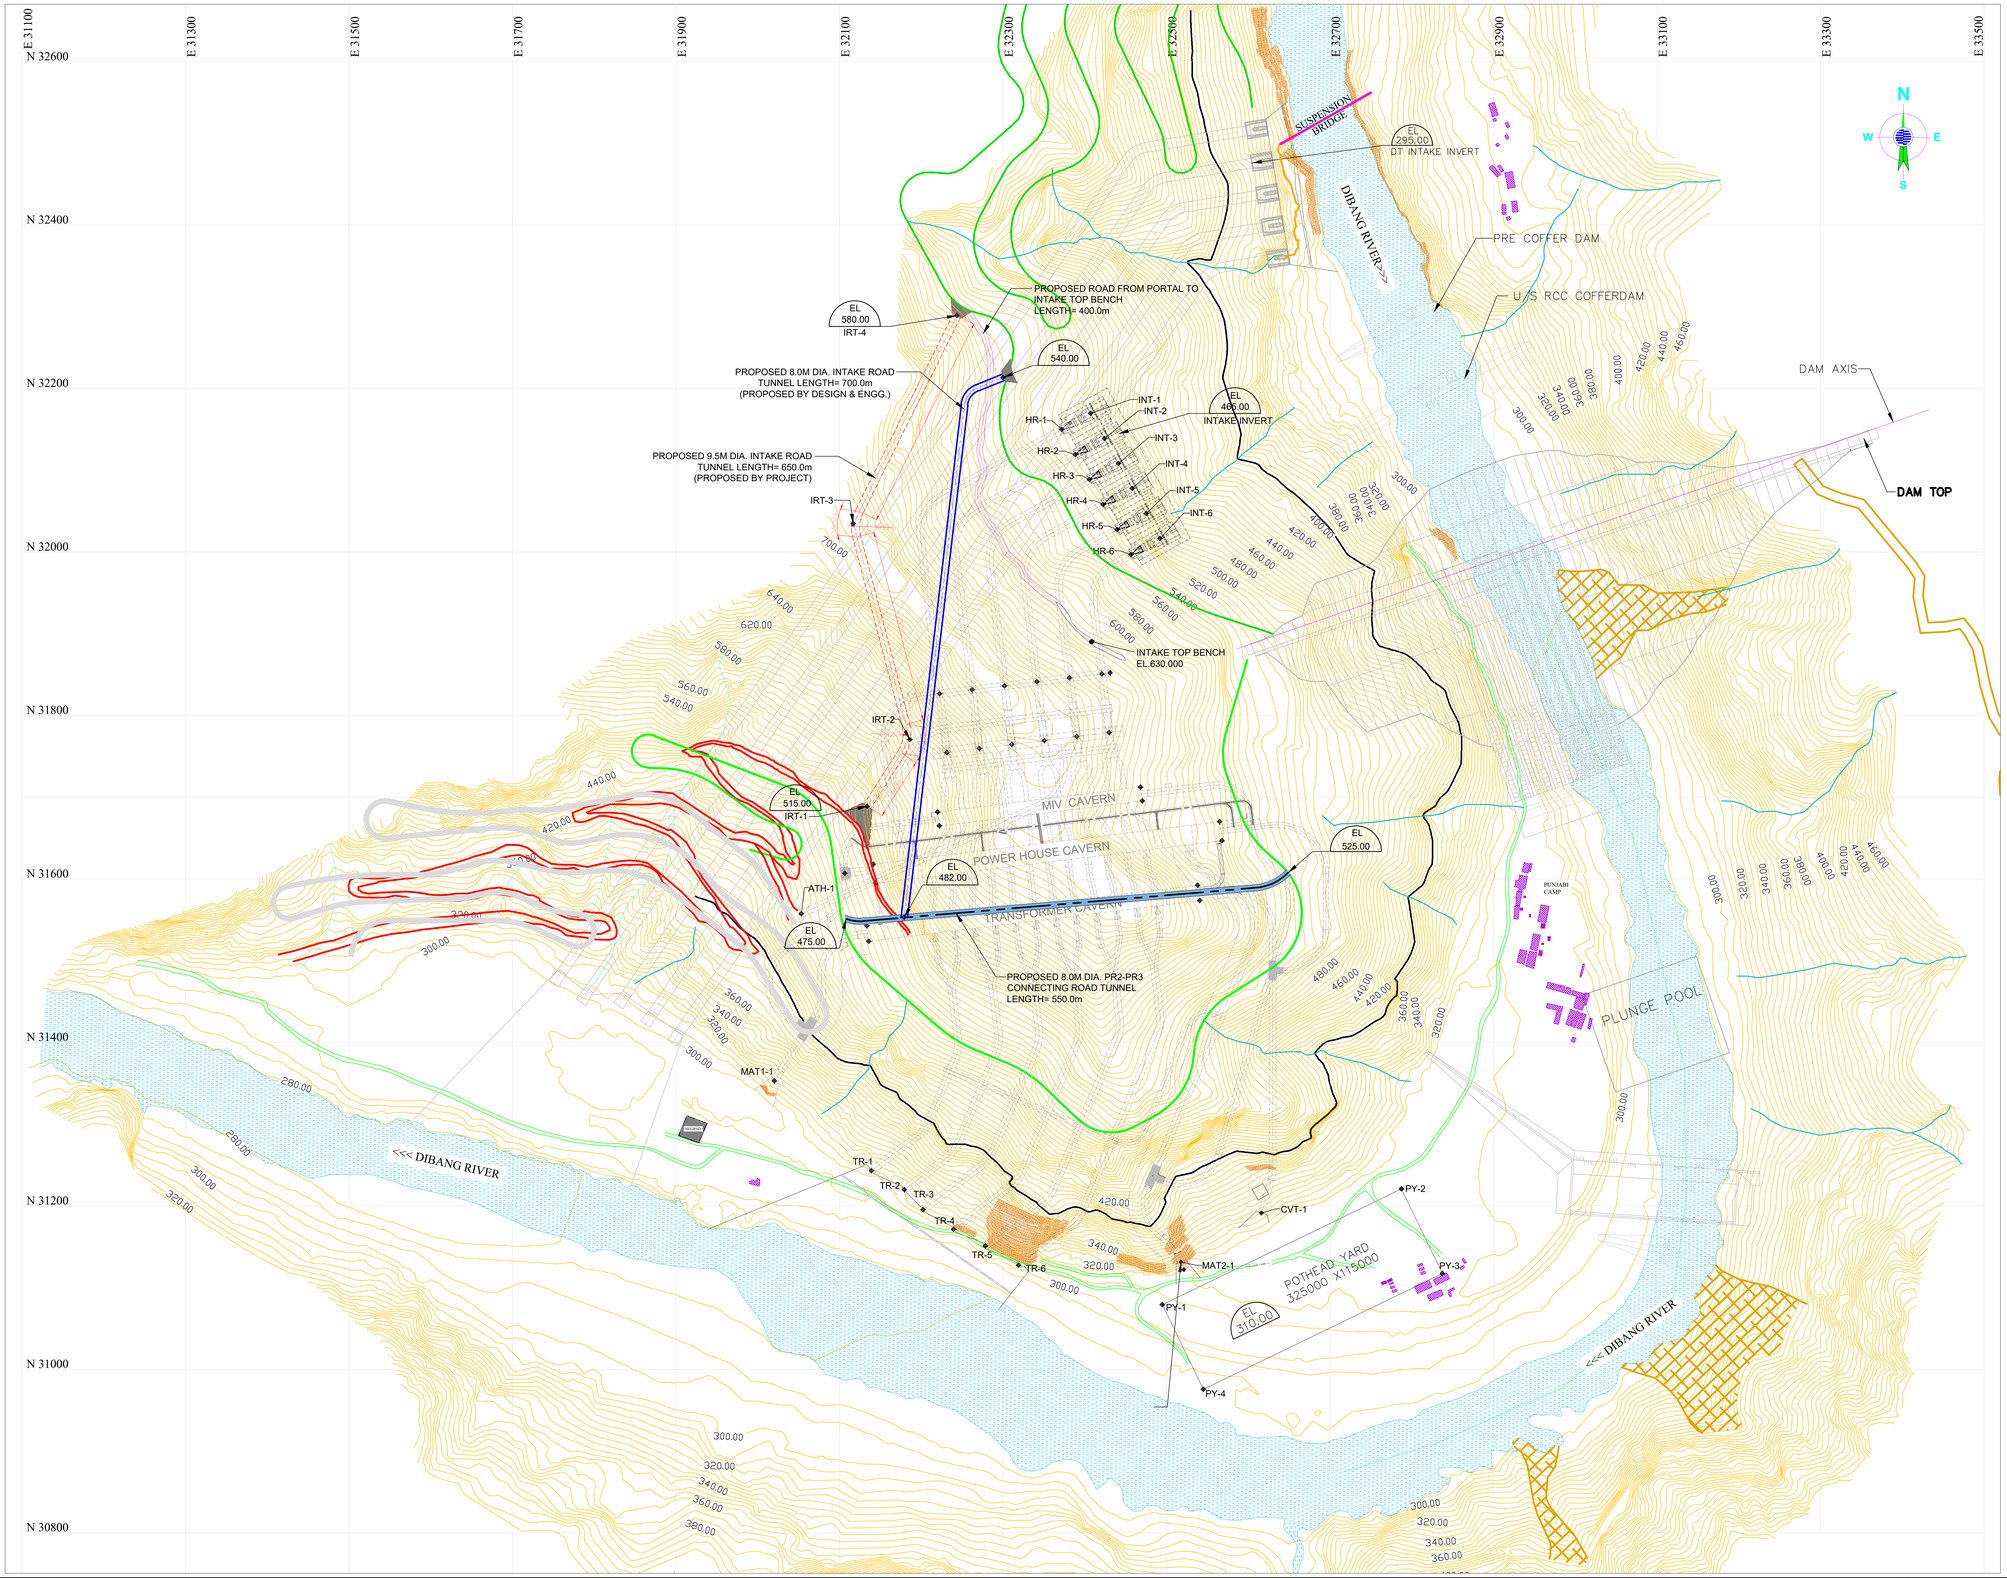

NOTES:

1. ALL DIMENSIONS ARE IN MILLIMETRE, ELEVATIONS & CHAINAGE AND LEVELS ARE IN METER.

LEGEND:

UNPAVED ROAD	
SHED	
RIVER	
HFL LINE	
STREAMS	
PILLARS	GR
MAJOR CONTOURS	
CONTOUR RL	300
ROCK	
SLIDING AREA	
SUSPENSION BRIDGE	

NOTES TO SCLAE:

एनएचपीसी NHPC A Navratna Company

NHPC Limited
(A GOVT. OF INDIA NAVRATNA ENTERPRISE)

DIBANG MULTIPURPOSE PROJECT

PLAN OF PROPOSED ROAD TUNNEL ALIGNMENT (ON RIGHT BANK)