

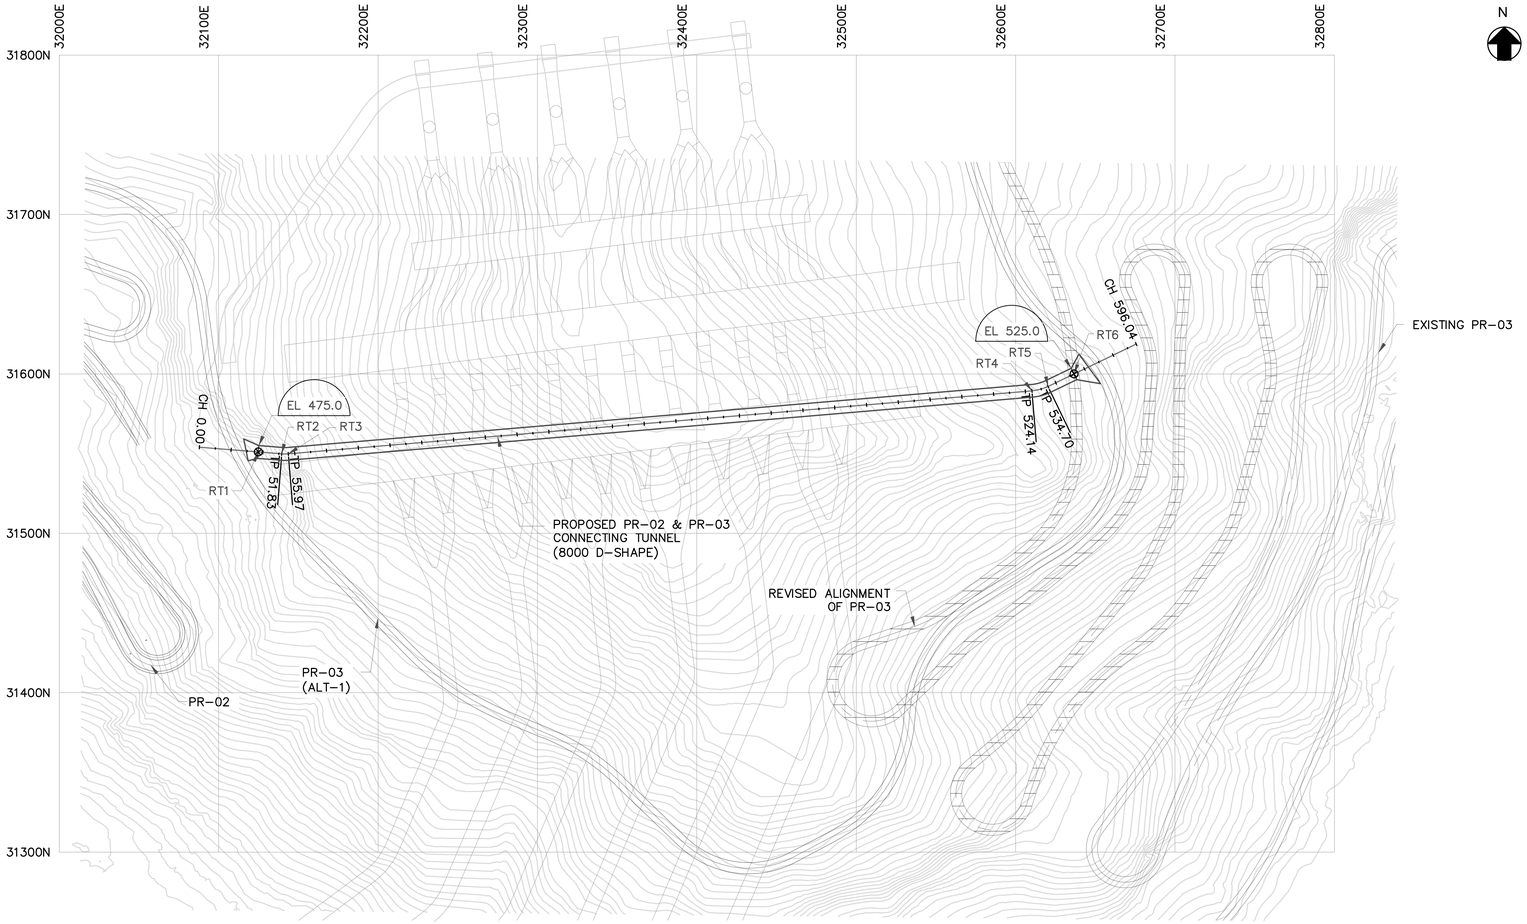



PLAN

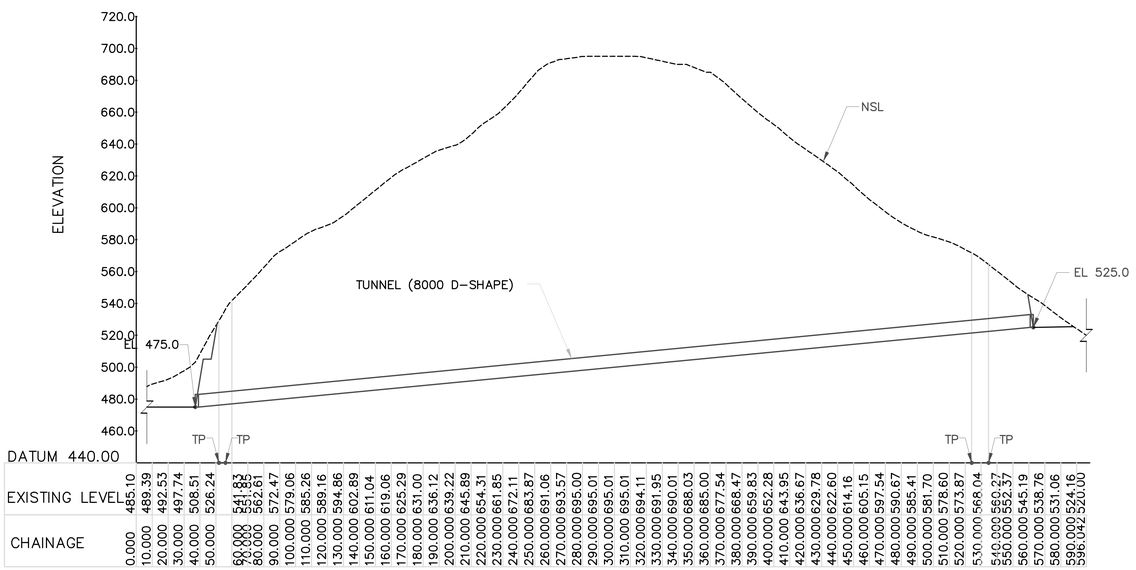

LONGITUDINAL SECTION

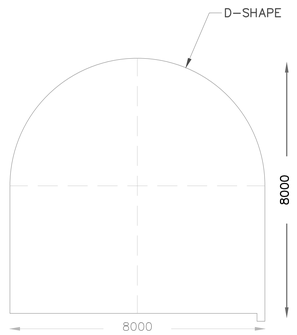

TYPICAL SECTION

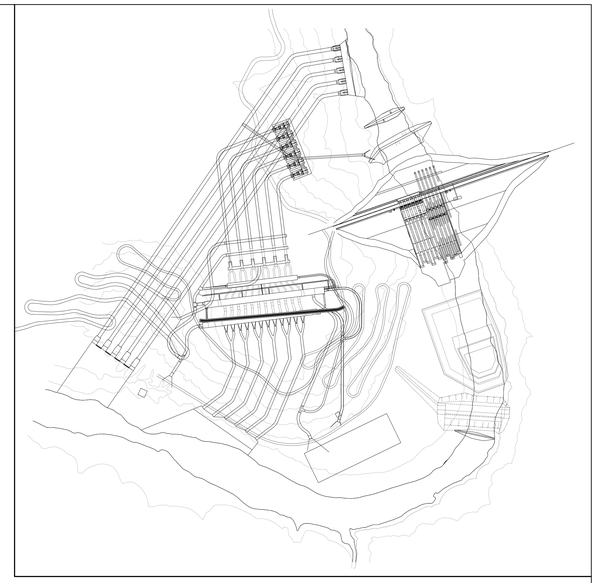

KEY PLAN

NOTES

1 दर्शाए गए ग्रिड तथा ऊँचाई मीटर में दर्शि गए हैं।
GRID AND ELEVATIONS SHOWN ARE IN METRE.

2 CONTOURS SHOWN IN THE DRAWING ARE AS PER THE RECENT TOPOGRAPHICAL SURVEY

3 THIS DRAWING SHOWS THE GENERAL ARRANGEMENT OF THE ROAD TUNNEL ONLY.

ROAD TUNNEL			
POINTS	NORTHING	EASTING	ELEVATION
RT1	31551.029	32124.840	475.00
RT6	31599.968	32636.612	525.00

SCALE:
0 25 50 75 100 125 METRE

एन एच पी सी लिमिटेड
(भारत सरकार का एक संघटन उद्यम)
NHPC Limited
(A GOVT. OF INDIA NAVRATNA ENTERPRISE)

दिबांग बहुउद्देशीय परियोजना
DIBANG MULTIPURPOSE PROJECT

PR-02 & PR-03 CONNECTING
ROAD TUNNEL
PLAN & SECTION

DATE	NO.	REVISION OR ISSUES	BY	CH.	APP.

DRAWN	SUBMITTED	RECOMMENDED		APPROVED
अंकित	प्रस्तुत	अनुशंसित		अनुमोदन

DESIGN MEMO NO. डिजाइन मेमो संख्या
DATE दिनांक
DRG. NO. ड्रॉइंग संख्या

DRG. NO.