


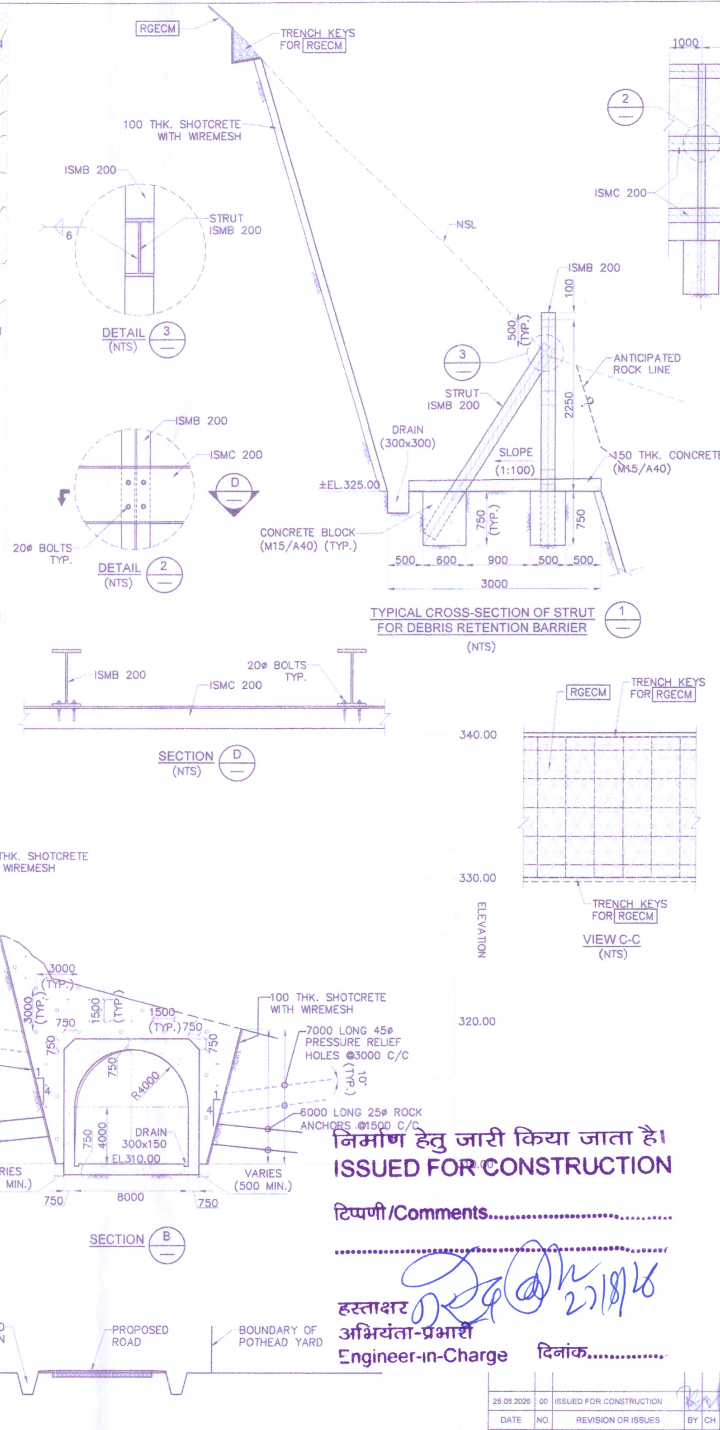

CO-ORDINATES			
SL. NO.	POINTS	NORTHING	EASTING
1	CVT1	31191.170N	32615.998E
2.	CVT2	31198.375N	32618.082E

- NOTES:-**
1. सोनी गांव सिमलियाई में फिफ्थ डायरेक्ट मैटैर में गंगा नदी है।
ALL DIMENSIONS ARE IN MILLIMETRE, GRIDS & ELEVATIONS ARE IN METRE.
 2. THIS DRAWING IS BASED ON SURVEY PROVIDED BY PROJECT VIDE IOM NO. NH/DIBANG/POWER/15/2016-CIVIL-2/14/32 DATED 15.04.2026 AND GEOLOGICAL APPRAISAL PROVIDED BY PROJECT VIDE IOM NO. NH/DIBANG/GEOLOGY/2026/60 DATED 30.05.2026.
 3. EXCAVATION SLOPE, IF REQUIRED, MAY BE MODIFIED TO SUIT THE SITE CONDITIONS WITH THE APPROVAL OF ENGINEER-IN-CHARGE.
 4. UNLESS SPECIFIED OTHERWISE, M15/A40 GRADE CONCRETE SHALL BE USED. THE CONCRETE SHALL CONFORM TO SECTION B-9 OF TECHNICAL SPECIFICATIONS.
 5. STEEL SECTIONS FOR POSTS AND STRUT SHALL CONFORM TO SECTION B-14 OF TECHNICAL SPECIFICATIONS.
 6. CUMMERBUCK FABRIC SHALL CONFORM TO SECTION B-4 OF TECHNICAL SPECIFICATIONS.
 7. THE MATERIAL FOR STEEL SECTIONS, BOLTS, NUTS AND WASHERS SHALL CONFORM TO IS 2062.
 8. ALL WELDING, WELDING ELECTRODES AND WORKSMANSHIP SHALL CONFORM TO IS 814 AND IS 816.
 9. REINFORCED 3D GEOSYNTHETIC EROSION CONTROL MAT SHALL CONFORM TO SECTION B.17 OF TECHNICAL SPECIFICATIONS. INSTALLATION SHALL BE IN ACCORDANCE WITH MANUFACTURERS INSTRUCTIONS.
 10. THE LAYOUT OF DEBRIS RETENTION BARRIER SHOWN IN DRAWING IS SCHEMATIC AND MAY BE MODIFIED AS PER SITE CONDITIONS AS DIRECTED BY ENGINEER-IN-CHARGE.
 11. THE DISTANCE BETWEEN THE TWO SECTIONS OF DEBRIS RETENTION BARRIER MAY BE MODIFIED AS PER SITE CONDITIONS WITH THE APPROVAL OF ENGINEER-IN-CHARGE.
 12. DISCHARGE CHANNEL IN DEPRESSION ZONE ABOVE PORTAL SHALL BE USING CATCH DRAIN.
 13. ADDITIONAL BACK SLOPE PROTECTION AS PER SITE ASSESSMENT AND REQUIREMENT AT HIGHER ELEVATION MAY BE INSTALLED.

LEGEND:

RGECM - REINFORCED 3D GEOSYNTHETIC
EROSION CONTROL MAT

REFERENCE DRAWING:

1. NHDB-4BC4-41-DD-1003

SCALE:



(1:250)

	एन एच पी सी लिमिटेड (एनएसएल का जुड़वा) NHPC Limited (A SOV. OF INDIA ENTERPRISE)
विद्युत बहुउद्देशीय परियोजना DIBANG MULTIPURPOSE PROJECT	
POWER HOUSE COMPLEX CABLE CUM VENTILATION TUNNEL PORTAL BACK SLOPE ADDITIONAL PROTECTION	

25.08.2026	00	ISSUED FOR CONSTRUCTION	BY	CH	APP	DAWN SUBMITTED VIRAJ KUMAR	RECOMMENDED प्रस्तावित किया गया JYOTSNA SAREY KUMAR	APPROVED अनुमोदित S. CHANDRAN
DATE	NO	REVISION OR ISSUES	BY	CH	APP	DATE AUG. 2026	DRG. NO. NHDB 4BC4	41 DD 1043 00
DESIGN MEMO NO. विशेषज्ञ के विवरण								