


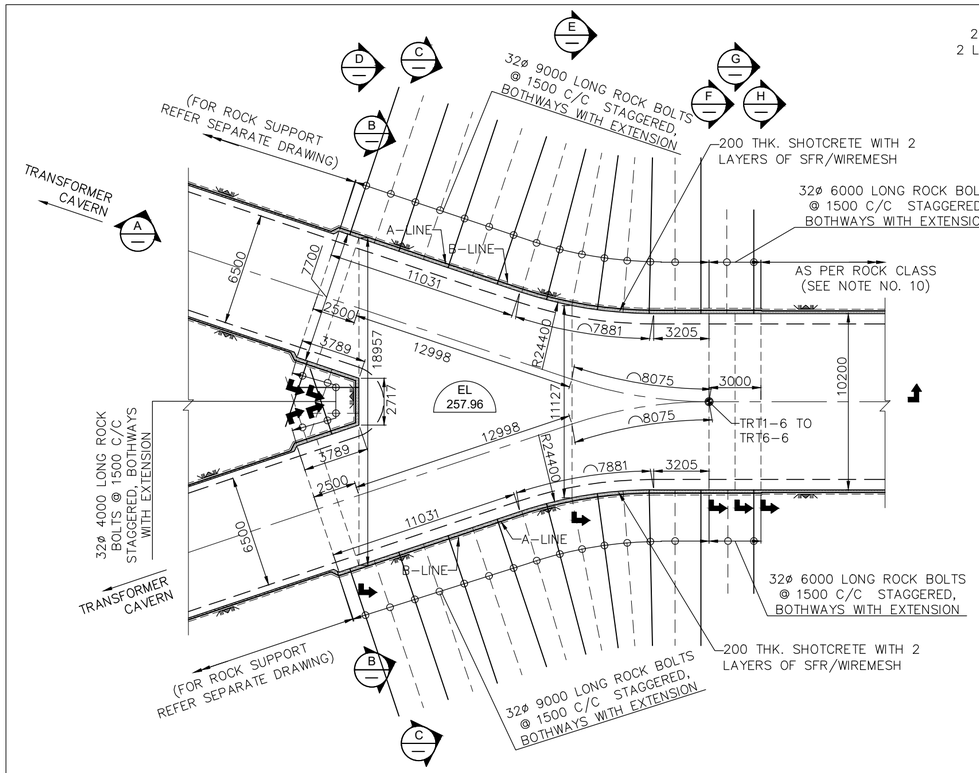



TYPICAL PLAN OF JUNCTION FOR BRANCH TAIL RACE TUNNEL - 1 TO 12

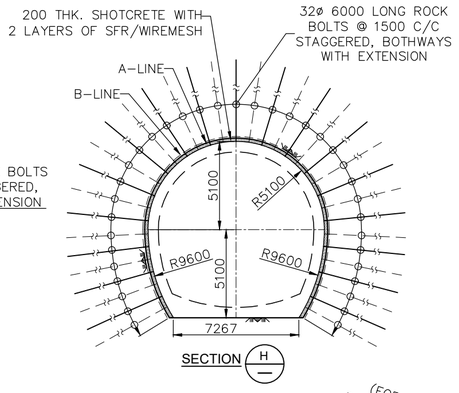

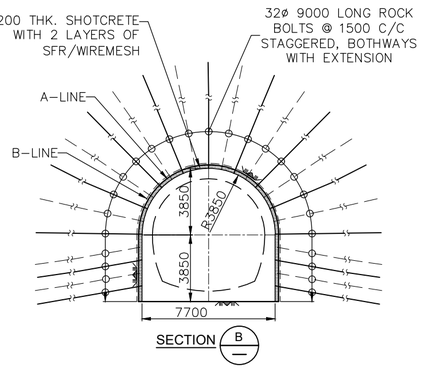

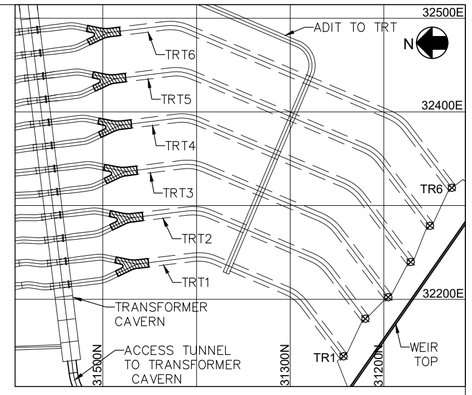

KEY PLAN
(NTS)

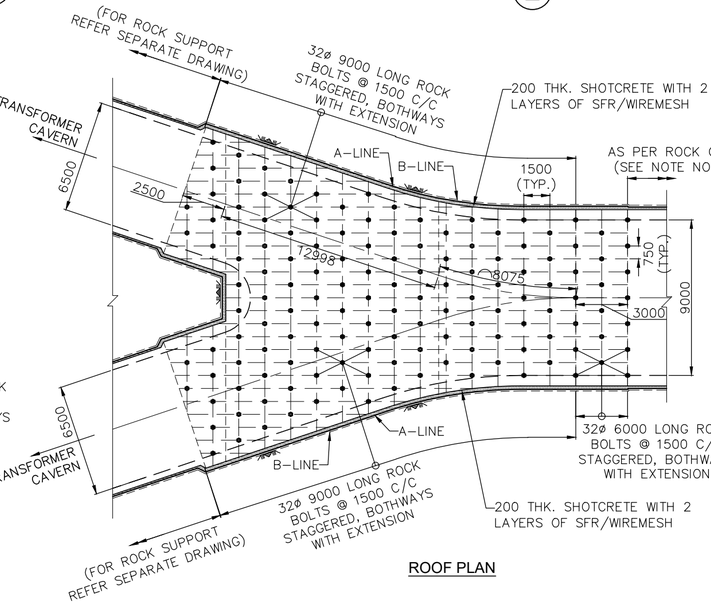


ROOF PLAN


NOTES: –


1. सभी माप मिलीमीटर में तथा ऊंचाई मीटर में दिए गए हैं।
 ALL DIMENSIONS ARE IN MILLIMETERS AND LEVELS IN METERS.
2. THE DEFINITION OF 'A' & 'B' LINE AND VARIOUS CLASSES OF EXCAVATION SHOWN SHALL BE AS PER SECTION B.3 OF TECHNICAL SPECIFICATION.
3. MINOR MODIFICATION IN THE LENGTH, ORIENTATION, PATTERN AND LOCATION OF ROCK ANCHORS/BOLTS MAY BE DONE TO SUIT THE SITE CONDITIONS WITH THE APPROVAL OF ENGINEER–IN–CHARGE.
4. ROCK ANCHORS/BOLTS SHOWN IN THE DRAWING SHALL BE CONFORMING TO SECTION B.4 OF TECHNICAL SPECIFICATION.
5. REQUIREMENT OF 45 MM DIA. 5000 LONG (INTO ROCK) PRESSURE RELIEF HOLES WITH 36 MM DIA. PERFORATED PVC PIPES AS PER SECTION B.7 OF TECHNICAL SPECIFICATION WILL BE DETERMINED BY ENGINEER–IN–CHARGE TO SUIT THE SITE CONDITION.
6. SHOTCRETE SHOWN ON DRAWING SHALL BE APPLIED AS SPECIFIED IN SECTION B.5 OF TECHNICAL SPECIFICATION.
7. UNDERGROUND EXCAVATION INCLUDING PROTECTION OF TUNNEL INVERT SHALL BE CONFIRMING TO SECTION B.3 OF TECHNICAL SPECIFICATION.
8. IF ADDITIONAL ROCK SUPPORT MEASURES ARE REQUIRED BASED ON THE SITE SPECIFIC CONDITIONS THEN REFER DRG. NO. NHDB– 4BC4–41–DD–1007.
9. FOR CONCRETE & REINFORCEMENT OF JUNCTION, REFER SEPARATE DRAWINGS.
10. FOR ROCK SUPPORTS OF TAIL RACE TUNNEL (9M DIA.) OUTSIDE THE LIMITS OF THE JUNCTION REFER DRAWING NO. NHDB–4DC4–41–DD–1009.


REFERENCE DRAWINGS :-


1. NHDB-4DC4-41-DD-0001 TO 0006
2. NHDB-4DC4-41-DD-1009 TO 1011
3. NHDB-4BC4-41-DD-1007

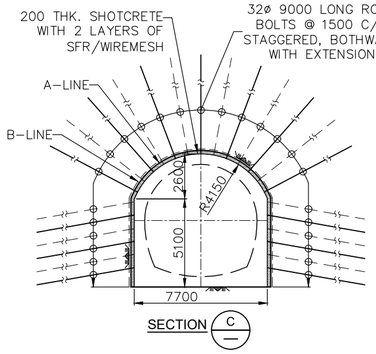


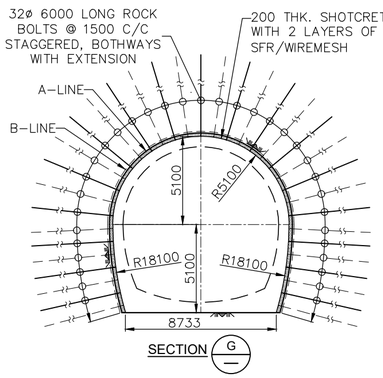


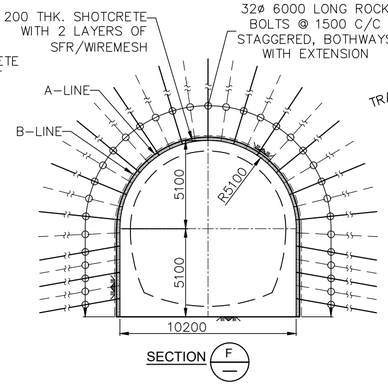

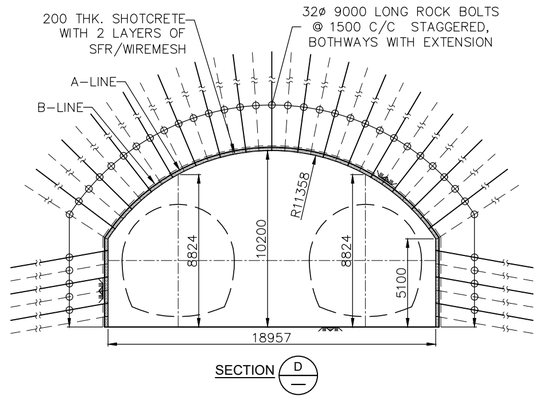

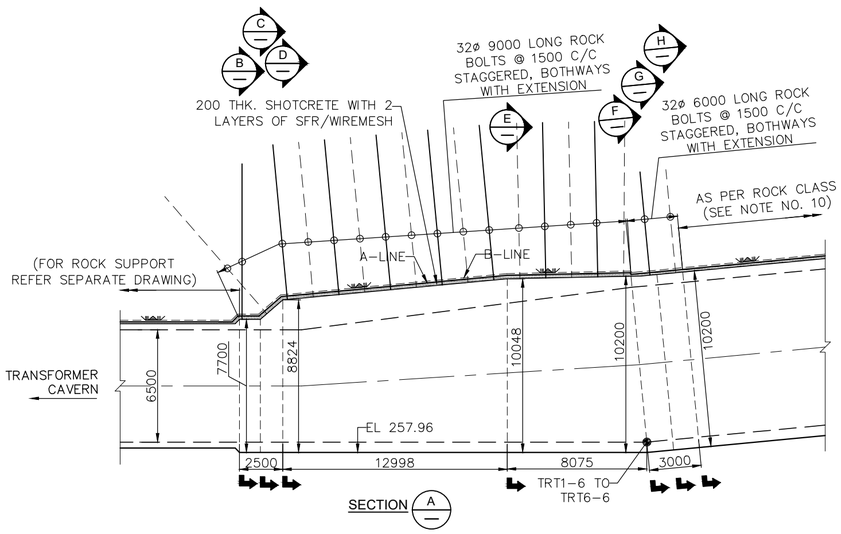

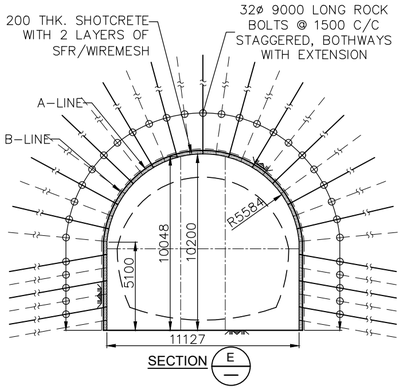

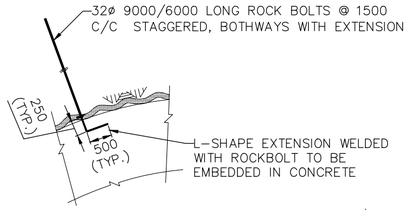

TYPICAL DETAIL OF ROCK BOLT WITH EXTENSION

SCALE :

0 2.5 5.0 7.5 10.0 12.5 METRE

(SCALE 1:250)

एन एच पी सी लिमिटेड
(भारत सरकार का एक नवरत्न उद्यम)
NHPC Limited
(A GOVT. OF INDIA NAVRATNA ENTERPRISE)

दिबांग बहुउद्देशीय परियोजना
DIBANG MULTIPURPOSE PROJECT

TAIL RACE TUNNEL
BRANCH TAIL RACE TUNNEL JUNCTION
ROCK SUPPORT DETAILS

DATE	NO.	REVISION OR ISSUES	BY	CH. APP
14.07.26	00	ISSUED FOR CONSTRUCTION		

DESIGN MEMO NO. डिजाइन मेमो संख्या

DRAWN ड्रेविंग्रा KASHISH YADAV | SUBMITTED प्रस्तुत ASHISH RAO | RECOMMENDED अनुशंसित SAURABH SINGH | APPROVED अनुमोदित

DATE दिनांक JULY 2026 | DRG. NO. ड्रेइंग संख्या | NHDB | 4DC4 | 41 | DD | 1013 | 00

DRG. NO. NHDB-4DC4-41-DD-1013-00