
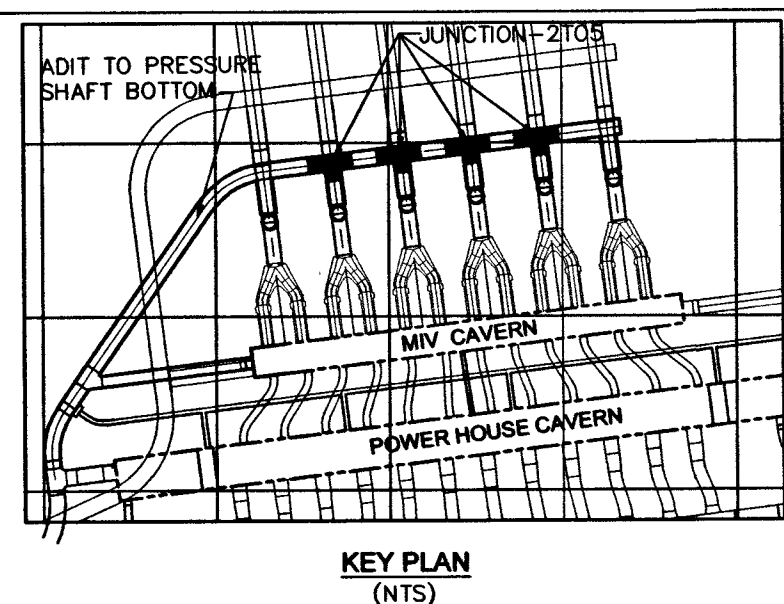


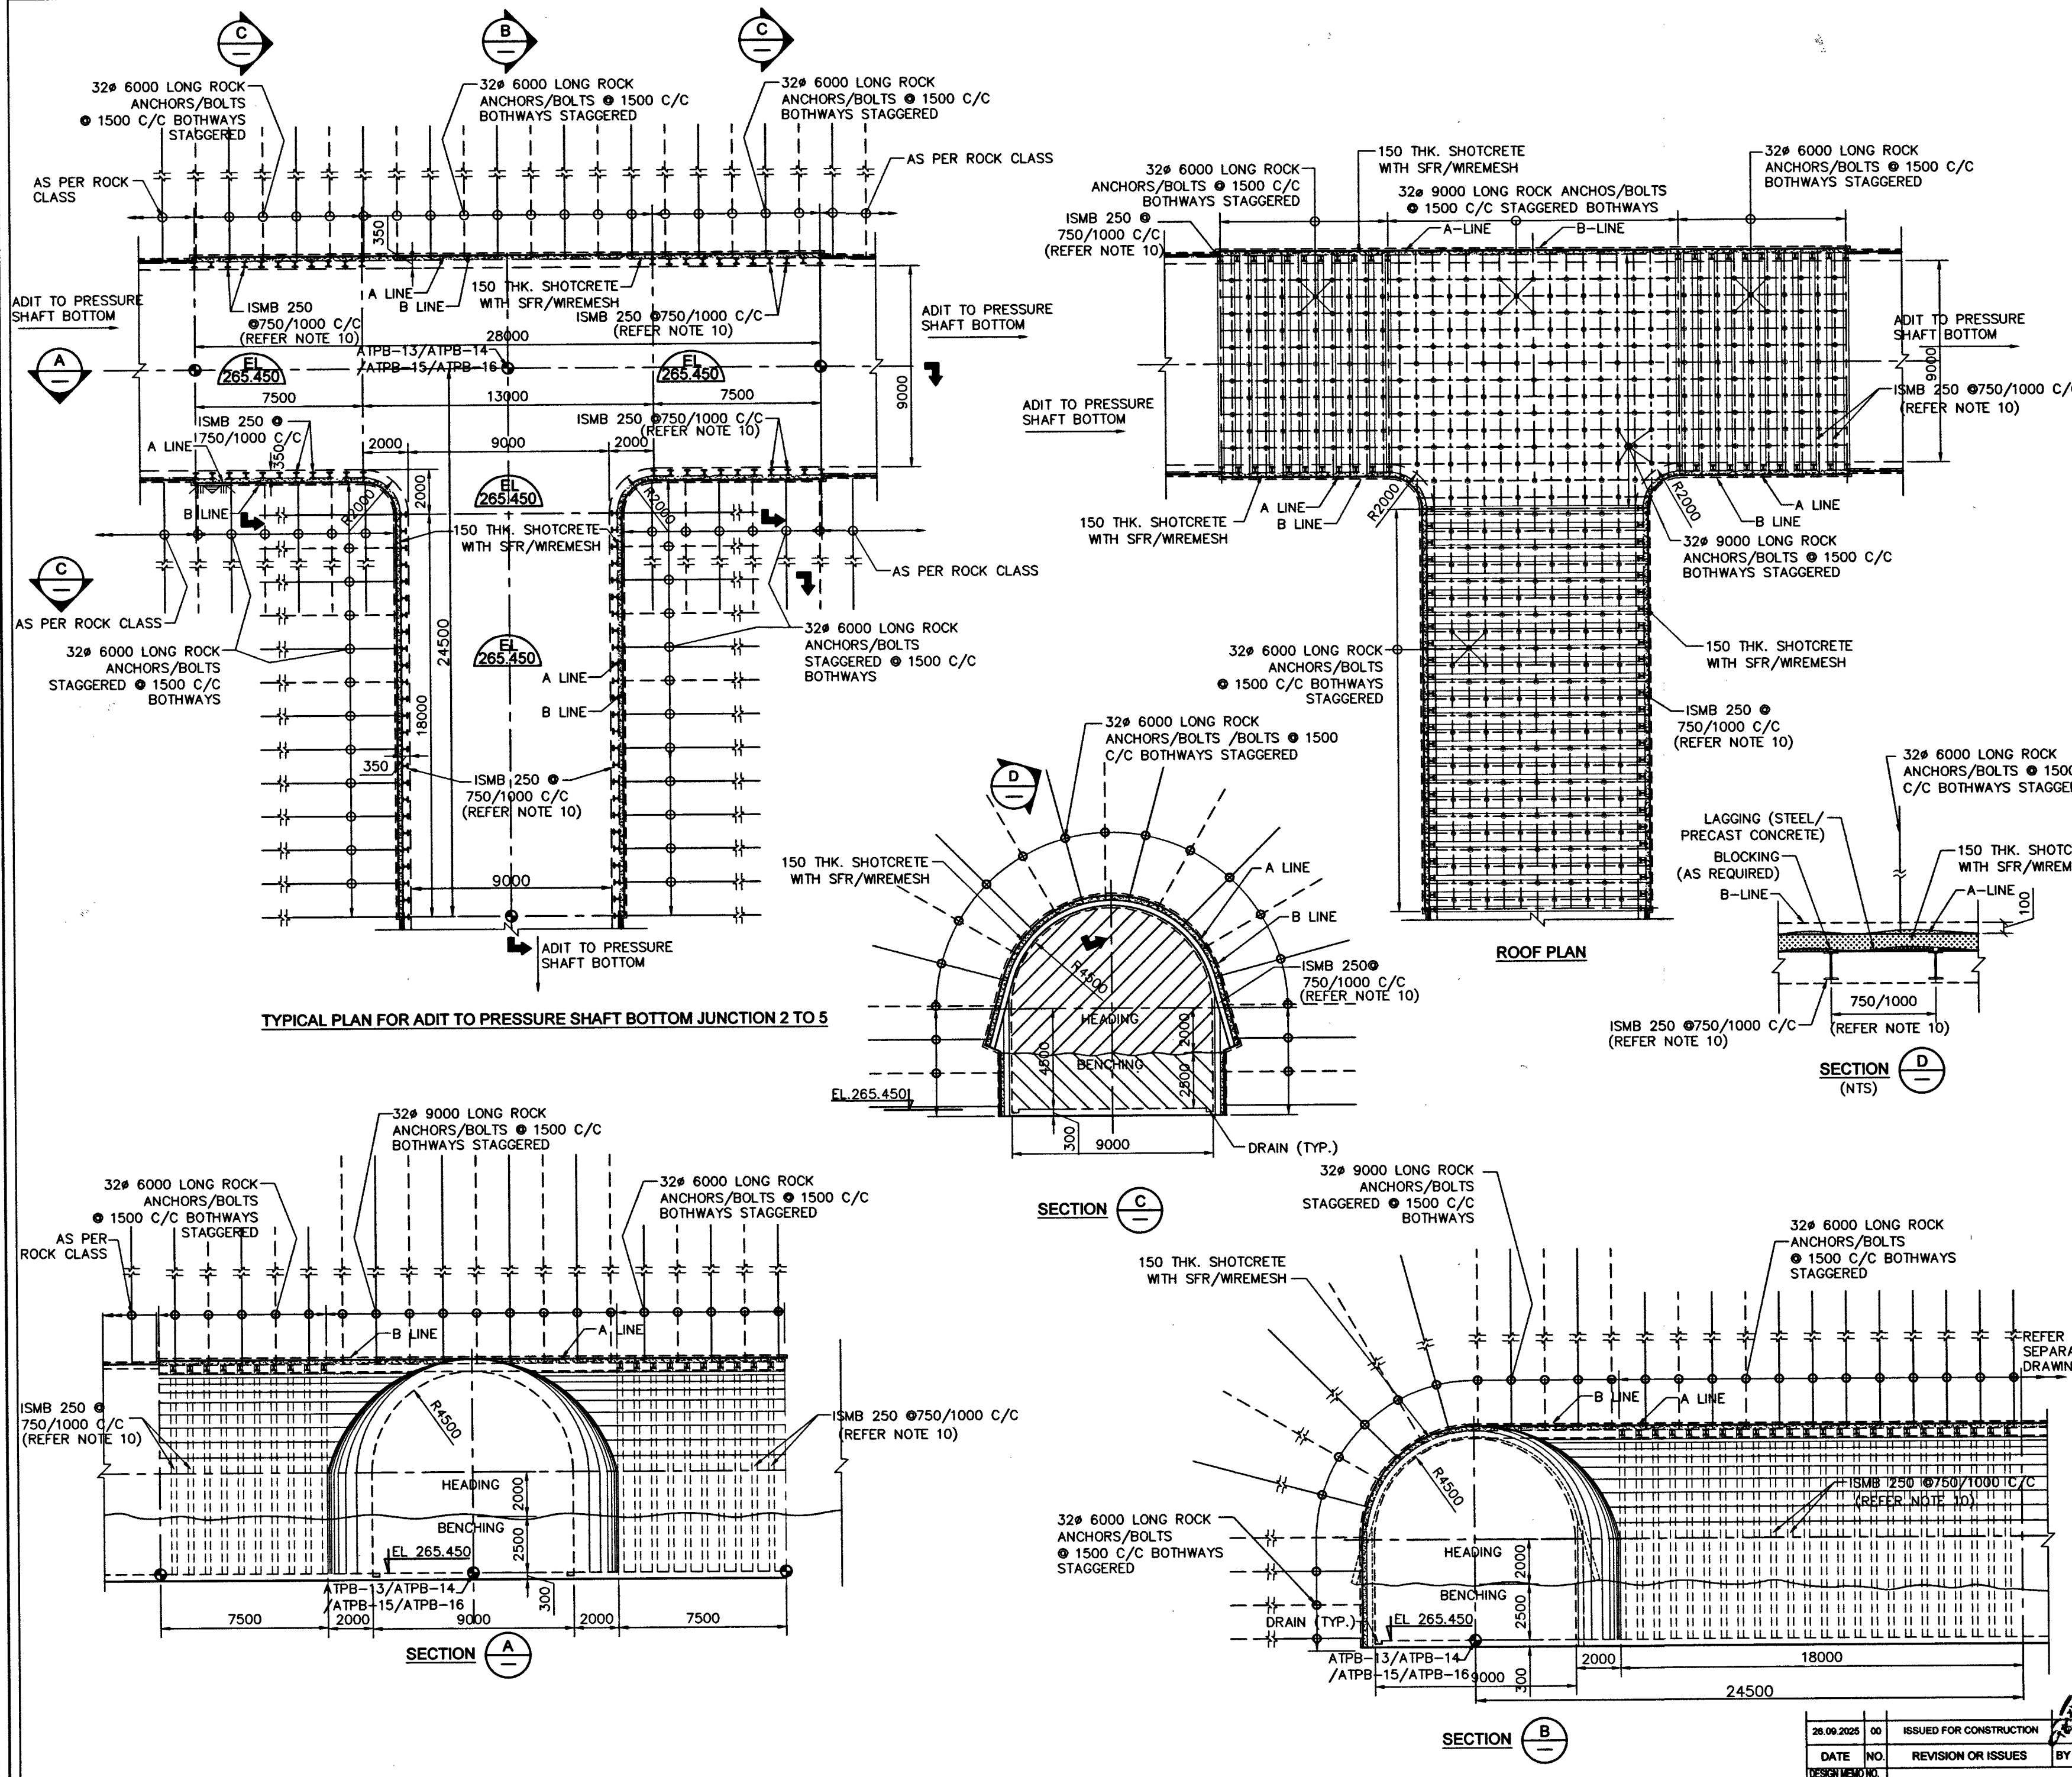

- NOTES:-**
- सभी माप मिलीमीटर में तथा ऊंचाई मीटर में दिए गए हैं।
ALL DIMENSIONS ARE IN MILLIMETERS AND LEVELS IN METERS.
 - THE DEFINITION OF 'A' & 'B' LINE AND VARIOUS CLASSES OF EXCAVATION SHOWN SHALL BE AS PER SECTION B.3 OF TECHNICAL SPECIFICATION.
 - MINOR MODIFICATION IN THE LENGTH, ORIENTATION, PATTERN AND LOCATION OF ROCK ANCHORS MAY BE DONE TO SUIT THE SITE CONDITIONS WITH THE APPROVAL OF ENGINEER-IN-CHARGE.
 - STEEL RIB SHALL BE CONFORMING TO SECTION B.4 OF TECHNICAL SPECIFICATION. SPACING OF STEEL RIBS SHOWN MAY BE MODIFIED TO SUIT THE SITE CONDITIONS WITH THE APPROVAL OF ENGINEER-IN-CHARGE.
 - ROCK ANCHORS/BOLTS SHOWN IN THE DRAWING SHALL BE CONFORMING TO SECTION B.4 OF TECHNICAL SPECIFICATION.
 - REQUIREMENT OF 45 MM DIA. 5000 LONG (INTO ROCK) PRESSURE RELIEF HOLES WITH 36 MM DIA. PERFORATED PVC PIPES AS PER SECTION B.7 OF TECHNICAL SPECIFICATION WILL BE DETERMINED BY ENGINEER-IN-CHARGE TO SUIT THE SITE CONDITION.
 - SHOTCRETE SHOWN ON DRAWING SHALL BE APPLIED AS SPECIFIED IN SECTION B.5 OF TECHNICAL SPECIFICATION.
 - STEEL LAGGING OR PRE CAST CONCRETE LAGGING AS SPECIFIED IN SECTION B.4 OF TECHNICAL SPECIFICATIONS SHALL BE USED AT THE JUNCTION WITH THE APPROVAL OF ENGINEER-IN-CHARGE.
 - UNDERGROUND EXCAVATION INCLUDING PROTECTION OF TUNNEL INVERT SHALL BE CONFORMING TO SECTION B.3 OF TECHNICAL SPECIFICATION.
 - THE SPACING OF STEEL RIBS AT THE JUNCTION SHALL BE @1000 C/C UPTO CLASS-IV AND @750 IN CLASS-VA & VB. THE SPACING OF RIBS MAY BE MODIFIED TO SUIT THE SITE CONDITIONS WITH THE APPROVAL OF ENGINEER-IN-CHARGE.
 - IF ADDITIONAL ROCK SUPPORT MEASURES ARE REQUIRED BASED ON THE SITE SPECIFIC CONDITIONS THEN REFER DRG. NO. NHDB-48C4-41-DD-1007 AS DIRECTED BY ENGINEER-IN-CHARGE.
 - FOR STEEL RIB DETAILS AT THE JUNCTION REFER DRG. NO. NHDB-38C4-41-DD-1003 TO 1004.
 - FOR ROCK SUPPORT OUTSIDE THE LIMITS SHOWN REFER DRG. NO. NHDB-38C4-41-DD-1002 TO 1004.
- REFERENCE DRAWINGS:-**
- NHDB-3KC4-41-DD-0001.
 - NHDB-38C4-41-DD-1002 TO 1004.
 - NHDB-3KC4-41-DD-1001 AND 1003.
- SCALE:**
- 0 2.0 4.0 6.0 8.0 10.0 METRE

एन एच पी सी लिमिटेड
(एन एच पी सी लिमिटेड का एक पूर्ण स्वतंत्र अंग)
NHPC Limited
(A GOVT. OF INDIA UNDERTAKING)

दिबांग बहुउद्देशीय परियोजना
DIBANG MULTIPURPOSE PROJECT

PRESSURE SHAFT
ADIT TO PRESSURE SHAFT BOTTOM
JUNCTION 2 TO 5 DETAILS

26.09.2025	00	ISSUED FOR CONSTRUCTION	DATE	NO.	REVISION OR ISSUES	BY	CH. APP.	DATE	NO.	REVISION OR ISSUES	BY	CH. APP.
26.09.2025	00	ISSUED FOR CONSTRUCTION	26.09.2025	00	ISSUED FOR CONSTRUCTION	CH. APP.	CH. APP.	26.09.2025	00	ISSUED FOR CONSTRUCTION	CH. APP.	CH. APP.

DESIGN MEMO NO. 18/2025

DRG. NO. NHDB 3KC4 41 DD 1002-00

REVISION NO. 03 EFF. DATE 21.07.2016