




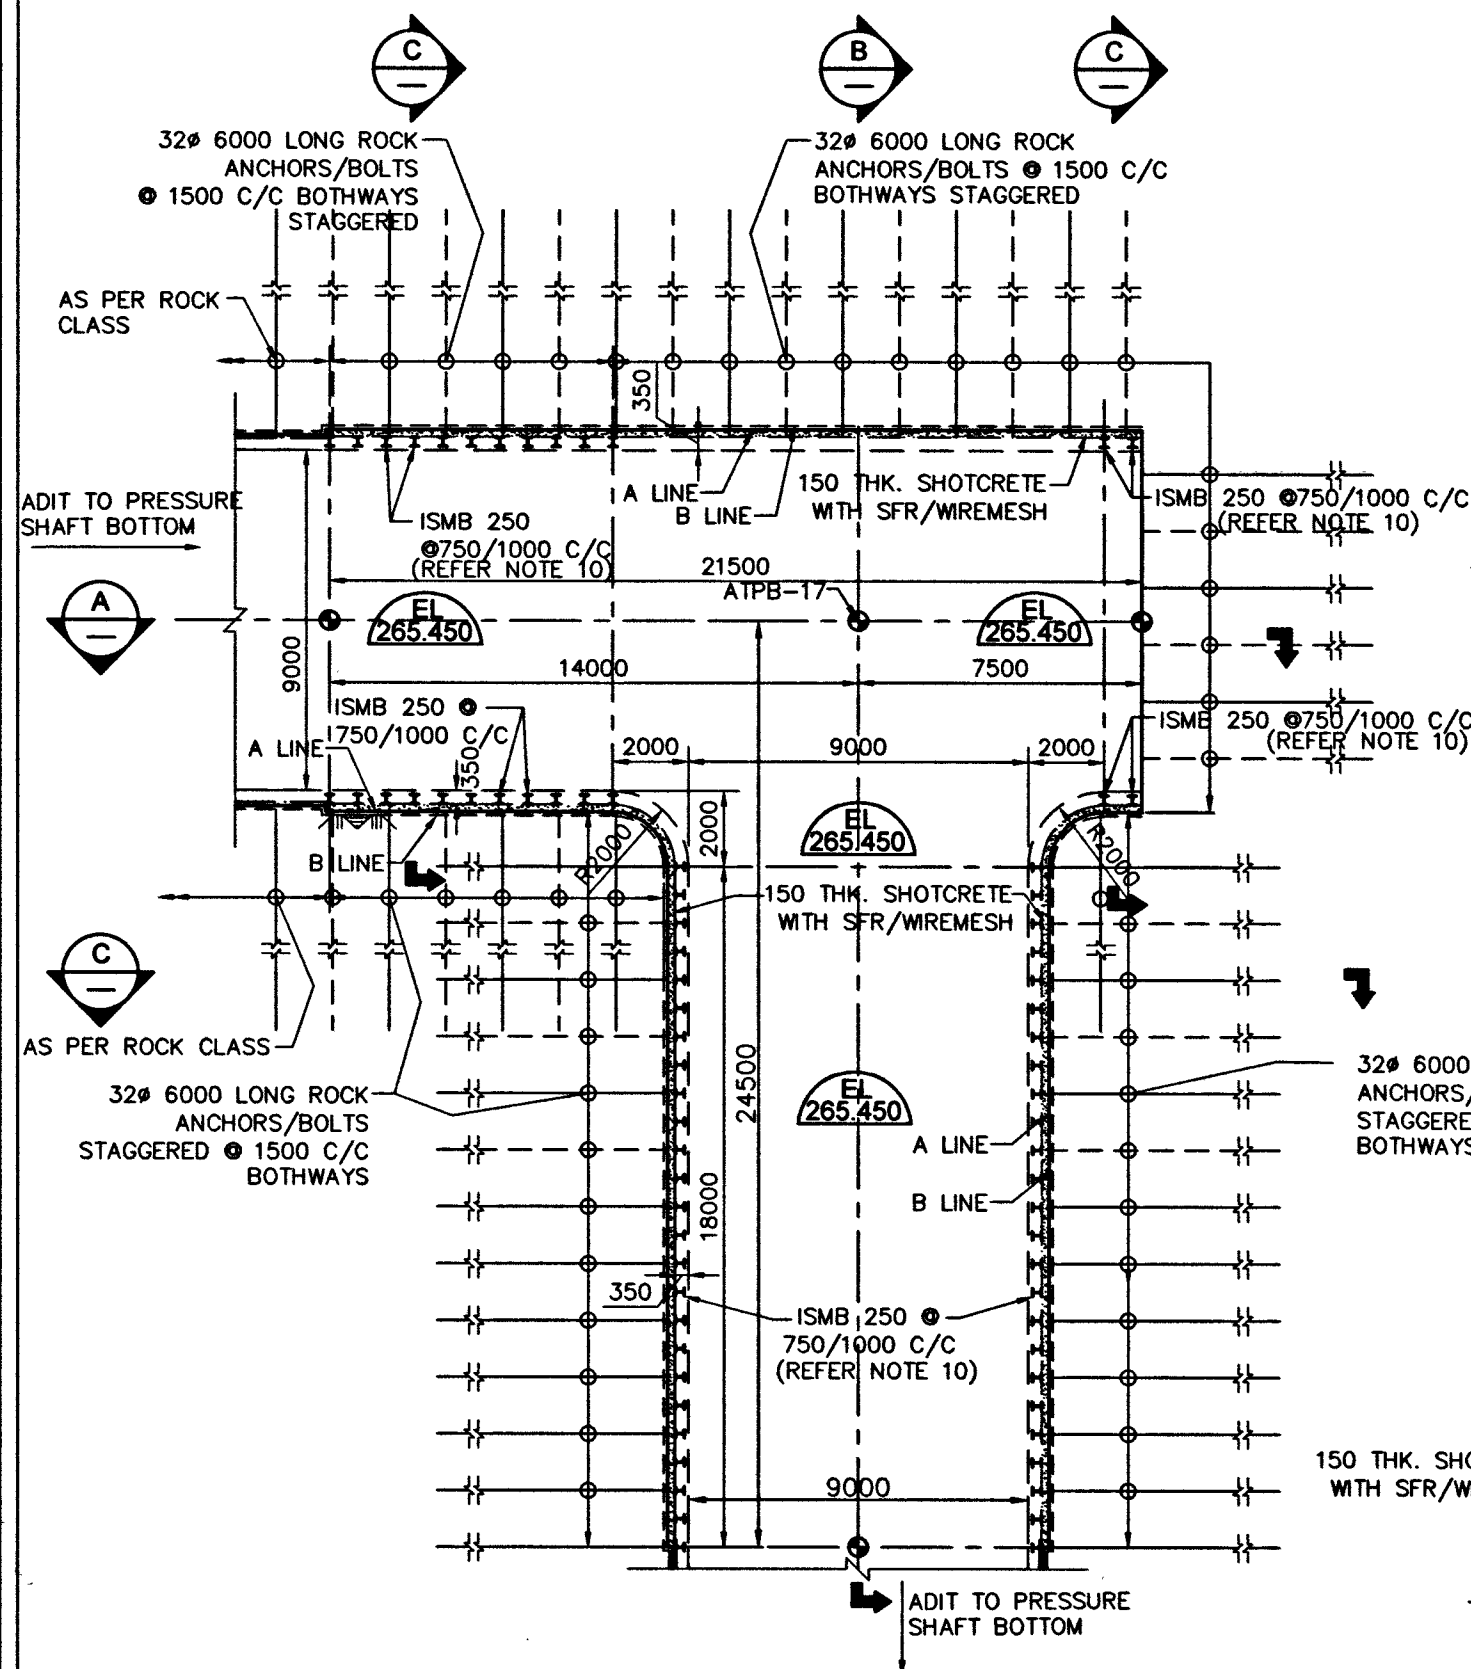


TYPICAL PLAN FOR ADIT TO PRESSURE SHAFT BOTTOM JUNCTION 6

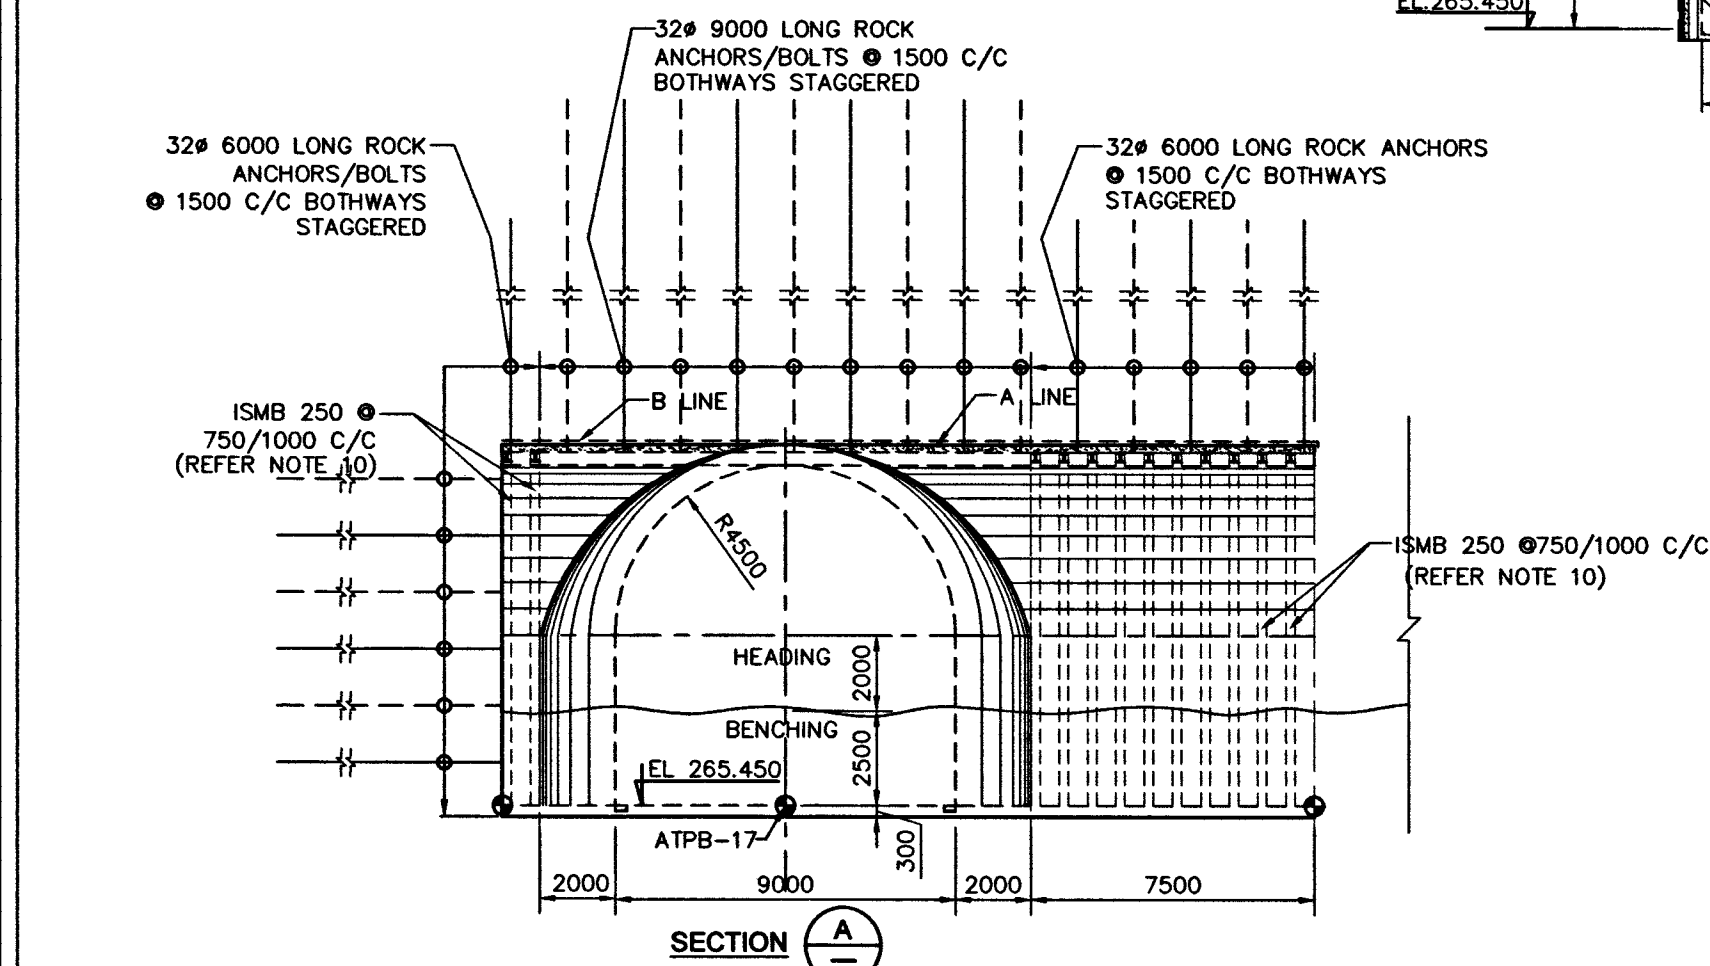

SECTION A-A

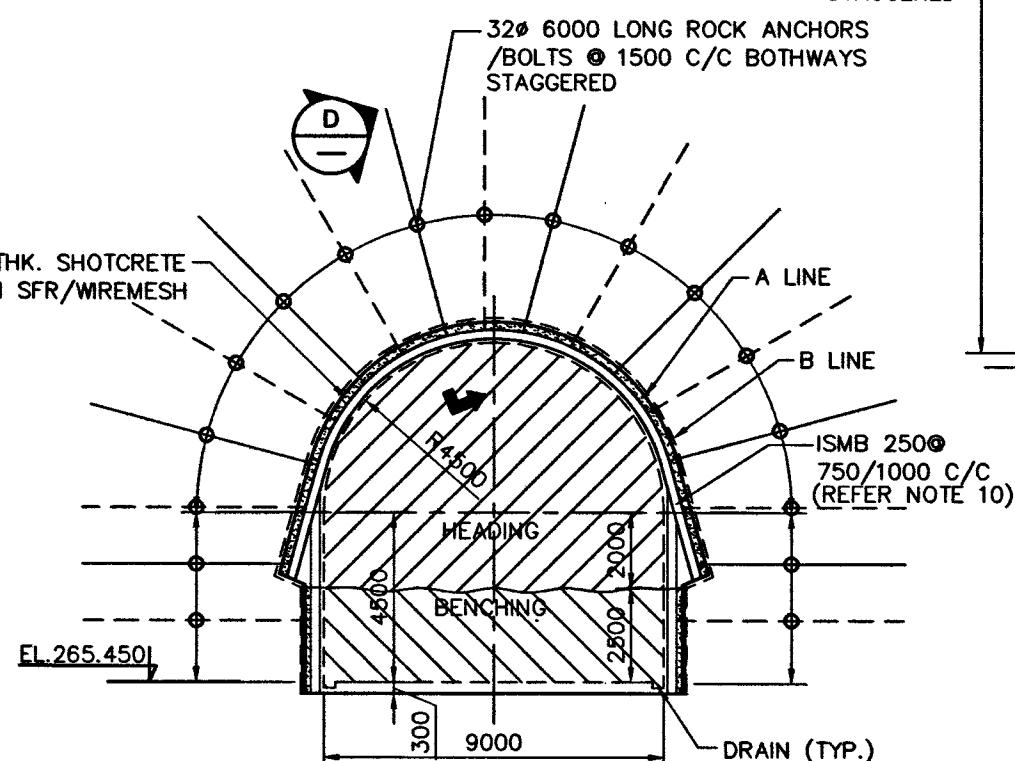


SECTION C-C

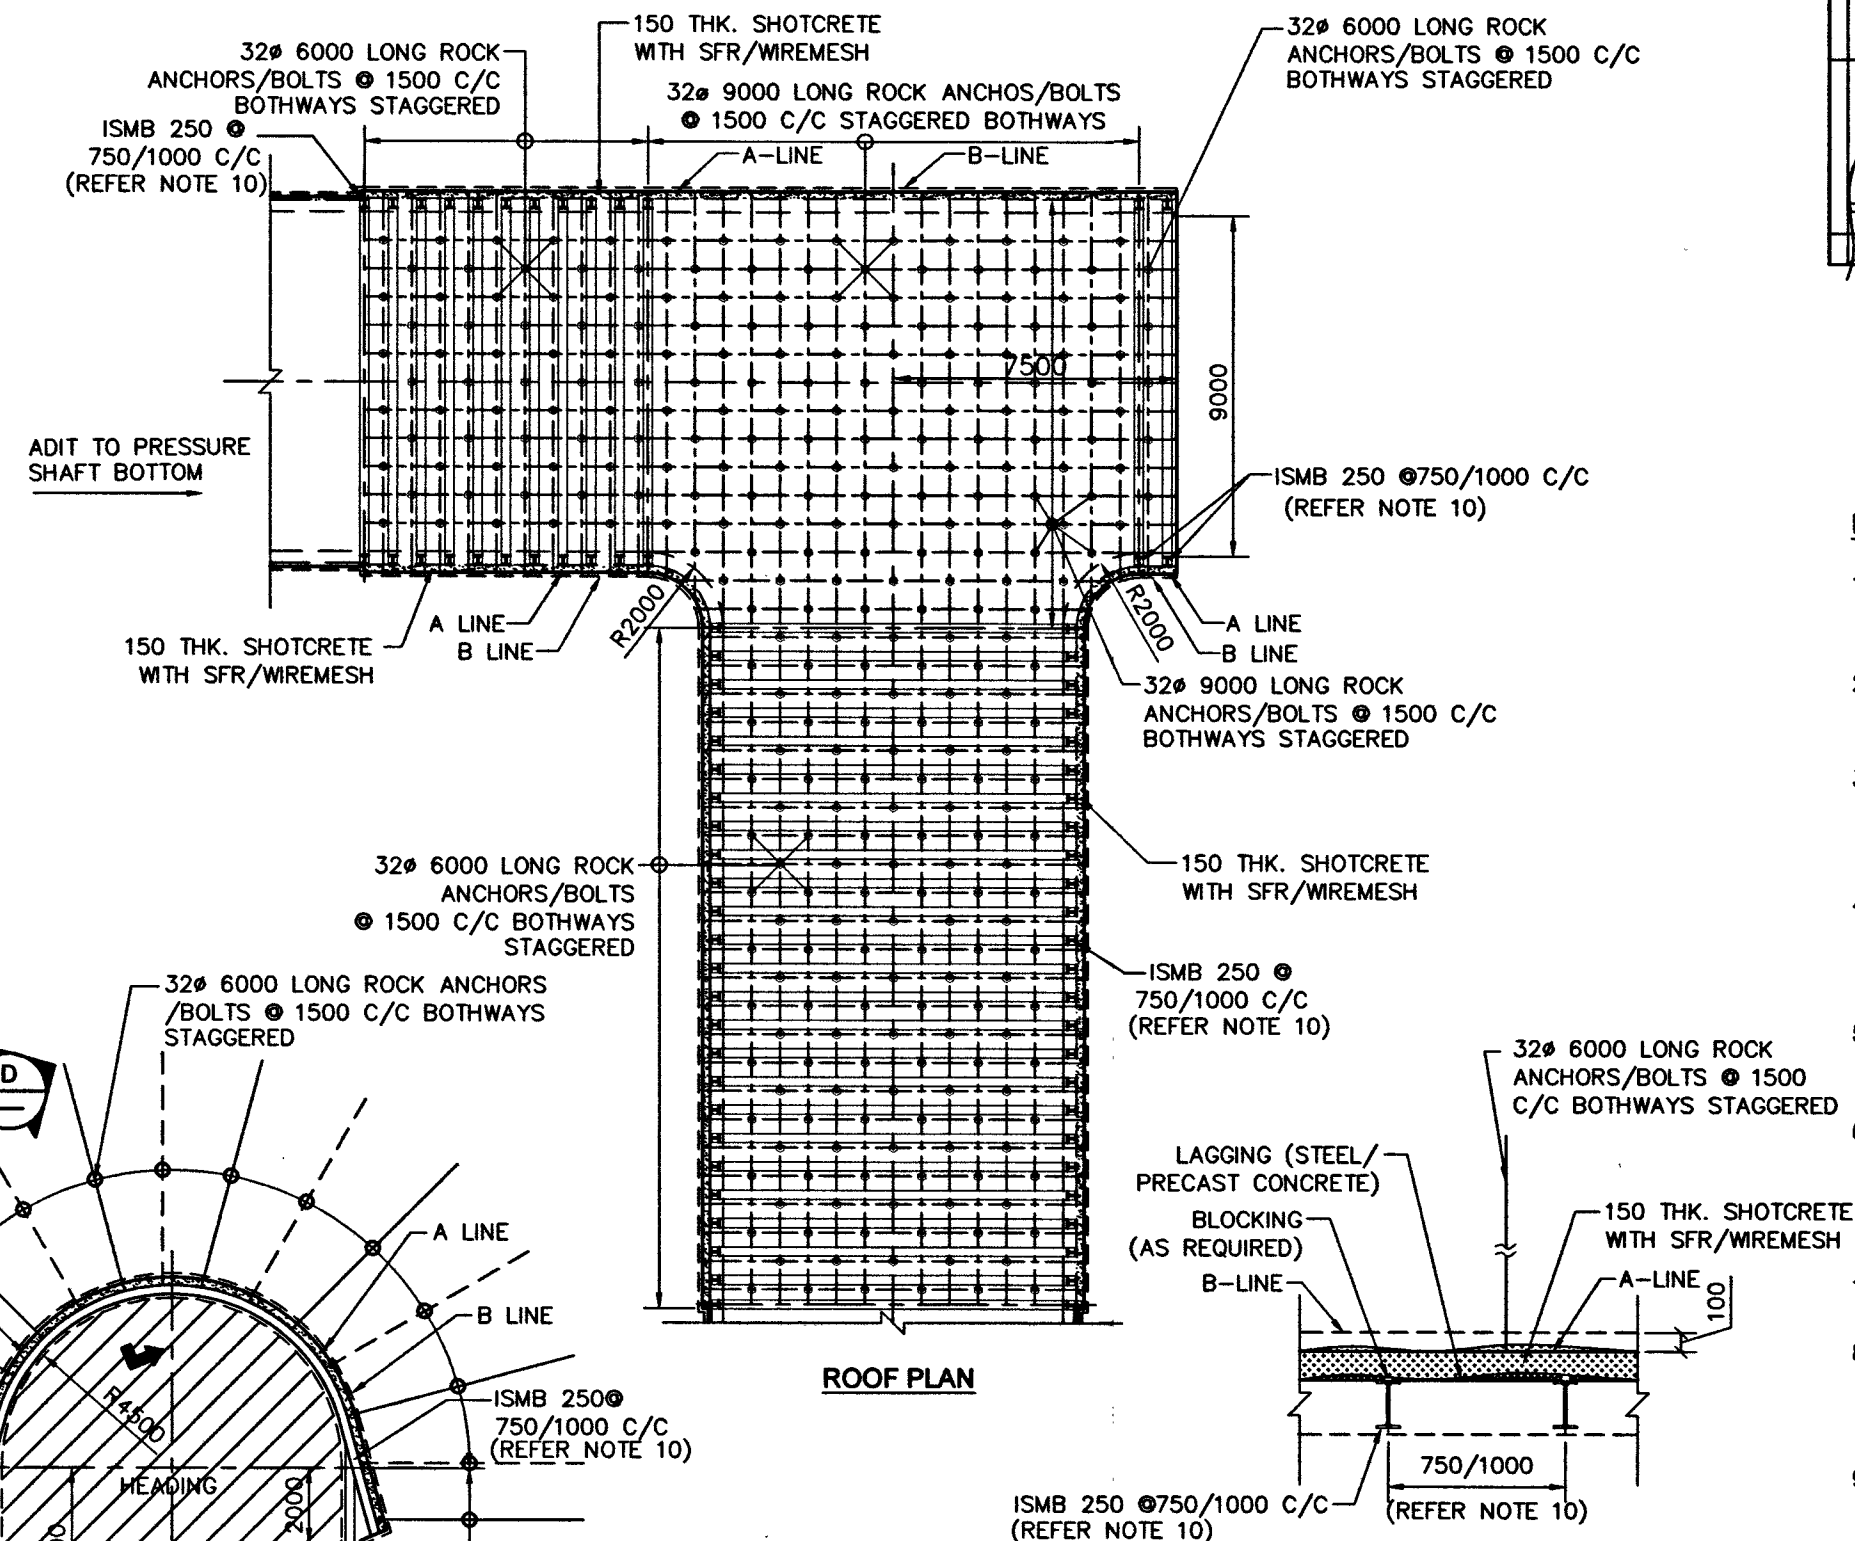


ROOF PLAN

SECTION D-D

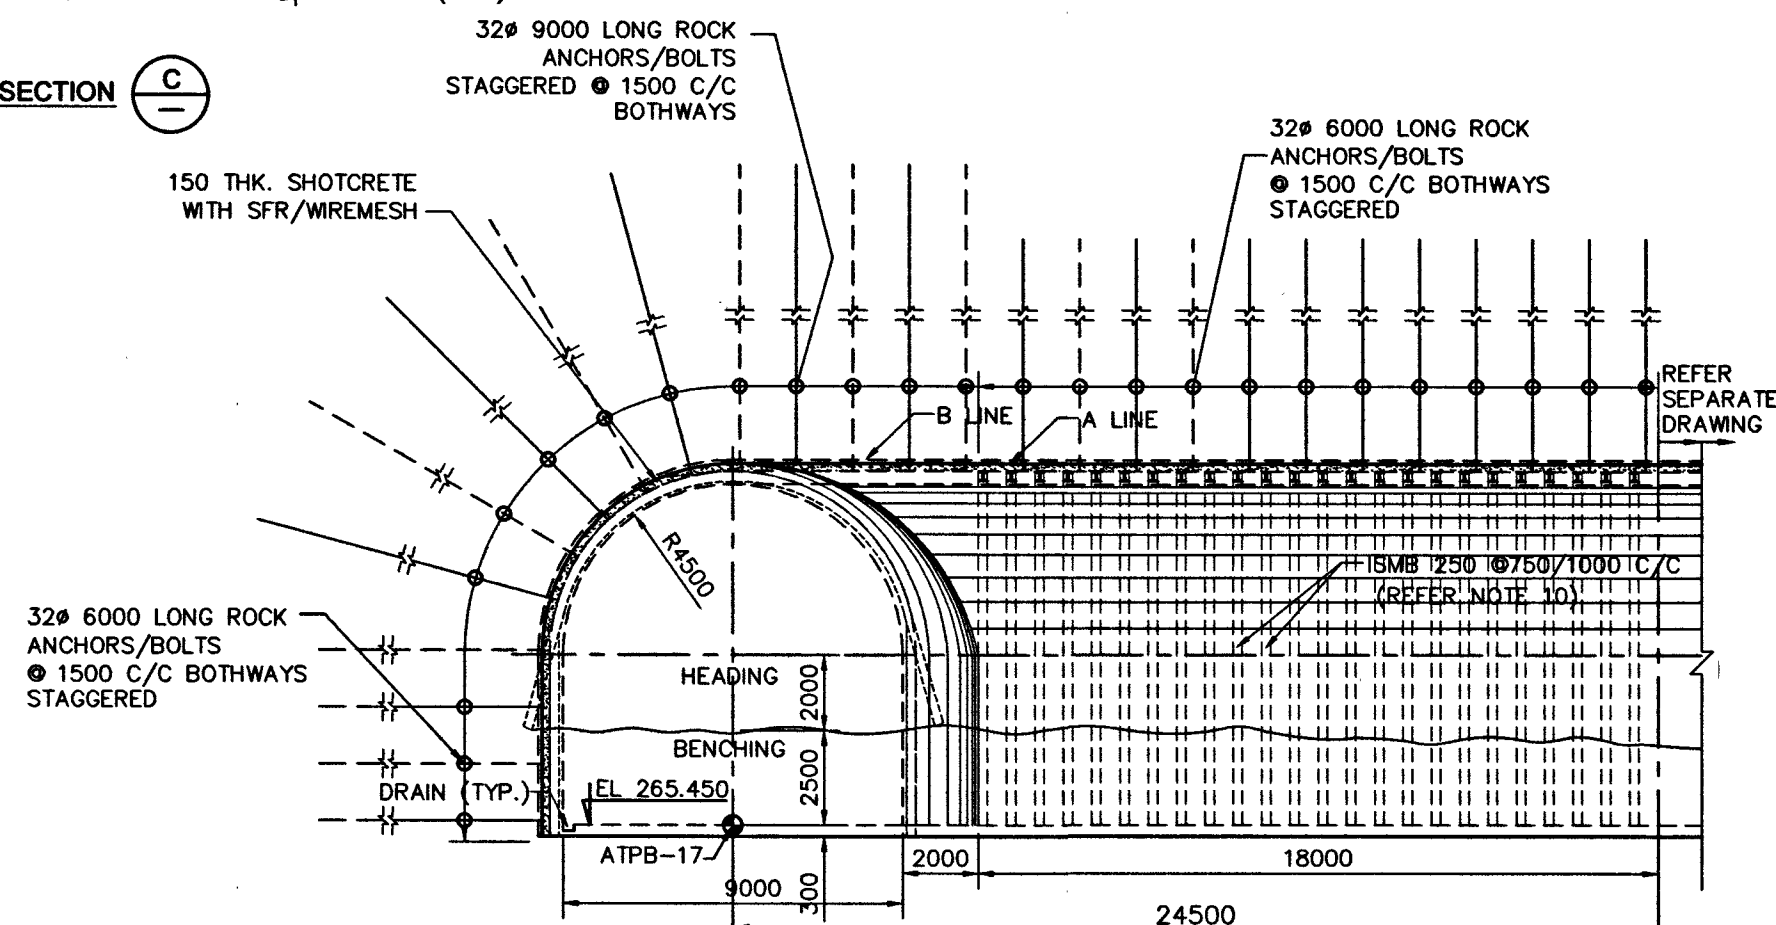

SECTION B-B

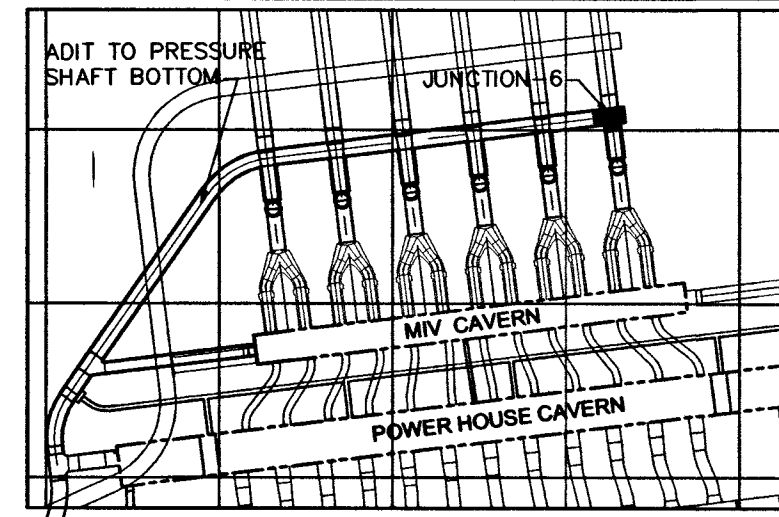

KEY PLAN (NTS)


NOTES:-

- सभी माप मिलीमीटर में तथा ऊंचाई मीटर में दिए गए हैं।
ALL DIMENSIONS ARE IN MILLIMETERS AND LEVELS IN METERS.
- THE DEFINITION OF 'A' & 'B' LINE AND VARIOUS CLASSES OF EXCAVATION SHOWN SHALL BE AS PER SECTION B.3 OF TECHNICAL SPECIFICATION.
- MINOR MODIFICATION IN THE LENGTH, ORIENTATION, PATTERN AND LOCATION OF ROCK ANCHORS MAY BE DONE TO SUIT THE SITE CONDITIONS WITH THE APPROVAL OF ENGINEER-IN-CHARGE.
- STEEL RIB SHALL BE CONFORMING TO SECTION B.4 OF TECHNICAL SPECIFICATION. SPACING OF STEEL RIBS SHOWN MAY BE MODIFIED TO SUIT THE SITE CONDITIONS WITH THE APPROVAL OF ENGINEER-IN-CHARGE.
- ROCK ANCHORS/BOLTS SHOWN IN THE DRAWING SHALL BE CONFORMING TO SECTION B.4 OF TECHNICAL SPECIFICATION.
- REQUIREMENT OF 45 MM DIA. 5000 LONG (INTO ROCK) PRESSURE RELIEF HOLES WITH 36 MM DIA. PERFORATED PVC PIPES AS PER SECTION B.7 OF TECHNICAL SPECIFICATION WILL BE DETERMINED BY ENGINEER-IN-CHARGE TO SUIT THE SITE CONDITION.
- SHOTCRETE SHOWN ON DRAWING SHALL BE APPLIED AS SPECIFIED IN SECTION B.5 OF TECHNICAL SPECIFICATION.
- STEEL LAGGING OR PRE CAST CONCRETE LAGGING AS SPECIFIED IN SECTION B.4 OF TECHNICAL SPECIFICATIONS SHALL BE USED AT THE JUNCTION WITH THE APPROVAL OF ENGINEER-IN-CHARGE.
- UNDERGROUND EXCAVATION INCLUDING PROTECTION OF TUNNEL INVERT SHALL BE CONFORMING TO SECTION B.3 OF TECHNICAL SPECIFICATION.
- THE SPACING OF STEEL RIBS AT THE JUNCTION SHALL BE 1000 C/C UPTO CLASS-IV AND 750 IN CLASS-VA & VB. THE SPACING OF RIBS MAY BE MODIFIED TO SUIT THE SITE CONDITIONS WITH THE APPROVAL OF ENGINEER-IN-CHARGE.
- IF ADDITIONAL ROCK SUPPORT MEASURES ARE REQUIRED BASED ON THE SITE SPECIFIC CONDITIONS THEN REFER DRG. NO. NHDB-48C4-41-DD-1007 AS DIRECTED BY ENGINEER-IN-CHARGE.
- FOR STEEL RIB DETAILS AT THE JUNCTION REFER DRG. NO. NHDB-38C4-41-DD-1002 TO 1004.
- FOR ROCK SUPPORT OUTSIDE THE LIMITS SHOWN REFER DRG. NO. NHDB-38C4-41-DD-1002 TO 1004.

REFERENCE DRAWINGS:-

- NHDB-3KC4-41-DD-0001.
- NHDB-38C4-41-DD-1002 TO 1004.
- NHDB-3KC4-41-DD-1001 TO 1002.

SCALE:

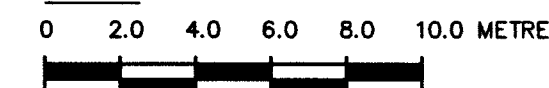

एन एच पी सी लिमिटेड NHPC Limited (A GOVT. OF INDIA NAVRATNA ENTERPRISE)	
दिवांग बहुउद्देशीय परियोजना DIBANG MULTIPURPOSE PROJECT	
PRESSURE SHAFT ADIT TO PRESSURE SHAFT BOTTOM JUNCTION 6 DETAILS	
26.06.2025 00 DATE NO. DESIGN MEMO NO. डिजाइन मेमो संख्या	ISSUED FOR CONSTRUCTION REVISION OR ISSUES BY CH. APP.
26.06.2025 00 DATE NO. DESIGN MEMO NO. डिजाइन मेमो संख्या	APPROVED अनुमोदित
SEPT 2025 DRG. NO. 3KC4 41 DD 1003 00	REV. NO.: 03 EFF. DATE 21.07.2018