




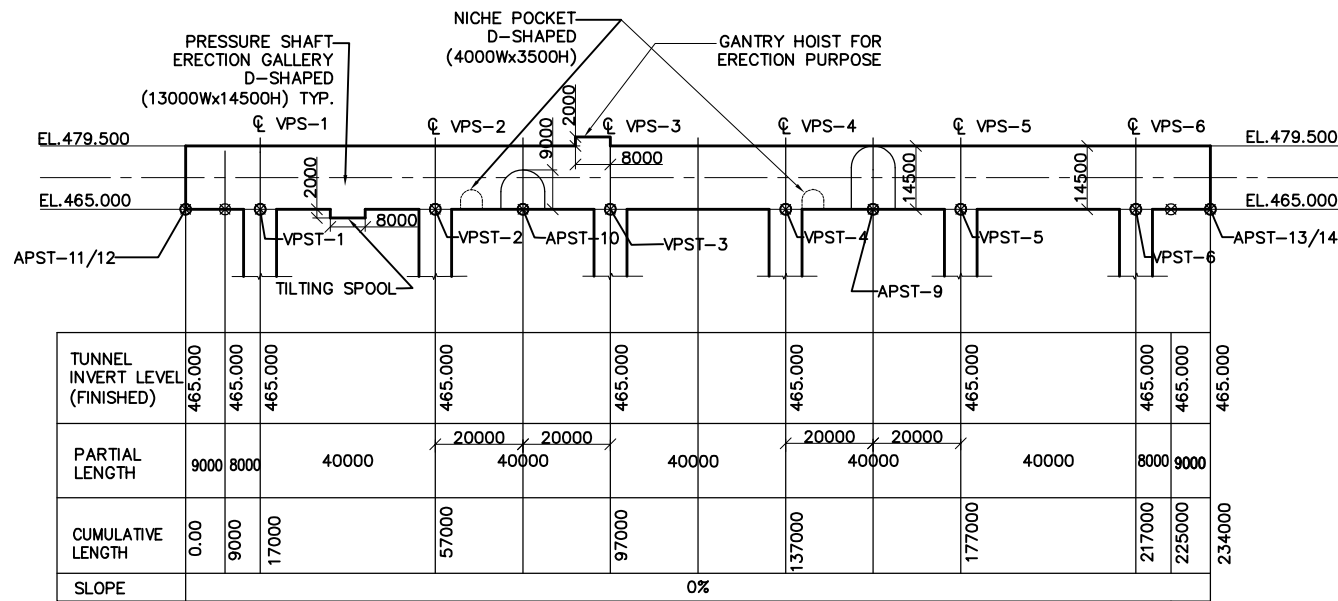


LONGITUDINAL SECTION

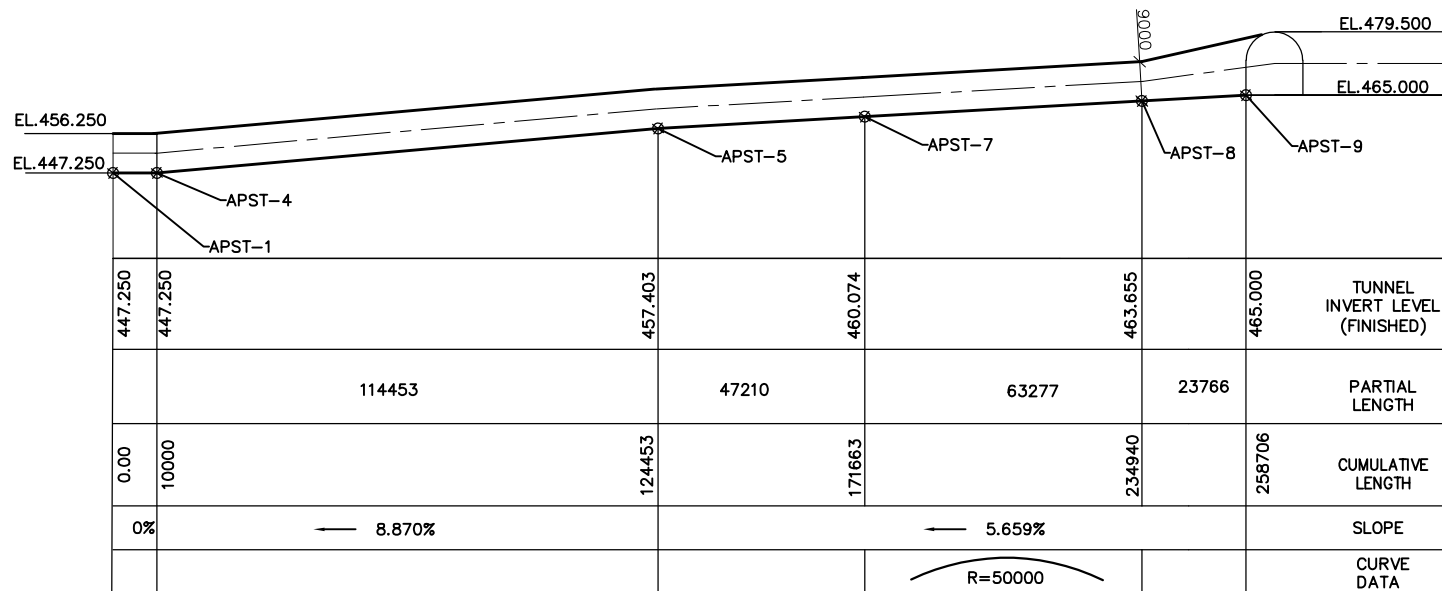

LONGITUDINAL SECTION

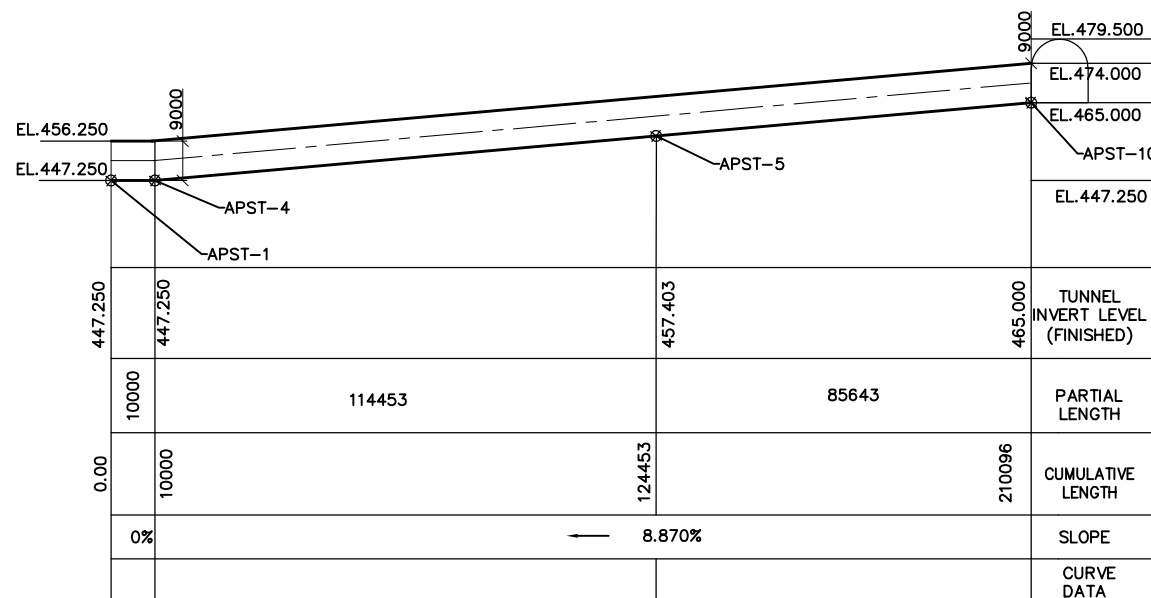

LONGITUDINAL SECTION

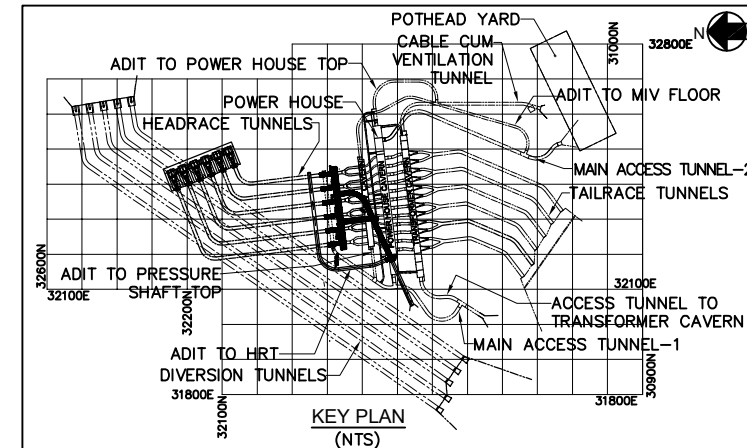


NOTES:-

- सभी माप मिलीमीटर में, ग्रीड तथा ऊंचाई मीटर में दिए गए हैं।
ALL DIMENSIONS ARE IN MILLIMETRE AND GRIDS, COORDINATES & ELEVATIONS ARE IN METRE.
- THIS DRAWING SHALL BE READ IN CONJUNCTION WITH DRAWING NO. NHDB-3KC4-41-DD-0009.
- FOR OTHER NOTES REFER DRAWING NO. NHDB-3KC4-41-DD-0009.
- THIS DRAWING SUPERCEDES THE DRAWING NO. NHDB-3KC4-41-DD-0002.

REFERENCE DRAWINGS:-

- NHDB-1AC4-41-DD-0001.
- NHDB-3BC4-41-DD-0001.
- NHDB-3BC4-41-DD-1002 TO 1004.

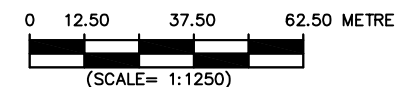

एन एच पी सी लिमिटेड (एन एच पी सी लिमिटेड) NHPC Limited (A GOVT. OF INDIA NAVRATNA ENTERPRISE)	
दिबांग बहुउद्देशीय परियोजना DIBANG MULTIPURPOSE PROJECT	
PRESSURE SHAFT ADIT TO PRESSURE SHAFT TOP LONGITUDINAL SECTION	
(SHEET 2 OF 2)	
15.07.2026 00	ISSUED FOR CONSTRUCTION
DATE NO.	REVISION OR ISSUES
DATE	BY, CH. APP.
15.07.2026	DRG. NO. 3KC4 41 DD 0010 00
डिजाइन	डिजाइन