

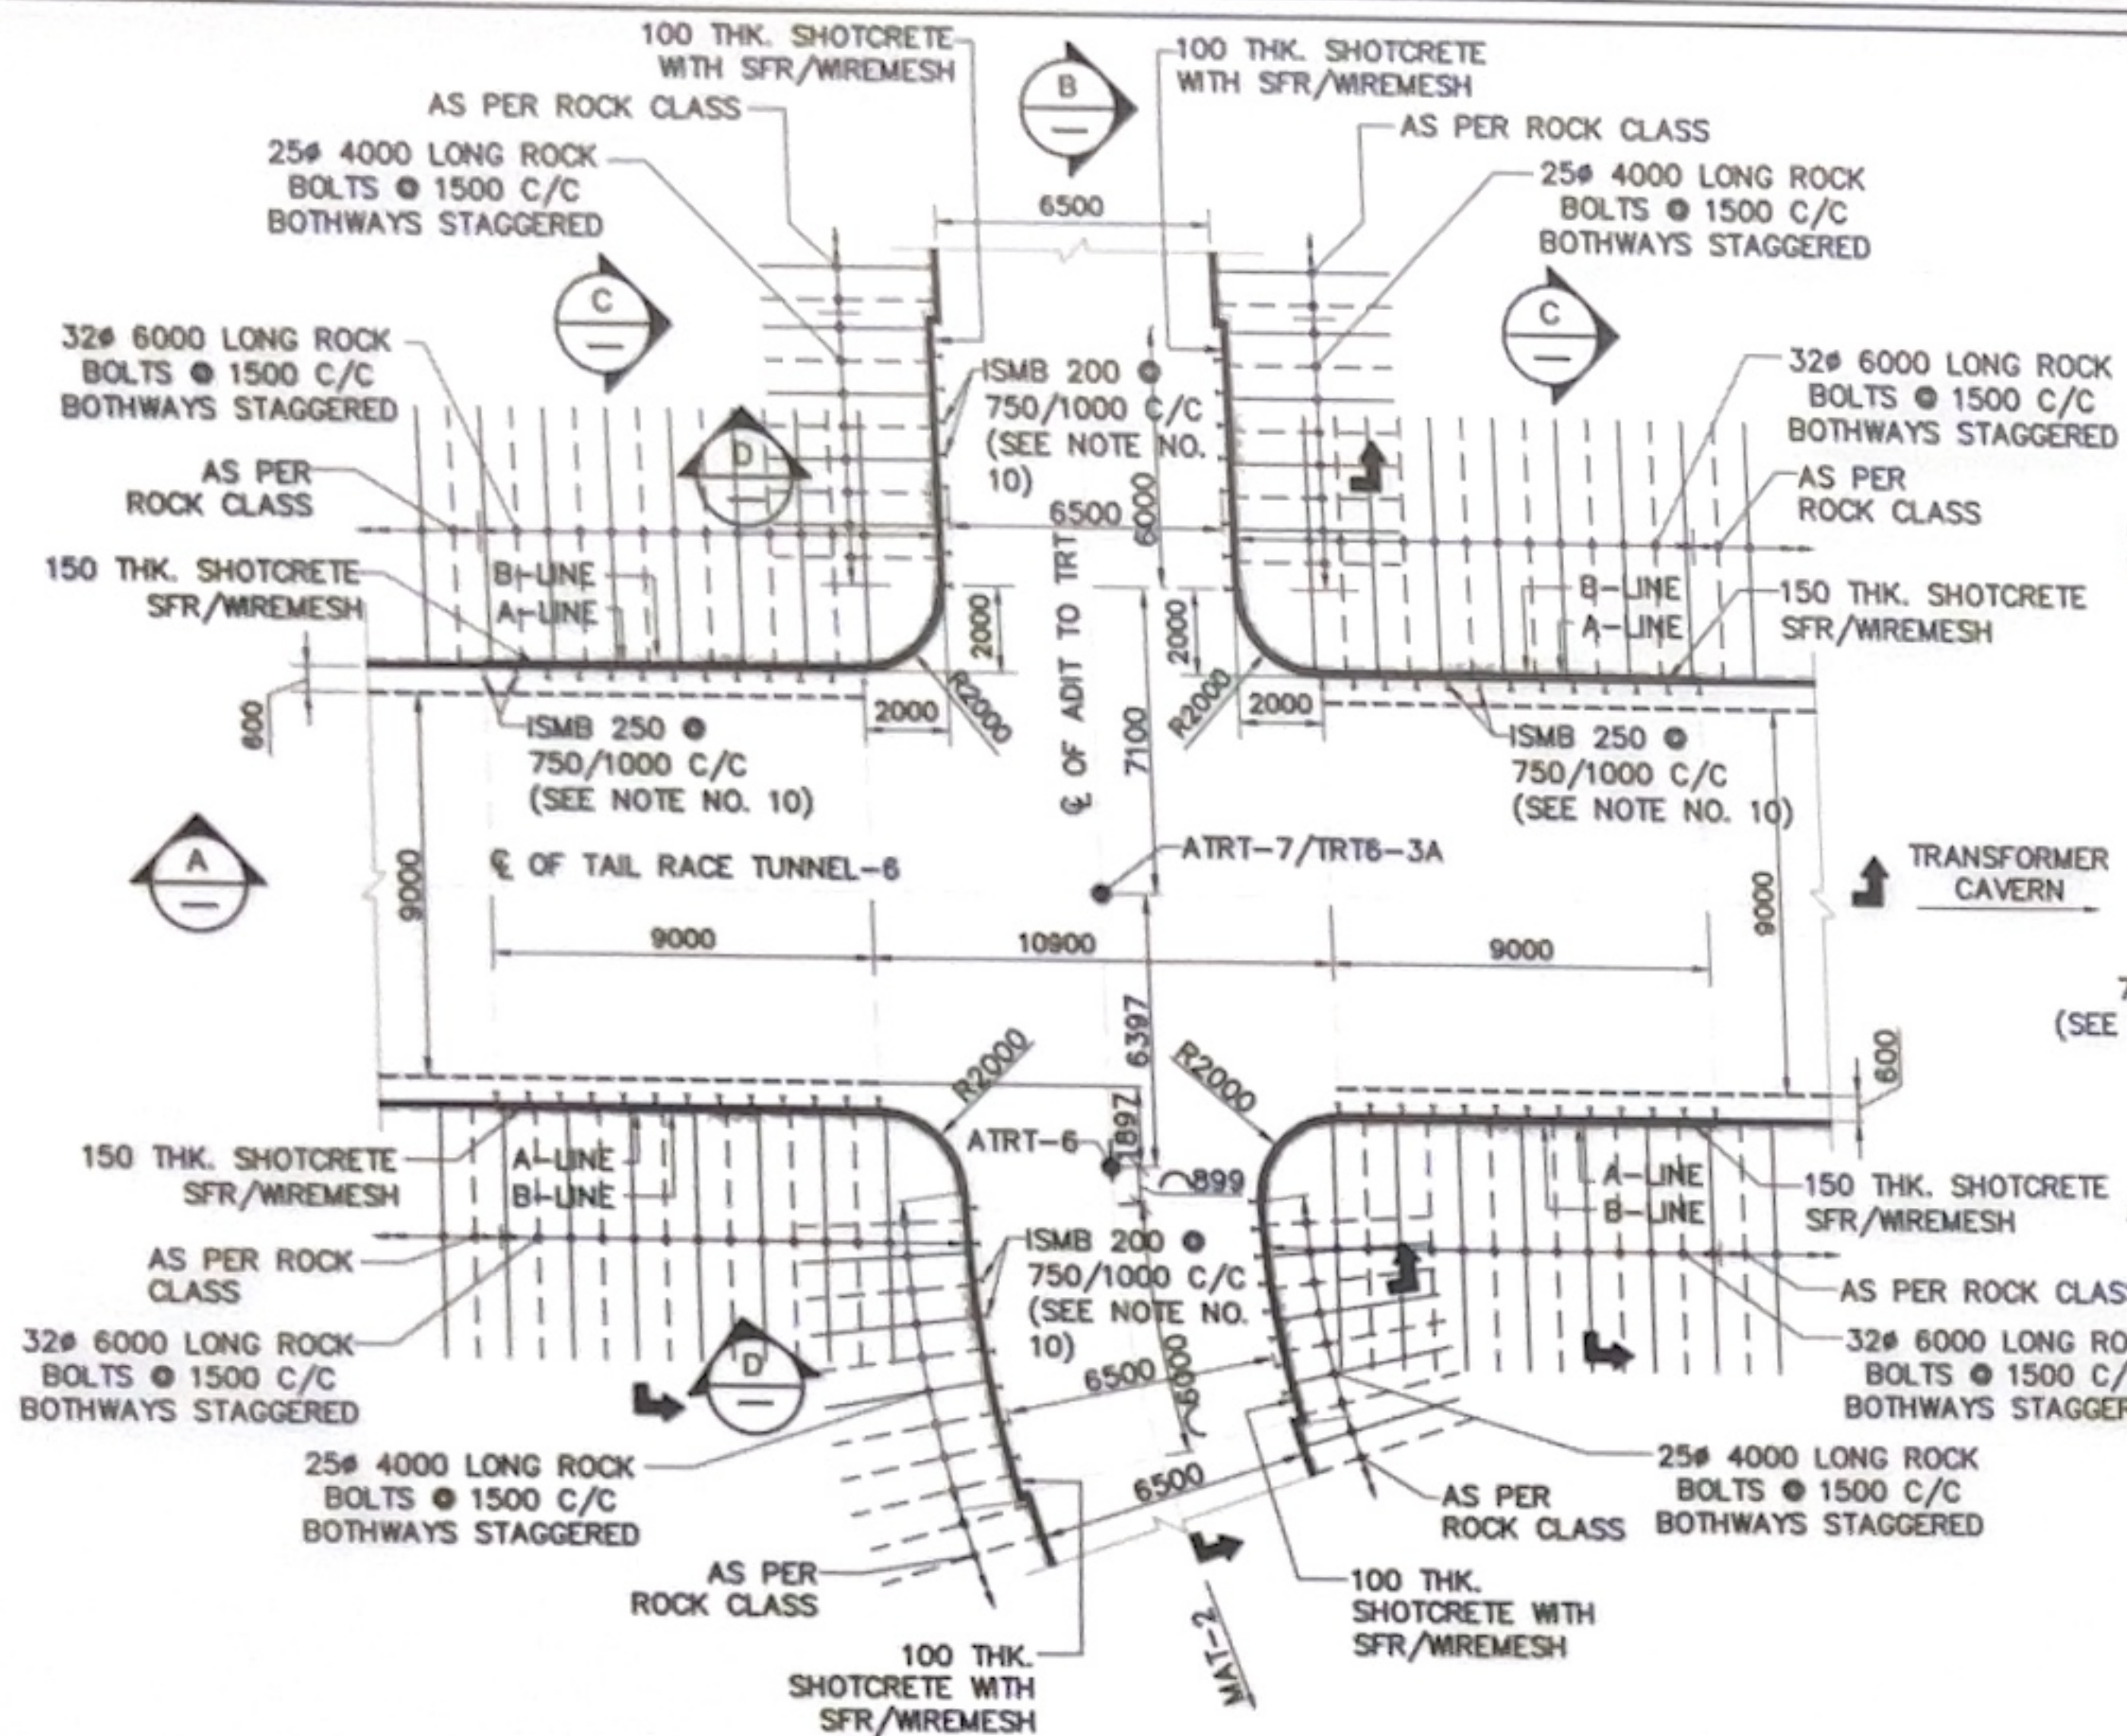
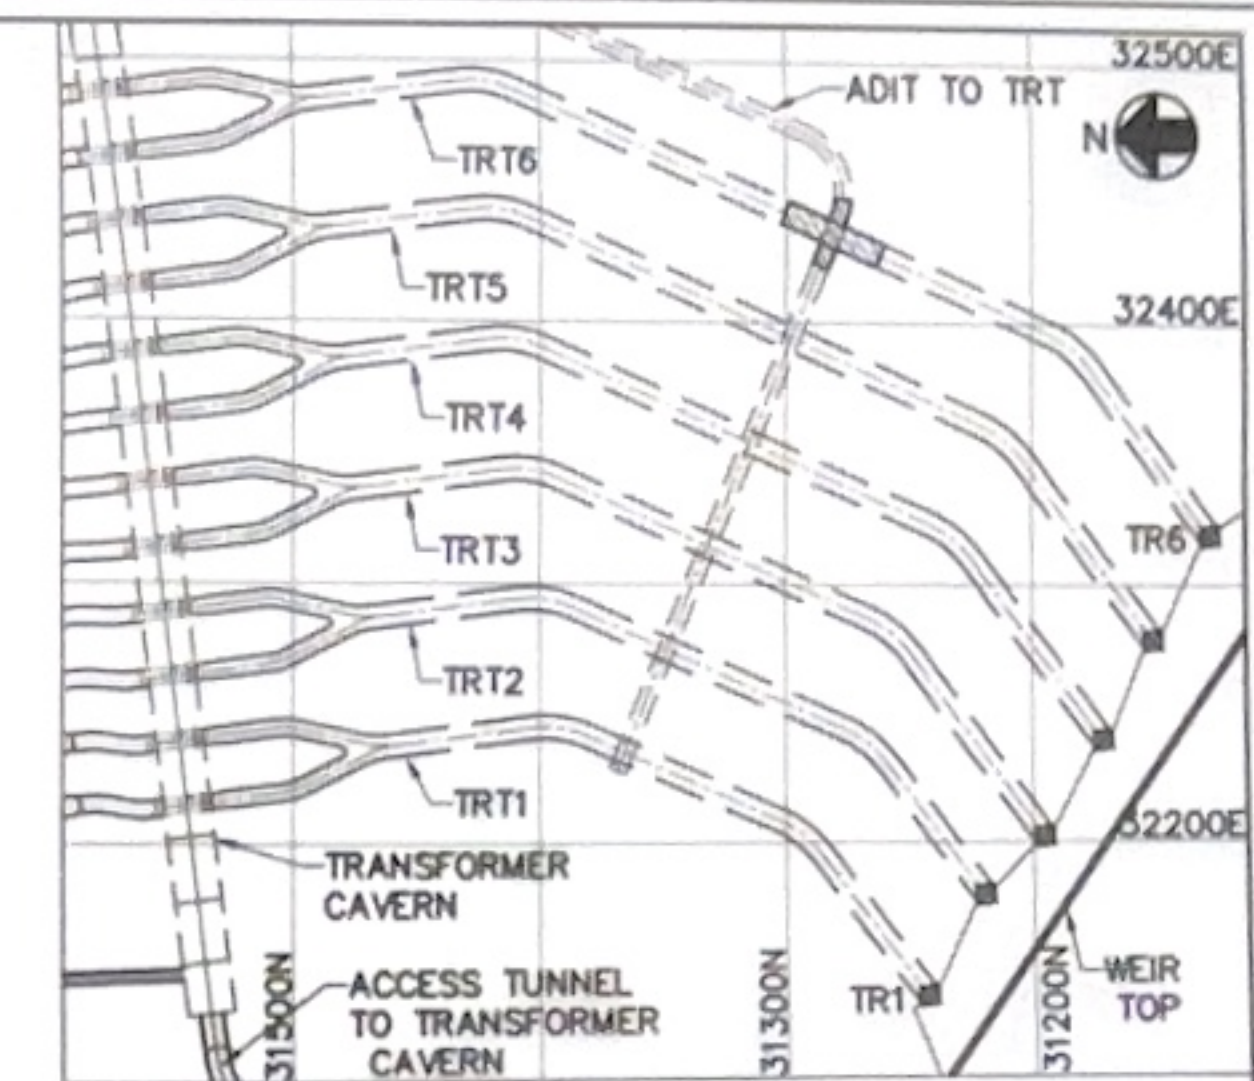
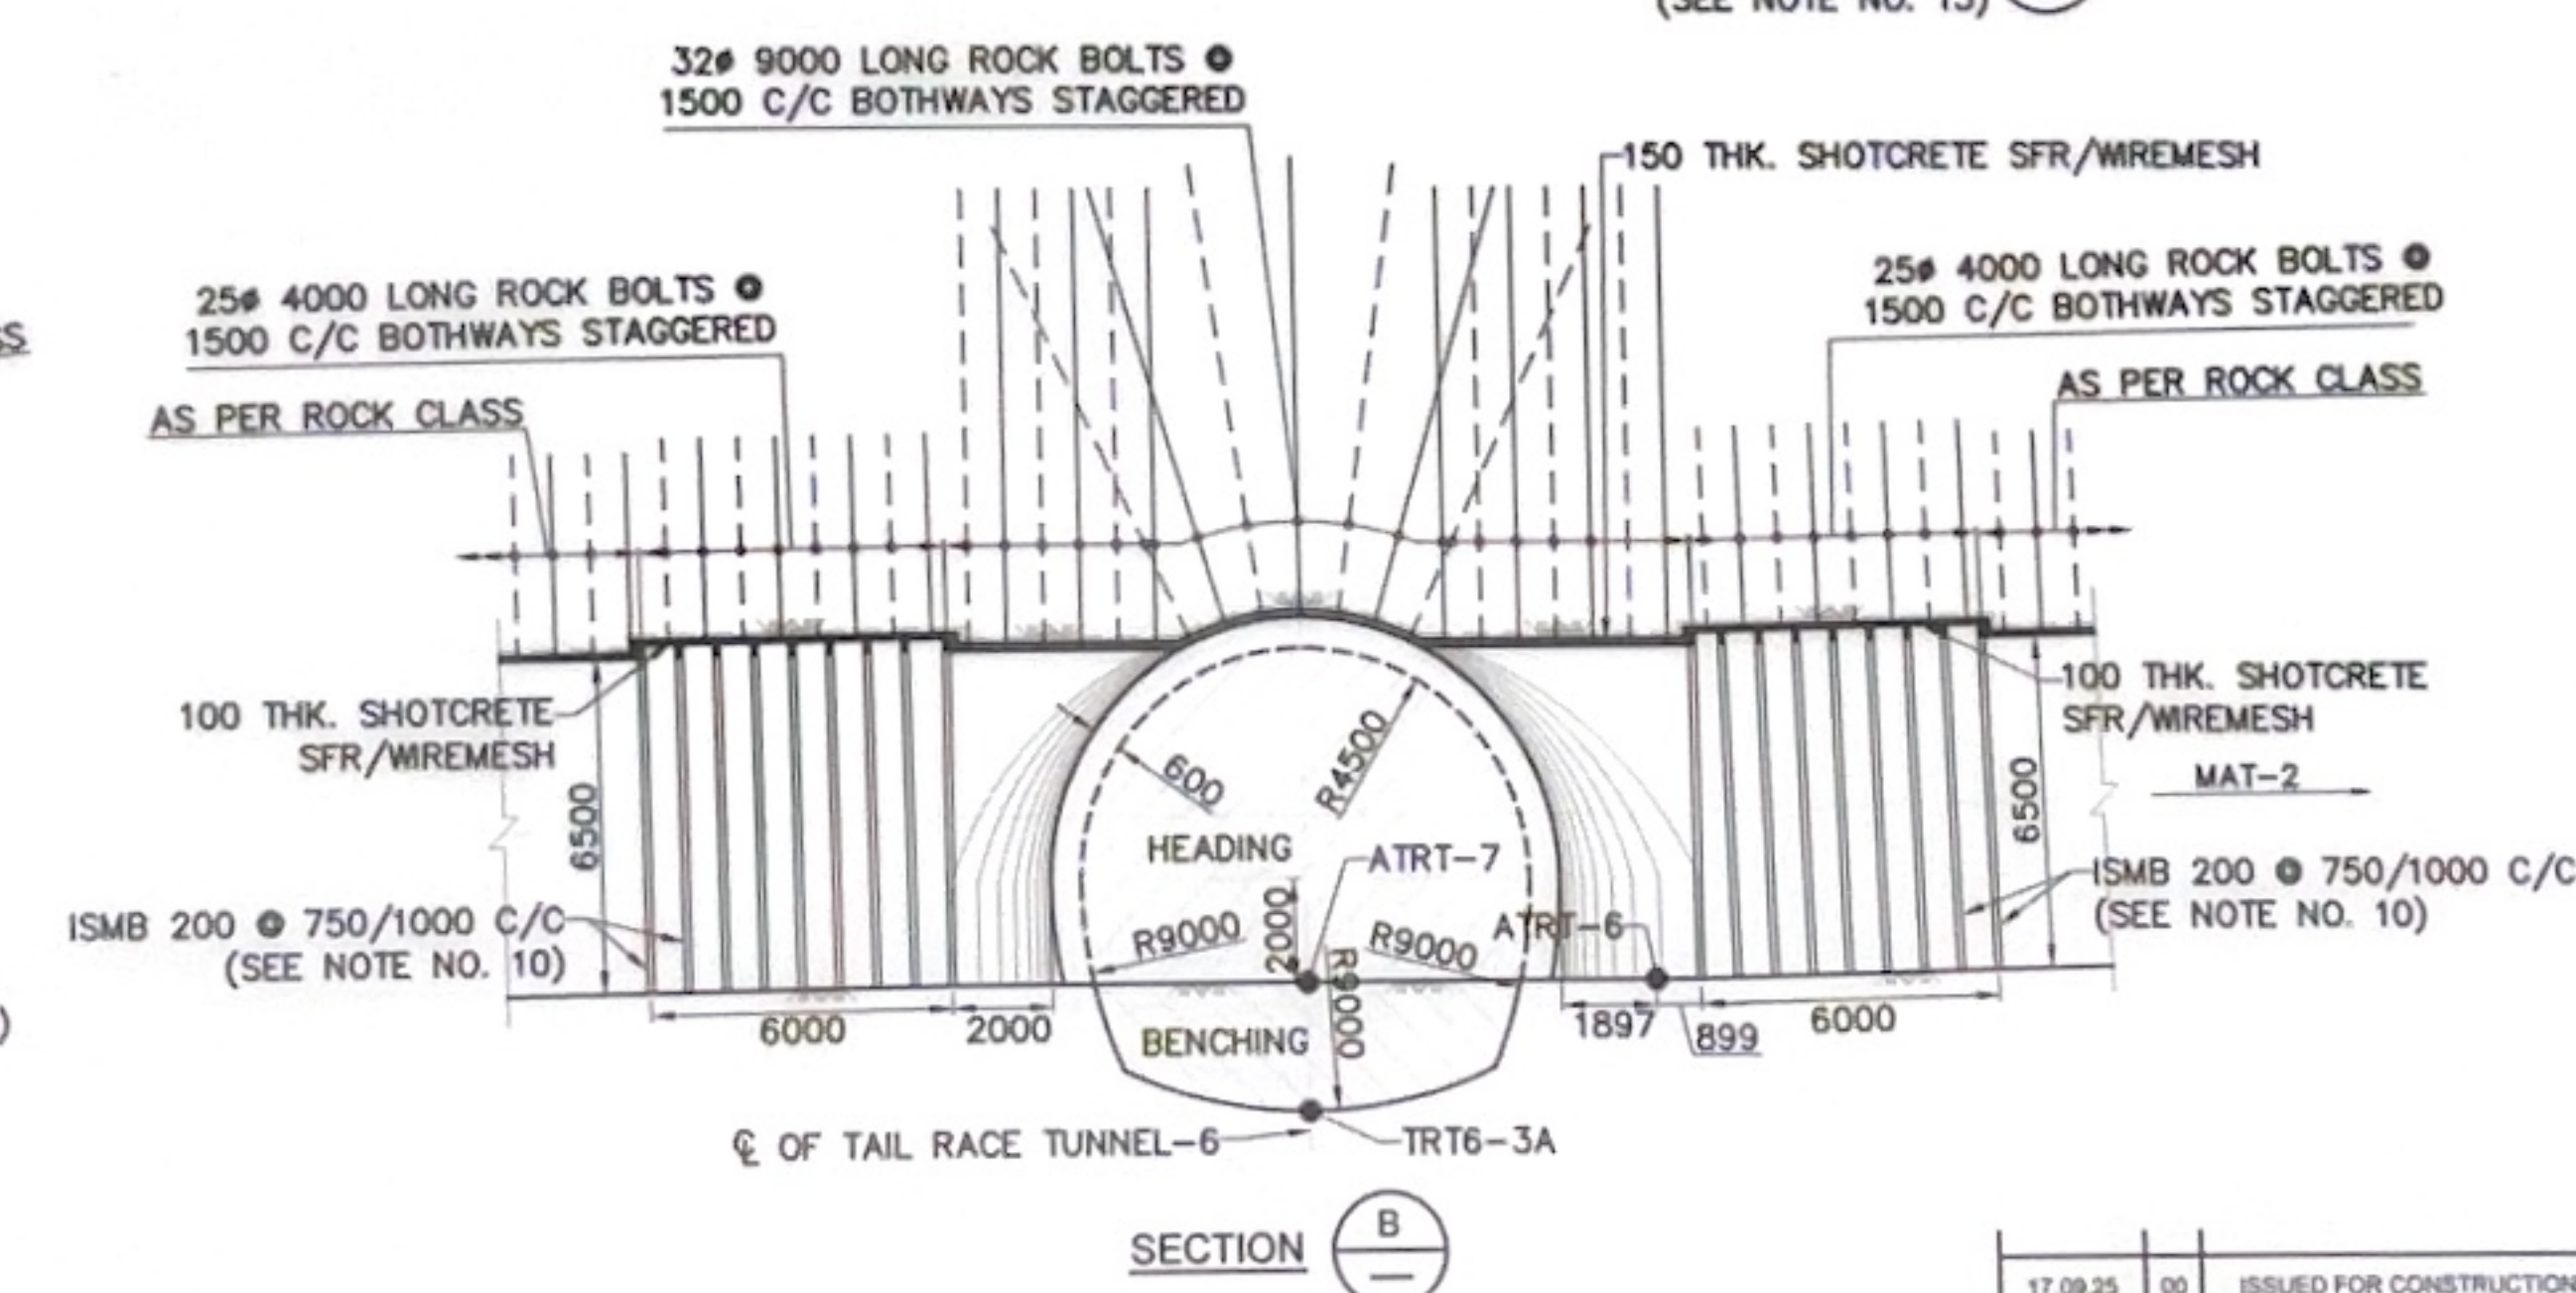
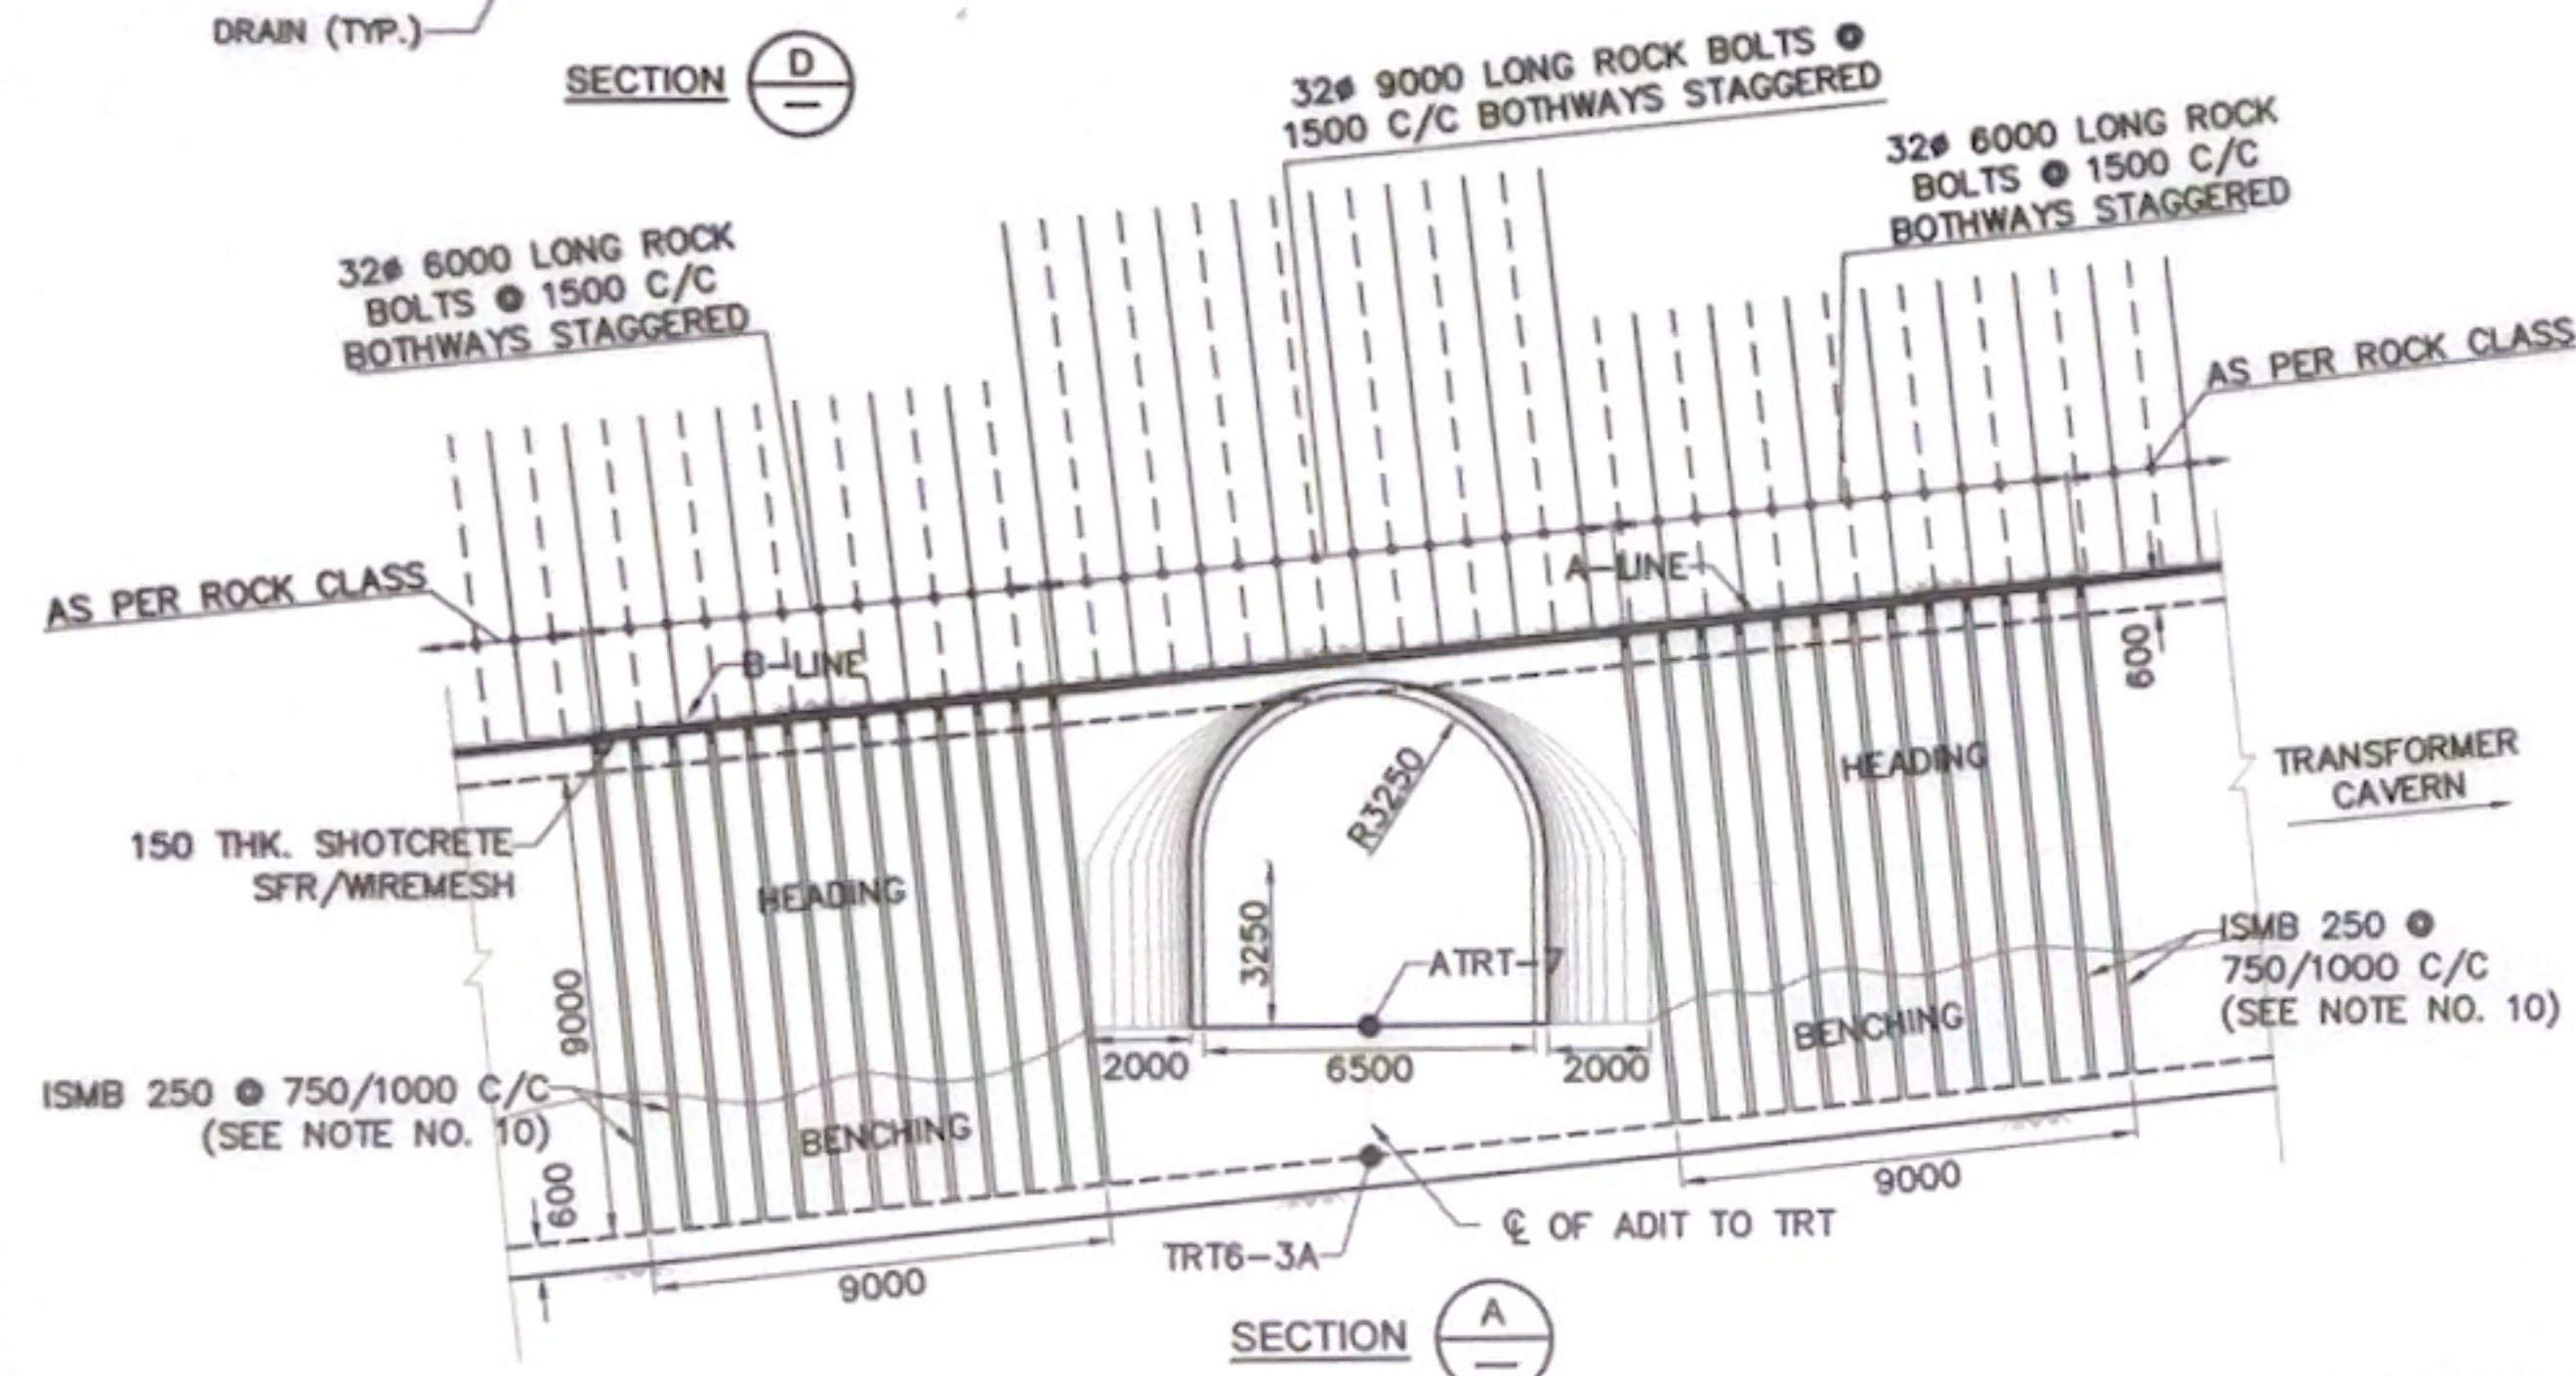
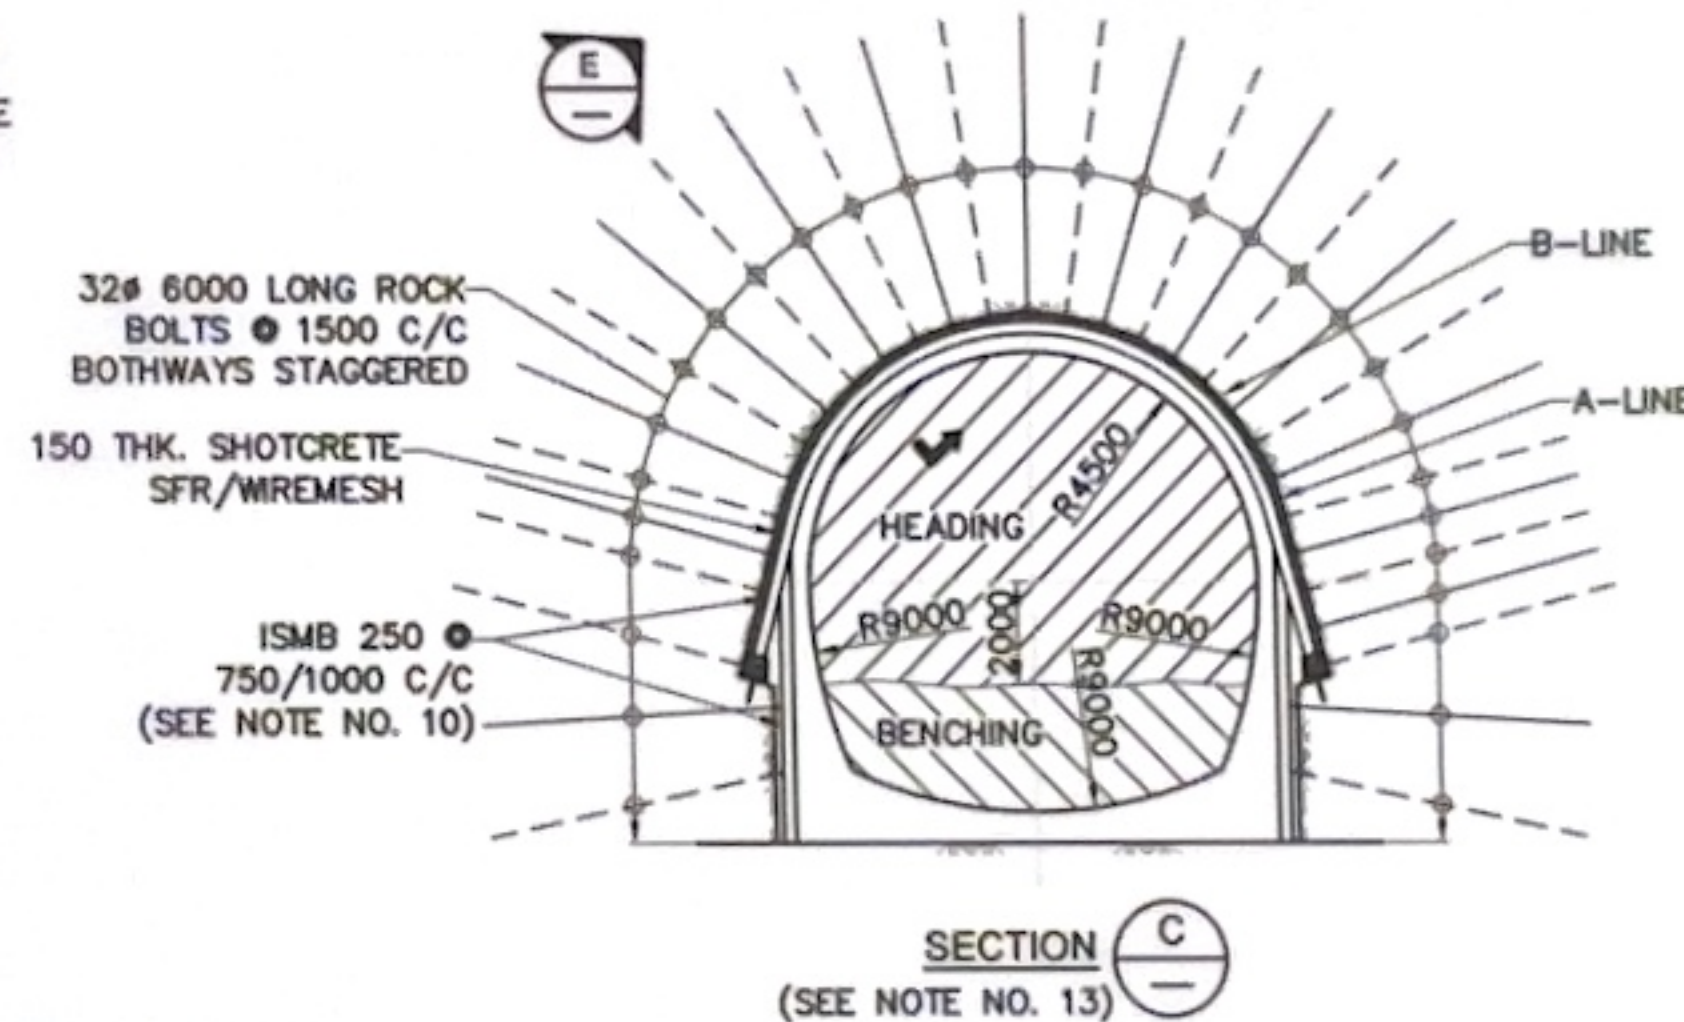


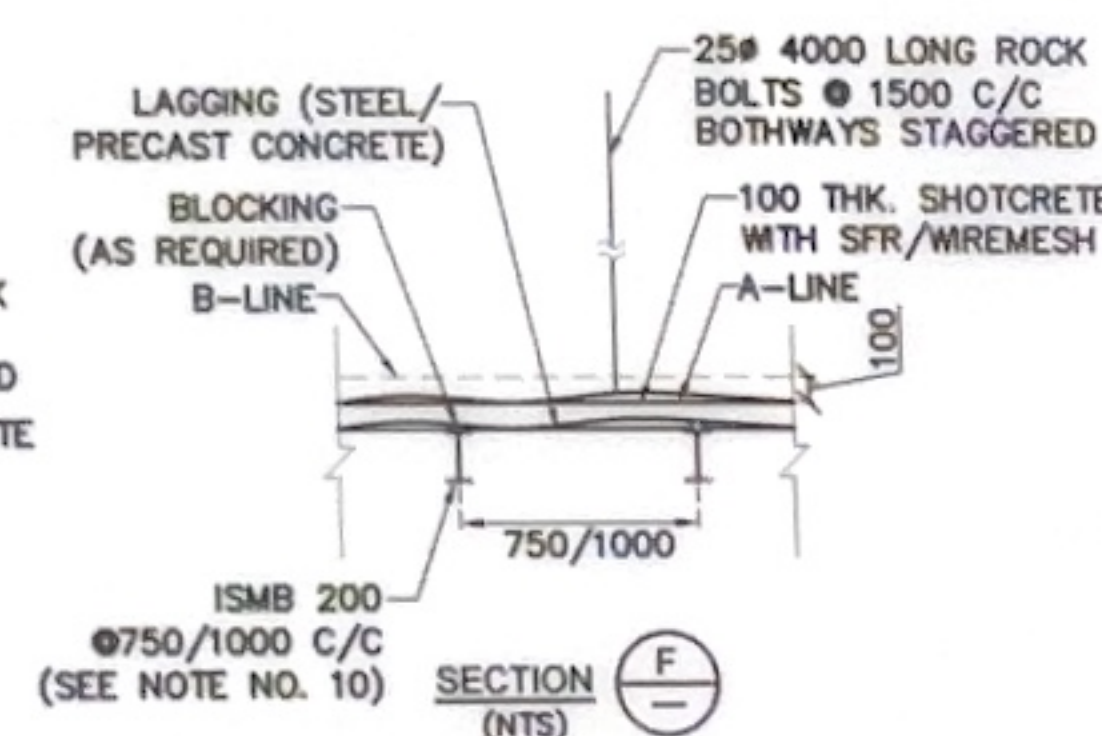

TYPICAL PLAN OF JUNCTION FOR TAIL RACE TUNNEL - 2 TO 5

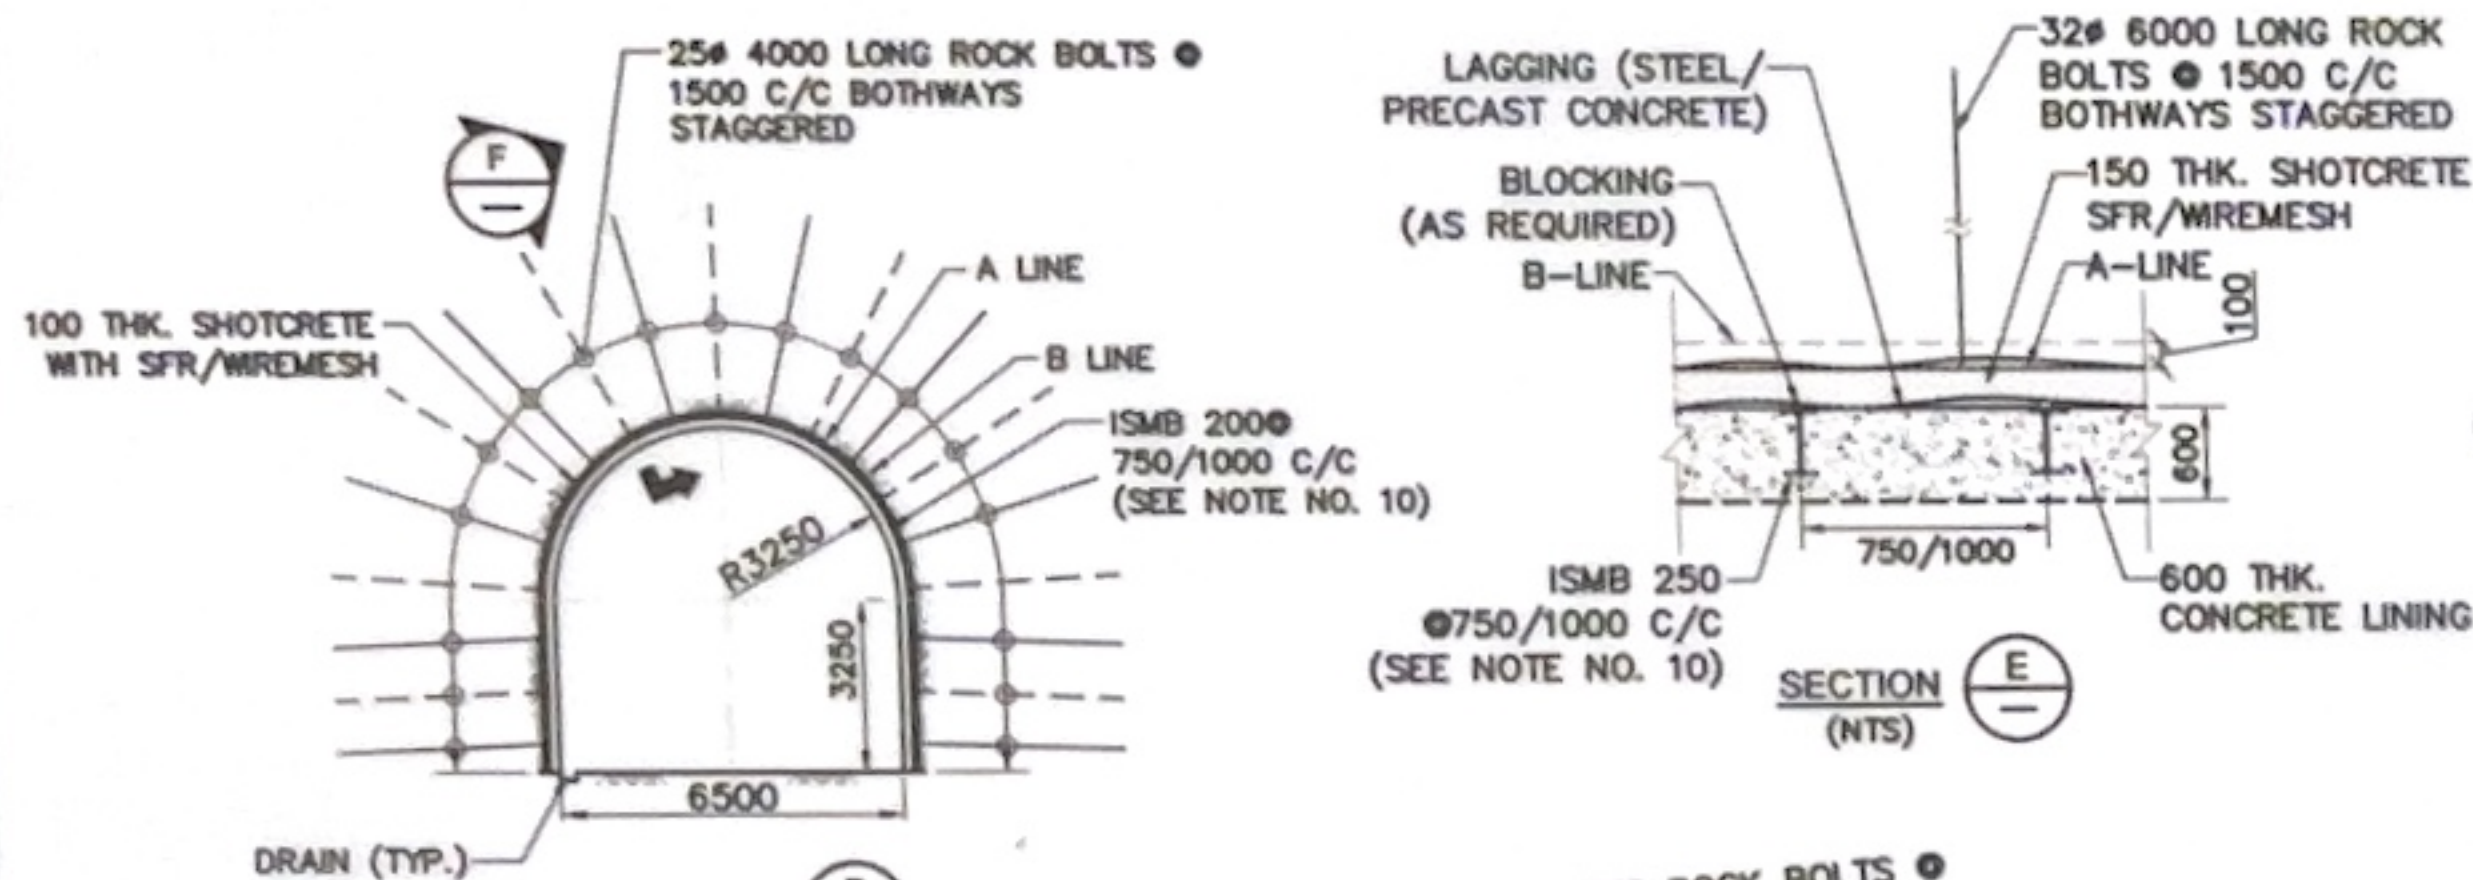

KEY PLAN
(NTS)


NOTES:-


1. सभी माप मिलीमीटर में तथा ऊंचाई मीटर में दिए गए हों।
ALL DIMENSIONS ARE IN MILLIMETERS AND LEVELS IN METERS.
2. THE DEFINITION OF 'A' & 'B' LINE AND VARIOUS CLASSES OF EXCAVATION SHOWN SHALL BE AS PER SECTION B.3 OF TECHNICAL SPECIFICATION.
3. MINOR MODIFICATION IN THE LENGTH, ORIENTATION, PATTERN AND LOCATION OF ROCK ANCHORS/BOLTS MAY BE DONE TO SUIT THE SITE CONDITIONS WITH THE APPROVAL OF ENGINEER-IN-CHARGE.
4. STEEL RIB SHALL BE CONFORMING TO SECTION B.4 OF TECHNICAL SPECIFICATION. SPACING OF STEEL RIBS SHOWN MAY BE MODIFIED TO SUIT THE SITE CONDITIONS WITH THE APPROVAL OF ENGINEER-IN-CHARGE.
5. ROCK ANCHORS/BOLTS SHOWN IN THE DRAWING SHALL BE CONFORMING TO SECTION B.4 OF TECHNICAL SPECIFICATION.
6. REQUIREMENT OF 45 MM DIA. 5000 LONG (INTO ROCK) PRESSURE RELIEF HOLES WITH 36 MM DIA. PERFORATED PVC PIPES AS PER SECTION B.7 OF TECHNICAL SPECIFICATION WILL BE DETERMINED BY ENGINEER-IN-CHARGE TO SUIT THE SITE CONDITION.
7. SHOTCRETE SHOWN ON DRAWING SHALL BE APPLIED AS SPECIFIED IN SECTION B.5 OF TECHNICAL SPECIFICATION.
8. STEEL LAGGING OR PRE CAST CONCRETE LAGGING AS SPECIFIED IN SECTION B.4 OF TECHNICAL SPECIFICATIONS SHALL BE USED AT THE JUNCTION WITH THE APPROVAL OF ENGINEER-IN-CHARGE.
9. UNDERGROUND EXCAVATION INCLUDING PROTECTION OF TUNNEL INVERT SHALL BE CONFIRMING TO SECTION B.3 OF TECHNICAL SPECIFICATION.
10. THE SPACING OF STEEL RIBS AT THE JUNCTION SHALL BE @ 1000 C/C UPTO CLASS-IV AND @ 750 IN CLASS-VA & VB. THE SPACING OF RIBS MAY BE MODIFIED TO SUIT THE SITE CONDITIONS WITH THE APPROVAL OF ENGINEER-IN-CHARGE.
11. IF ADDITIONAL ROCK SUPPORT MEASURES ARE REQUIRED BASED ON THE SITE SPECIFIC CONDITIONS THEN REFER DRG. NO. NHDB-4BC4-41-DD-1007.
12. FOR CONCRETE & REINFORCEMENT OF JUNCTION, REFER SEPARATE DRAWINGS.
13. FOR STEEL RIBS DETAILS IN TAIL RACE TUNNEL AT THE JUNCTION REFER SEPARATE DRAWING.
14. FOR ROCK SUPPORTS OF ADIT TO TRT OUTSIDE THE LIMITS OF THE JUNCTION REFER DRG. NO. NHDB-4DC4 -41-DD-1003.
15. FOR STEEL RIBS AND LATTICE GIRDER DETAILS IN ADIT TO TRT REFER DRG. NO. NHDB-4DC4-41-DD-1004 & 1005.
16. FOR ROCK SUPPORTS OF TAIL RACE TUNNEL OUTSIDE THE LIMITS OF THE JUNCTION REFER SEPARATE DRAWING.

REFERENCE DRAWING:-

1. NHDB-4DC4-41-DD-0006
2. NHDB-4DC4-41-DD-0007

SCALE :

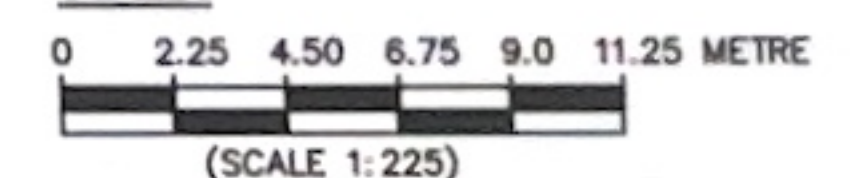

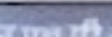	एन एच पी सी लिमिटेड (एकमात्र सरकार का एक सार्वजनिक उद्योग) NHPC Limited (A GOVT. OF INDIA INNOVATIVE ENTERPRISE) दिबांग बहुउद्देशीय परियोजना DIBANG MULTIPURPOSE PROJECT
---	--

TAIL RACE TUNNEL
TAIL RACE TUNNEL-6 & ADIT TO TAIL RACE TUNNEL
JUNCTION
ROCK SUPPORT DETAILS

17.09.25	00	ISSUED FOR CONSTRUCTION	BY CH APP	DATE 17.09.25	SEP 2025	DRG NO. 41 DD	1008	00
DATE	NO	REVISION OR ISSUES	BY CH APP	DATE	SEP 2025	DRG NO.	NHDB	4DC4
DESIGN MEMO NO.								