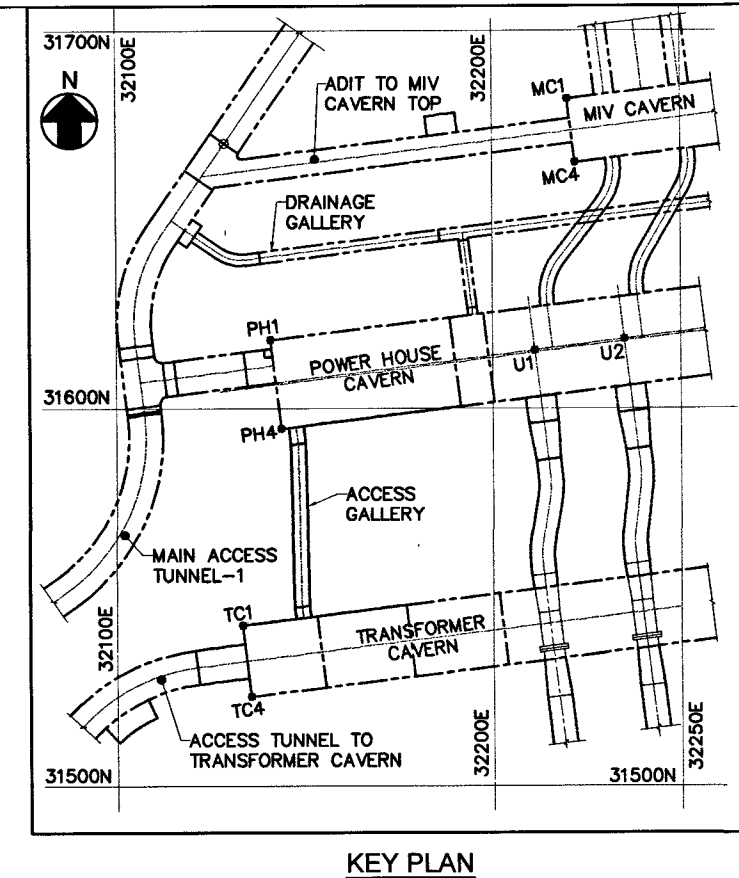
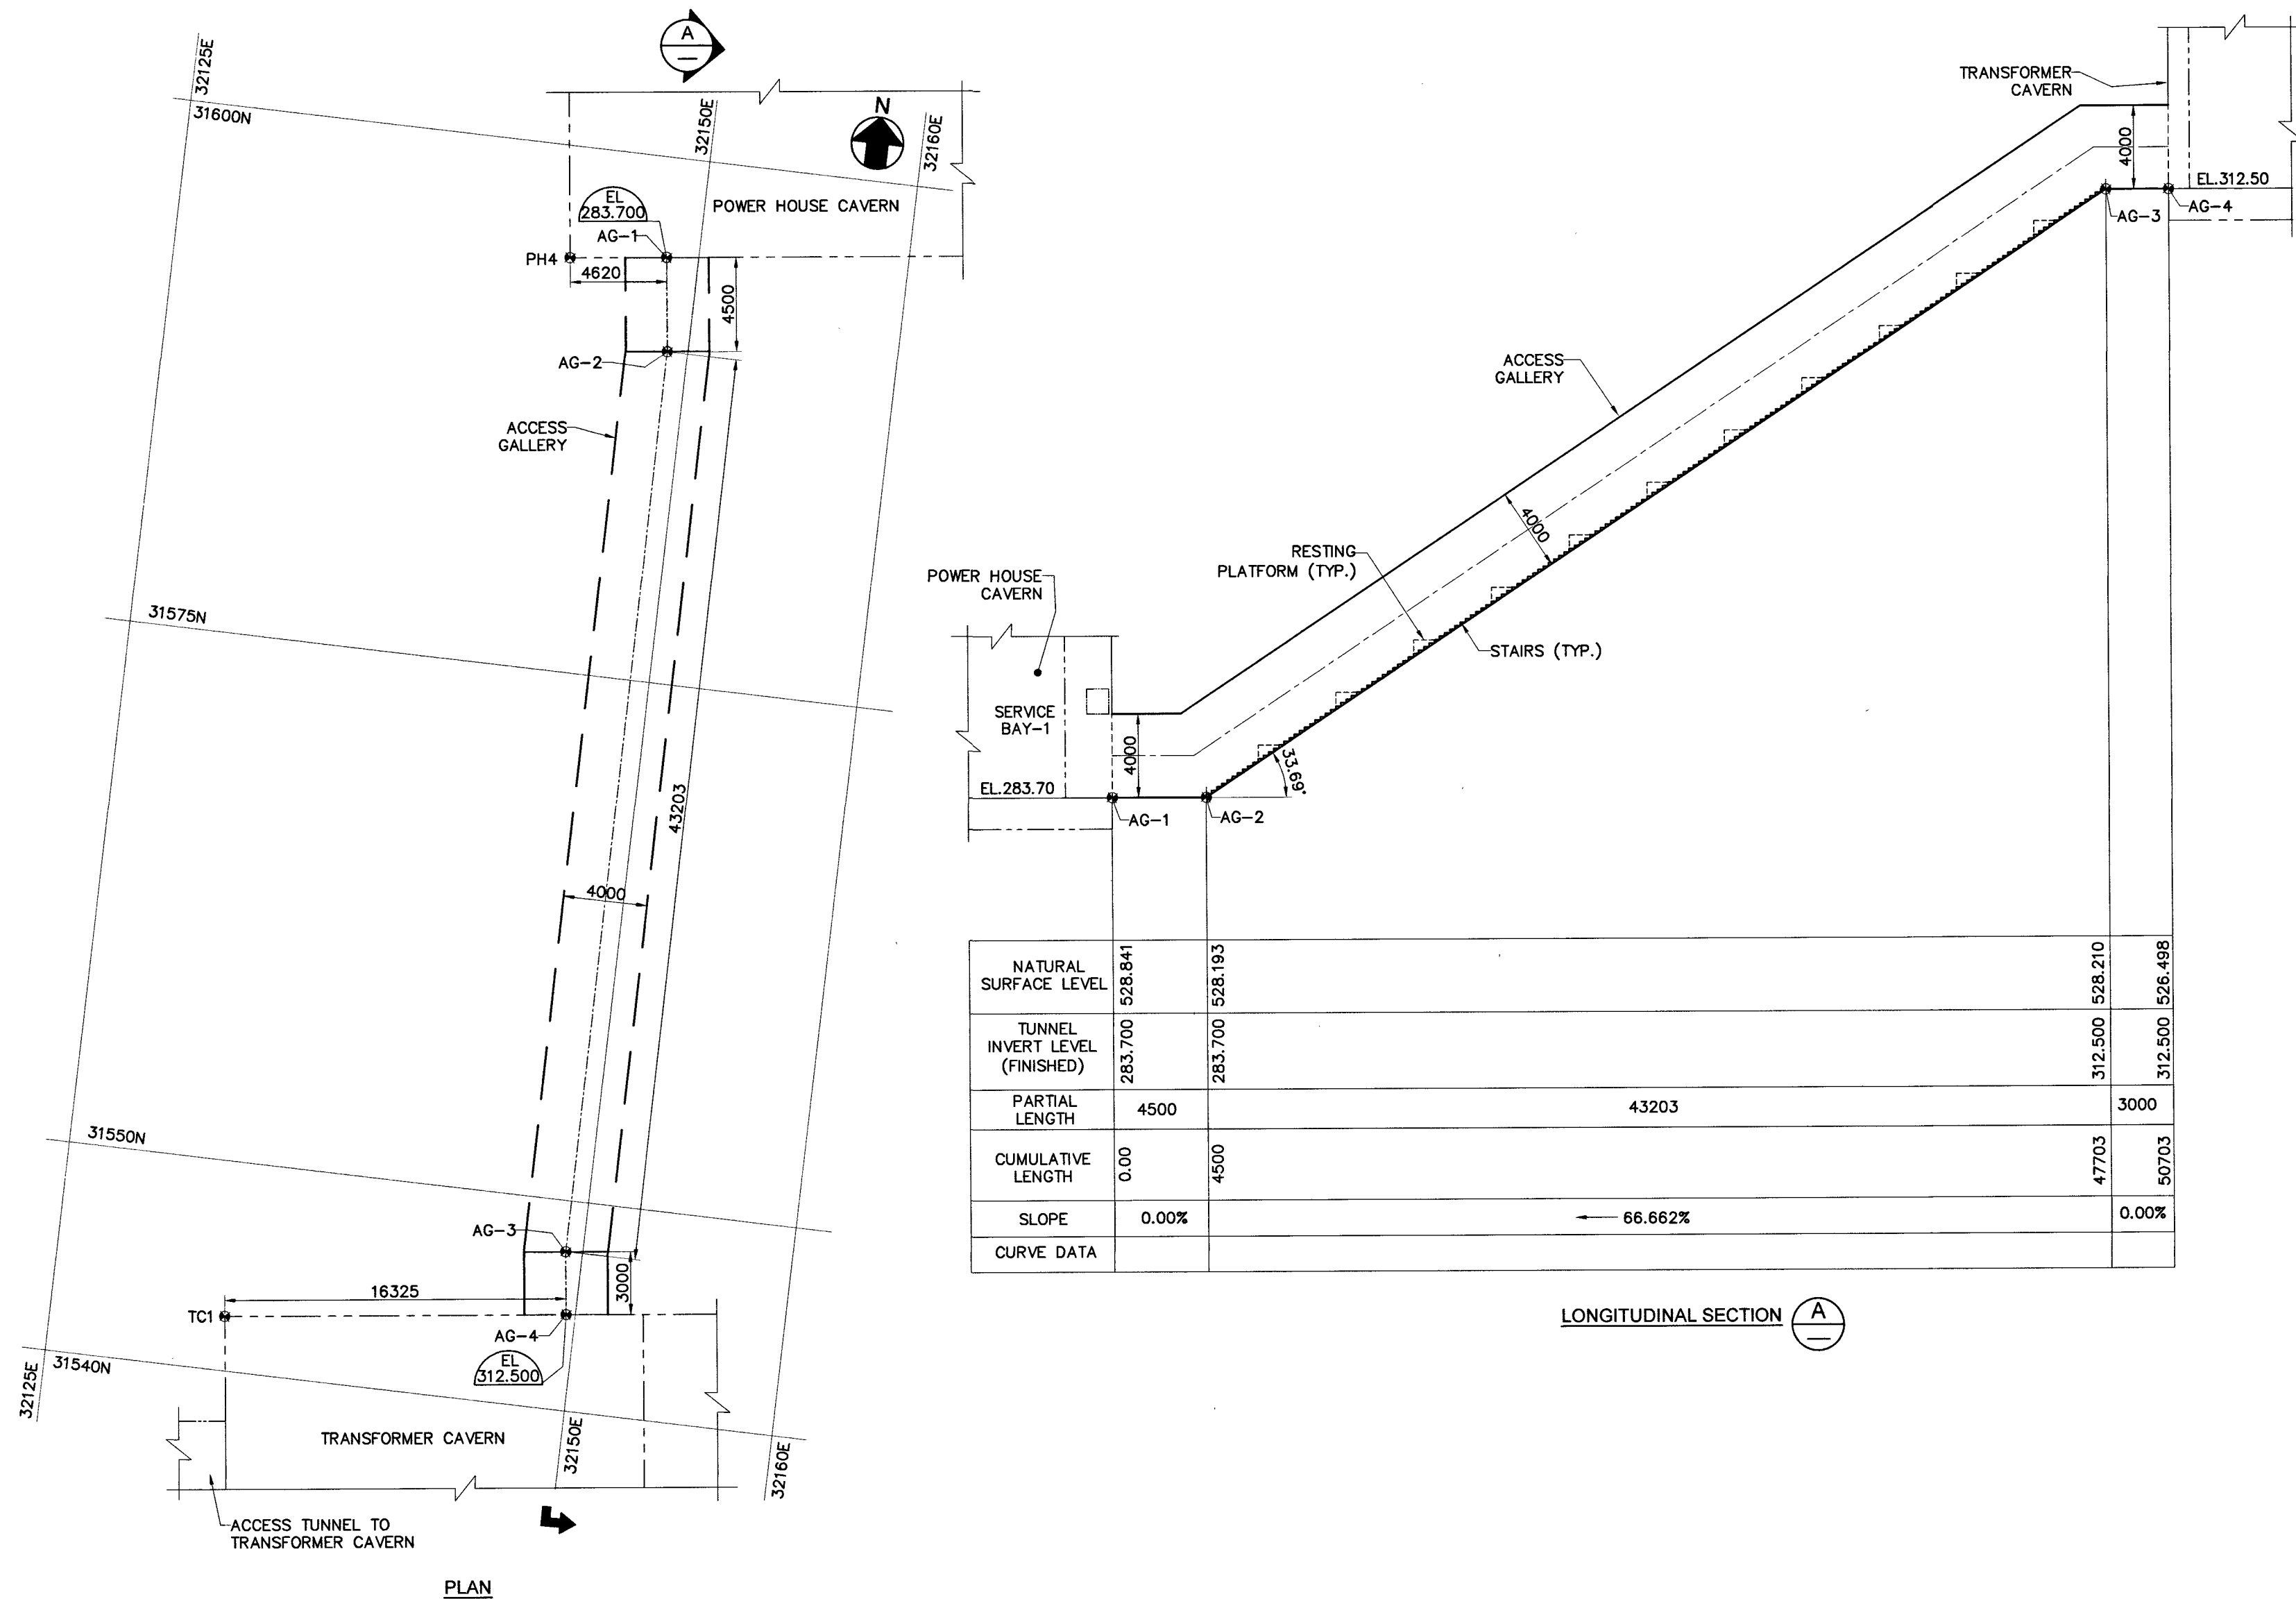


**NOTES:-**


- सभी माप मिलीमीटर में, ग्रिड तथा ऊचाई मीटर में दिए गए हैं।
ALL DIMENSIONS ARE IN MILLIMETRE, GRIDS AND ELEVATIONS ARE IN METRE
- GRIDS AND THE VALUES OF NSL HAVE BEEN REPRODUCED FROM S.O.I. SHEET. THE ACCURACY OF THE SAME SHALL BE ESTABLISHED WITH EXISTING S.O.I. BENCH MARK AT SITE BEFORE ADOPTING CO-ORDINATES.
- THE LEVELS SHOWN CORRESPONDS TO THE FINISHED SURFACES/LINES. FOR LEVELS OF EXCAVATION REFER EXCAVATION DRAWING.
- FOR EXCAVATION AND ROCK SUPPORT DETAILS REFER DRAWING NO. NHDB-4CC4-41-DD-1031.
- THIS DRAWING SHALL BE READ IN CONJUNCTION WITH DRG. NO. NHDB-1AC4-41-DD-0001 & NHDB-4AC4-41-DD-0001.

REFERENCE:

- NHDB-1AC4-41-DD-0001.
- NHDB-4AC4-41-DD-0001

CO-ORDINATES:-
(ACCESS GALLERY)

POINTS	NORTHING IN METRE	EASTING IN METRE
PH4	31594.672	32143.900
TC1	31542.599	32133.358
AG-1	31595.235	32148.486
AG-2	31590.769	32149.034
AG-3	31547.566	32149.195
AG-4	31544.589	32149.561

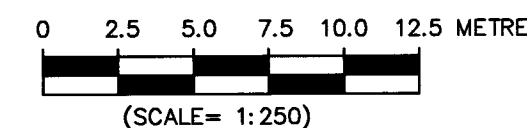

30.04.2026	00	ISSUED FOR CONSTRUCTION	BY: CH. APP.	DATE	NO.	REVISION OR ISSUES	BY: CH. APP.	DATE	NO.	REVISION OR ISSUES	BY: CH. APP.	DATE	NO.	REVISION OR ISSUES	BY: CH. APP.
30.04.2026	00	ISSUED FOR CONSTRUCTION	BY: CH. APP.	DATE	NO.	REVISION OR ISSUES	BY: CH. APP.	DATE	NO.	REVISION OR ISSUES	BY: CH. APP.	DATE	NO.	REVISION OR ISSUES	BY: CH. APP.