


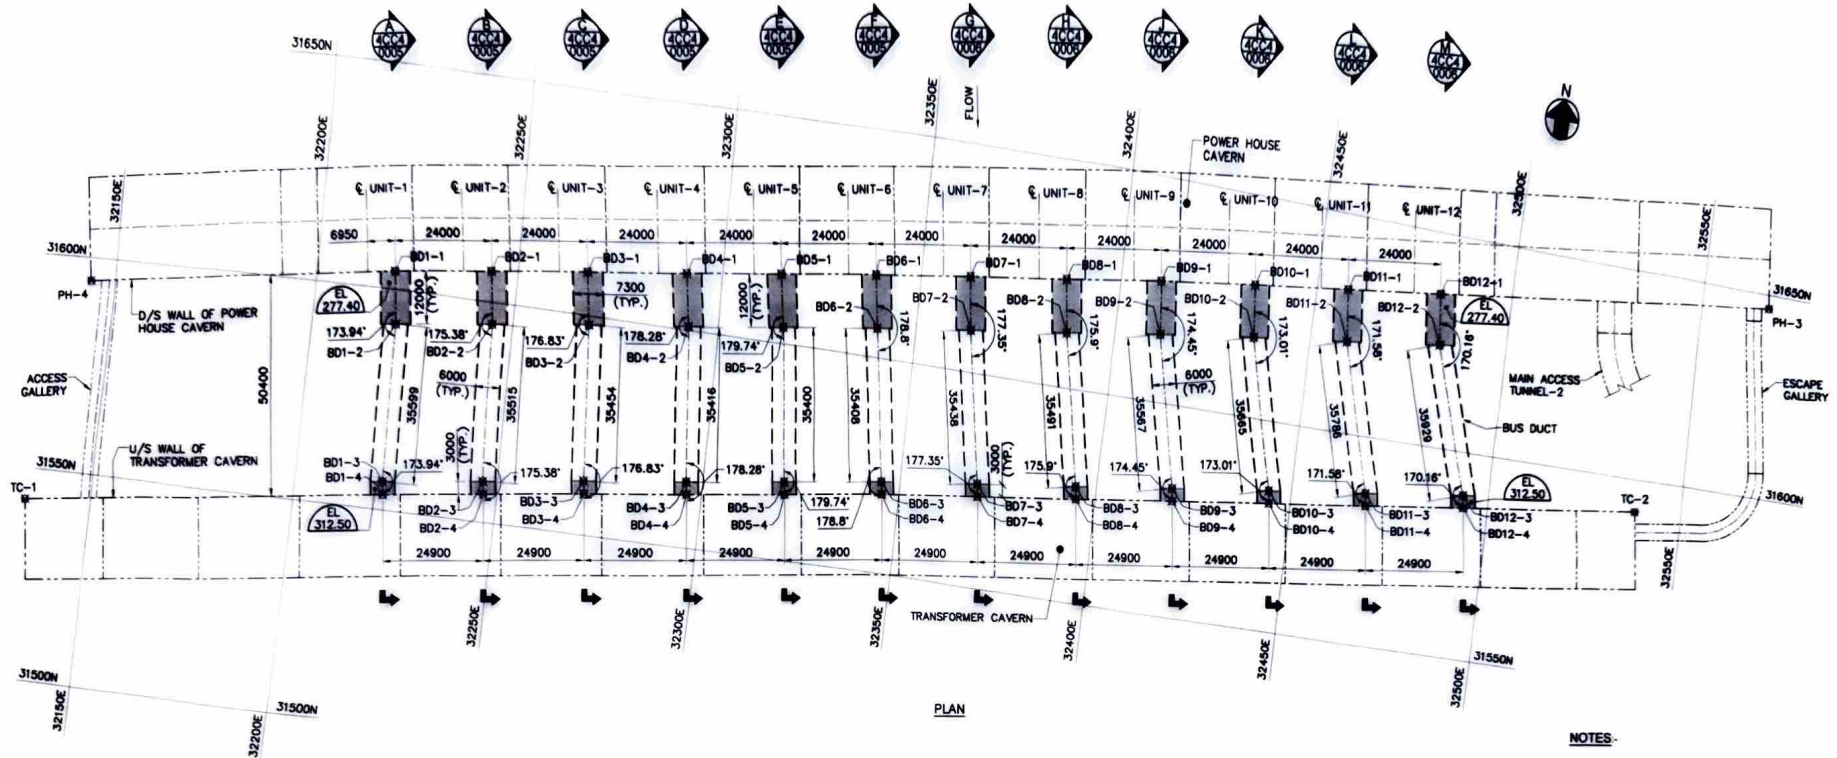

CO-ORDINATES-

POINTS	NORTHING (IN METRE)	EASTING (IN METRE)
PH3	31646.710	32567.717
PH4	31594.672	32143.900
TC1	31542.599	32133.358
TC2	31592.298	32538.118
BD1-1	31603.976	32219.671
BD1-2	31592.065	32221.133
BD1-3	31556.471	32221.716
BD1-4	31553.493	32222.081
BD2-1	31606.901	32243.492
BD2-2	31594.990	32244.955
BD2-3	31559.505	32246.430
BD2-4	31556.528	32246.796
BD3-1	31609.825	32267.313
BD3-2	31587.915	32268.776
BD3-3	31562.540	32271.144
BD3-4	31559.562	32271.510
BD4-1	31612.750	32291.134
BD4-2	31600.840	32292.597
BD4-3	31565.574	32295.859
BD4-4	31562.597	32296.224

CO-ORDINATES-

POINTS	NORTHING (IN METRE)	EASTING (IN METRE)
BD5-1	31615.675	32314.955
BD5-2	31603.765	32316.418
BD5-3	31568.609	32320.573
BD5-4	31565.631	32320.939
BD6-1	31618.600	32338.777
BD6-2	31606.689	32340.239
BD6-3	31571.643	32345.288
BD6-4	31568.666	32345.653
BD7-1	31621.525	32362.598
BD7-2	31609.614	32364.060
BD7-3	31574.678	32370.002
BD7-4	31571.700	32370.368
BD8-1	31624.450	32386.419
BD8-2	31612.539	32387.881
BD8-3	31577.713	32394.716
BD8-4	31574.735	32395.082

CO-ORDINATES-

POINTS	NORTHING (IN METRE)	EASTING (IN METRE)
BD9-1	31627.375	32410.240
BD9-2	31615.464	32411.702
BD9-3	31580.747	32419.431
BD9-4	31577.769	32419.796
BD10-1	31630.299	32434.061
BD10-2	31618.389	32435.523
BD10-3	31583.782	32444.145
BD10-4	31580.804	32444.511
BD11-1	31633.224	32457.882
BD11-2	31621.314	32459.344
BD11-3	31586.816	32468.860
BD11-4	31583.839	32469.225
BD12-1	31636.149	32481.703
BD12-2	31624.239	32483.166
BD12-3	31589.851	32493.574
BD12-4	31586.873	32493.940

NOTES:-

1. सभी कार निर्माण में दिए गए अर्थों में दिए गए हैं।
ALL DIMENSIONS ARE IN MILLIMETRE, GRIDS AND ELEVATIONS ARE IN METRE.
2. GRIDS HAVE BEEN REPRODUCED FROM S.O.I. TOPO SHEET. THE ACCURACY OF THE GRID SYSTEM SHALL BE ESTABLISHED WITH EXISTING S.O.I. BENCH MARK AT SITE BEFORE ADOPTING COORDINATES.
3. THE LEVELS SHOWN CORRESPONDS TO THE FINISHED SURFACES/LINES. FOR LEVELS OF EXCAVATION REFER EXCAVATION DRAWING.
4. FOR EXCAVATION AND ROCK SUPPORT DETAILS REFER SEPARATE DRAWINGS.
5. THIS DRAWING SHALL BE READ IN CONJUNCTION WITH DRG. NO. NHDB-4AC4-41-DD-0001 & NHDB-4AC4-41-DD-1003.
6. FOR INTERDEPENDENT EXCAVATION SEQUENCE REFER DRAWING NO. NHDB-4AC4-41-DD-1003.

REFERENCE DRAWINGS:-

1. NHDB-4AC4-41-DD-0001.
2. NHDB-4AC4-41-DD-1003.

0 9 18 27 36 45 METRE
(SCALE = 1:500)

एन एच पी सी लिमिटेड
NHPC Limited
प्रधान कार्यकारी अधिकारी
DIBANG MULTIPURPOSE PROJECT

POWER HOUSE
BUS DUCTS
SETTING OUT

(SHEET 1 OF 3)

25.06.2026	00	ISSUED FOR CONSTRUCTION	BY	CH	APPROVED	RECOMMENDED	REVIEWED	APPROVED	REVIEWED
DATE	NO	REVISION OR ISSUES	BY	CH	APPROVED	RECOMMENDED	REVIEWED	APPROVED	REVIEWED
DATE	NO	REVISION OR ISSUES	BY	CH	APPROVED	RECOMMENDED	REVIEWED	APPROVED	REVIEWED
JUN 2026	00								
DATE	NO	REVISION OR ISSUES	BY	CH	APPROVED	RECOMMENDED	REVIEWED	APPROVED	REVIEWED
JUN 2026	00								