




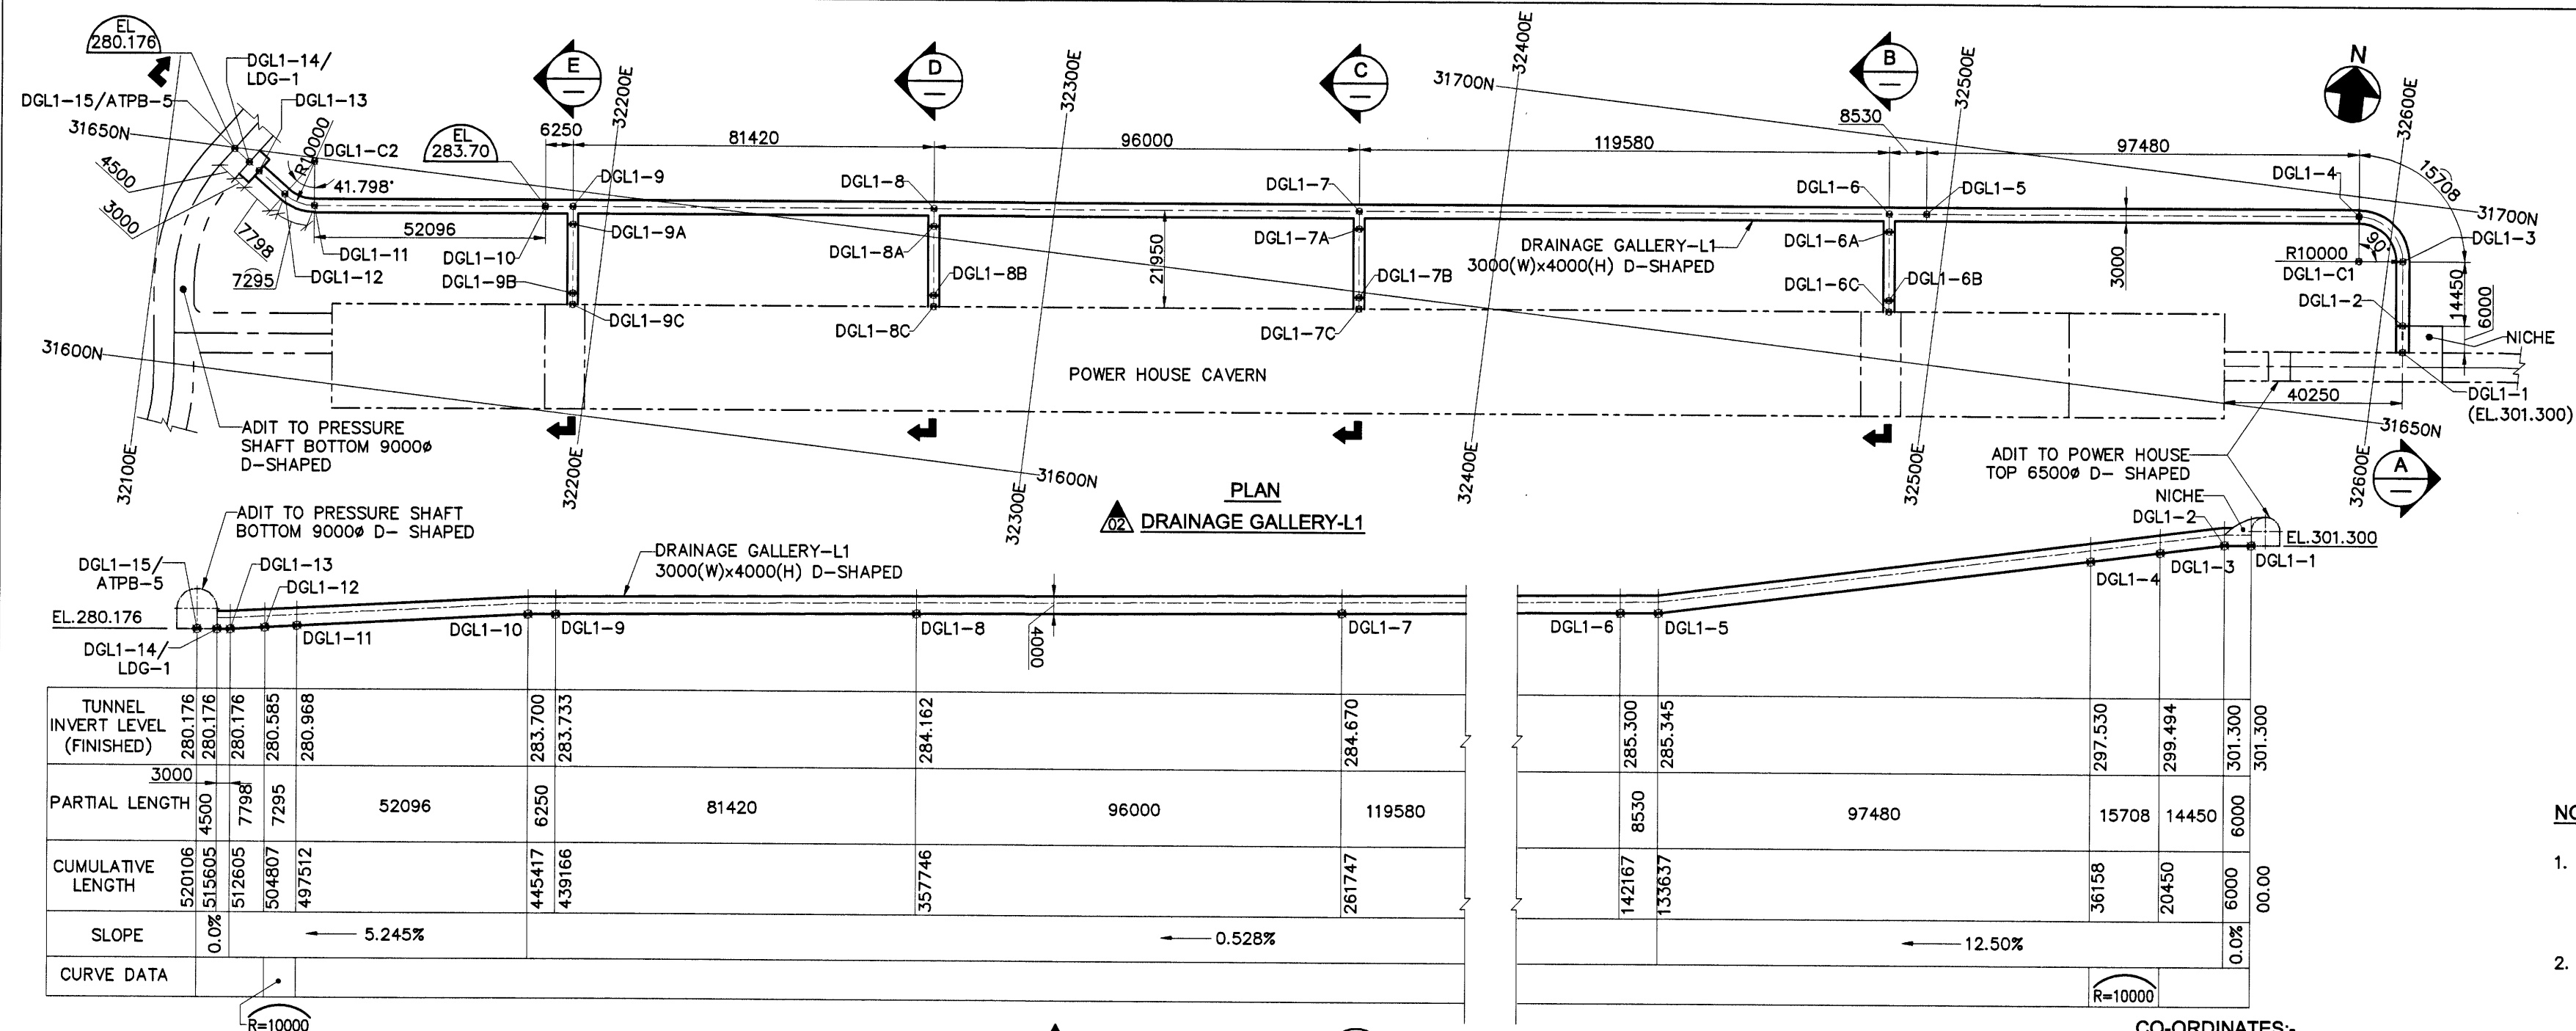


LONGITUDINAL SECTION (A)

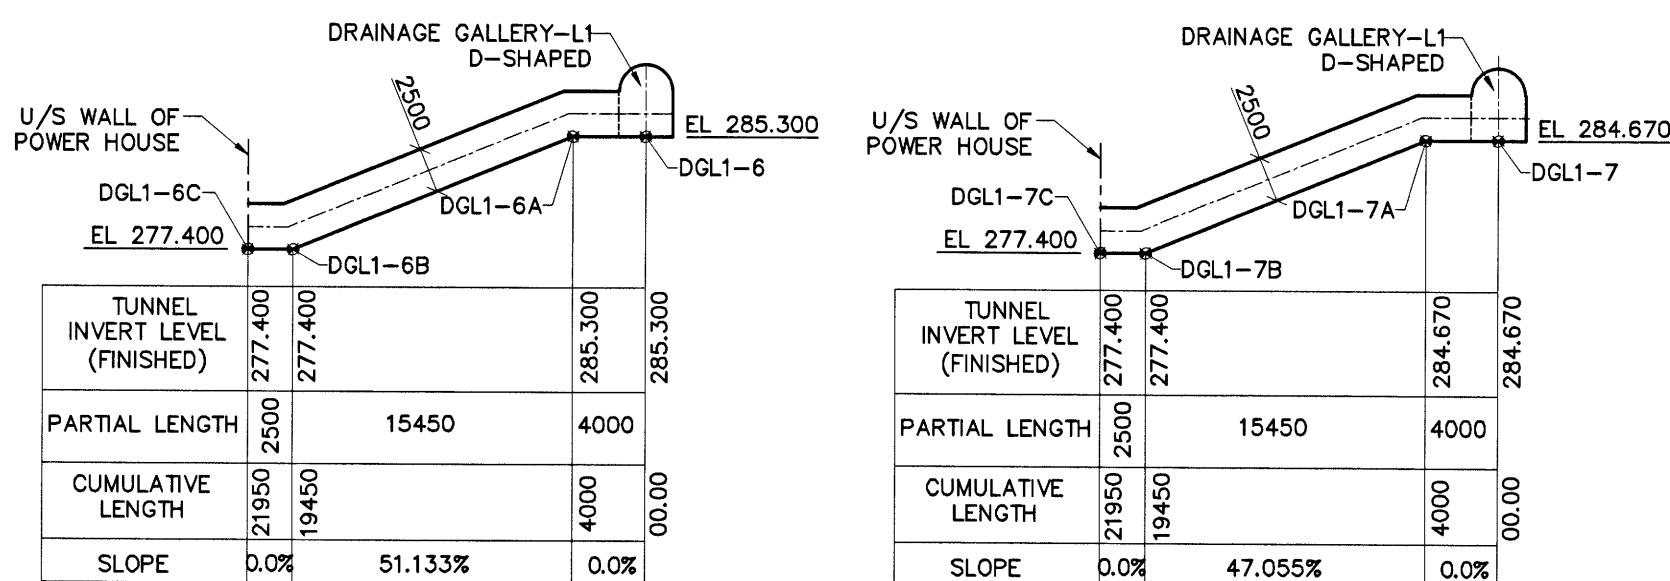


SECTION B (NTS)

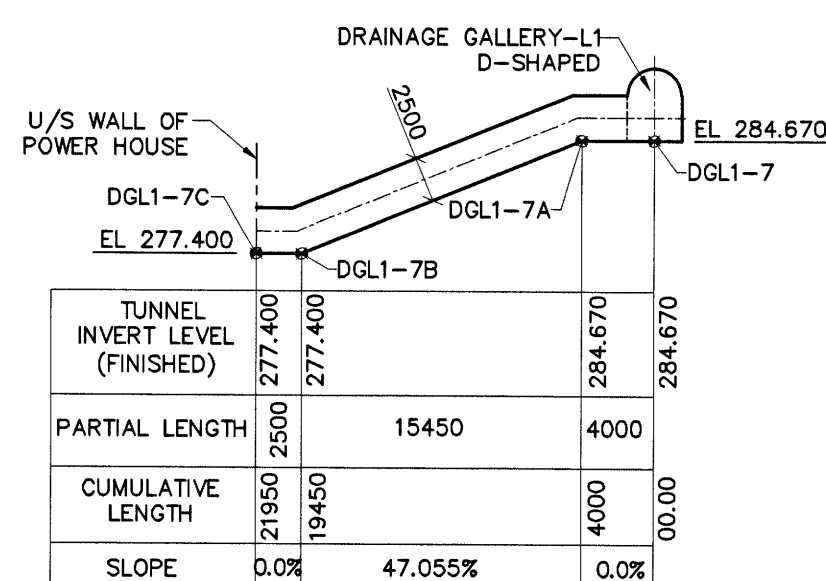


SECTION C (NTS)

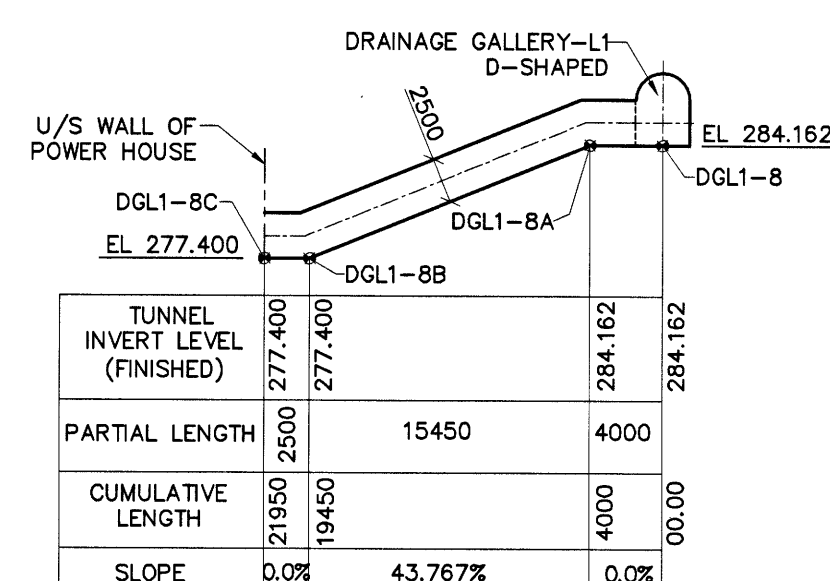

SECTION D (NTS)

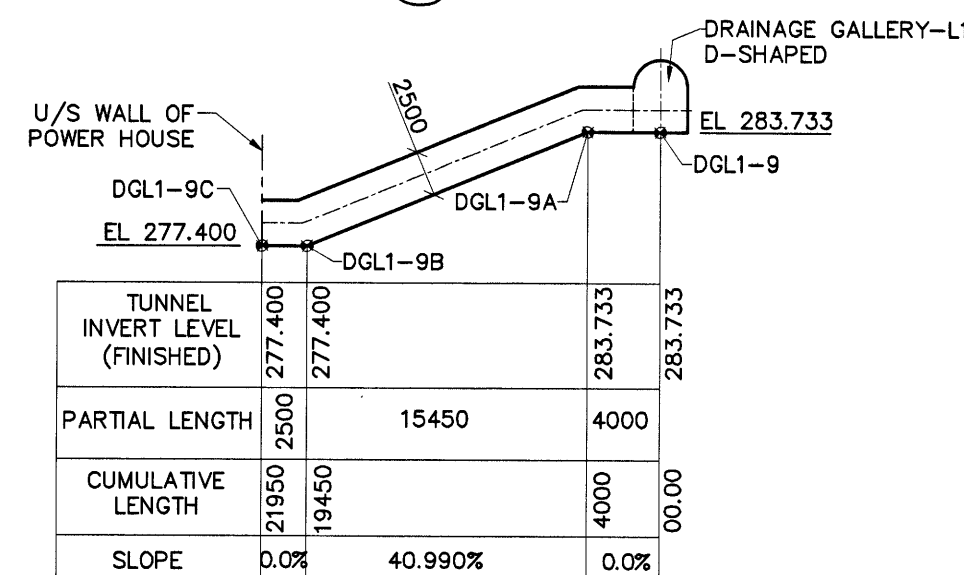

SECTION E (NTS)

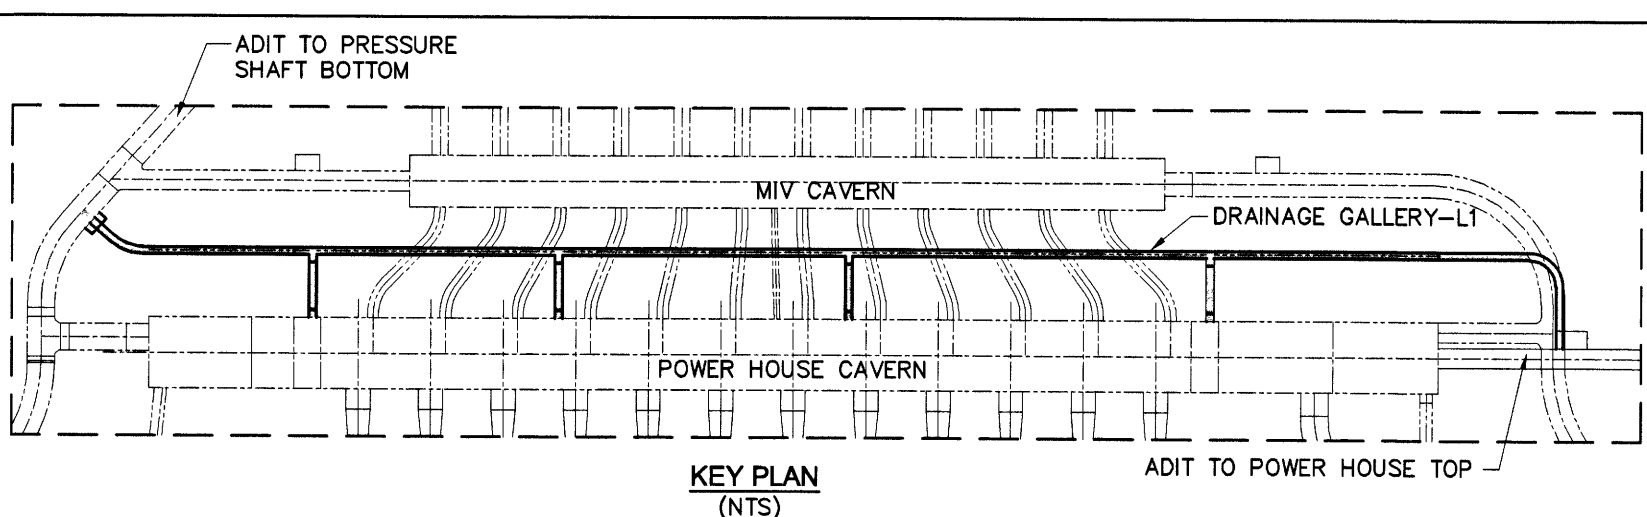

KEY PLAN (NTS)

CO-ORDINATES:-
(DRAINAGE GALLERY-L1)

POINTS	NORTHING IN METRE	EASTING IN METRE
DGL1-1	31666.504	32605.839
DGL1-2	31672.459	32605.108
DGL1-3	31686.801	32603.347
DGL1-4	31695.508	32592.203
DGL1-C1	31685.583	32593.421
DGL1-5	31683.628	32495.450
DGL1-6	31682.589	32486.984
DGL1-7	31668.016	32368.295
DGL1-8	31656.316	32273.011
DGL1-9	31646.394	32192.198
DGL1-10	31645.632	32185.994
DGL1-11	31639.283	32134.287
DGL1-12	31640.997	32127.361
DGL1-C2	31649.209	32133.068
DGL1-13	31645.447	32120.958
DGL1-14 /LDG-1	31647.159	32118.494
DGL1-15/ATPB-5	31649.728	32114.799
DGL1-6A	31678.619	32487.471
DGL1-6B	31663.284	32489.355
DGL1-6C	31660.802	32489.658
DGL1-7A	31664.046	32368.782
DGL1-7B	31648.711	32370.665
DGL1-7C	31646.229	32370.969
DGL1-8A	31652.346	32273.498
DGL1-8B	31637.011	32275.380
DGL1-8C	31634.530	32275.685
DGL1-9A	31642.423	32192.685
DGL1-9B	31627.089	32194.567
DGL1-9C	31624.607	32194.872

NOTES:-

- सभी माप मिलीमीटर में, फिट तथा ऊंचाई मीटर में दिए गए हैं।
ALL DIMENSIONS ARE IN MILLIMETRE, GRIDS AND ELEVATIONS ARE IN METRE
- GRIDS HAVE BEEN REPRODUCED FROM S.O.I. TOPO SHEET. THE ACCURACY OF THE GRID SYSTEM SHALL BE ESTABLISHED WITH EXISTING S.O.I. BENCH MARK AT SITE BEFORE ADOPTING COORDINATES.
- THE LEVELS SHOWN CORRESPONDS TO THE FINISHED SURFACES/LINES. FOR LEVELS OF EXCAVATION REFER EXCAVATION DRAWING.
- FOR EXCAVATION AND ROCK SUPPORT DETAILS REFER SEPARATE DRAWINGS.
- THIS DRAWING SHALL BE READ IN CONJUNCTION WITH DRG. NO. NHDB-1AC4-41-DD-0001 & NHDB-4AC4-41-DD-0001.

REFERENCE DRAWINGS:-

- NHDB-1AC4-41-DD-0001.
- NHDB-4AC4-41-DD-0001.
- NHDB-4BC4-41-DD-0004.
- NHDB-3KC4-41-DD-0001.

0 12.50 37.50 62.50 METRE

एन एच पी सी लिमिटेड
(भारत सरकार का उद्यम)
NHPC Limited
(A GOVT. OF INDIA ENTERPRISE)

दिवंग बहुउद्देशीय परियोजना
DIBANG MULTIPURPOSE PROJECT

POWER HOUSE
DRAINAGE GALLERY - L1
SETTING OUT PLAN AND LONGITUDINAL SECTION

10.11.2025	△	SLOPE & SIZE OPTIMISED, COORDINATES VALUE UPDATED, GENERAL UPDATION	Sd./	Sd./	Sd./
12.06.2025	△	COORDINATES VALUE UPDATED.	Sd./	Sd./	Sd./
17.04.2025	00	ISSUED FOR CONSTRUCTION	Sd./	Sd./	Sd./
DATE	NO.	REVISION OR ISSUES	BY.	CH.	APP.
DATE	DRG. NO.	DRG. NO.	NHDB	4CC4	41 DD
डिजाइन-मेमो संख्या	डिजाइन-मेमो संख्या	डिजाइन-मेमो संख्या	डिजाइन-मेमो संख्या	डिजाइन-मेमो संख्या	डिजाइन-मेमो संख्या

DRAWN	Sd./	SUBMITTED	Sd./	RECOMMENDED	Sd./	APPROVED	Sd./
डिजाइन	डिजाइन	डिजाइन	डिजाइन	डिजाइन	डिजाइन	डिजाइन	डिजाइन
DATE	APR 2025	DRG. NO.	NHDB	4CC4	41 DD	0001	02