
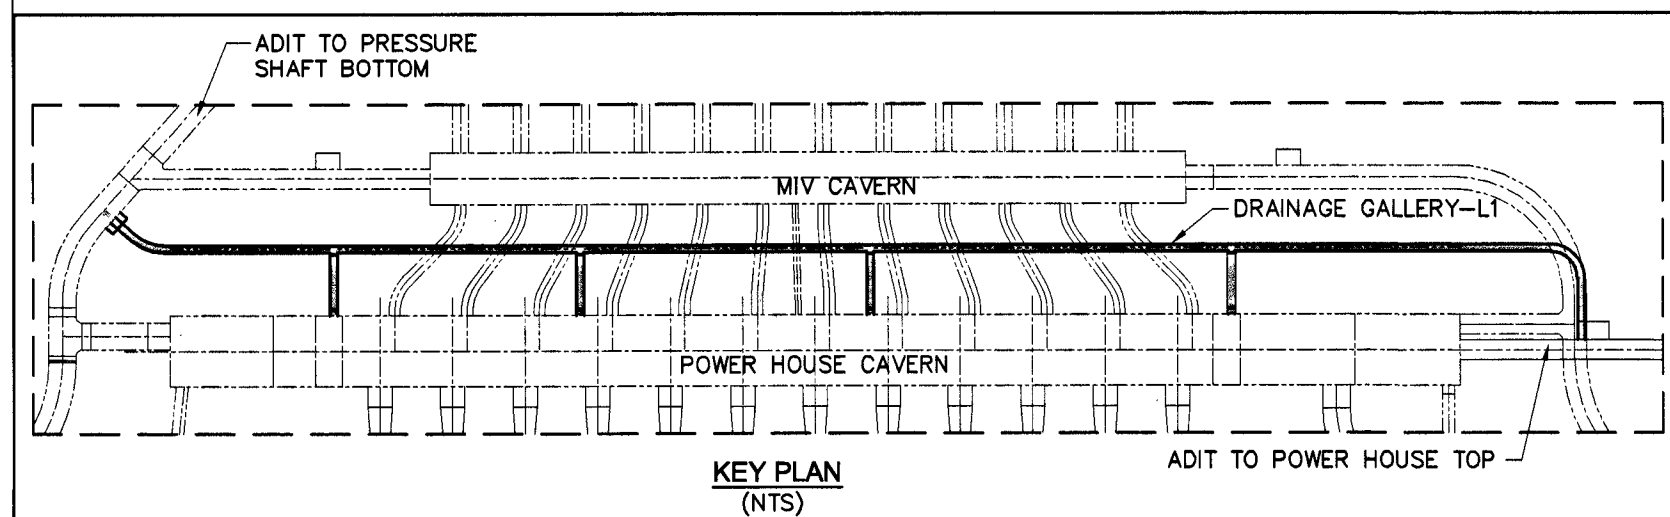
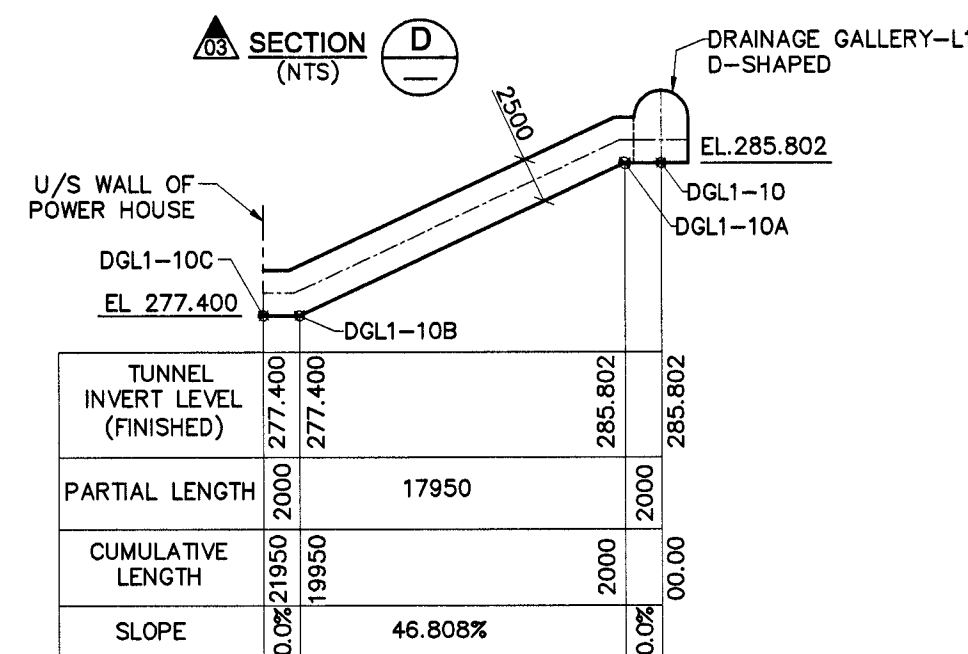
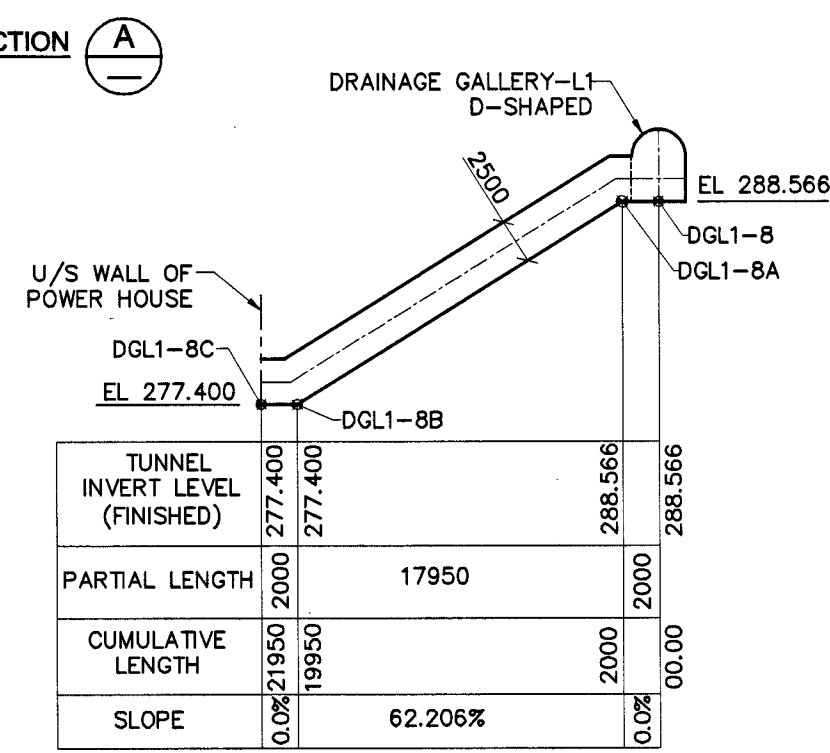
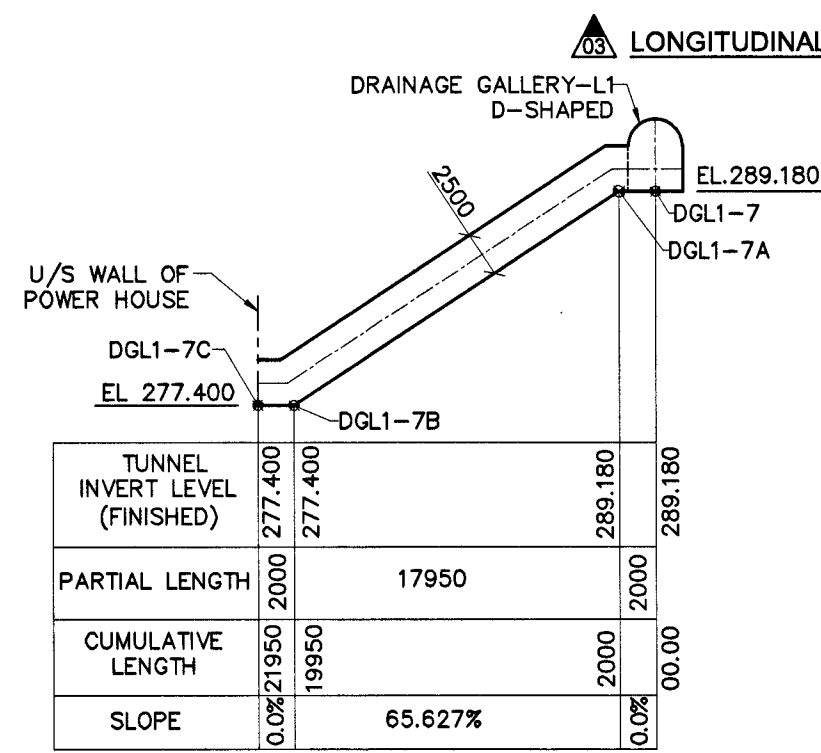
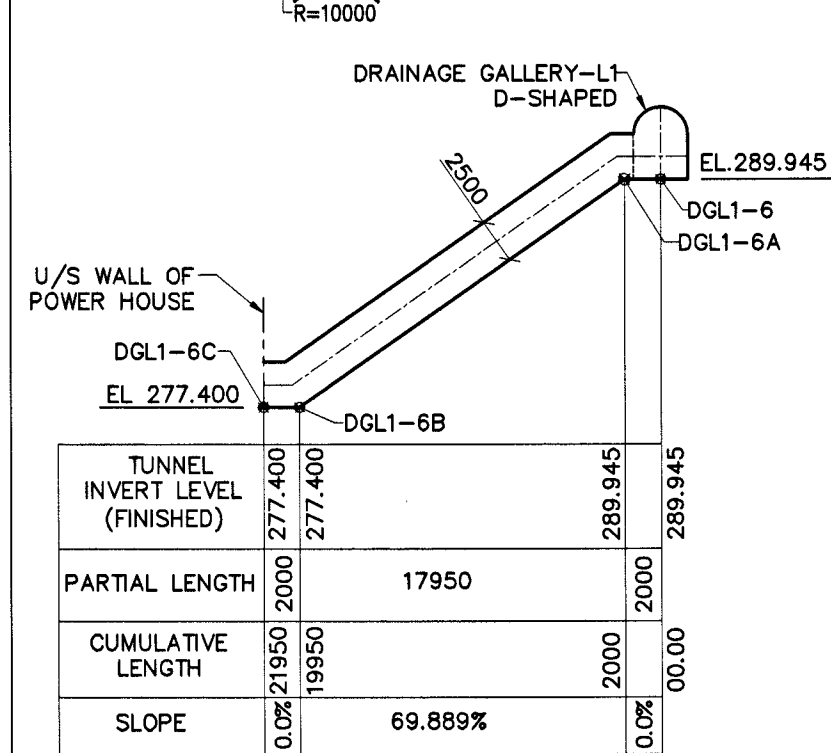


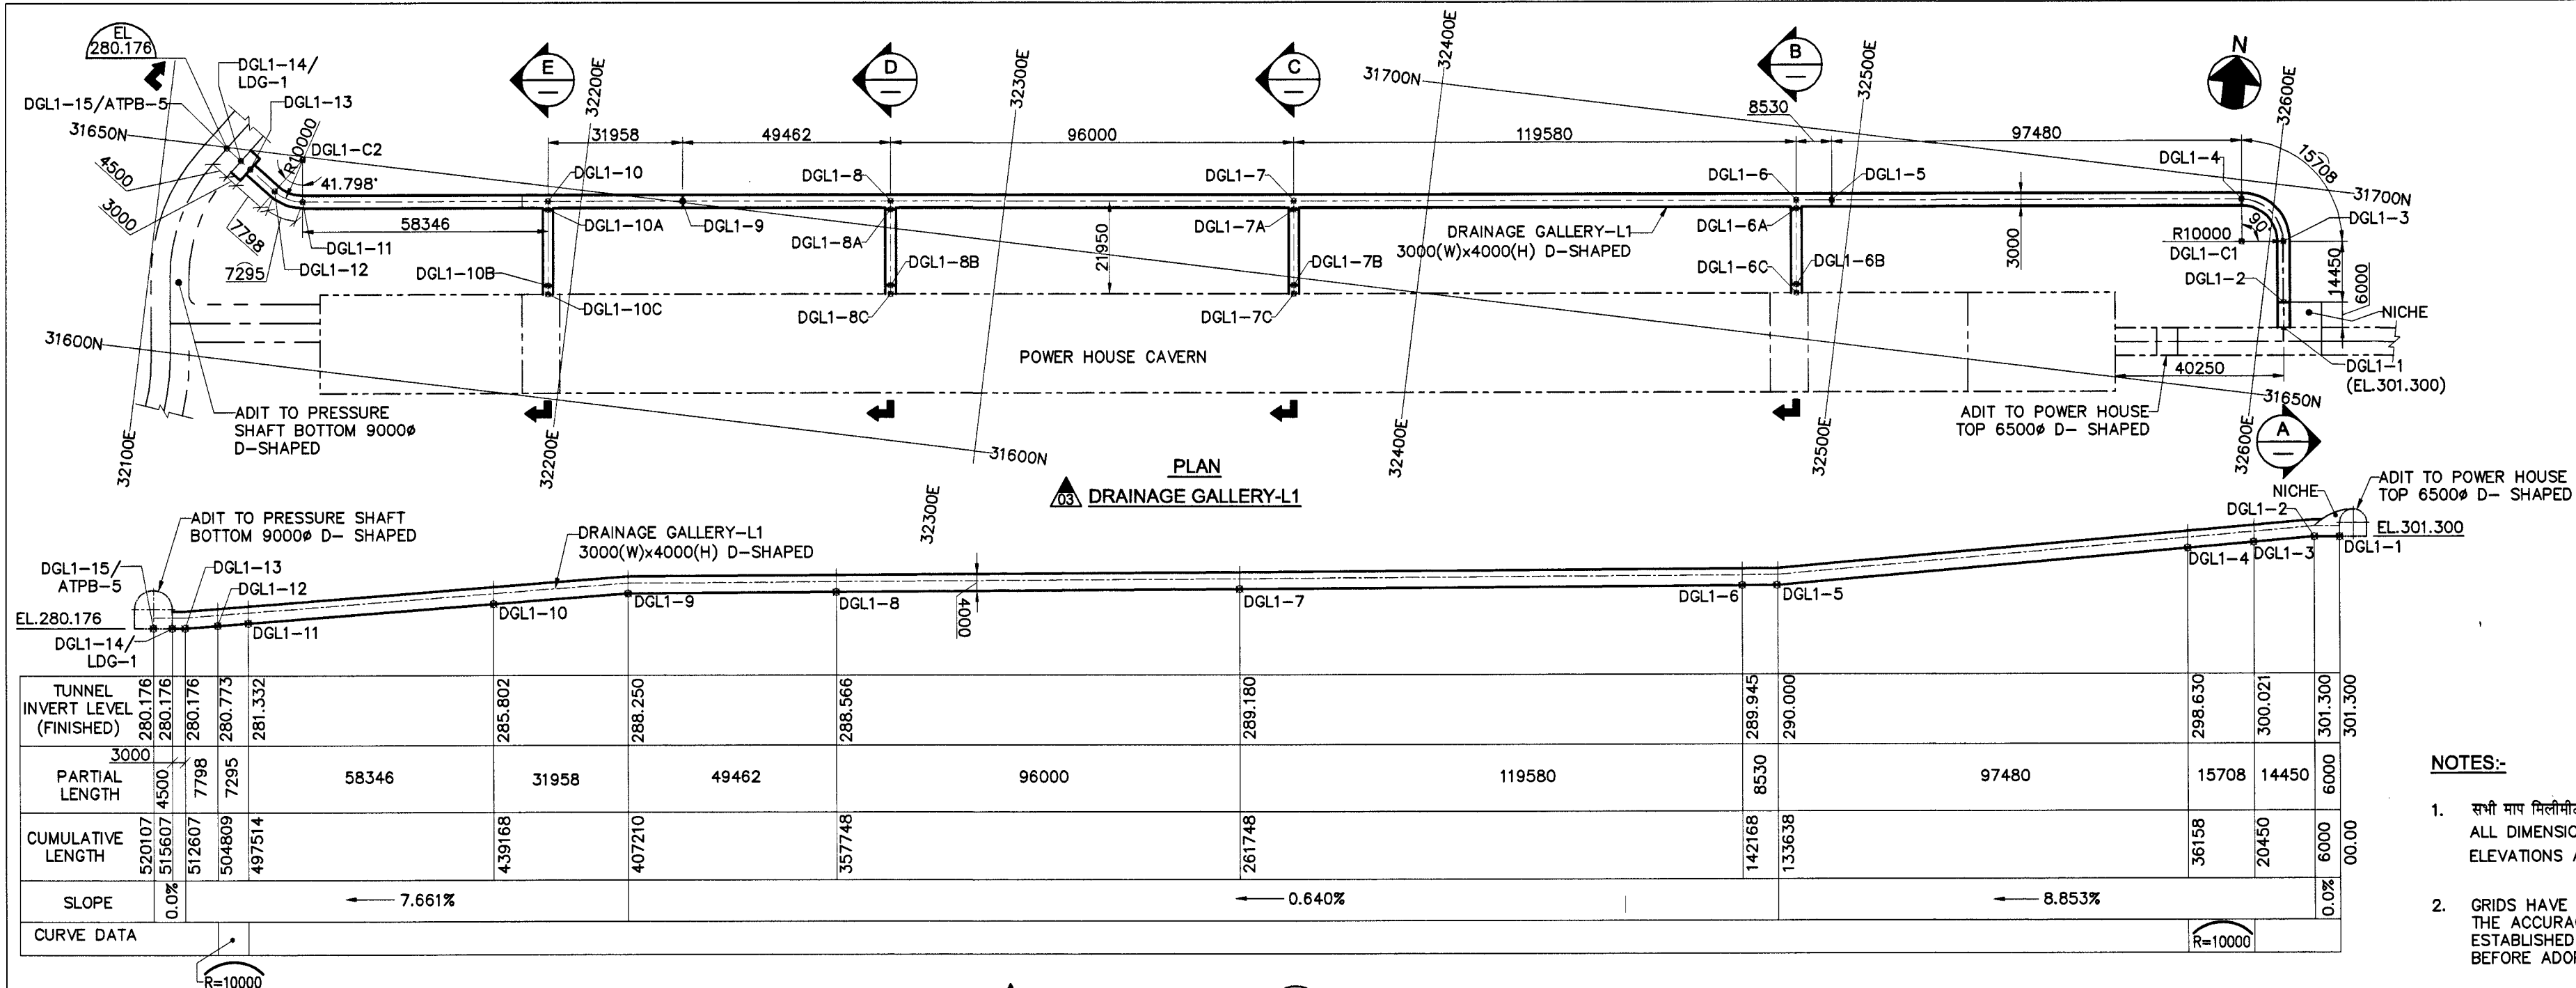

CO-ORDINATES:- (DRAINAGE GALLERY-L1)

POINTS	NORTHING IN METRE	EASTING IN METRE
DGL1-1	31666.504	32605.839
DGL1-2	31672.459	32605.108
DGL1-3	31686.801	32603.347
DGL1-4	31695.508	32592.203
DGL1-C1	31685.583	32593.421
DGL1-5	31683.628	32495.450
DGL1-6	31682.589	32486.984
DGL1-7	31668.016	32368.295
DGL1-8	31656.316	32273.011
DGL1-9	31650.288	32223.918
DGL1-10	31646.394	32192.198
DGL1-11	31639.283	32134.287
DGL1-12	31640.997	32127.361
DGL1-C2	31649.209	32133.068
DGL1-13	31645.447	32120.958
DGL1-14 /LDG-1	31647.159	32118.494
DGL1-15 /ATPB-5	31649.728	32114.799
DGL1-6A	31680.604	32487.227
DGL1-6B	31662.788	32489.414
DGL1-6C	31660.802	32489.658
DGL1-7A	31666.031	32368.539
DGL1-7B	31648.214	32370.726
DGL1-7C	31646.229	32370.969
DGL1-8A	31654.331	32273.254
DGL1-8B	31636.515	32275.441
DGL1-8C	31634.530	32275.685
DGL1-10A	31644.409	32192.441
DGL1-10B	31626.592	32194.628
DGL1-10C	31624.607	32194.872

19.11.2025	LEVEL & SLOPE MODIFIED, COORDINATES VALUE UPDATED, GENERAL UPDATION	Sd./- Sd./- Sd./-
10.11.2025	SLOPE & SIZE OPTIMISED, COORDINATES VALUE UPDATED, GENERAL UPDATION	Sd./- Sd./- Sd./-
12.08.2025	COORDINATES VALUE UPDATED.	Sd./- Sd./- Sd./-
17.04.2025	ISSUED FOR CONSTRUCTION	Sd./- Sd./- Sd./-
DATE	NO.	REVISION OR ISSUES
APR 2025	03	REVISED

NOTES:-

- सभी माप मिलीमीटर में, ग्रिड तथा ऊचाई मीटर में दिए गए हैं।
ALL DIMENSIONS ARE IN MILLIMETRE, GRIDS AND ELEVATIONS ARE IN METRE
- GRIDS HAVE BEEN REPRODUCED FROM S.O.I. TOPO SHEET. THE ACCURACY OF THE GRID SYSTEM SHALL BE ESTABLISHED WITH EXISTING S.O.I BENCH MARK AT SITE BEFORE ADOPTING COORDINATES.
- THE LEVELS SHOWN CORRESPONDS TO THE FINISHED SURFACES/LINES. FOR LEVELS OF EXCAVATION REFER EXCAVATION DRAWING.
- FOR EXCAVATION AND ROCK SUPPORT DETAILS REFER SEPARATE DRAWINGS.
- THIS DRAWING SHALL BE READ IN CONJUNCTION WITH DRG. NO. NHDB-1AC4-41-DD-0001 & NHDB-4AC4-41-DD-0001.

REFERENCE DRAWINGS:-

- NHDB-1AC4-41-DD-0001.
- NHDB-4AC4-41-DD-0001.
- NHDB-4BC4-41-DD-0004.
- NHDB-3KC4-41-DD-0001.

0 12.50 37.50 62.50 METRE

एन एच पी सी लिमिटेड (भारत सरकार का उद्यम) NHPC Limited (A GOVT. OF INDIA ENTERPRISE)	
दिबांग बहुउद्देशीय परियोजना DIBANG MULTIPURPOSE PROJECT	
POWER HOUSE DRAINAGE GALLERY - L1 SETTING OUT PLAN AND LONGITUDINAL SECTION	
DRAWN DEEPAK	SUBMITTED प्रस्तुत PRABHAT KISHOR
RECOMMENDED अनुमोदित RAJEEV KUMAR	APPROVED अनुमोदित S. CHOWDHURY
DATE दिनांक APR 2025	DRG. NO. संख्या NHDB 4CC4 41 DD 0001 03