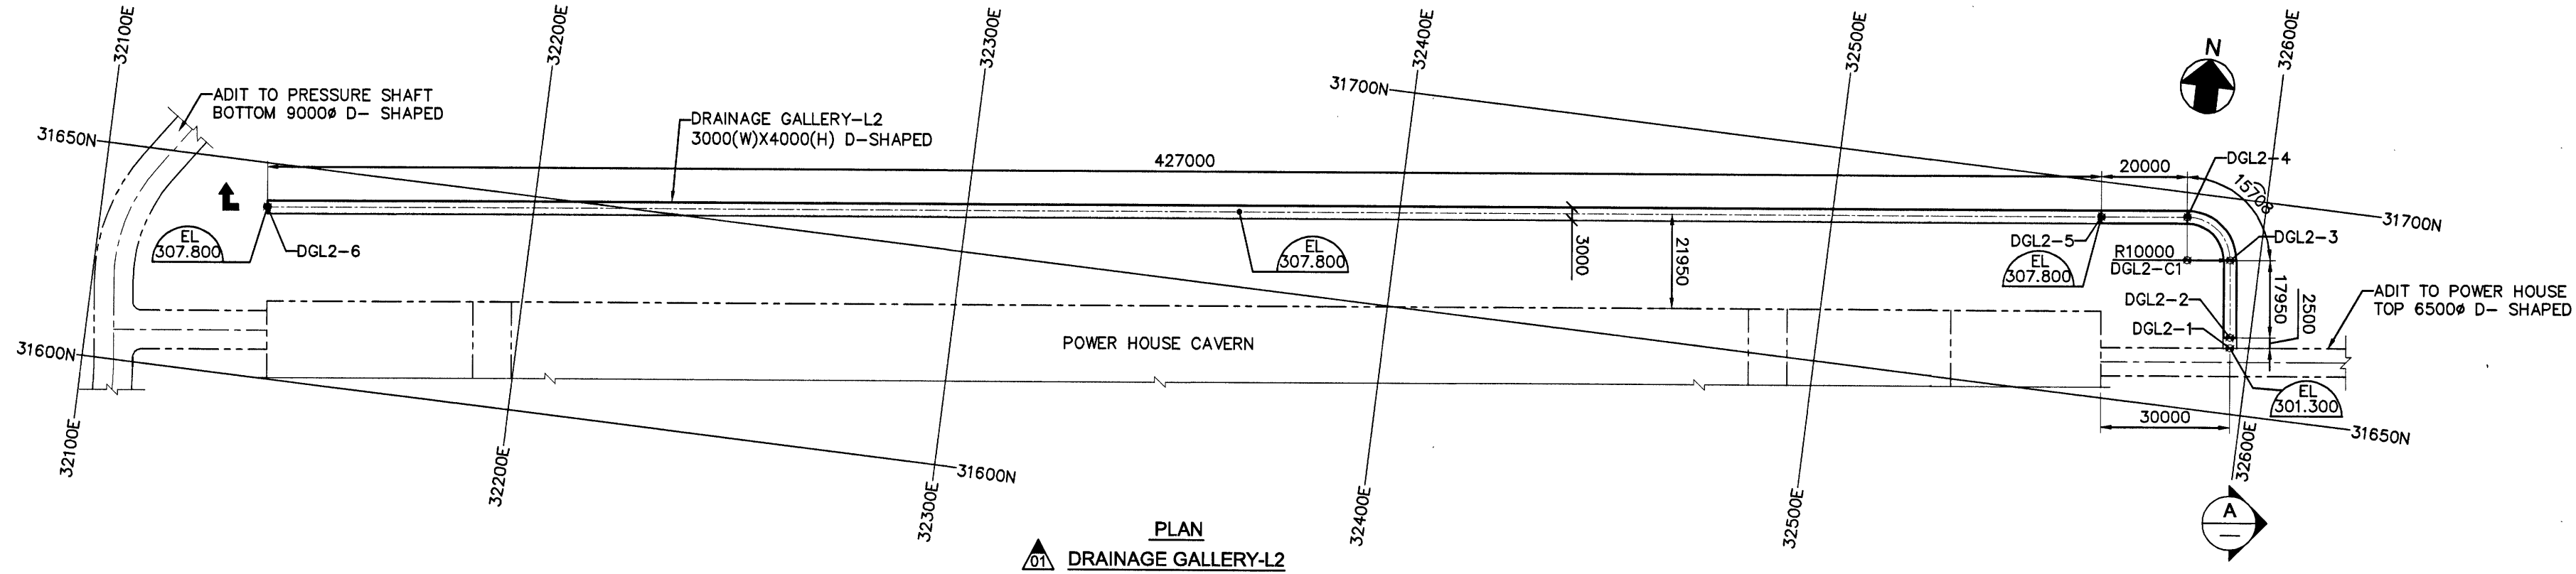


LONGITUDINAL SECTION A-A

CO-ORDINATES :-
(DRAINAGE GALLERY-L2)

POINTS	NORTHING IN METRE	EASTING IN METRE
DGL2-1	31665.255	32595.666
DGL2-2	31667.736	32595.361
DGL2-3	31685.552	32593.174
DGL2-4	31694.259	32582.03
DGL2-C1	31684.334	32583.249
DGL2-5	31691.822	32562.179
DGL2-6	31639.784	32138.362


NOTES:-

- सभी माप मिलीमीटर में, ग्रिड तथा ऊंचाई मीटर में दिए गए हैं।
ALL DIMENSIONS ARE IN MILLIMETRE, GRIDS AND ELEVATIONS ARE IN METRE
- GRIDS HAVE BEEN REPRODUCED FROM S.O.I. TOPO SHEET. THE ACCURACY OF THE GRID SYSTEM SHALL BE ESTABLISHED WITH EXISTING S.O.I. BENCH MARK AT SITE BEFORE ADOPTING COORDINATES.
- THE LEVELS SHOWN CORRESPONDS TO THE FINISHED SURFACES/LINES. FOR LEVELS OF EXCAVATION REFER EXCAVATION DRAWING.
- FOR EXCAVATION AND ROCK SUPPORT DETAILS REFER SEPARATE DRAWINGS.
- THIS DRAWING SHALL BE READ IN CONJUNCTION WITH DRG. NO. NHDB-1AC4-41-DD-0001 & NHDB-4AC4-41-DD-0001.

REFERENCE DRAWINGS:-

- NHDB-1AC4-41-DD-0001.
- NHDB-4AC4-41-DD-0001.
- NHDB-4BC4-41-DD-0004.

0 12.50 37.50 62.50 METRE

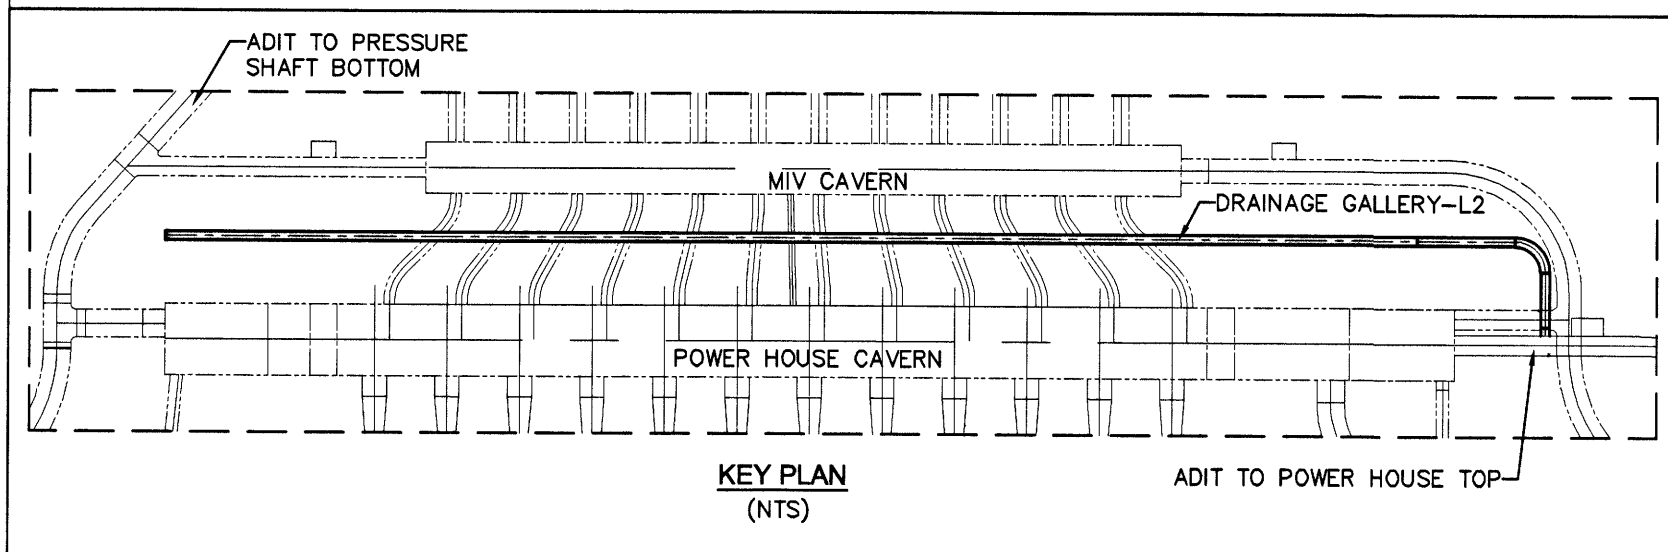

10.11.2025	01	SLOPE & SIZE OPTIMISED. POINT NO. DGL2-5 MODIFIED & POINT NO. DGL2-6 ADDED. GENERAL UPDATION	Sd/-	Sd/-	Sd/-
17.04.2025	00	ISSUED FOR CONSTRUCTION	Sd/-	Sd/-	Sd/-
DATE	NO.	REVISION OR ISSUES	BY.	CH. APP.	

एन एच पी सी लिमिटेड (भारत सरकार का अधिनियम) NHPC Limited (A GOVT. OF INDIA ENTERPRISE)					
दिबांग बहुउद्देशीय परियोजना DIBANG MULTIPURPOSE PROJECT					
POWER HOUSE DRAINAGE GALLERY - L2 SETTING OUT PLAN AND LONGITUDINAL SECTION					
DESIGN MEMO NO.-	DRG. NO.	REV. NO.	NHDB	4CC4	41 DD 0002 01