

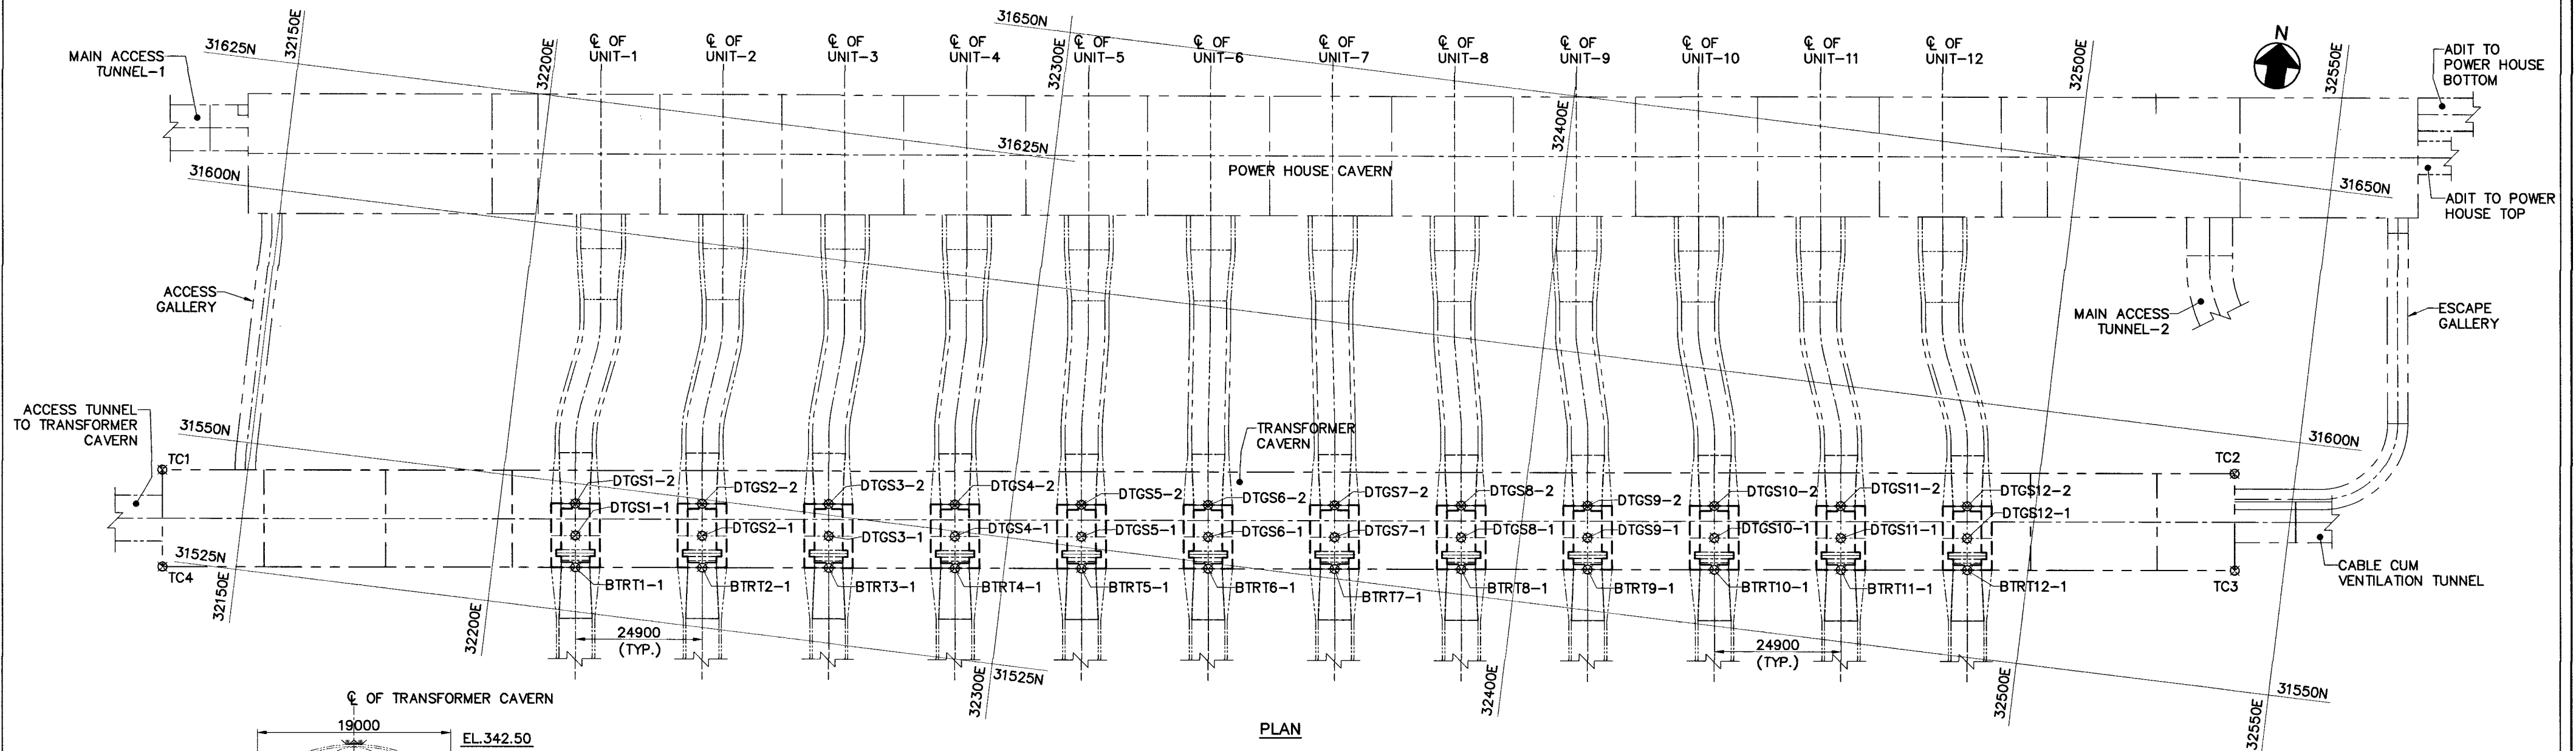


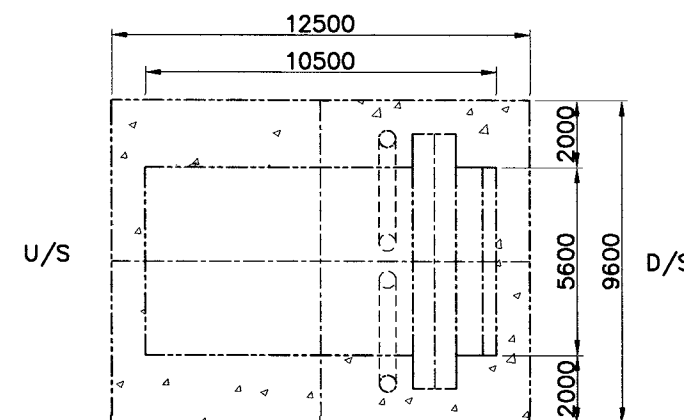

PLAN

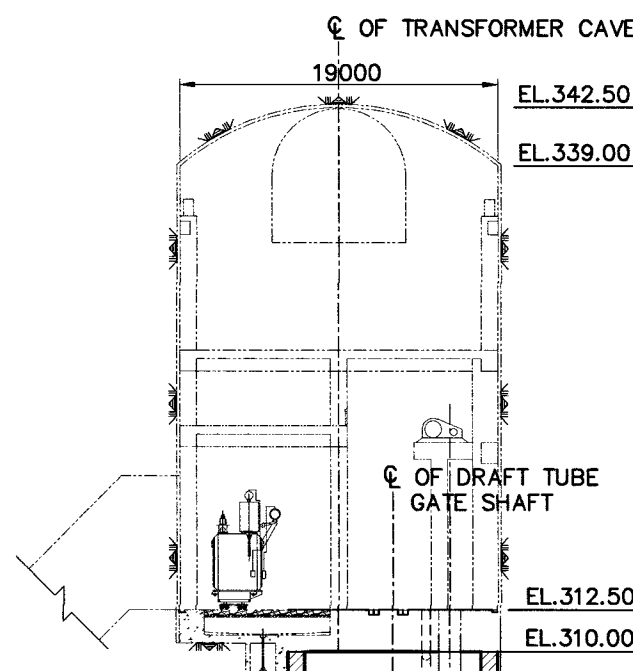

TYPICAL SECTION A-A
(SCALE= 1:225)

TYPICAL SECTION B-B
(SCALE= 1:300)

CO-ORDINATES:-


POINTS	NORTHING (IN METRE)	EASTING (IN METRE)
DTGS1-1	31539.846	32215.556
DTGS1-2	31546.050	32214.794
DTGS2-1	31542.881	32240.270
DTGS2-2	31549.084	32239.508
DTGS3-1	31545.915	32264.985
DTGS3-2	31552.119	32264.223
DTGS4-1	31548.950	32289.699
DTGS4-2	31555.153	32288.937
DTGS5-1	31551.984	32314.413
DTGS5-2	31558.188	32313.652
DTGS6-1	31555.019	32339.128
DTGS6-2	31561.222	32338.366
DTGS7-1	31558.053	32363.842
DTGS7-2	31564.257	32363.080
DTGS8-1	31561.088	32388.557
DTGS8-2	31567.291	32387.795
DTGS9-1	31564.122	32413.271
DTGS9-2	31570.326	32412.509
DTGS10-1	31567.157	32437.985
DTGS10-2	31573.360	32437.224
DTGS11-1	31570.192	32462.700
DTGS11-2	31576.395	32461.938
DTGS12-1	31573.226	32487.414
DTGS12-2	31579.430	32486.652

NOTES:-

- सभी माप मिलीमीटर में, ग्रिड तथा ऊंचाई मीटर में दिए गए हैं।
ALL DIMENSIONS ARE IN MILLIMETRE, GRIDS AND ELEVATIONS ARE IN METRE.
- GRIDS HAVE BEEN REPRODUCED FROM S.O.I. TOPO SHEET. THE ACCURACY OF THE GRID SYSTEM SHALL BE ESTABLISHED WITH EXISTING S.O.I BENCH MARK AT SITE BEFORE ADOPTING COORDINATES.
- THE LEVELS SHOWN CORRESPONDS TO THE FINISHED SURFACES/LINES. FOR LEVELS OF EXCAVATION REFER EXCAVATION DRAWING.
- FOR EXCAVATION AND ROCK SUPPORT DETAILS REFER SEPARATE DRAWINGS.
- THIS DRAWING SHALL BE READ IN CONJUNCTION WITH DRAWING NO. NHDB-4AC4-41-DD-0001 AND DRAWING NO. NHDB-4DC4-41-DD-0001 TO 0006.

REFERENCE DRAWINGS:-

- NHDB-4AC4-41-DD-0001.
- NHDB-4DC4-41-DD-0001 TO 0006.

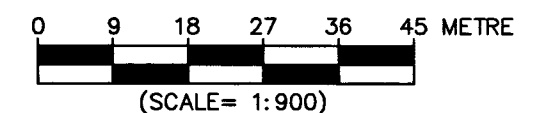

एन एच पी सी लिमिटेड NHPC Limited (A GOVT. OF INDIA NAVRATNA ENTERPRISE)	
दिवांग बहुउद्देशीय परियोजना DIBANG MULTIPURPOSE PROJECT	
DRAFT TUBE GATE SHAFT SETTING OUT PLAN AND LONGITUDINAL SECTIONS	
24.04.2026	00
DATE	NO.
ISSUED FOR CONSTRUCTION	REVISION OR ISSUES
BY	CH. APP.
DRG. NO.	41 DD 0001
DATE	APR. 2026
DRG. NO.	NHDB 4HC4 41 DD 0001
DATE	APR. 2026
DRG. NO.	NHDB 4HC4 41 DD 0001
DATE	APR. 2026
DRG. NO.	NHDB 4HC4 41 DD 0001