




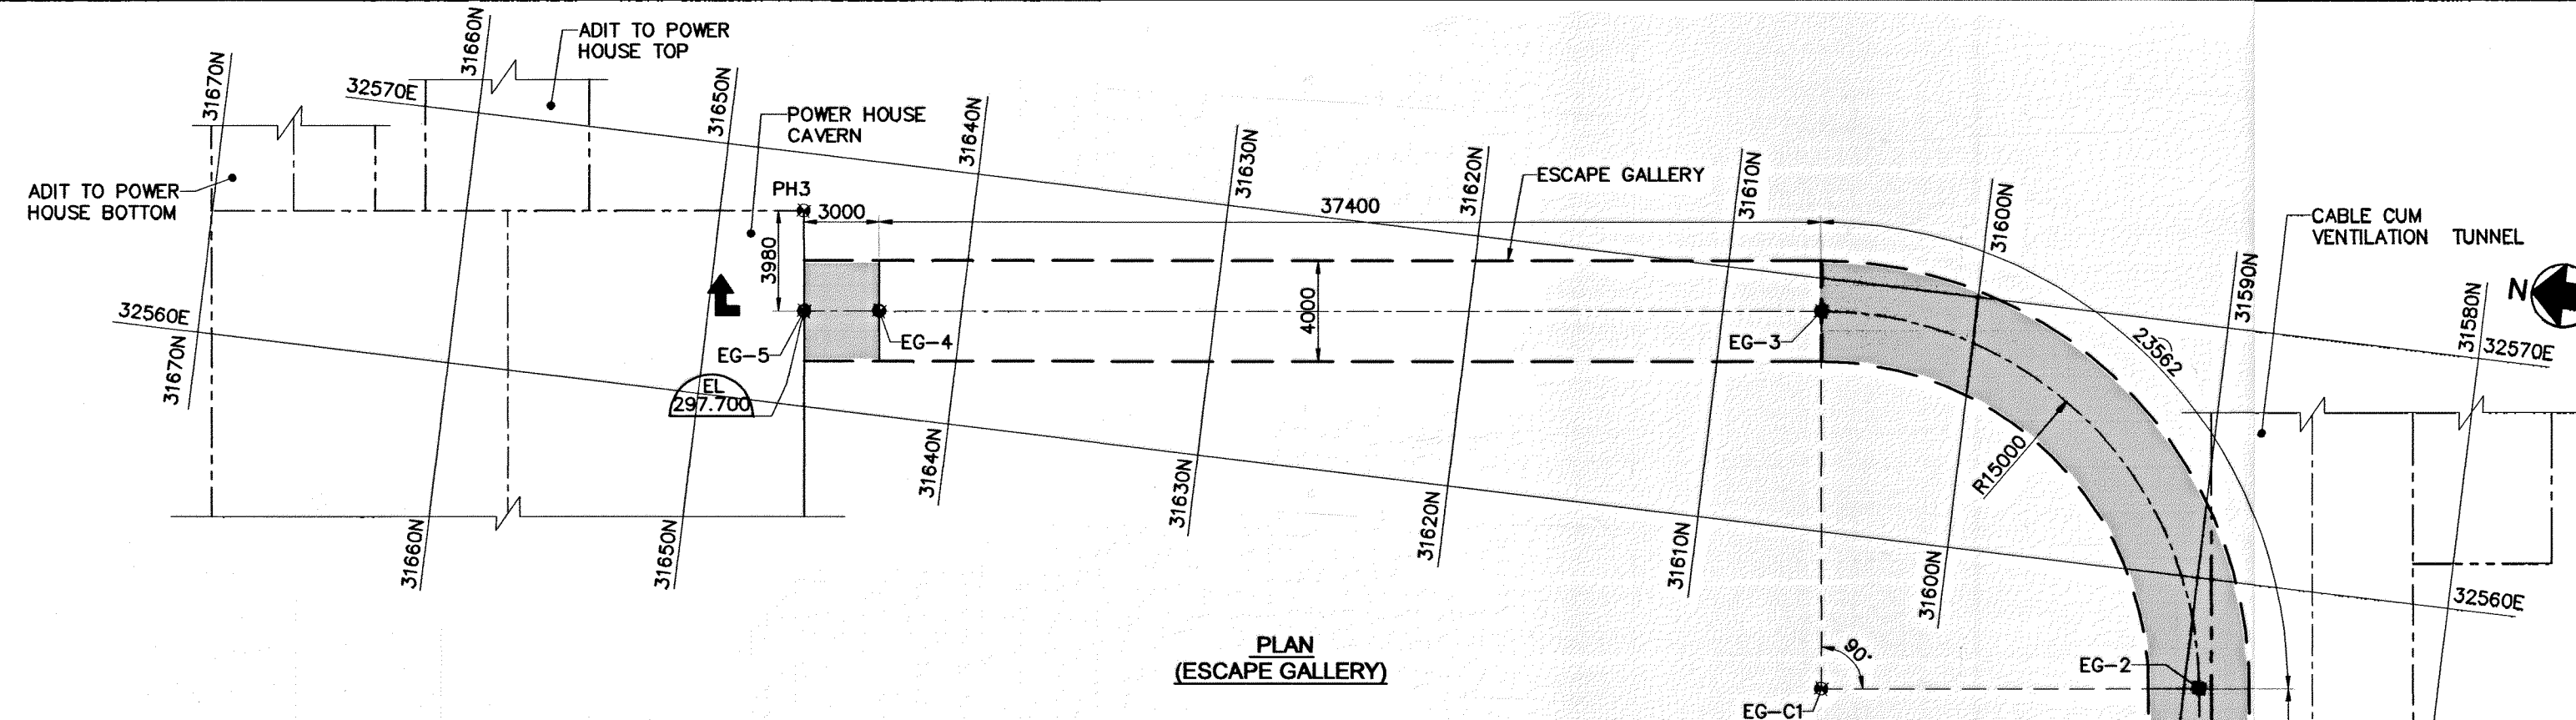


PLAN
(ESCAPE GALLERY)

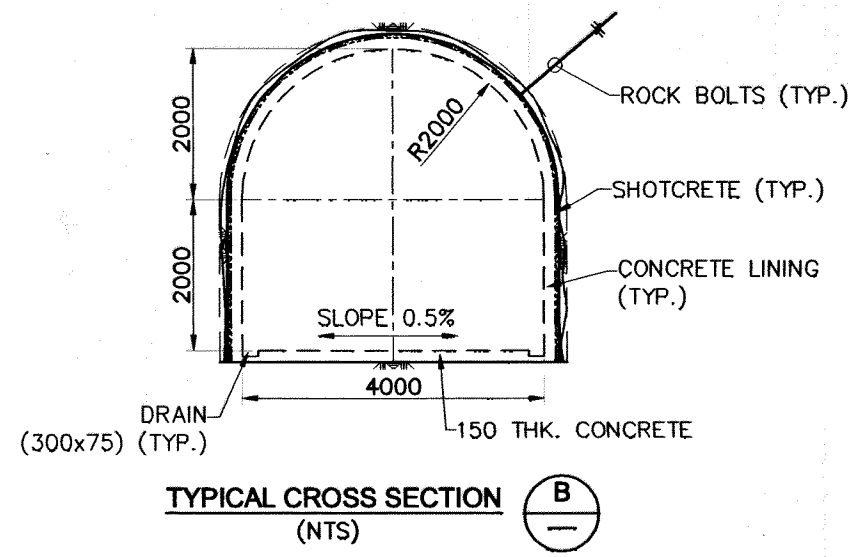


TYPICAL CROSS SECTION
(NTS)

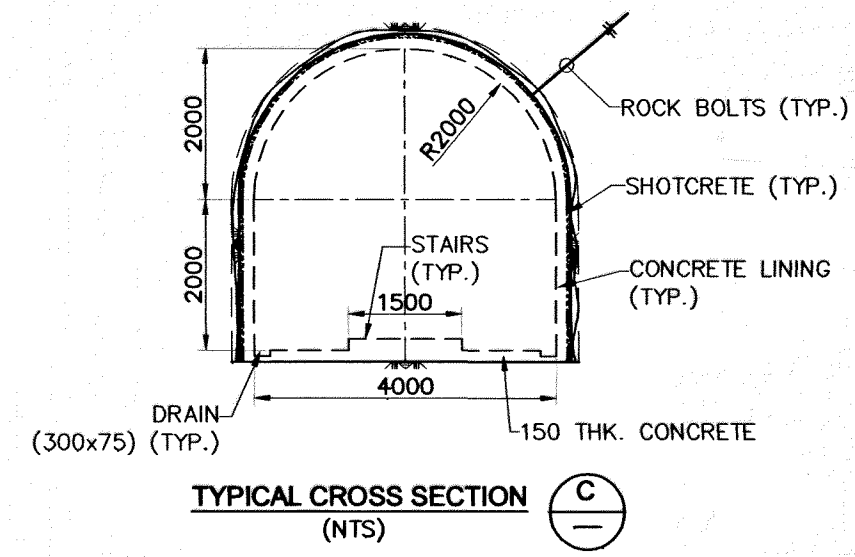

TYPICAL CROSS SECTION
(NTS)

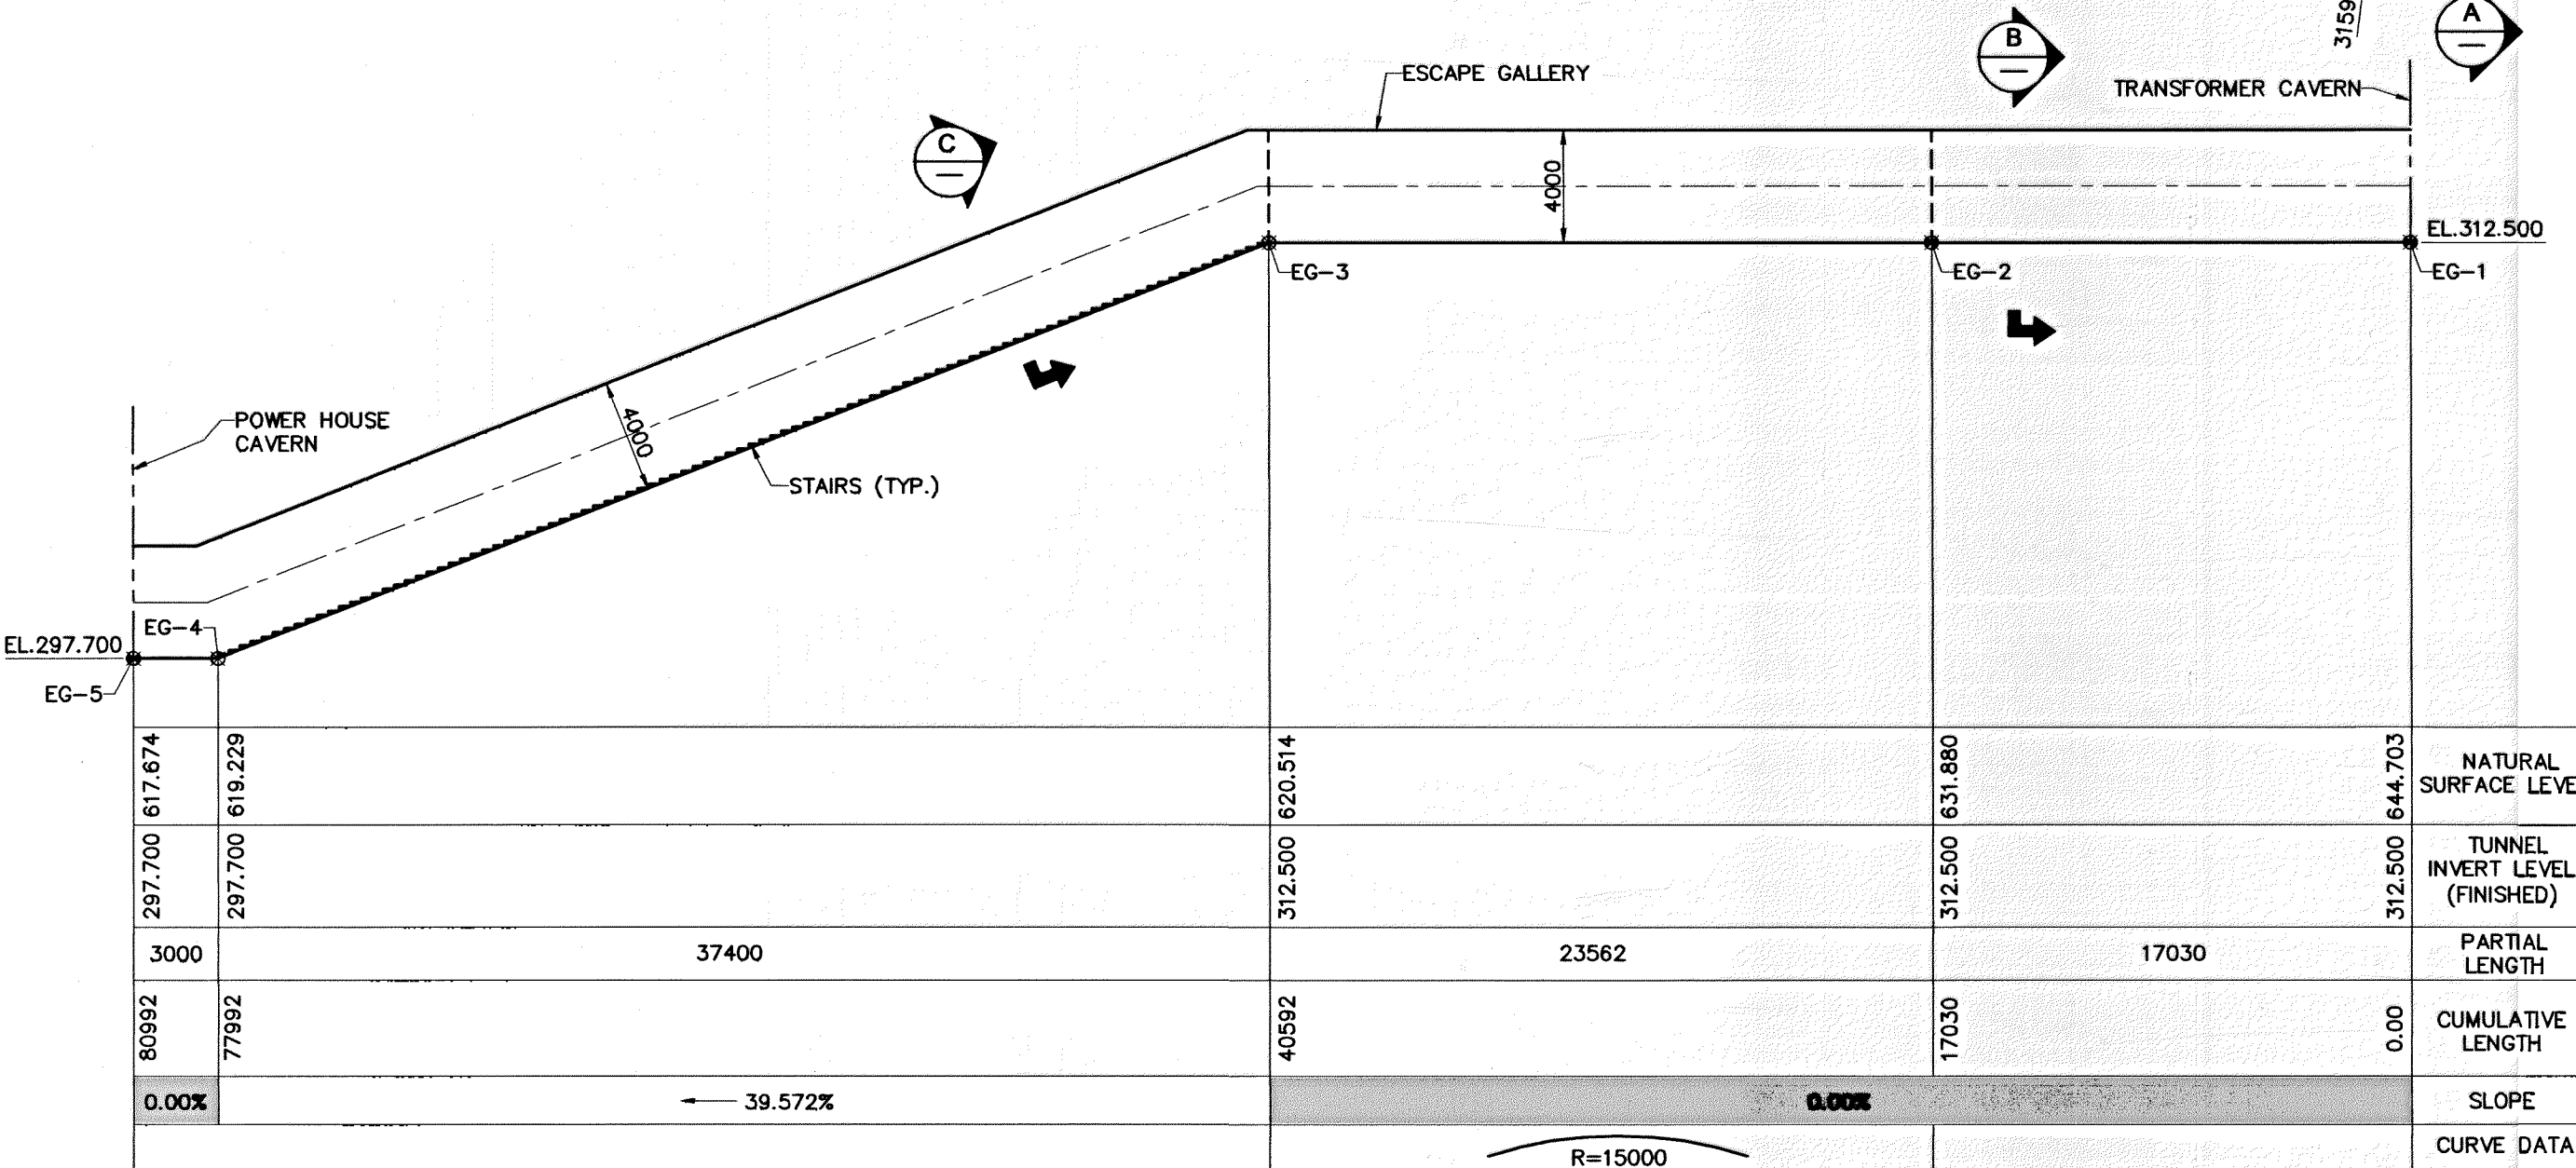

LONGITUDINAL SECTION
(A)

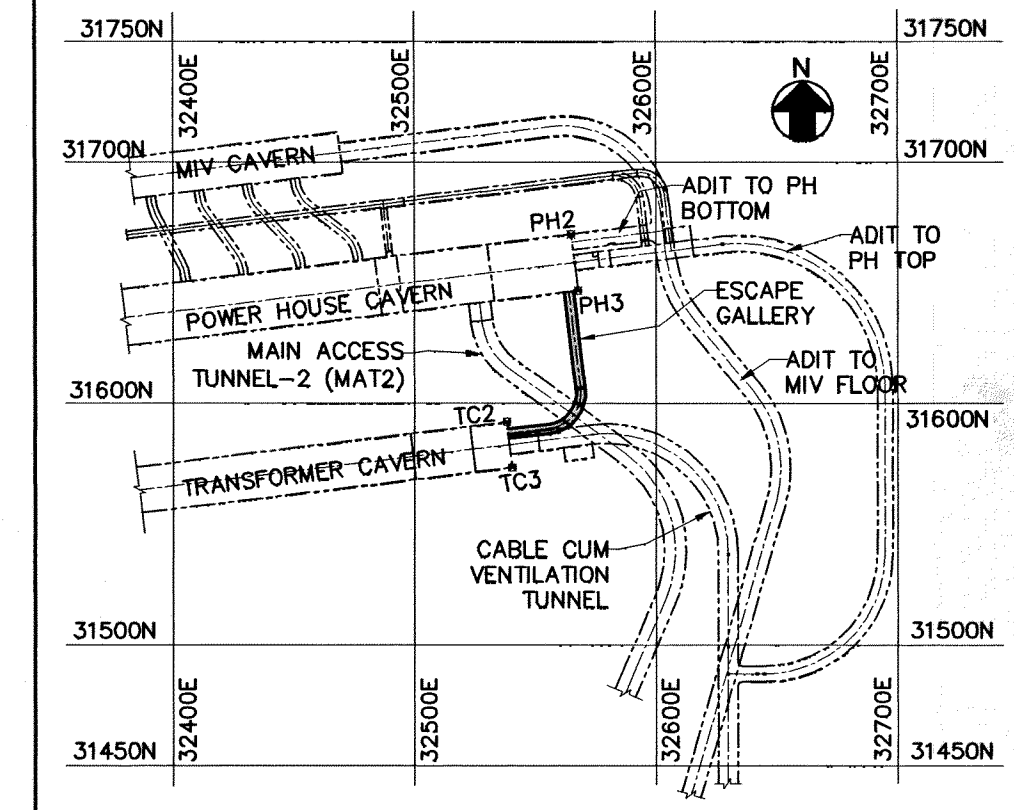

KEY PLAN
(NTS)

NOTES:-


- सभी माप मिलीमीटर में, ग्रिड तथा ऊंचाई मीटर में दिए गए हैं।
ALL DIMENSIONS ARE IN MILLIMETRE, GRIDS AND ELEVATIONS ARE IN METRE
- GRIDS AND THE VALUES OF NSL HAVE BEEN REPRODUCED FROM S.O.I. SHEET. THE ACCURACY OF THE SAME SHALL BE ESTABLISHED WITH EXISTING S.O.I. BENCH MARK AT SITE BEFORE ADOPTING CO-ORDINATES.
- THE LEVELS SHOWN CORRESPONDS TO THE FINISHED SURFACES/LINES. FOR LEVELS OF EXCAVATION REFER EXCAVATION DRAWING.
- FOR EXCAVATION AND ROCK SUPPORT DETAILS REFER SEPARATE DRAWINGS.
- THIS DRAWING SHALL BE READ IN CONJUNCTION WITH DRG. NO. NHDB-1AC4-41-DD-0001 & NHDB-4AC4-41-DD-0001.

REFERENCE:

- NHDB-1AC4-41-DD-0001.
- NHDB-4AC4-41-DD-0001

CO-ORDINATES:-
(ESCAPE GALLERY)

POINTS	NORTHING IN METRE	EASTING IN METRE
EG-1	31587.335	32538.727
EG-2	31589.410	32555.630
EG-C1	31604.298	32553.802
EG-3	31606.126	32568.690
EG-4	31643.248	32564.132
EG-5	31646.225	32563.767

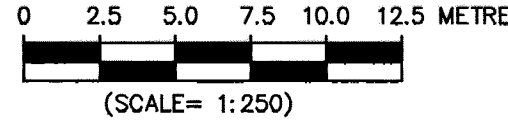

एन एच सी लिमिटेड NHPC Limited (A GOVT. OF INDIA NAVRATNA ENTERPRISE)	
दिबांग बहुउद्देशीय परियोजना DIBANG MULTIPURPOSE PROJECT	
POWER HOUSE ESCAPE GALLERY SETTING OUT PLAN AND LONGITUDINAL SECTION	
30.01.2026 00	ISSUED FOR CONSTRUCTION
DATE NO.	REVISION OR ISSUES
DESIGN MEMO NO. दिबांग मेरी संस्था	DATE JAN. 2026
DRG. NO. 41 DD 0003 00	REV. NO. : 03 EFF. DATE 21.07.2016