
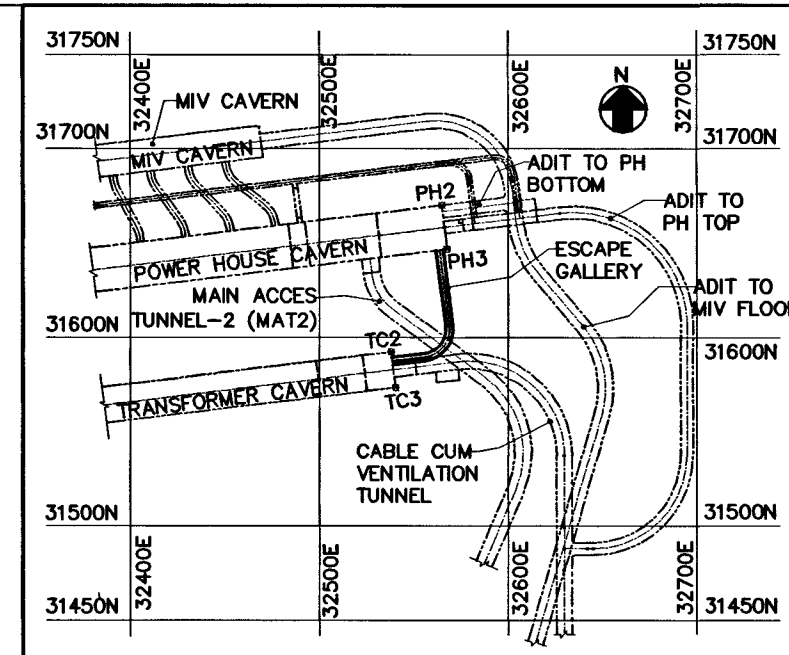


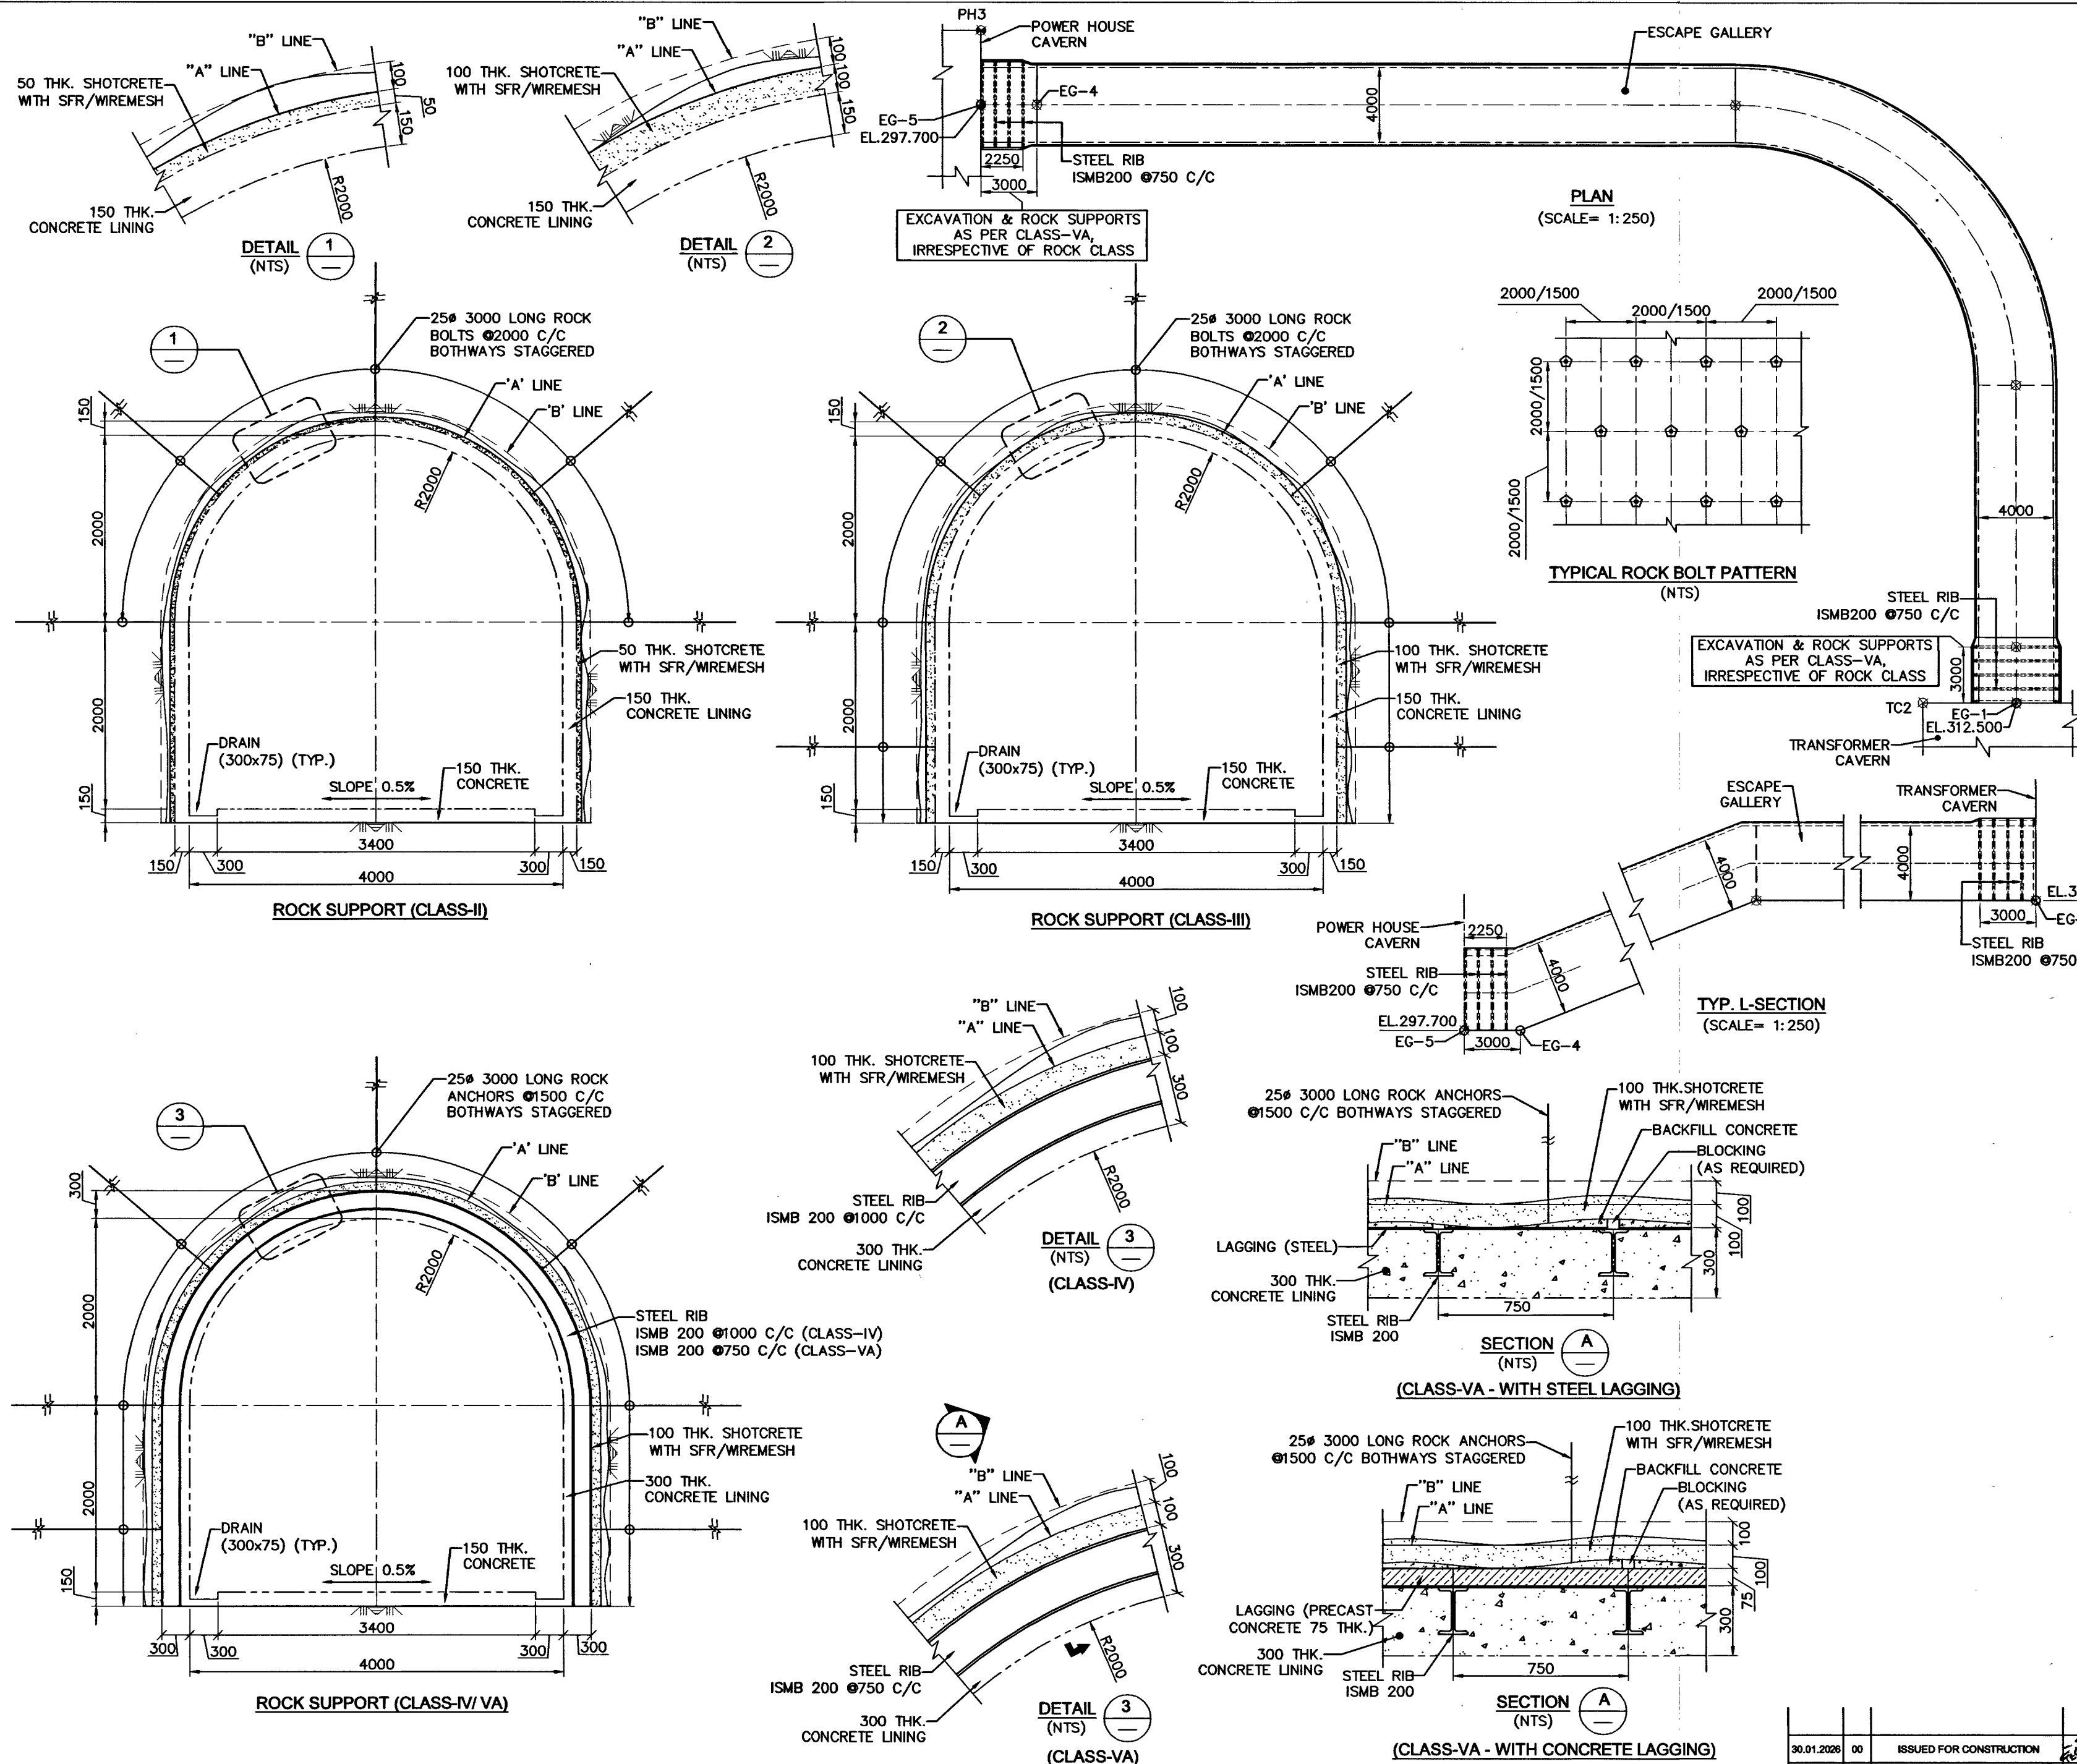


- NOTES:-**
- सभी माप मिलीमीटर में तथा ऊंचाई मीटर में दिए गए हैं।
 - ALL DIMENSIONS ARE IN MILLIMETERS AND LEVELS IN METERS.
 - THE DEFINITION OF 'A', & 'B' LINE AND VARIOUS CLASSES OF EXCAVATION SHOWN SHALL BE AS PER SECTION B.3 OF TECHNICAL SPECIFICATIONS.
 - UNDERGROUND EXCAVATION INCLUDING PROTECTION OF TUNNEL INVERT SHALL BE CONFORMING TO SECTION B.3 OF TECHNICAL SPECIFICATIONS.
 - ROCK BOLTS/ANCHORS SHOWN IN THE DRAWING SHALL BE CONFORMING TO SECTION B.4 OF TECHNICAL SPECIFICATIONS.
 - MINOR MODIFICATION IN THE LENGTH, ORIENTATION, PATTERN AND LOCATION OF ROCK BOLTS/ANCHORS MAY BE DONE TO SUIT THE SITE CONDITIONS WITH THE APPROVAL OF ENGINEER-IN-CHARGE.
 - SFR SHOTCRETE SHOWN IN THE DRAWING SHALL BE APPLIED AS SPECIFIED IN SECTION B.5 OF TECHNICAL SPECIFICATIONS. IF REQUIRED, PLAIN SHOTCRETE WITH WIREMESH CAN BE USED WITH THE APPROVAL OF ENGINEER-IN-CHARGE. 50MM THK. MINIMUM SHOTCRETE SHALL BE PROVIDED AS FINAL SUPPORT IN ENTIRE LENGTH OF TUNNEL IRRESPECTIVE OF ROCK CLASS.
 - STEEL BOLTS/ANCHORS SHOWN IN THE DRAWING SHALL BE CONFORMING TO SECTION B.4 OF TECHNICAL SPECIFICATION. THE SPACING OF BOLTS SHOWN MAY BE MODIFIED TO SUIT THE SITE CONDITIONS WITH THE APPROVAL OF ENGINEER-IN-CHARGE. FOR STEEL RIB DETAILS REFER SEPARATE DRAWING.
 - STEEL LAGGING OR PRE CAST CONCRETE LAGGING AS SPECIFIED IN SECTION B.4 OF TECHNICAL SPECIFICATION SHALL BE USED WITH THE APPROVAL OF ENGINEER-IN-CHARGE.
 - 45# 5000 LONG (INTO ROCK) CONSOLIDATION GROUTING @3000 C/C STAGGERED BOTHWAYS SHALL BE PROVIDED IN CLASS VA OR AS DIRECTED BY ENGINEER-IN-CHARGE, AS PER SECTION B.7 OF TECHNICAL SPECIFICATION.
 - PREGRouting/FOREPOLING MAY BE USED WHERE RMR VALUE IS LESS THAN 35 OR AS DIRECTED BY ENGINEER-IN-CHARGE.
 - M25/A40 GRADE FOR INVERT & OVERT CONCRETE AND M15/A40 FOR BACKFILL CONCRETE CONFORMING TO SECTION B.9 OF TECHNICAL SPECIFICATIONS SHALL BE USED.
 - FOR CONCRETE & REINFORCEMENT DETAILS OF ESCAPE GALLERY REFER SEPARATE DRAWINGS.

REFERENCE DRAWINGS:-

- NHDB 4CC4-41-DD-0003.

SCALE:

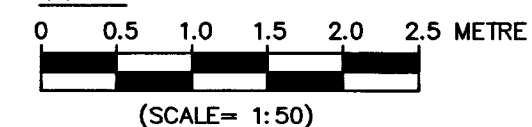

एन एच पी सी लिमिटेड NHPC Limited (A GOVT. OF INDIA NAVY/NAVY ENTERPRISE)	
दिवांग बहुउद्देशीय परियोजना DIBANG MULTIPURPOSE PROJECT	
POWER HOUSE ESCAPE GALLERY EXCAVATION AND ROCK SUPPORTS TYPICAL CROSS SECTIONS	
30.01.2026 00	ISSUED FOR CONSTRUCTION
DATE NO.	REVISION OR ISSUES
BY: CH. APP.	BY: CH. APP.
DESIGN MEMO NO. दिवांग मरो संख्या	DATE JAN. 2026 रिक्त
DRG. NO. संख्या	NHDB 4CC4 41 DD 1026 00