
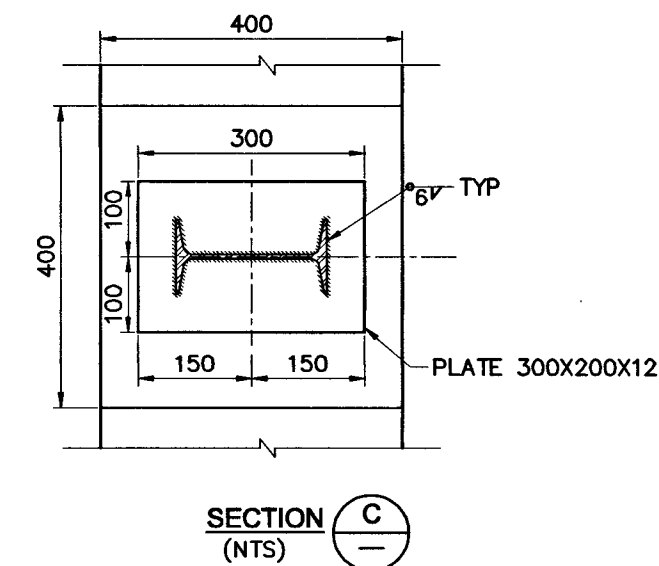
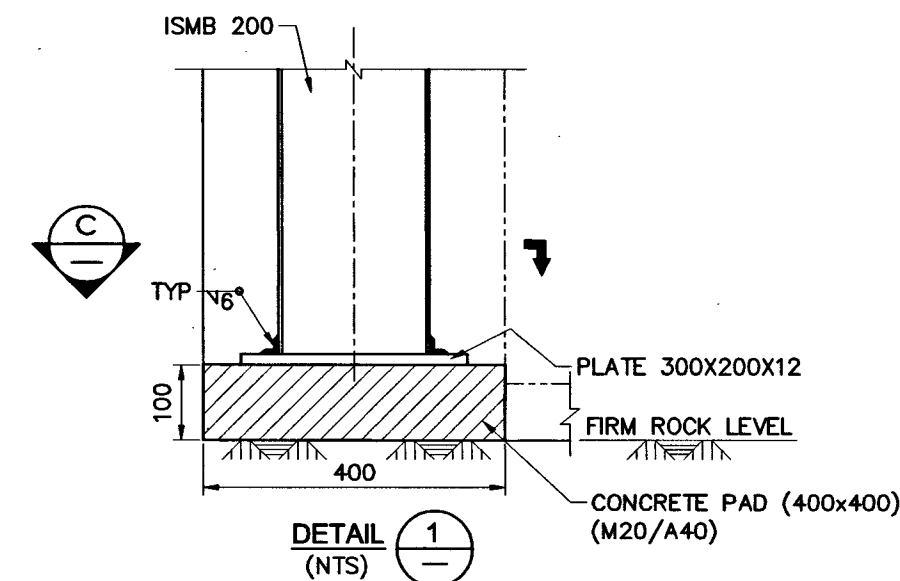
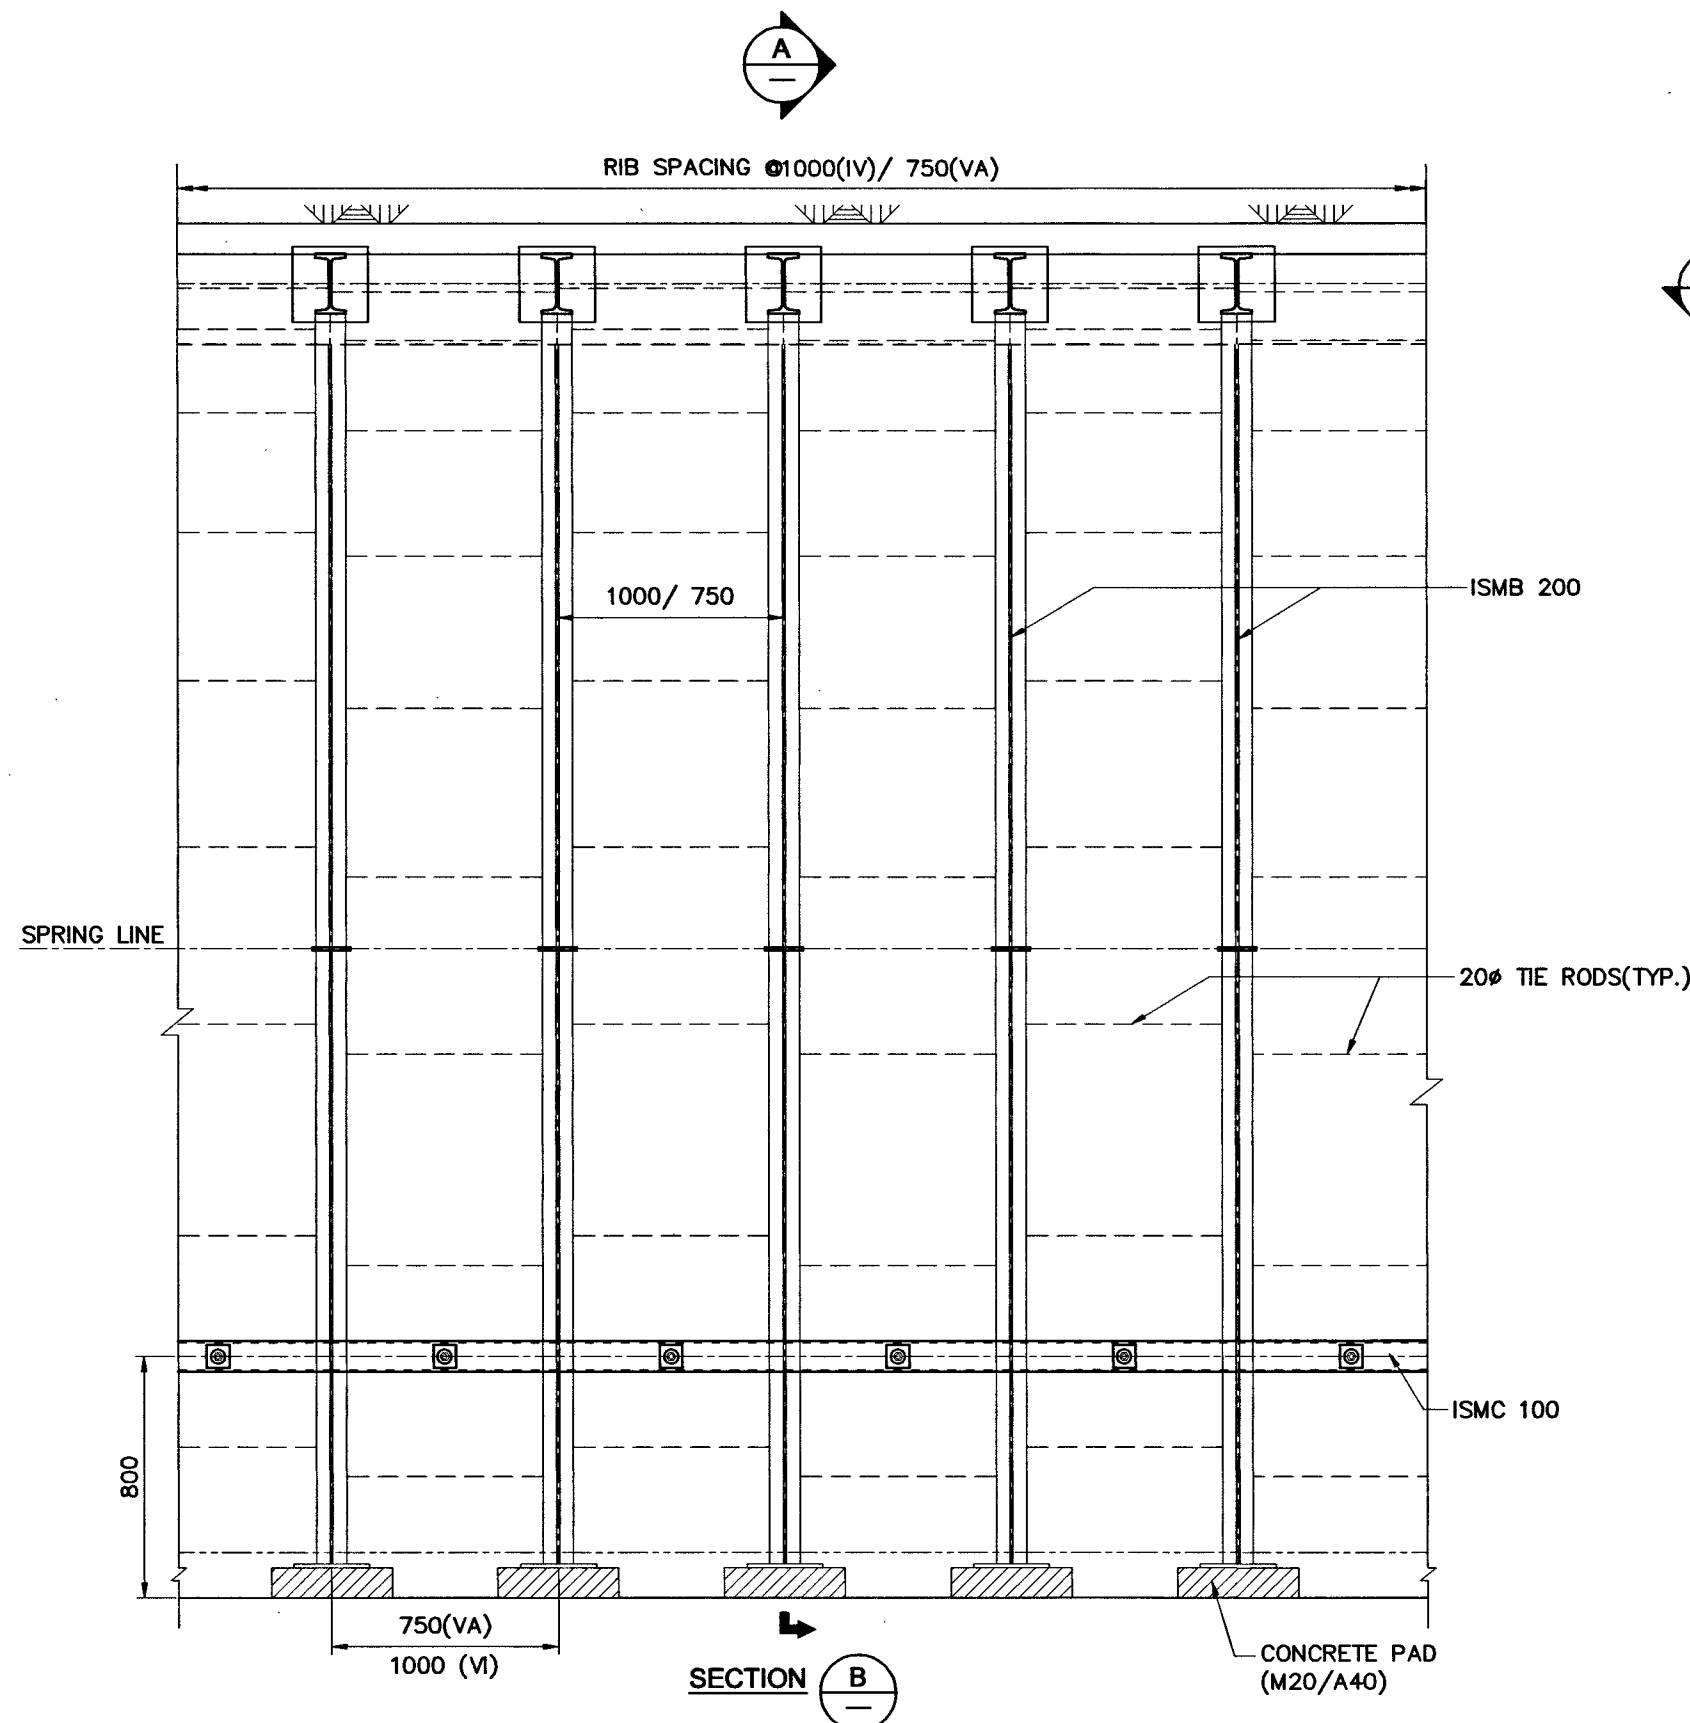


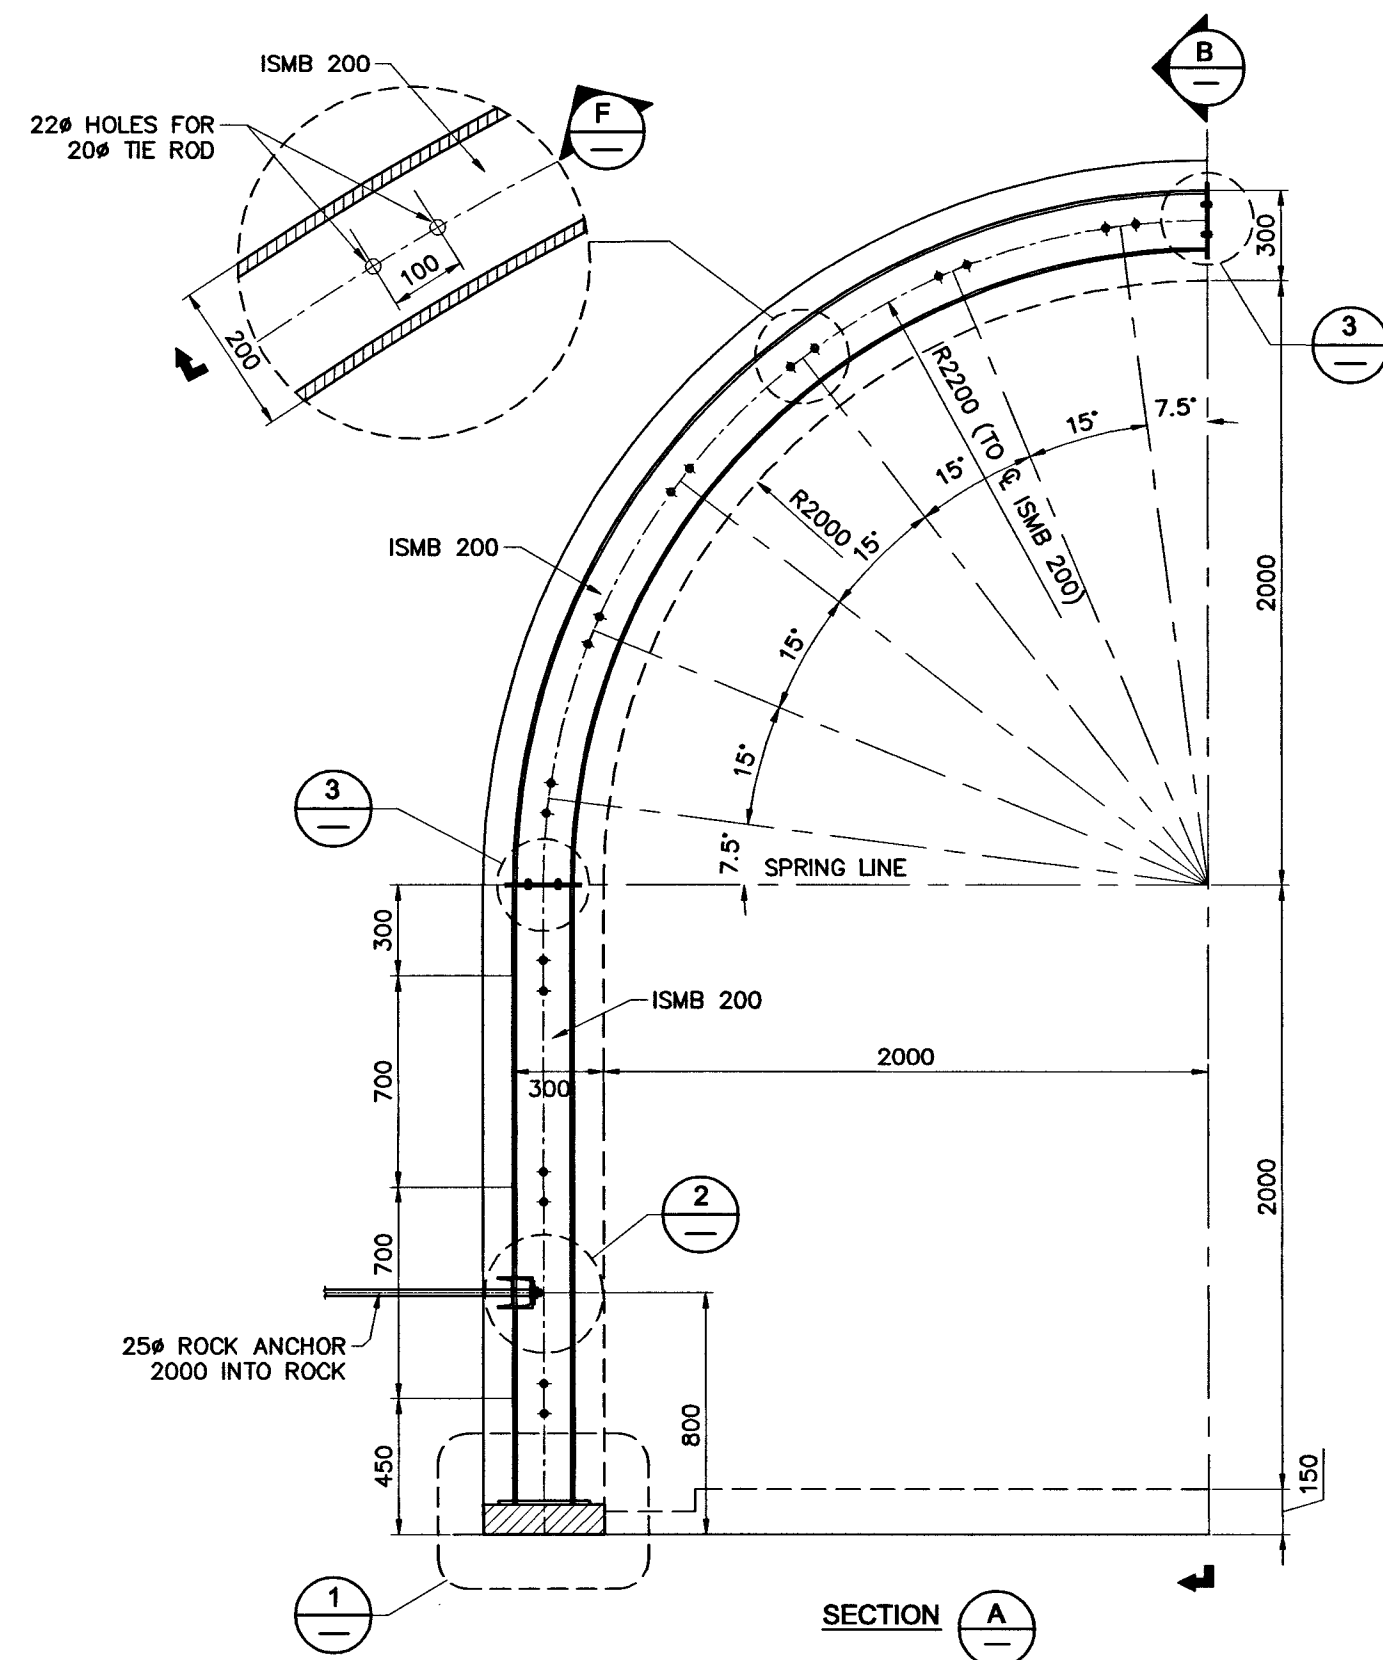


NOTES:-

- सभी मप मिलीमीटर में तथा ऊंचाई मीटर में दिए गए हैं।
ALL DIMENSIONS ARE IN MILLIMETERS AND LEVELS IN METERS.
- ALL STEEL SECTIONS AND PLATES FOR RIB AND ACCESSORIES SHALL CONFORM TO SECTION B-4 OF TECHNICAL SPECIFICATIONS.
- STEEL FOR BOLTS, NUTS AND WASHERS SHALL CONFORM TO IS: 8500.
- ALL WELDING, WELDING ELECTRODES AND WORKMANSHIP SHALL CONFORM TO IS: 814 AND IS: 816.
- FOOTING FOR STEEL RIBS SHALL BE PLACED ON IN-SITU CONCRETE PAD OF M20/A40 GRADE. THE CONCRETE PAD SHALL BE FOUND ON FIRM ROCK.
- THE SPACING OF RIBS SHALL BE 1000 C/C IN CLASS-IV & 750 C/C IN CLASS-VA. THE SPACING OF RIBS MAY BE MODIFIED TO SUIT THE SITE CONDITION WITH THE APPROVAL OF ENGINEER-IN-CHARGE.
- THE LOCATION OF STEEL RIB JOINT, TIE ROD, LOCATION OF WALL ANCHORING MAY BE MODIFIED MARGINALLY TO SUIT THE SITE CONDITION.
- PROFILE OF THE STEEL RIBS MAY BE MODIFIED AT SITE TO INTERFACE WITH THE FORE-POLING PROFILE.

REFERENCE DRAWINGS:-

- NHDB-4CC4-41-DD-1026.

SCALE:

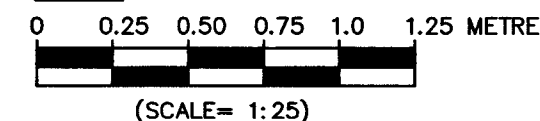

		एन एच पी सी लिमिटेड NHPC Limited (A GOVT. OF INDIA NAVRATNA ENTERPRISE)	
दिबांग बहुउद्देशीय परियोजना DIBANG MULTIPURPOSE PROJECT			
POWER HOUSE ESCAPE GALLERY (4M D-SHAPE) STEEL RIB DETAILS			
06.02.2026 DATE 00 NO.	ISSUED FOR CONSTRUCTION REVISION OR ISSUES	BY: CH. APP. 00 NO.	APPROVED 00 NO.
DESIGN MEMO NO. दिबांग गैलरी	DRG. NO. 41 DD 1027	NHDB 4CC4	00