



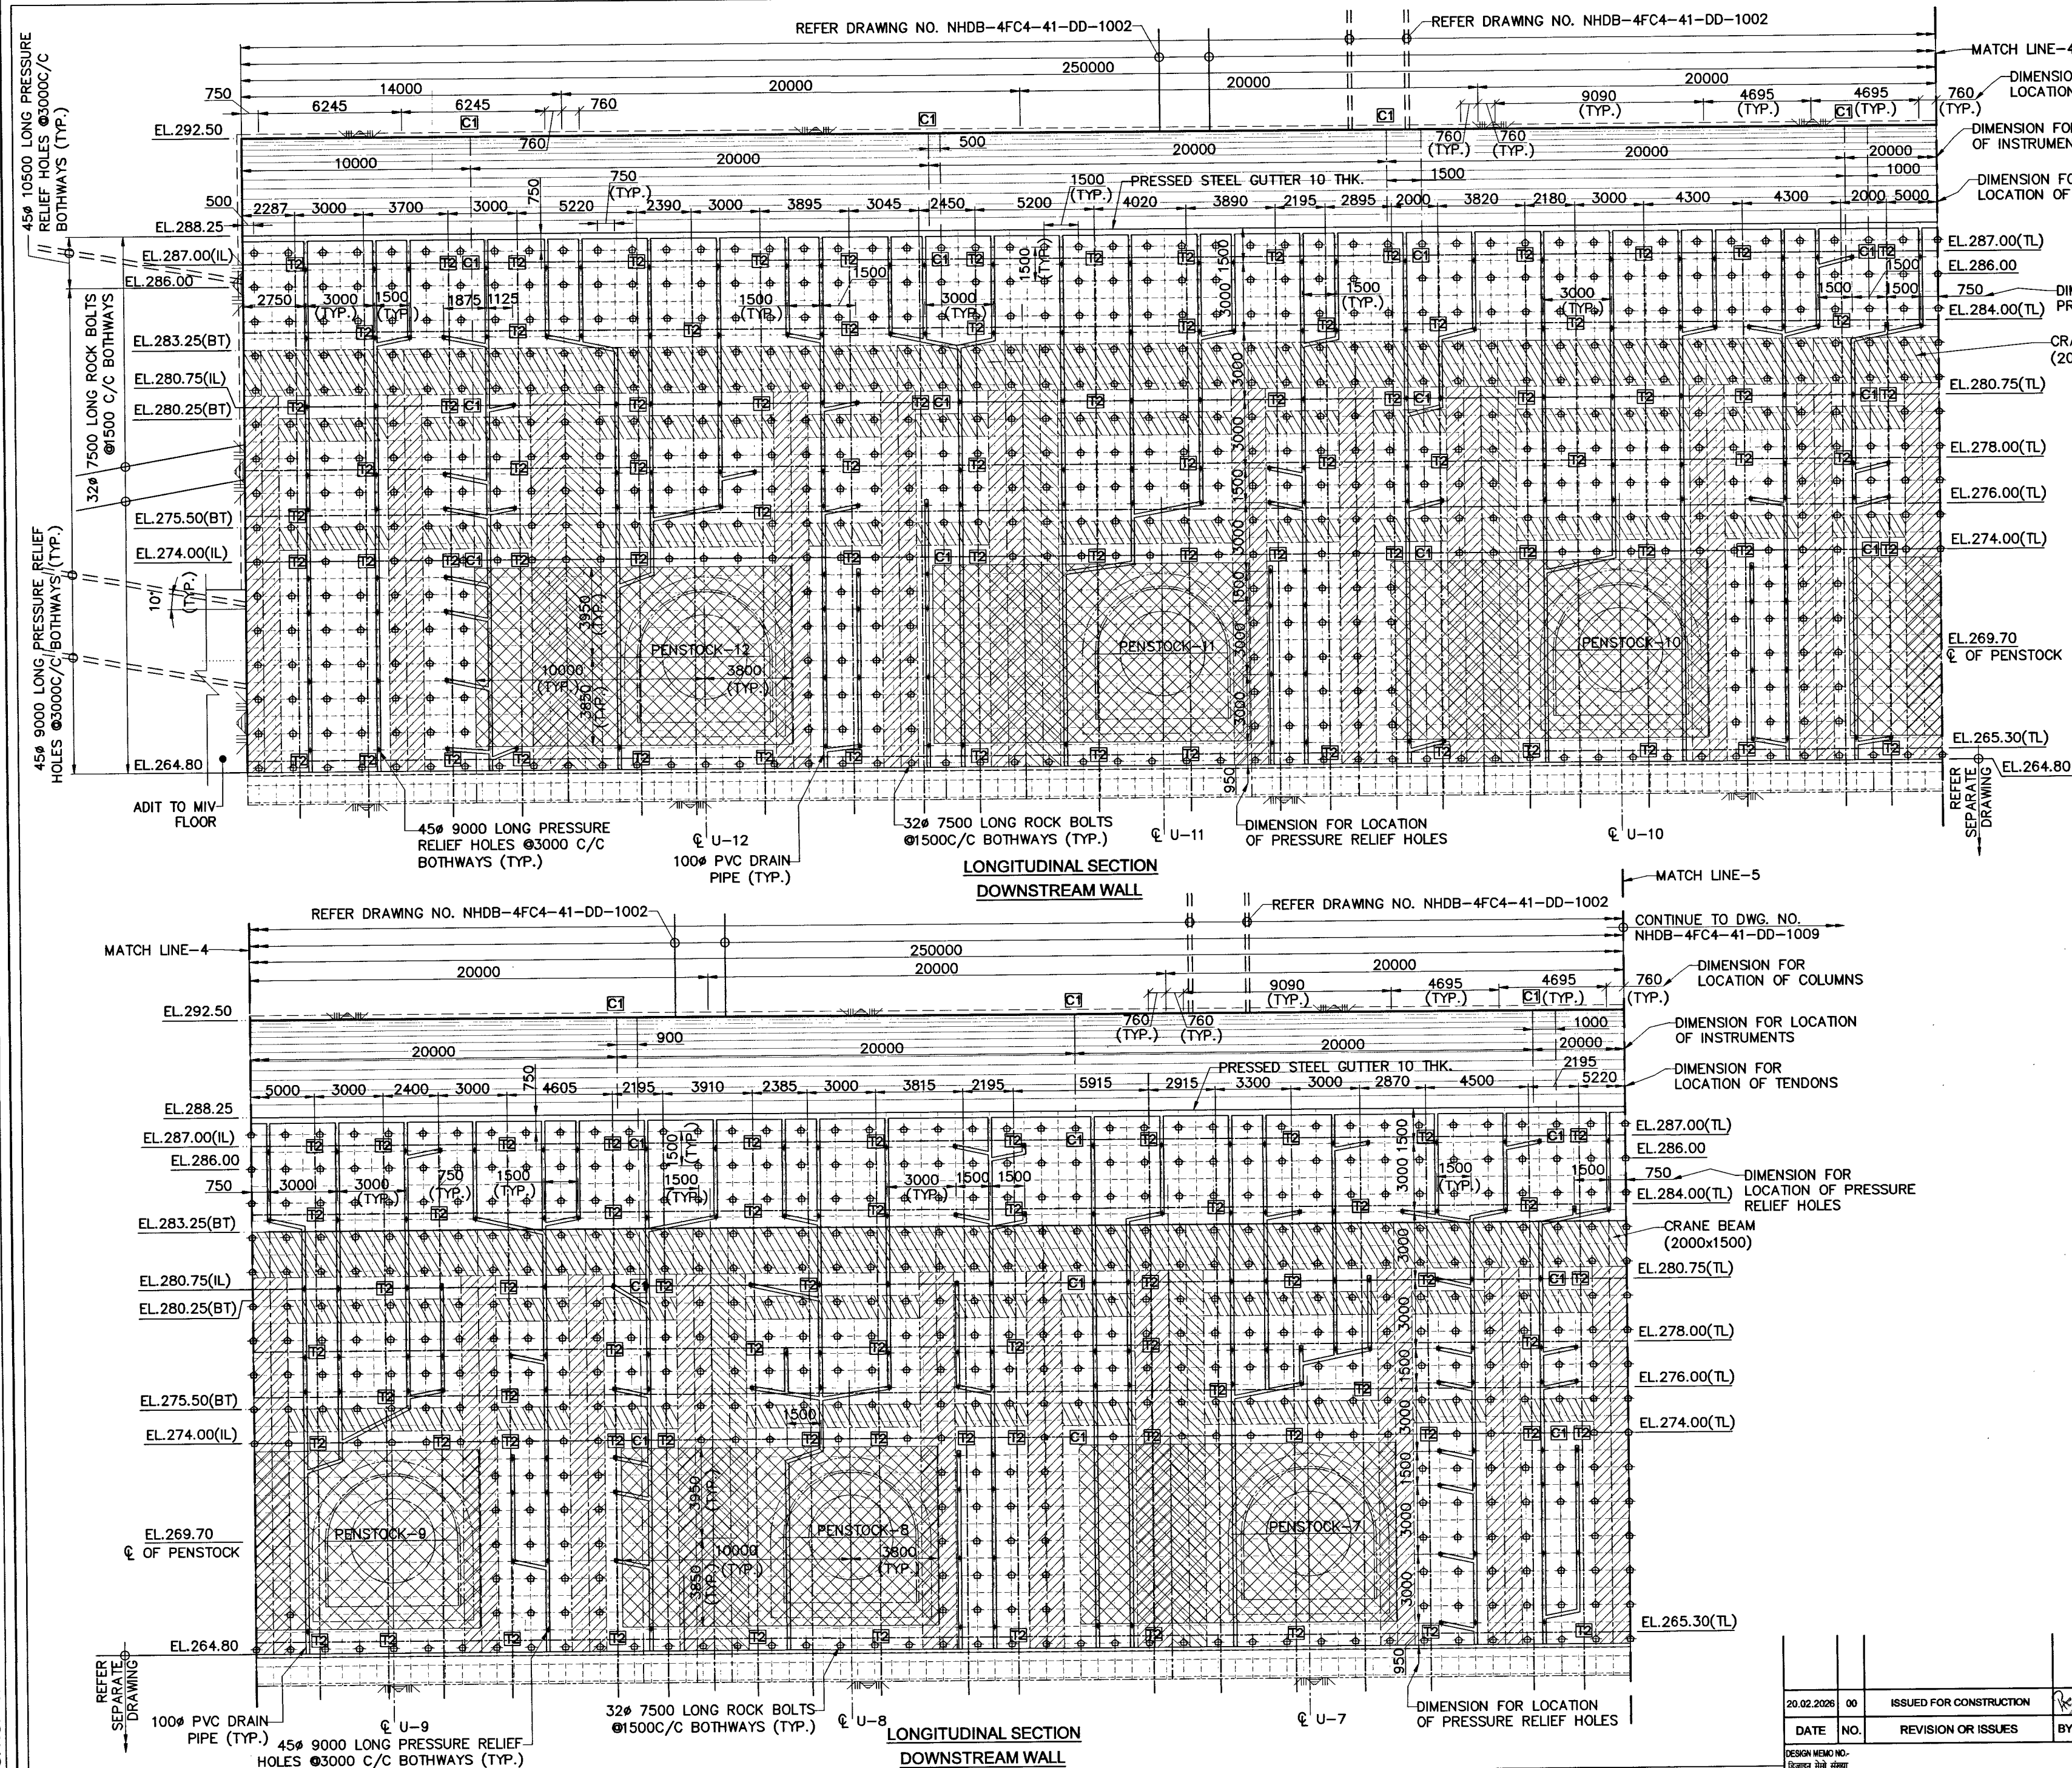

- NOTES:**
- सभी माप मिलीमीटर में तथा ऊंचाई मीटर में दिए गए हैं।
ALL DIMENSIONS ARE IN MILLIMETRE AND ELEVATIONS ARE IN METRE.
 - FOR OTHER NOTES REFER DRAWING NO. NHDB-4FC4-41-DD-1006.
 - THIS DRAWING SHALL BE READ IN CONJUNCTION WITH RELEVANT JUNCTION EXCAVATION DRAWING OF ADITS/PENSTOCKS WITH MIV CAVERN WALL.

- LEGENDS:-**
- 32# 7500 LONG ROCK BOLTS
 - (T2) (TYPE-2)-1200KN GUARANTEED ULTIMATE TENSILE STRENGTH (GUTS), LOCK OFF LOAD SHALL BE 60% OF GUTS, TOTAL LENGTH=36.75M.
 - 45# 9000/10500 LONG PRESSURE RELIEF HOLE
 - × CONVERGENCE MEASUREMENT (OPTICAL TARGETS)
 - ⊙ LOAD CELL (30T CAPACITY)
 - ⊕ MULTIPLE POINT BORE HOLE EXTENSOMETER (5M, 10M, 15M) (3 POINTS)
 - ⊠ × ⊕ ⊙ (COMBINATION OF INSTRUMENTS-1)
 - BT BEAM TOP LEVEL
 - TL TENDONS LEVEL
 - IL INSTRUMENTATION LEVEL
 - ROCK SUPPORTS AND PRESSURE RELIEF HOLES IN MARKED ZONE SHALL BE INSTALLED AS PER RELEVANT JUNCTION DRAWINGS OF INTERFACING STRUCTURE.

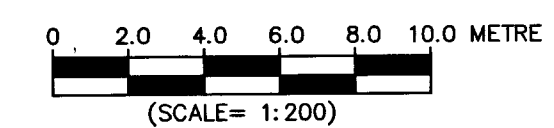

एन एच पी सी लिमिटेड (भारत सरकार का एक अन्तर्गत कर्मा) NHPC Limited (A GOVT. OF INDIA NAVATNA ENTERPRISE)	
दिबांग बहुउद्देशीय परियोजना DIBANG MULTIPURPOSE PROJECT	
MIV CAVERN ROCK SUPPORTS, CABLE TENDONS, PRESSURE RELIEF HOLES AND INSTRUMENTATION TYPICAL ARRANGEMENT WALL ELEVATION	
SHEET 3 OF 5	
20.02.2026 00 DATE NO.	ISSUED FOR CONSTRUCTION REVISION OR ISSUES
BY: CH. APP.	APPROVED
DESIGN MEMO NO- डिबांग में सेला	DATE FEB. 2026 DRG. NO. NHDB 4FC4 41 DD 1008 00