



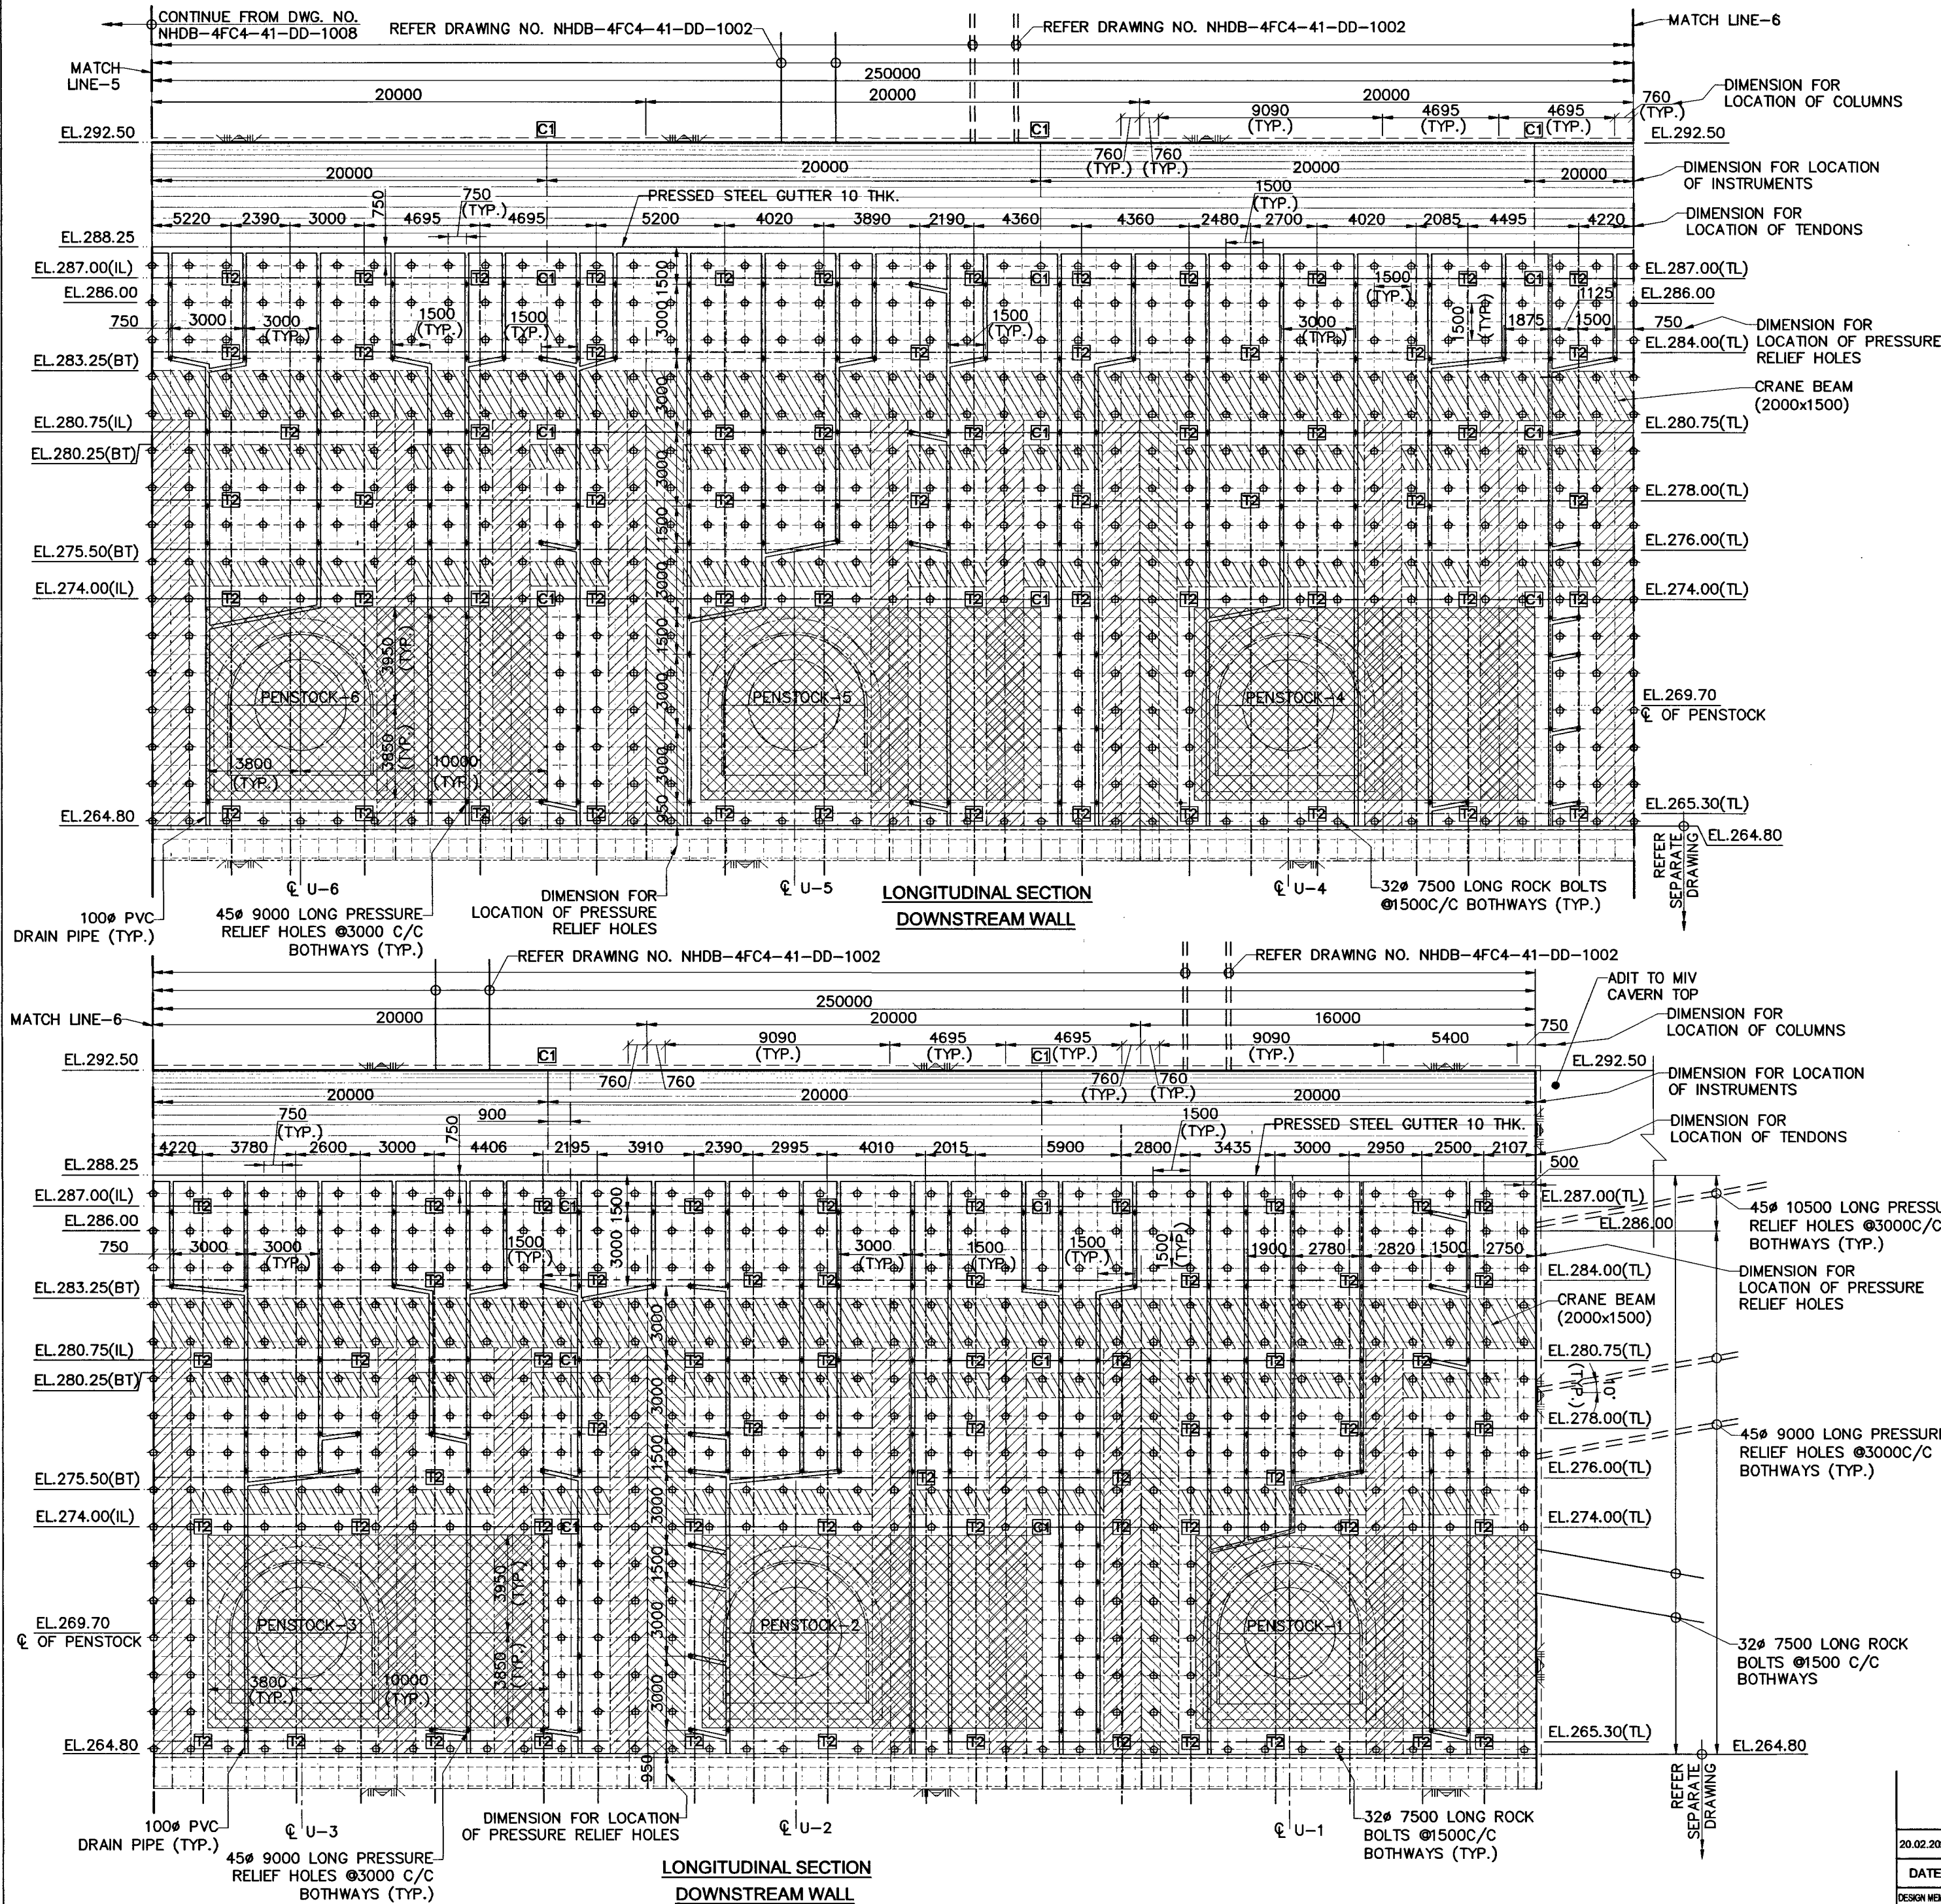

- NOTES:**
- सभी माप मिलीमीटर में तथा ऊंचाई मीटर में दिए गए हैं।  
ALL DIMENSIONS ARE IN MILLIMETRE AND ELEVATIONS ARE IN METRE.
  - FOR OTHER NOTES REFER DRAWING NO. NHDB-4FC4-41-DD-1006.
  - THIS DRAWING SHALL BE READ IN CONJUNCTION WITH RELEVANT JUNCTION EXCAVATION DRAWING OF ADITS/PENSTOCKS WITH MIV CAVERN WALL.

- LEGENDS:-**
- 32# 7500 LONG ROCK BOLTS
  - (TYPE-2)-1200KN GUARANTEED ULTIMATE TENSILE STRENGTH (GUTS), LOCK OFF LOAD SHALL BE 60% OF GUTS, TOTAL LENGTH=36.75M.
  - 45# 9000/10500 LONG PRESSURE RELIEF HOLE
  - × CONVERGENCE MEASUREMENT (OPTICAL TARGETS)
  - ⊙ LOAD CELL (30T CAPACITY)
  - # MULTIPLE POINT BORE HOLE EXTENSOMETER (5M, 10M, 15M) (3 POINTS)
  - ⊠ × # ⊙ (COMBINATION OF INSTRUMENTS-1)
  - BT BEAM TOP LEVEL
  - TL TENDONS LEVEL
  - IL INSTRUMENTATION LEVEL
  - ROCK SUPPORTS AND PRESSURE RELIEF HOLES IN MARKED ZONE SHALL BE INSTALLED AS PER RELEVANT JUNCTION DRAWINGS OF INTERFACING STRUCTURE.

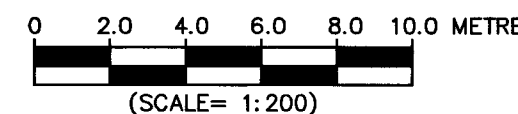

|   |                                   |
|---|-----------------------------------|
| <p>एन एच पी सी लिमिटेड<br/>NHPC Limited<br/>(A GOVT. OF INDIA NAVRATNA ENTERPRISE)</p>                                                       |                                   |
| <p>दिवांग बहुउद्देशीय परियोजना<br/>DIBANG MULTIPURPOSE PROJECT</p>                                                                           |                                   |
| <p>MIV CAVERN<br/>ROCK SUPPORTS, CABLE TENDONS,<br/>PRESSURE RELIEF HOLES AND INSTRUMENTATION<br/>TYPICAL ARRANGEMENT<br/>WALL ELEVATION</p> |                                   |
| <p>SHEET 4 OF 5</p>   |                                   |
| <p>20.02.2026 00</p>   | <p>ISSUED FOR CONSTRUCTION</p>    |
| <p>DATE NO.</p>   | <p>REVISION OR ISSUES</p>         |
| <p>BY. CH. APP.</p>   | <p>APPROVED</p>                   |
| <p>DESIGN MEMO NO.<br/>डिजाइन मेमो संख्या</p>                                                                                                | <p>DATE<br/>दिनांक</p>            |
| <p>FEB. 2026</p>   | <p>DRG. NO.<br/>डिजाइन संख्या</p> |
| <p>NHDB 4FC4 41 DD 1009 00</p>   | <p>00</p>                         |