




CONTINUE FROM DRG. NO.
NHDB-4FC4-41-DD-1011

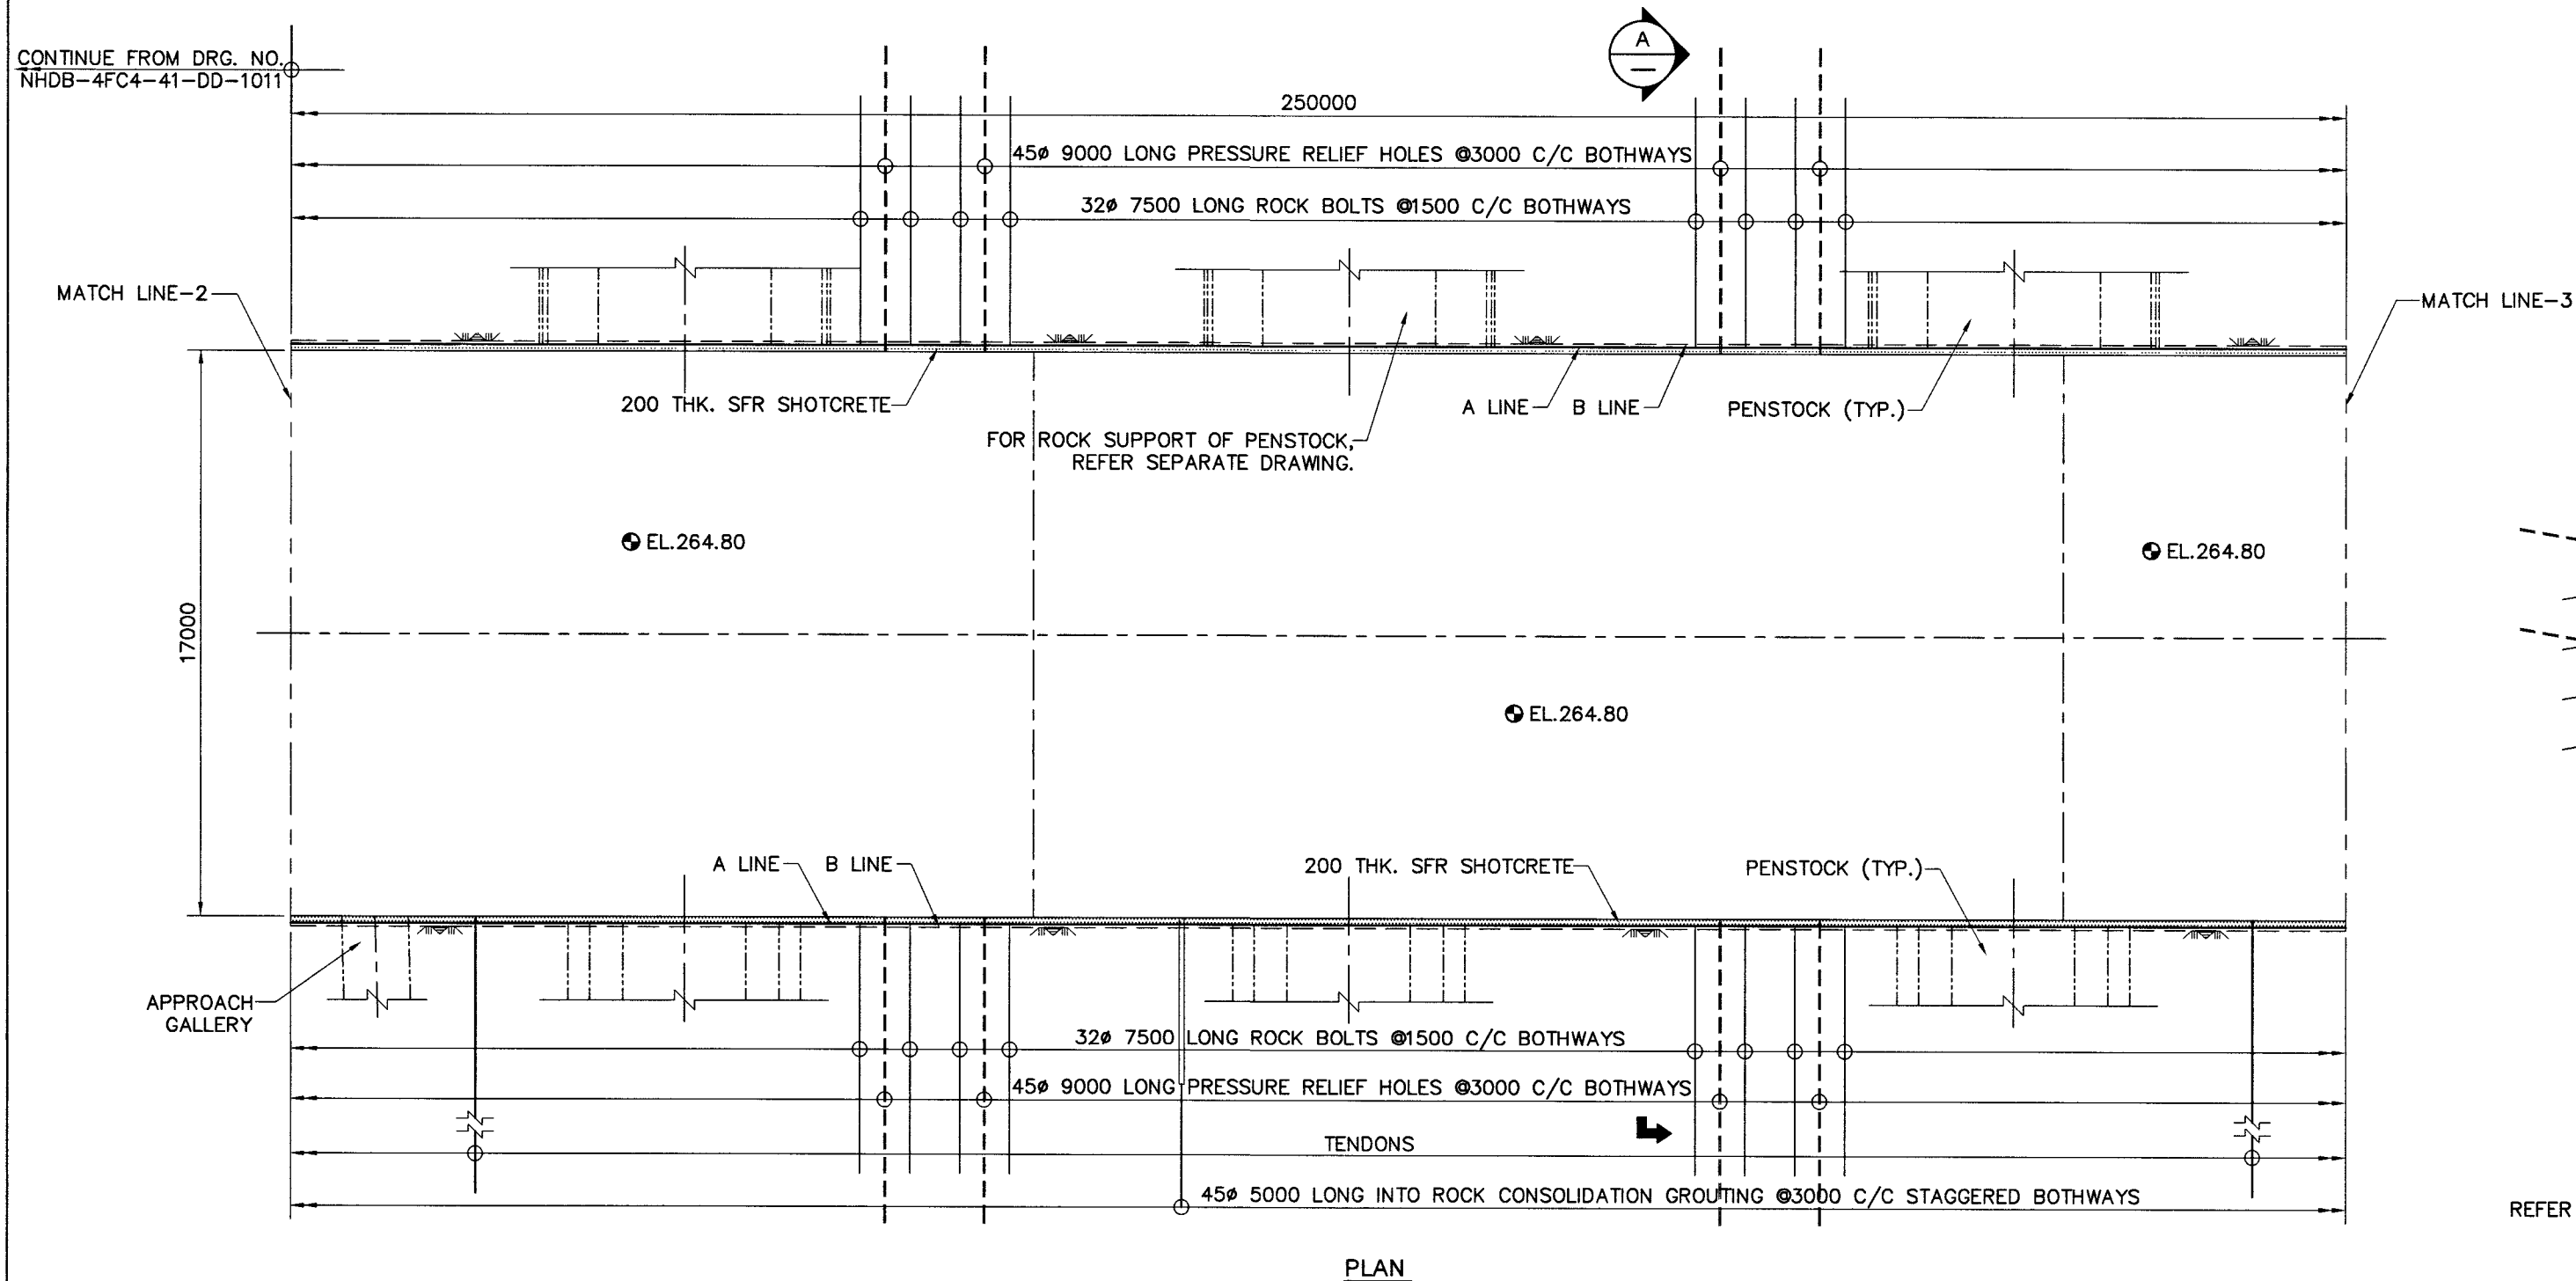

PLAN

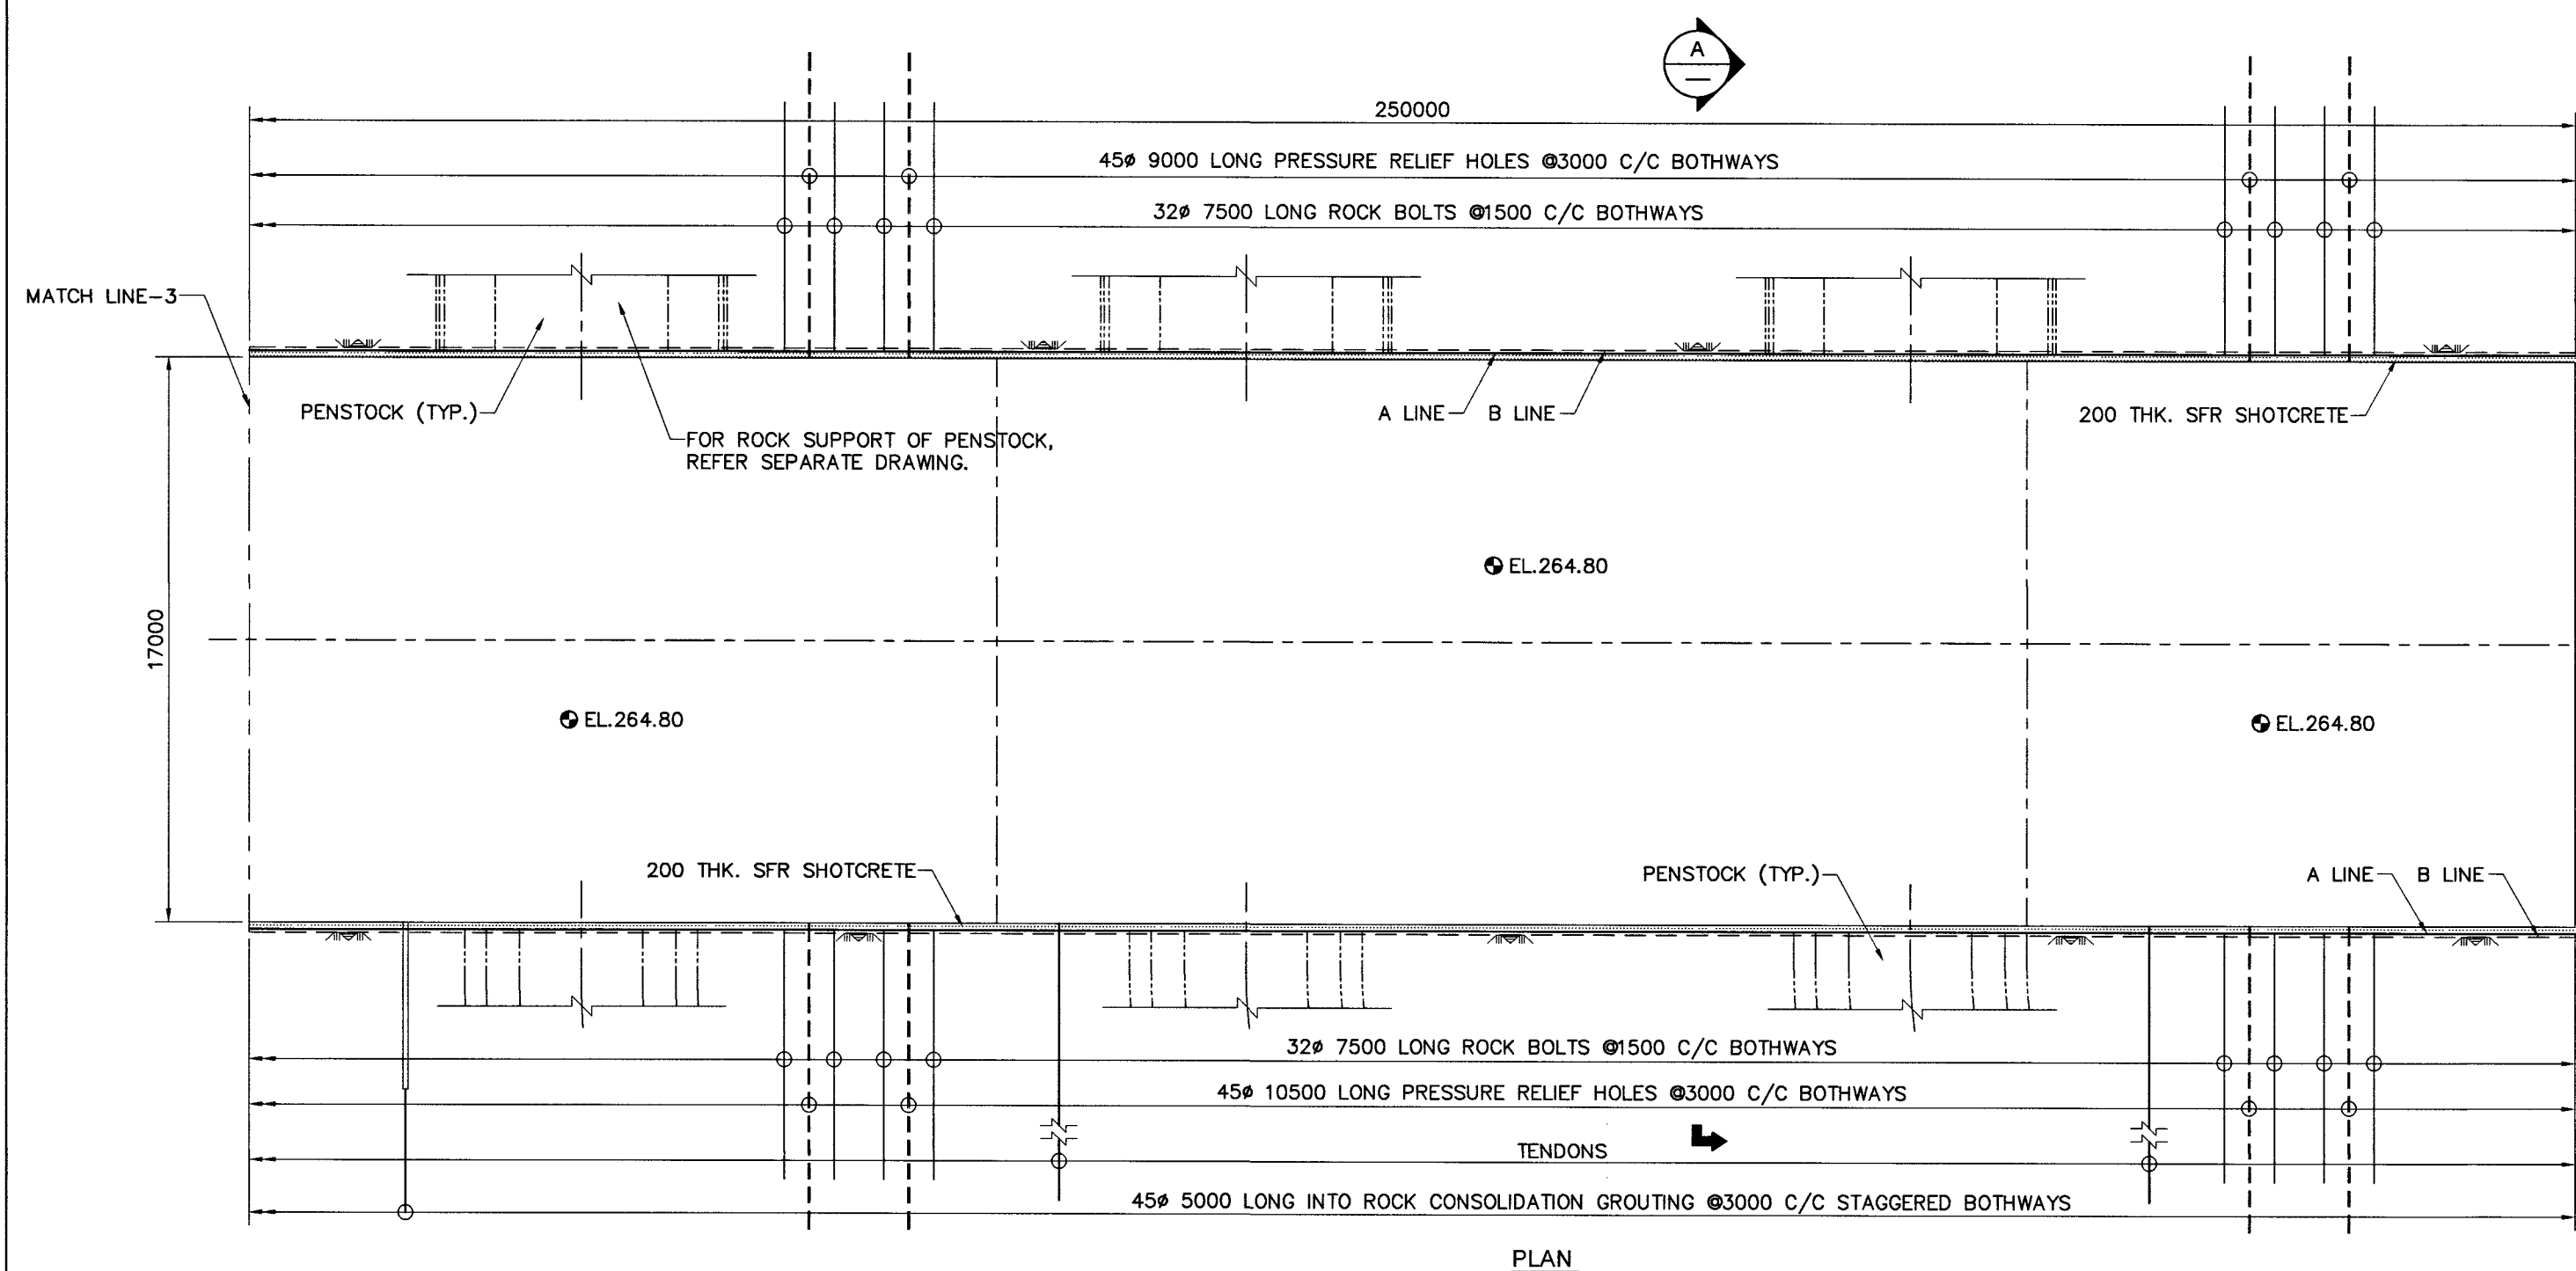

PLAN

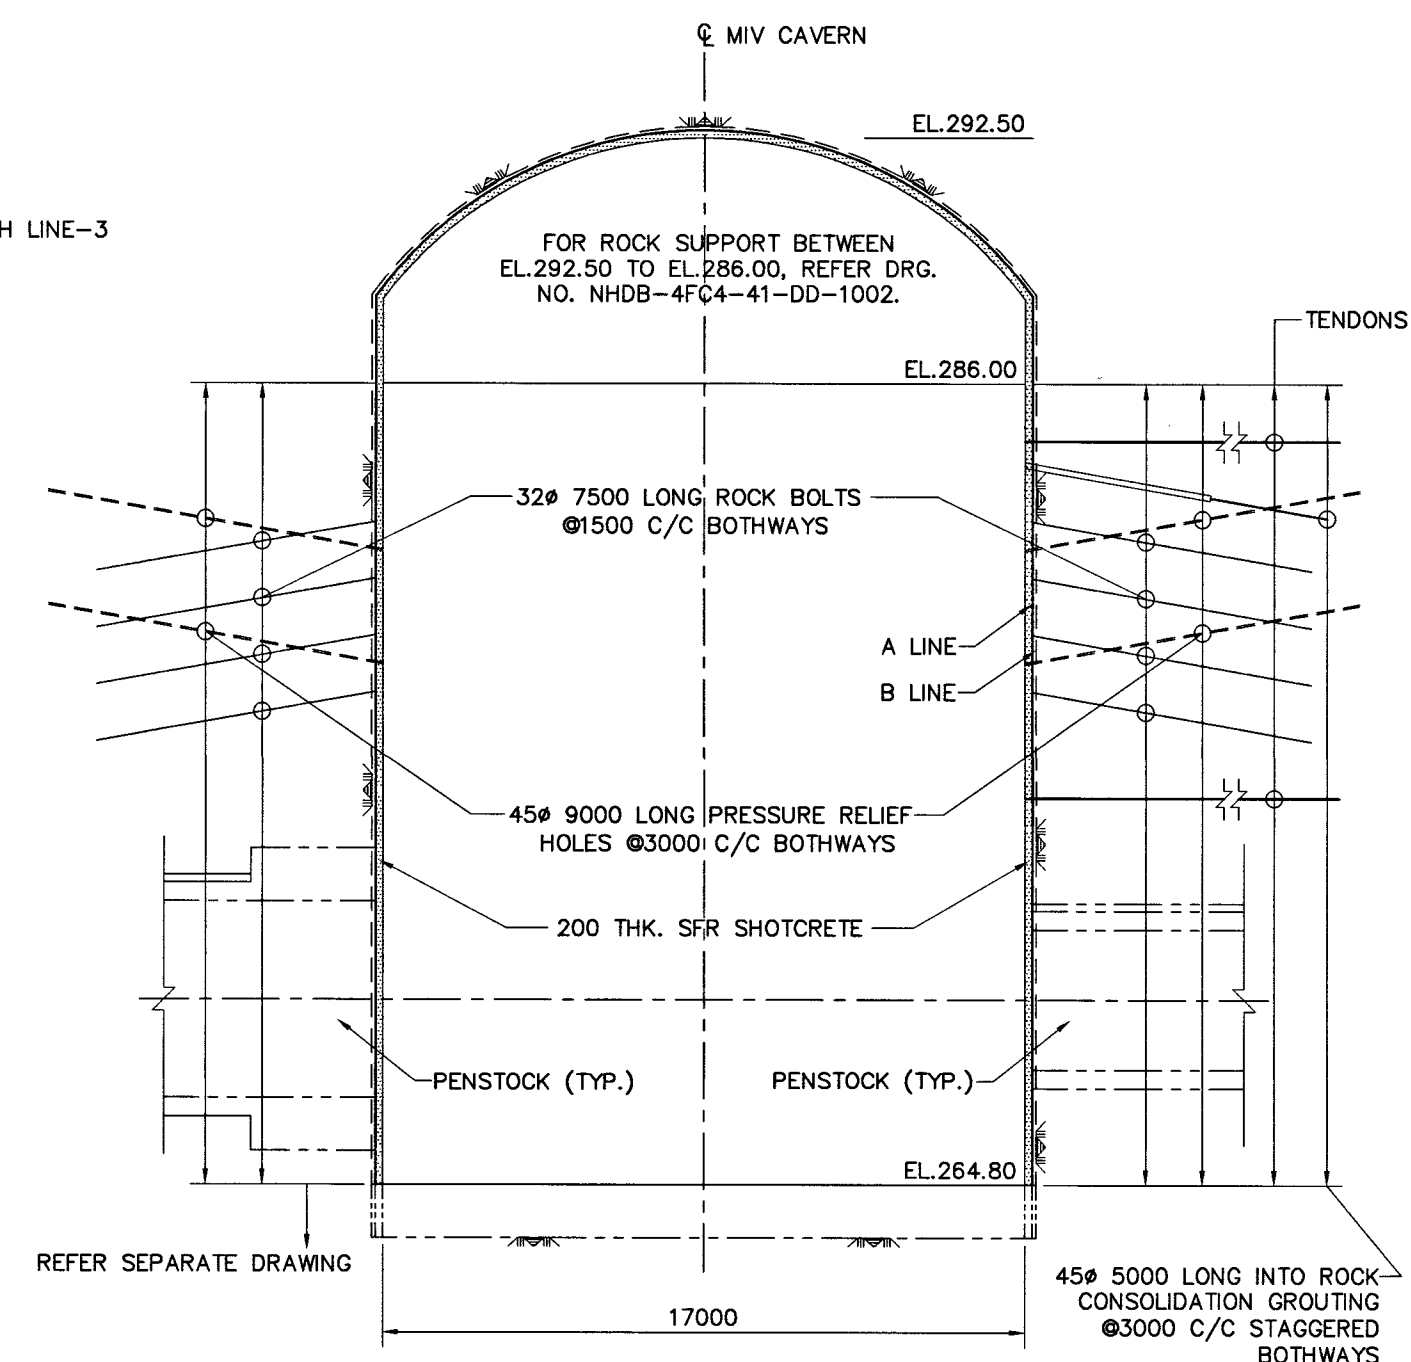

TYPICAL SECTION

ON  

- NOTES:**
1. सभी माप मिलीमीटर में तथा ऊचाई मीटर में लिए गए हैं।
ALL DIMENSIONS ARE IN MILLIMETRE AND ELEVATIONS ARE IN METRE.
2. FOR OTHER NOTES, REFER DRAWING NO.
NHDB-4FC4-41-DD-1011.

SCALE:
0 2.0 4.0 6.0 8.0 10.0 METRE

	एन एच पी सी लिमिटेड (भारत सरकार का उद्यम) NHPC Limited (A GOVT. OF INDIA ENTERPRISE)
दिबांग बहुउद्देशीय परियोजना DIBANG MULTIPURPOSE PROJECT	

**MIV CAVERN
EXCAVATION AND ROCK SUPPORTS
FROM EL. 286.00M TO EL. 264.80M**

SHEET 2 OF 2

SHEET 2 OF 2											
31.03.2026	00	ISSUED FOR CONSTRUCTION	BY	CH. APP.	DESIGN	SUBMITTED	RECOMMENDED			APPROVED	
DATE	NO.	REVISION OR ISSUES	BY	CH. APP.	डिजाइन	प्रस्तुत	अनुमोदित	अनुमोदित	REVISION	अनुमोदित	अनुमोदित
DESIGN MEMO NO.					डिजाइन मेमो संख्या						
					DATE	MAR 2026	DRG. NO.	NHDB	4FC4	41 DD	1012 00

IMS/DED/F-02 REV. NO. : 03 EFF. DATE 21.07.2015

DRG. NO. NHDB-4FC4-41-DD-1012-00