
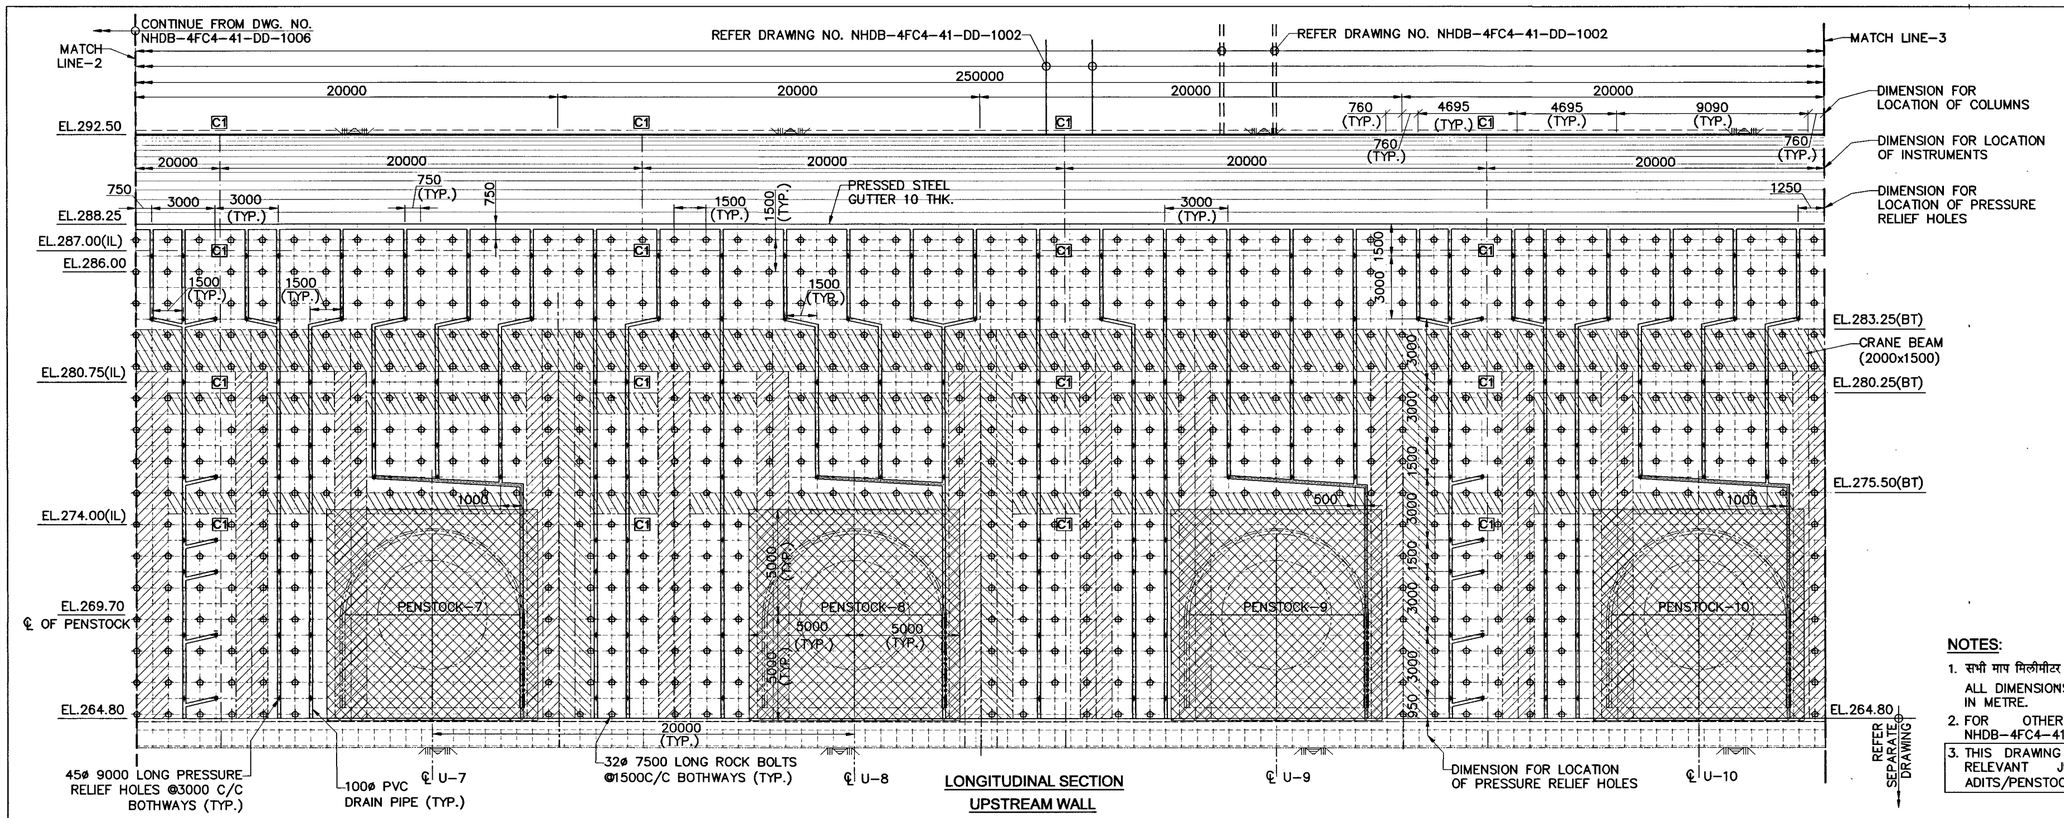



LONGITUDINAL SECTION
UPSTREAM WALL

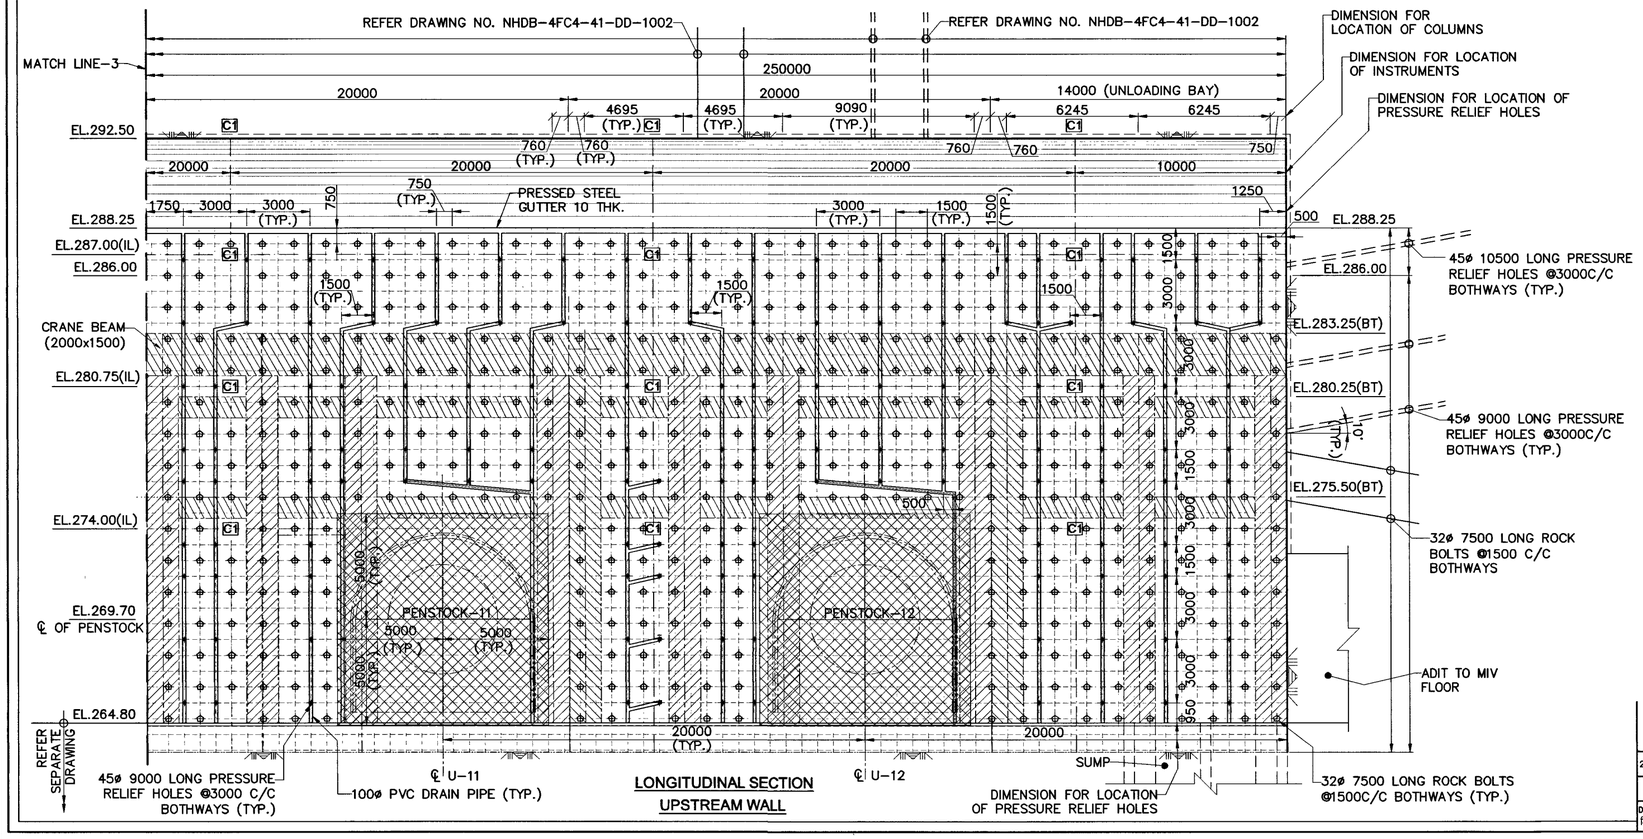


LONGITUDINAL SECTION
UPSTREAM WALL

## NOTES:

1. सभी माप मिलीमीटर में तथा ऊंचाई मीटर में दिए गए हैं ।
   ALL DIMENSIONS ARE IN MILLIMETRE AND ELEVATIONS ARE IN METRE.
2. FOR OTHER NOTES REFER DRAWING NO. NHDB-4FC4-41-DD-1006.
3. THIS DRAWING SHALL BE READ IN CONJUNCTION WITH RELEVANT JUNCTION EXCAVATION DRAWING OF ADITS/PENSTOCKS WITH MIV CAVERN WALL.

## LEGENDS:-

- 32ø 7500 LONG ROCK BOLTS
- 45ø 9000/10500 LONG PRESSURE RELIEF HOLE
- CONVERGENCE MEASURMENT (OPTICAL TARGETS)
- LOAD CELL (30T CAPACITY)
- MULTIPLE POINT BORE HOLE EXTENSOMETER (5M, 10M, 15M) (3 POINTS)
- C1 × # ⊙ (COMBINATION OF INSTRUMENTS-1)
- BT BEAM TOP LEVEL
- IL INSTRUMENTATION LEVEL
- ROCK SUPPORTS AND PRESSURE RELIEF HOLES IN MARKED ZONE SHALL BE INSTALLED AS PER RELEVANT JUNCTION DRAWINGS OF INTERFACING STRUCTURE.

0 2.0 4.0 6.0 8.0 10.0 METRE
(SCALE= 1:200)

एन एच पी सी लिमिटेड
(भारत सरकार का एक नवरत्न उद्यम)
NHPC Limited
(A GOVT. OF INDIA NAVRATNA ENTERPRISE)
A Navratna Company

दिबांग बहुउद्देशीय परियोजना
DIBANG MULTIPURPOSE PROJECT

MIV CAVERN
ROCK SUPPORTS, CABLE TENDONS,
PRESSURE RELIEF HOLES AND INSTRUMENTATION
TYPICAL ARRANGEMENT
WALL ELEVATION
SHEET 2 OF 5

| DATE | NO. | REVISION OR ISSUES | BY. | CH. | APP |
|---|---|---|---|---|---|
| 20.02.2026 | 00 | ISSUED FOR CONSTRUCTION | | | |

DESIGN MEMO NO.- डिजाइन मेमो संख्या

| DRAWN अंकित | SUBMITTED प्रस्तुत | RECOMMENDED अनुशंसित | APPROVED अनुमोदन |
|---|---|---|---|
| VINAY KUMAR | PRABHAT ASHWAL | HITESH JOSHI RAJEEV KUMAR | DEM/HM |

| DATE दिनांक | DRG. NO. ड्रेग संख्या | | | | | |
|---|---|---|---|---|---|---|
| FEB. 2026 | NHDB | 4FC4 | 41 | DD | 1007 | 00 |

DRG. NO. NHDB-4FC4-41-DD-1007-00