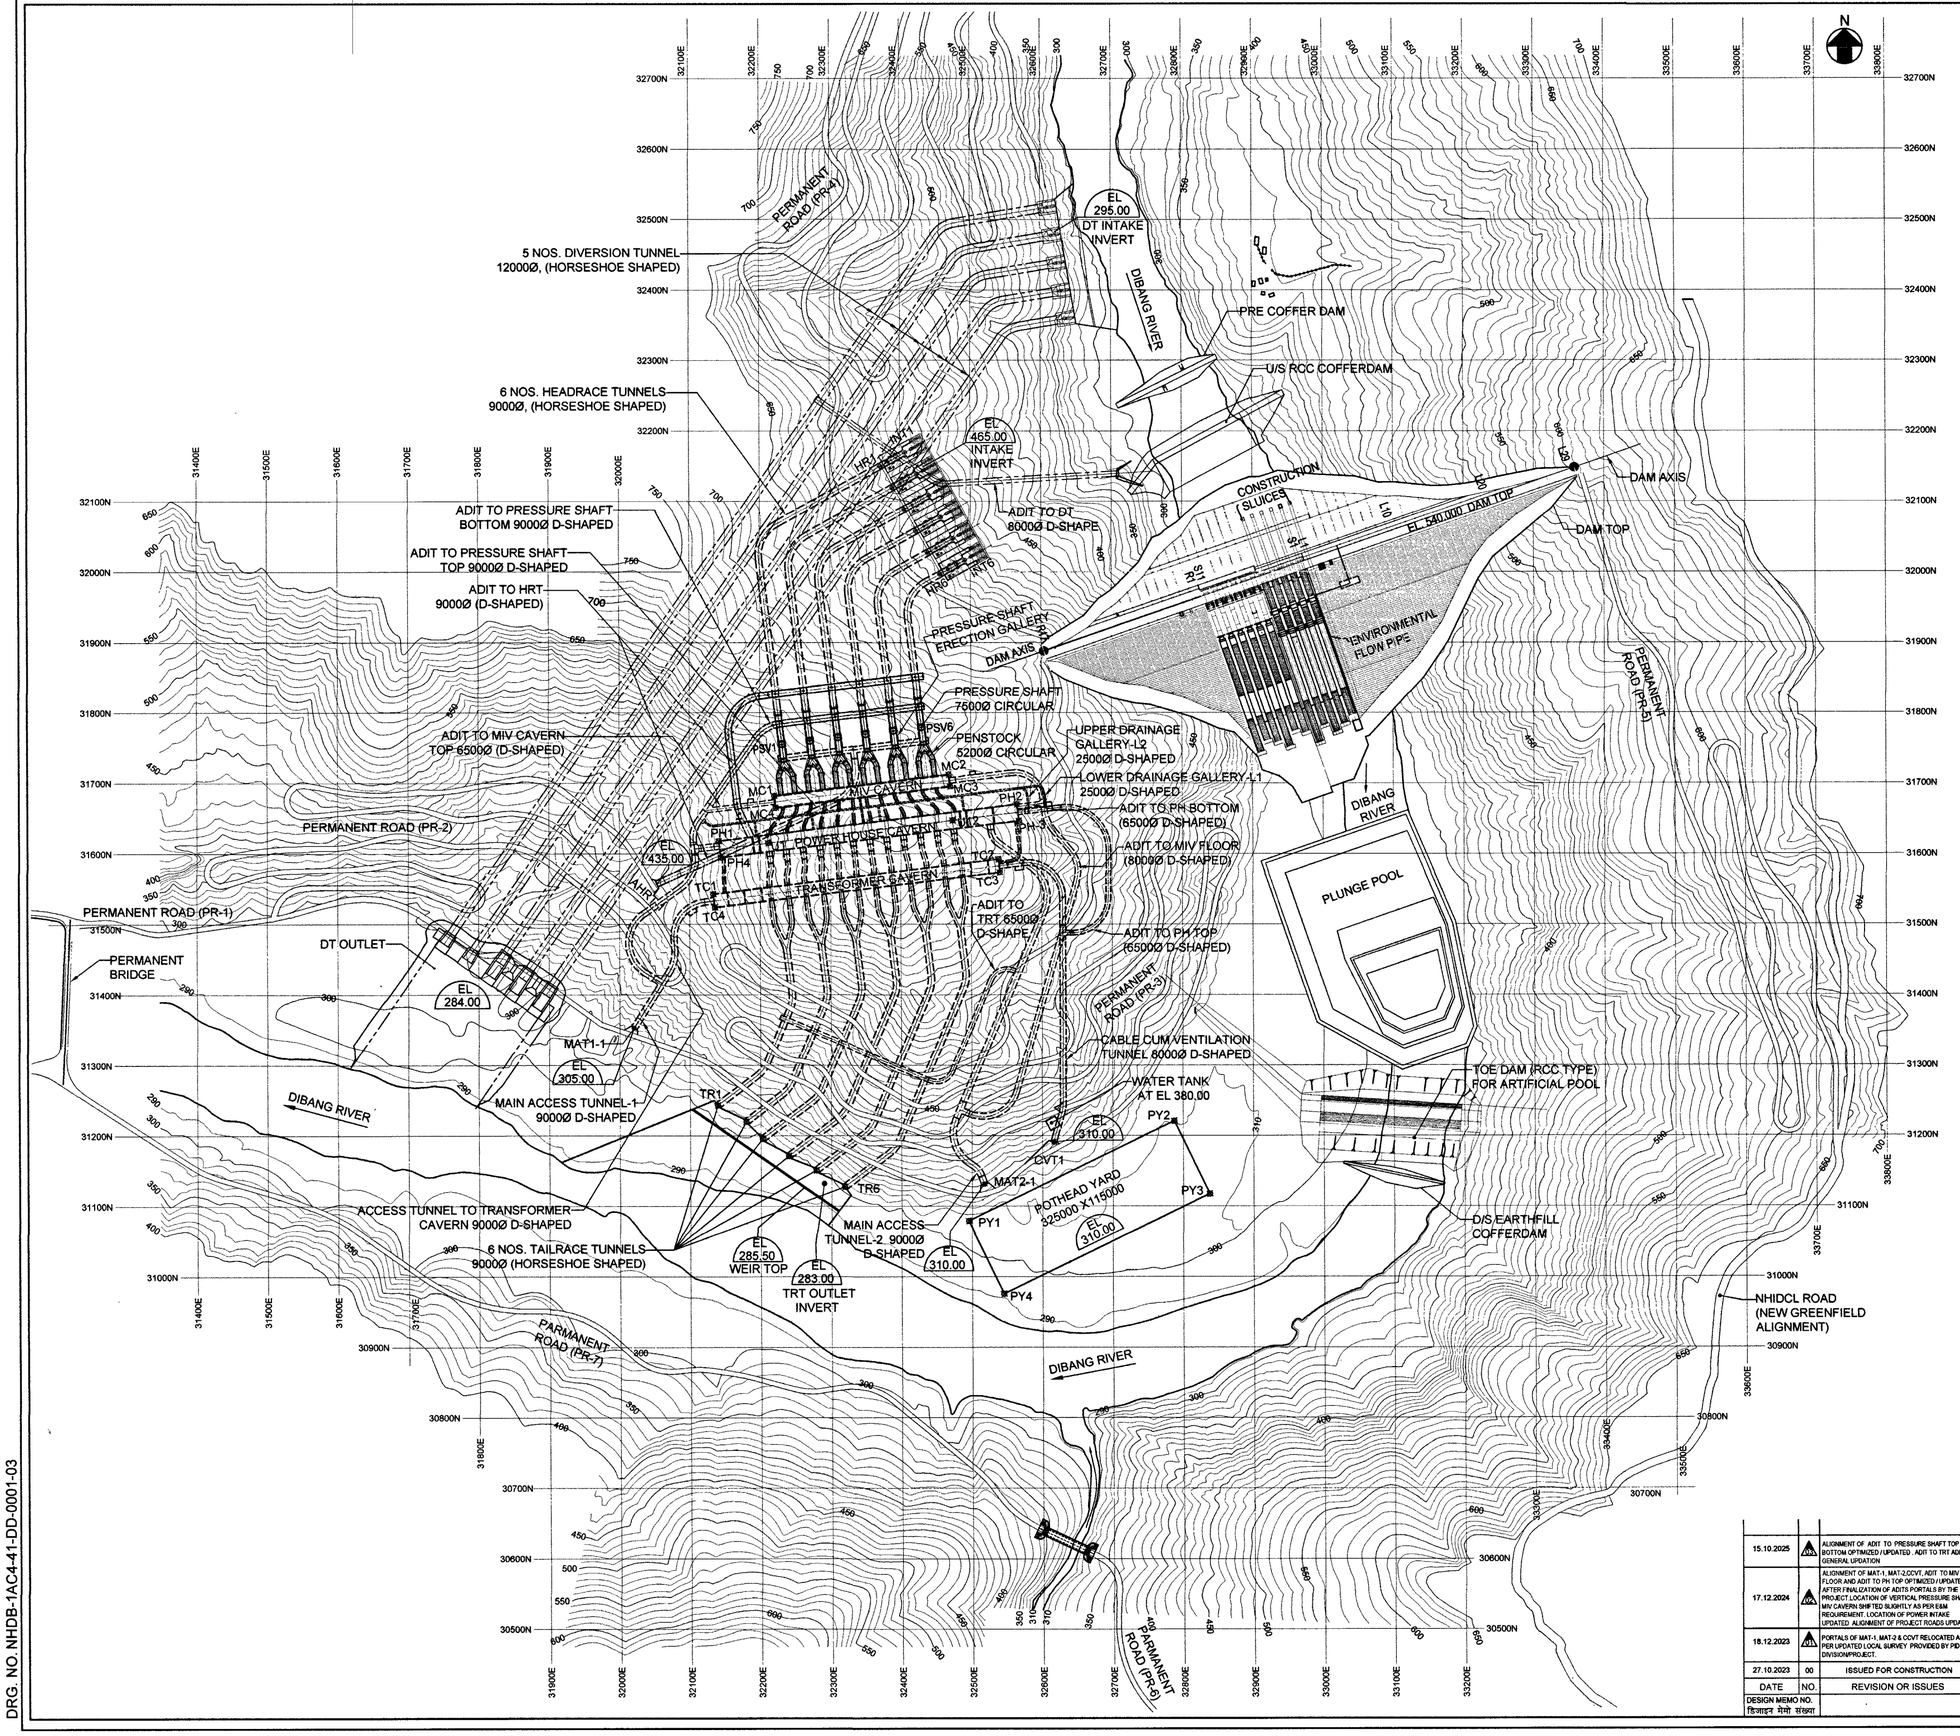



| POINTS | DESCRIPTION | NORTHING IN METRE | EASTING IN METRE | ELEVATION IN METRE |
|---|---|---|---|---|
| MAT1-1 | MAIN ACCESS TUNNEL-1 | 31352.819 | 32020.194 | 305.00 |
| MAT2-1 | MAIN ACCESS TUNNEL-2 | 31131.292 | 32517.573 | 310.00 |
| CVT1 | CABLE CUM VENTILATION TUNNEL | 31191.170 | 32615.998 | 310.00 |
| AHRT-1 | ADIT TO HRT | 31557.297 | 32053.283 | 435.00 |
| | | | | |
| INT1 | HRT INTAKE-1 | 32169.498 | 32407.056 | 465.00 |
| INT2 | HRT INTAKE-2 | 32138.898 | 32424.045 | 465.00 |
| INT3 | HRT INTAKE-3 | 32108.298 | 32441.034 | 465.00 |
| INT4 | HRT INTAKE-4 | 32077.698 | 32458.023 | 465.00 |
| INT5 | HRT INTAKE-5 | 32047.097 | 32475.012 | 465.00 |
| INT6 | HRT INTAKE-6 | 32016.497 | 32492.001 | 465.00 |
| | | | | |
| HR1 | HEADRACE TUNNEL-1 | 32149.767 | 32371.516 | 465.00 |
| HR2 | HEADRACE TUNNEL-2 | 32119.166 | 32388.505 | 465.00 |
| HR3 | HEADRACE TUNNEL-3 | 32088.566 | 32405.494 | 465.00 |
| HR4 | HEADRACE TUNNEL-4 | 32057.966 | 32422.483 | 465.00 |
| HR5 | HEADRACE TUNNEL-5 | 32027.366 | 32439.472 | 465.00 |
| HR6 | HEADRACE TUNNEL-6 | 31996.765 | 32456.461 | 465.00 |
| | | | | |
| PSV1 | PRESSURE SHAFT VERTICAL-1 | 31754.660 | 32231.252 | 454.50 |
| PSV2 | PRESSURE SHAFT VERTICAL-2 | 31759.535 | 32270.954 | 454.50 |
| PSV3 | PRESSURE SHAFT VERTICAL-3 | 31764.410 | 32310.656 | 454.50 |
| PSV4 | PRESSURE SHAFT VERTICAL-4 | 31769.285 | 32350.358 | 454.50 |
| PSV5 | PRESSURE SHAFT VERTICAL-5 | 31774.159 | 32390.060 | 454.50 |
| PSV6 | PRESSURE SHAFT VERTICAL-6 | 31779.034 | 32429.762 | 454.50 |
| | | | | |
| MC1 | MIV CAVERN | 31681.851 | 32220.042 | 264.80 |
| MC2 | MIV CAVERN | 31712.319 | 32468.179 | 264.80 |
| MC3 | MIV CAVERN | 31695.445 | 32470.25 | 264.80 |
| MC4 | MIV CAVERN | 31664.978 | 32222.114 | 264.80 |
| | | | | |
| PH1 | POWER HOUSE CAVERN | 31617.997 | 32141.036 | 283.70 |
| PH2 | POWER HOUSE CAVERN | 31670.035 | 32564.853 | 283.70 |
| PH3 | POWER HOUSE CAVERN | 31646.710 | 32567.717 | 283.70 |
| PH4 | POWER HOUSE CAVERN | 31594.672 | 32143.900 | 283.70 |
| U1 | POWER HOUSE UNIT-1 | 31615.287 | 32211.280 | 269.70 |
| U12 | POWER HOUSE UNIT-12 | 31647.461 | 32473.312 | 269.70 |
| | | | | |
| TC1 | TRANSFORMER CAVERN | 31542.599 | 32133.358 | 312.50 |
| TC2 | TRANSFORMER CAVERN | 31592.298 | 32538.118 | 312.50 |
| TC3 | TRANSFORMER CAVERN | 31573.439 | 32540.433 | 312.50 |
| TC4 | TRANSFORMER CAVERN | 31523.741 | 32135.673 | 312.50 |
| | | | | |
| TR1 | TAIL RACE TUNNEL-1 | 31240.673 | 32135.826 | 283.00 |
| TR2 | TAIL RACE TUNNEL-2 | 31213.155 | 32170.388 | 283.00 |
| TR3 | TAIL RACE TUNNEL-3 | 31203.900 | 32213.538 | 283.00 |
| TR4 | TAIL RACE TUNNEL-4 | 31178.910 | 32249.762 | 283.00 |
| TR5 | TAIL RACE TUNNEL-5 | 31157.772 | 32287.601 | 283.00 |
| TR6 | TAIL RACE TUNNEL-6 | 31130.452 | 32322.956 | 283.00 |
| | | | | |
| PY1 | POTHEAD YARD | 31079.104 | 32494.879 | 310.00 |
| PY2 | POTHEAD YARD | 31220.843 | 32787.343 | 310.00 |
| PY3 | POTHEAD YARD | 31117.356 | 32837.497 | 310.00 |
| PY4 | POTHEAD YARD | 30975.617 | 32545.033 | 310.00 |

NOTES:

1. सभी माप मिलीमीटर में, ग्रिड तथा ऊचांई मीटर में दिए गए हैं ।
   ALL DIMENSIONS ARE IN MILLIMETRE, GRIDS AND ELEVATIONS ARE IN METRE.
2. GRIDS HAVE BEEN REPRODUCED FROM S.O.I. SHEET. THE ACCURACY OF THE GRID SYSTEM SHALL BE ESTABLISHED WITH EXISTING S.O.I. BENCH MARK AT SITE BEFORE ADOPTING CO-ORDINATES. CONTOURS SHOWN ARE TAKEN FROM S.O.I. CONTOUR MAP, SAME SHALL BE VERIFIED WITH EXISTING S.O.I. BENCH MARKS AT SITE.
3. FOR DETAILED SETTING OUT OF EACH STRUCTURE REFER SEPARATE DRAWINGS.
4. PROJECT ROADS SHOWN ARE INDICATIVE.

SCALE:

0 60 120 180 240 300 METRE

| | | | | | |
|---|---|---|---|---|---|
| 15.10.2025 | 4 | ALIGNMENT OF ADIT TO PRESSURE SHAFT TOP & BOTTOM OPTIMIZED / UPDATED , ADIT TO TRT ADDED. GENERAL UPDATION | | | |
| 17.12.2024 | 3 | ALIGNMENT OF MAT-1, MAT-2,CVT, ADIT TO MIV FLOOR AND ADIT TO PH TOP OPTIMIZED / UPDATED AFTER FINALIZATION OF ADITS PORTALS BY THE PROJECT, LOCATION OF VERTICAL PRESSURE SHAFT & MIV CAVERN SHIFTED SLIGHTLY AS PER E&M REQUIREMENT. LOCATION OF POWER INTAKE UPDATED. ALIGNMENT OF PROJECT ROADS UPDATED. | Sd/- | Sd/- | Sd/- |
| 18.12.2023 | 2 | PORTALS OF MAT-1, MAT-2 & CCVT RELOCATED AS PER UPDATED LOCAL SURVEY PROVIDED BY PD DIVISIONPROJECT. | Sd/- | Sd/- | Sd/- |
| 27.10.2023 | 00 | ISSUED FOR CONSTRUCTION | Sd/- | Sd/- | Sd/- |
| DATE | NO. | REVISION OR ISSUES | BY | CH. | APP. |

DESIGN MEMO NO. डिजाइन मेमो संख्या

एन एच पी सी लिमिटेड
(भारत सरकार का एक नवरत्न उपक्रम)
NHPC Limited
(A GOVT. OF INDIA NAVRATNA ENTERPRISE)

दिबांग बहुउद्देशीय परियोजना
DIBANG MULTIPURPOSE PROJECT

PROJECT GENERAL LAYOUT PLAN

| DRAWN अंकित | SUBMITTED प्रस्तुत | RECOMMENDED अनुशंसित | DEM / HM | APPROVED अनुमोदन |
|---|---|---|---|---|
| Sd/- PRABHAT ASIWAL | Sd/- PRABHAT ASIWAL | Sd/- RAJEEV KUMAR | | Sd/- S.CHOWDHURY |

| DATE दिनांक | DRG. NO. ड्रेग संख्या | | | | | |
|---|---|---|---|---|---|---|
| OCT 2023 | NHDB | 1AC4 | 41 | DD | 0001 | 03 |

DRG. NO. NHDB-1AC4-41-DD-0001-03