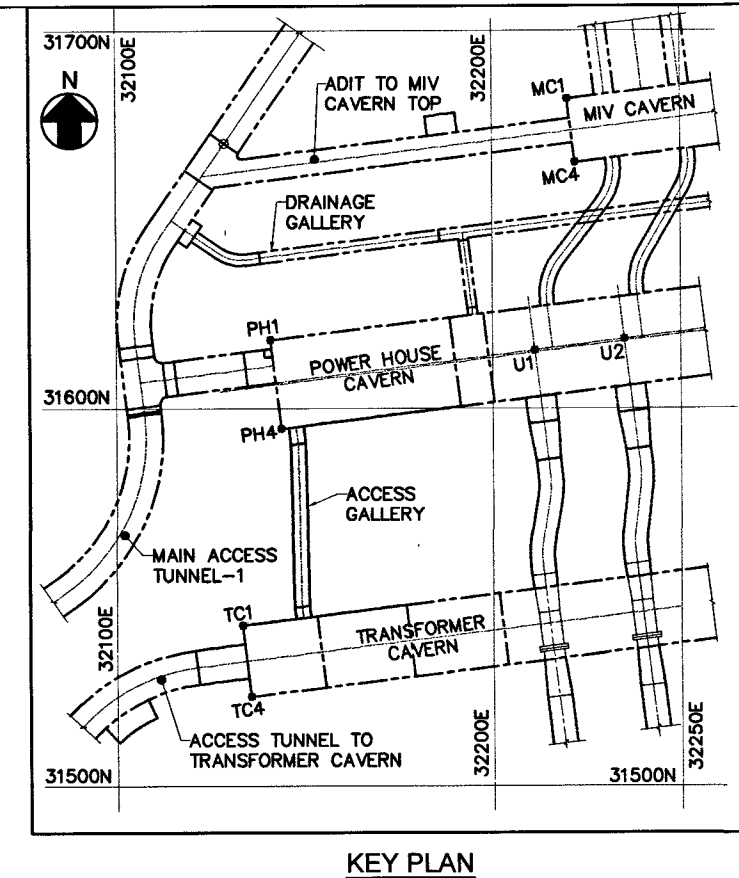
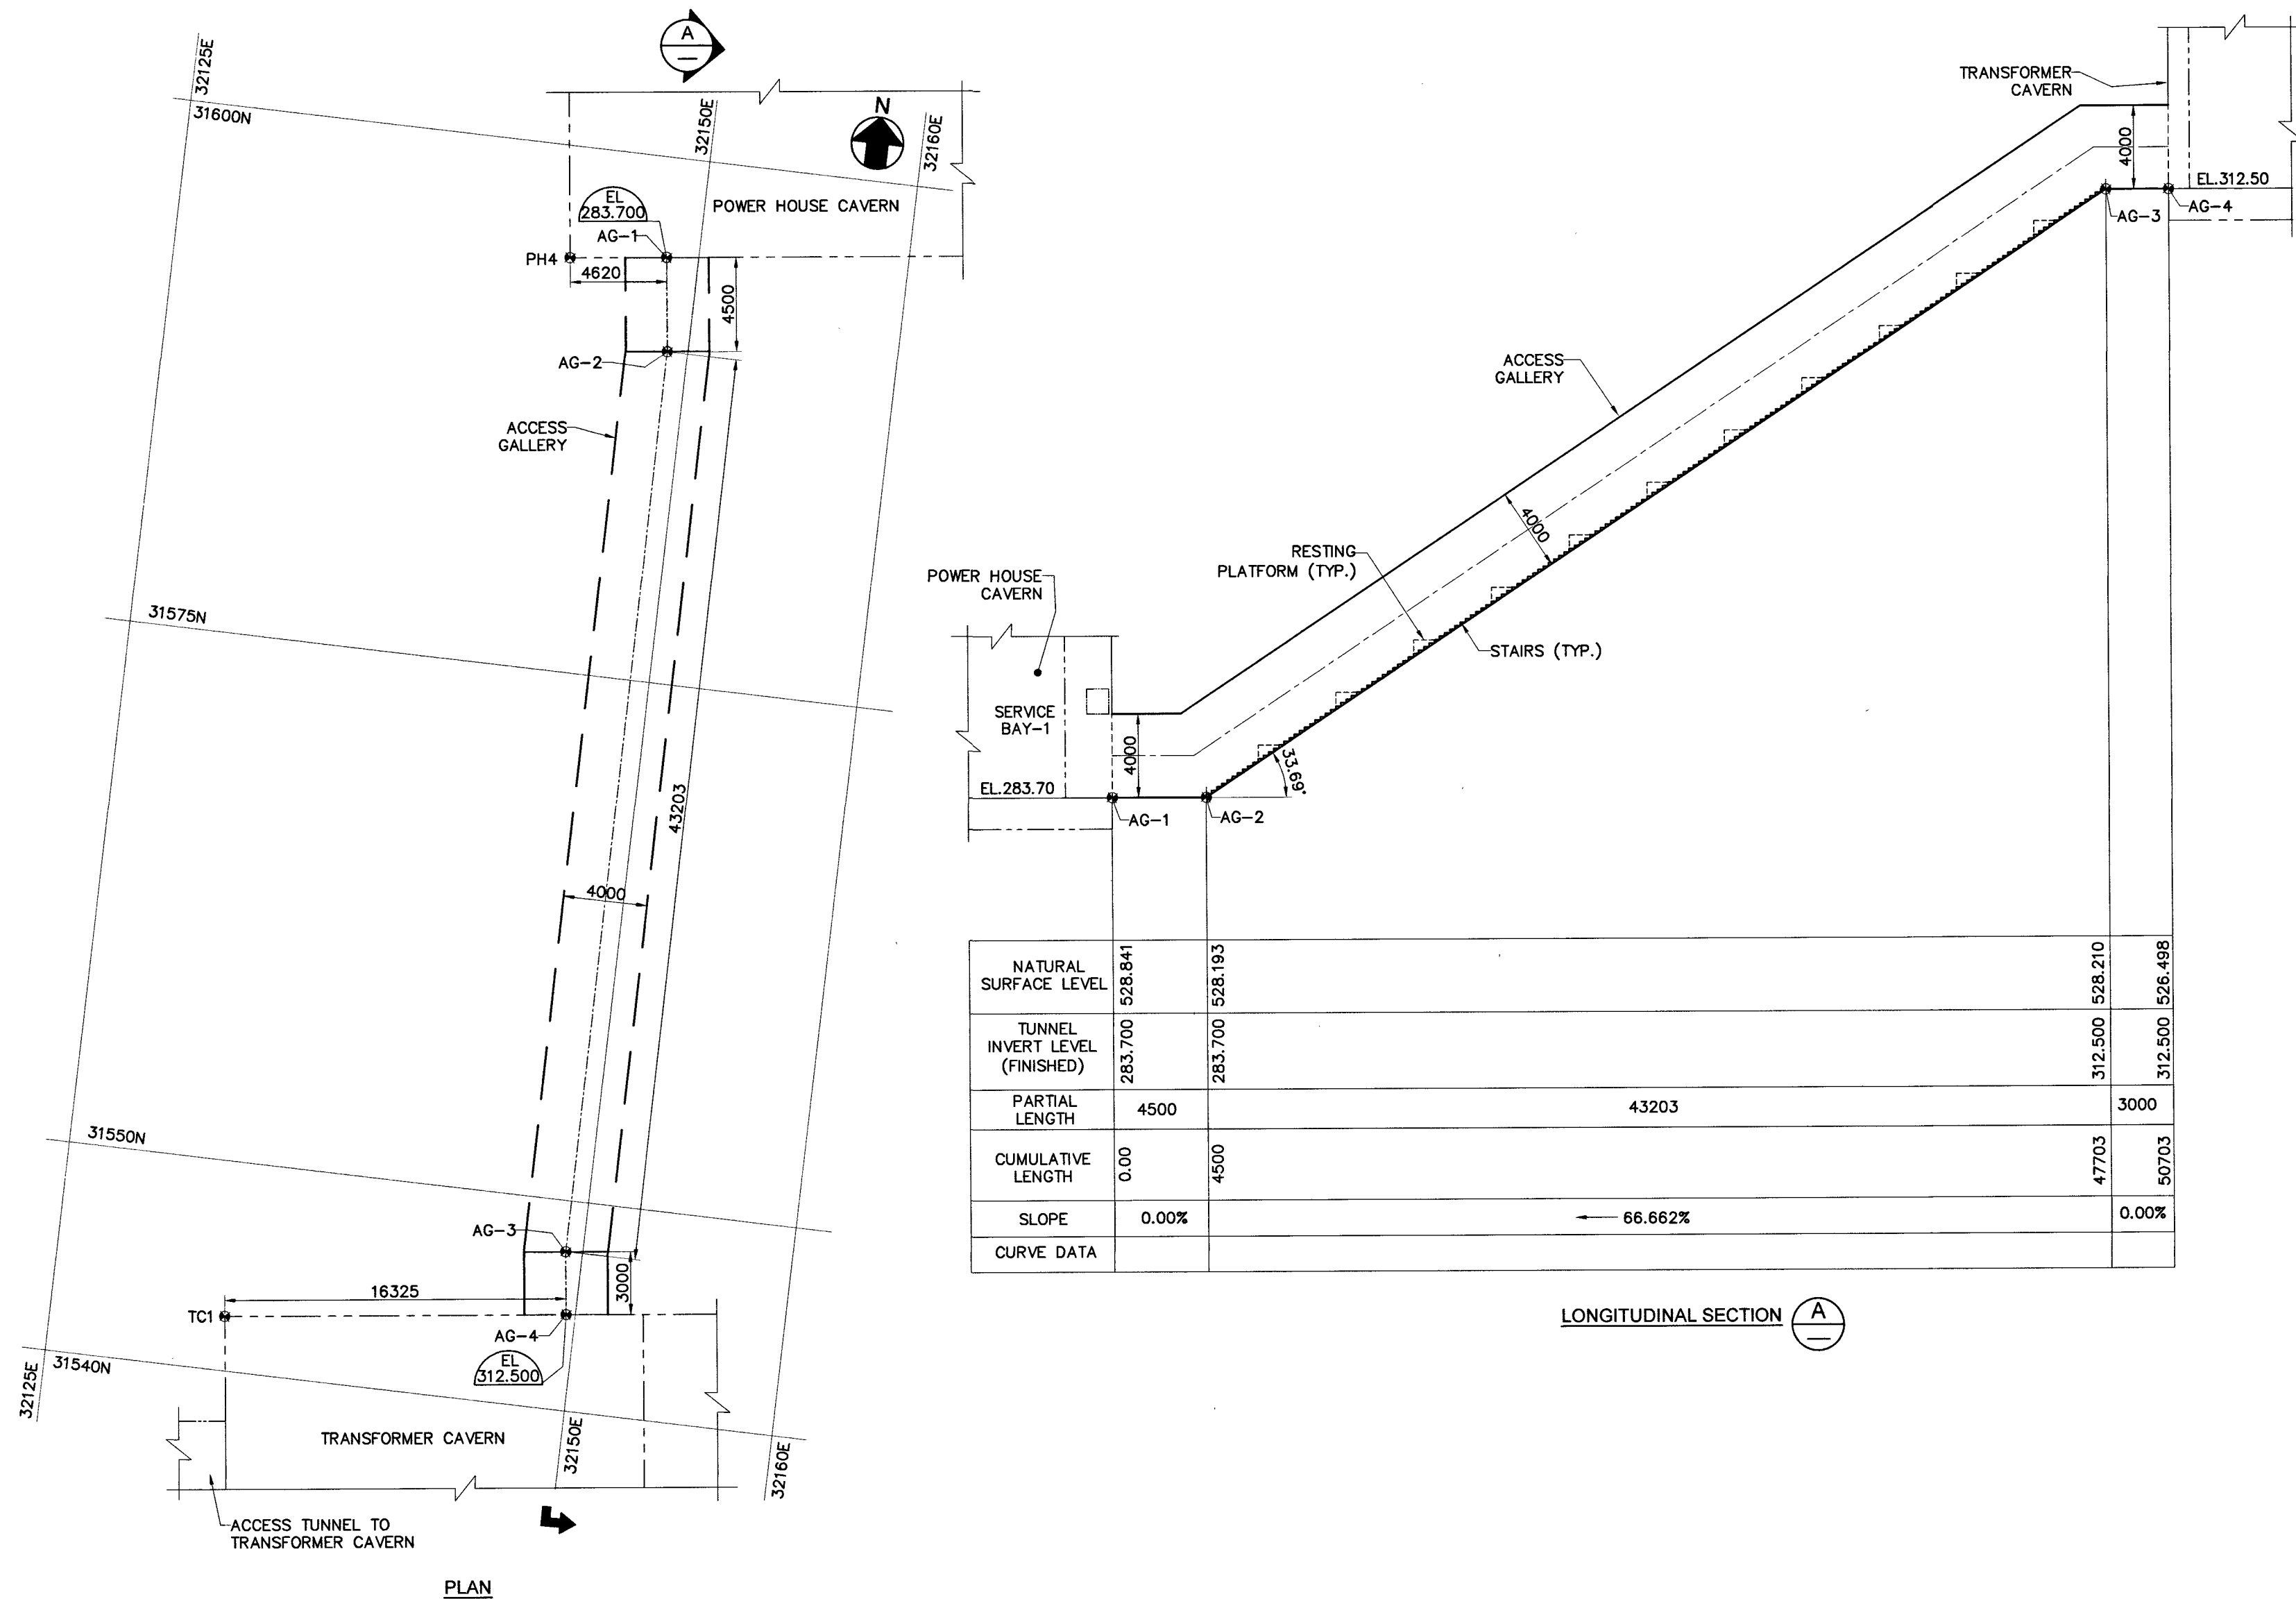


**NOTES:-**


- सभी माप मिलीमीटर में, ग्रिड तथा ऊचाई मीटर में दिए गए हैं।
ALL DIMENSIONS ARE IN MILLIMETRE, GRIDS AND ELEVATIONS ARE IN METRE
- GRIDS AND THE VALUES OF NSL HAVE BEEN REPRODUCED FROM S.O.I. SHEET. THE ACCURACY OF THE SAME SHALL BE ESTABLISHED WITH EXISTING S.O.I. BENCH MARK AT SITE BEFORE ADOPTING CO-ORDINATES.
- THE LEVELS SHOWN CORRESPONDS TO THE FINISHED SURFACES/LINES. FOR LEVELS OF EXCAVATION REFER EXCAVATION DRAWING.
- FOR EXCAVATION AND ROCK SUPPORT DETAILS REFER DRAWING NO. NHDB-4CC4-41-DD-1031.
- THIS DRAWING SHALL BE READ IN CONJUNCTION WITH DRG. NO. NHDB-1AC4-41-DD-0001 & NHDB-4AC4-41-DD-0001.

REFERENCE:

- NHDB-1AC4-41-DD-0001.
- NHDB-4AC4-41-DD-0001

CO-ORDINATES:-
(ACCESS GALLERY)

POINTS	NORTHING IN METRE	EASTING IN METRE
PH4	31594.672	32143.900
TC1	31542.599	32133.358
AG-1	31595.235	32148.486
AG-2	31590.769	32149.034
AG-3	31547.566	32149.195
AG-4	31544.589	32149.561

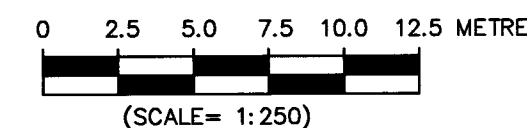

एन एच पी सी लिमिटेड (भारत सरकार का नवरोज उद्यम) NHPC Limited (A GOVT. OF INDIA NAVRATNA ENTERPRISE)	
दिवांग बहुउद्देशीय परियोजना DIBANG MULTIPURPOSE PROJECT	
POWER HOUSE ACCESS GALLERY SETTING OUT PLAN AND LONGITUDINAL SECTION	
30.04.2026 00	ISSUED FOR CONSTRUCTION
DATE NO.	REVISION OR ISSUES
BY CH. APP.	BY CH. APP.
DATE	DRG. NO.
APR. 2026	NHDB 4CC4 41 DD 0007 00