
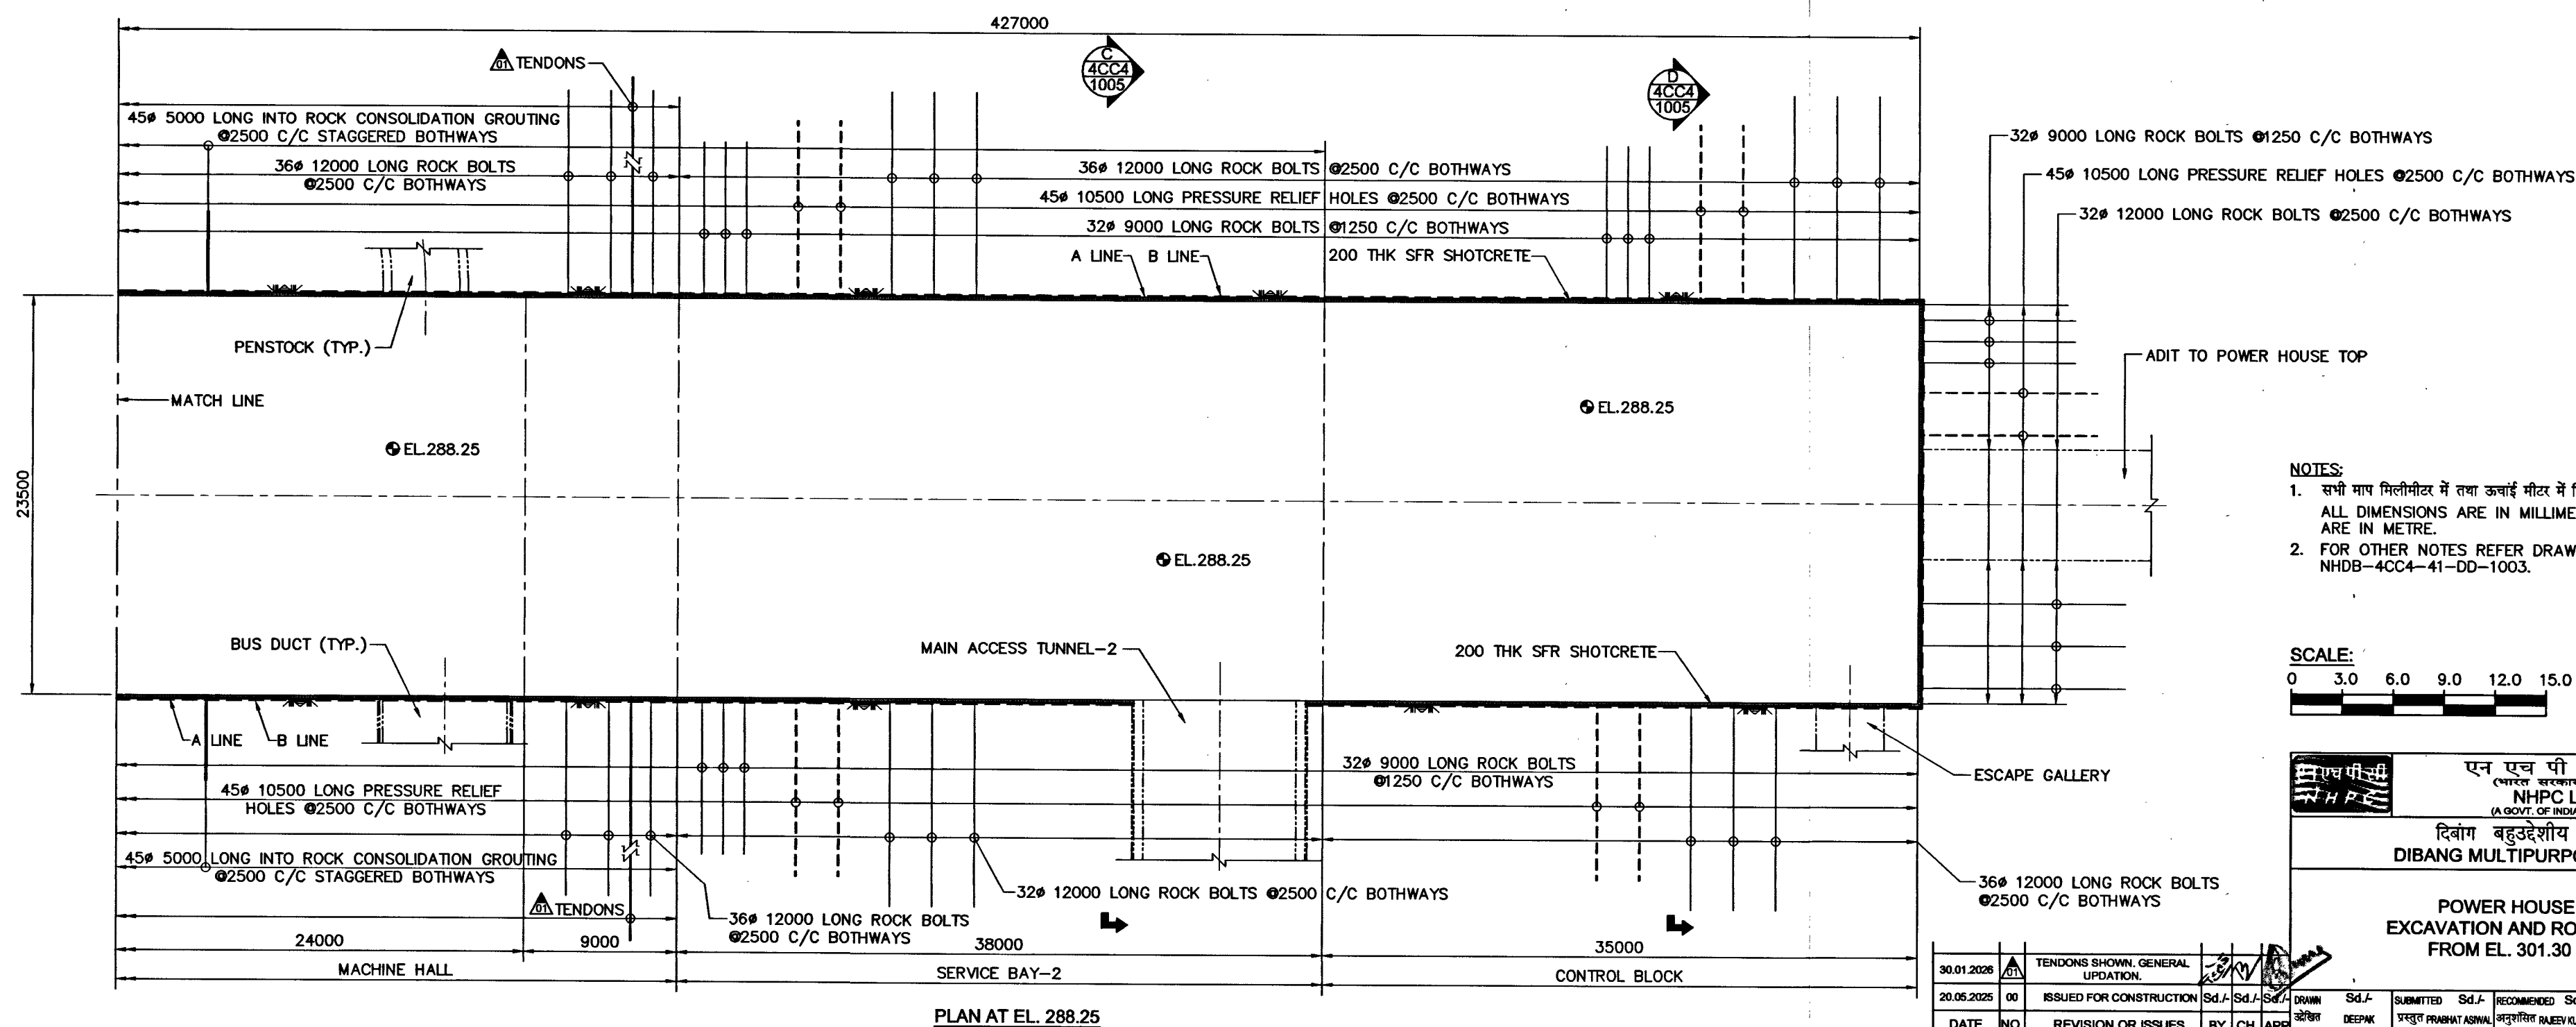


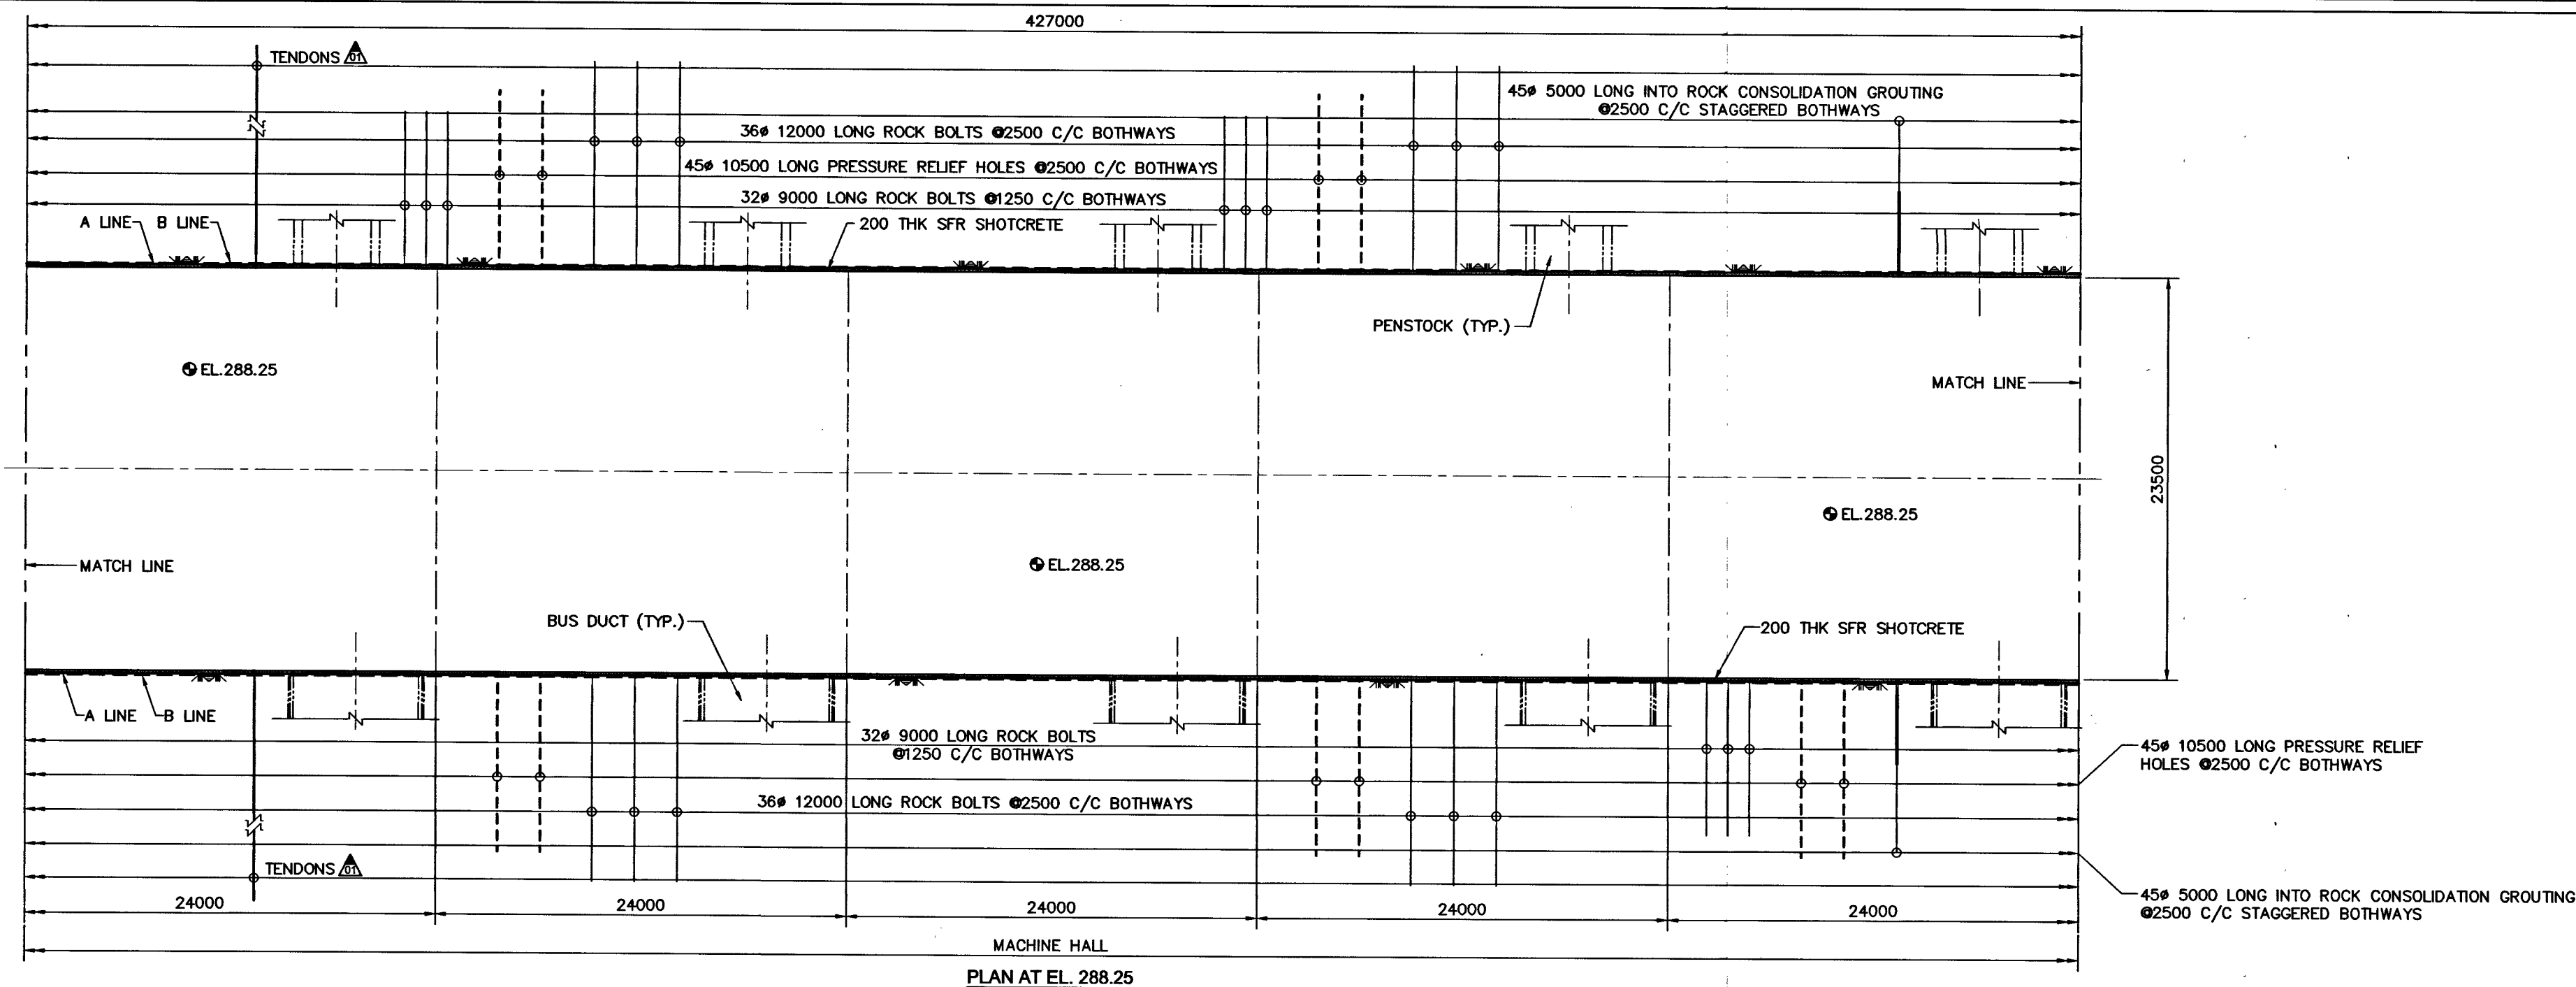

NOTES:

1. सभी माप मिलीमीटर में तथा ऊचाई मीटर में दिए गए है।
ALL DIMENSIONS ARE IN MILLIMETRE AND ELEVATIONS ARE IN METRE.
2. FOR OTHER NOTES REFER DRAWING NO.
NHDB-4CC4-41-DD-1003.

SCALE:
0 3.0 6.0 9.0 12.0 15.0 METRE

POWER HOUSE CAVERN
EXCAVATION AND ROCK SUPPORTS
FROM EL. 301.30 TO 288.25

30.01.2026				TENDONS SHOWN, GENERAL UPDATION.				FROM EL. 301.30 TO 288.25										SHEET 2 OF 2			
20.05.2025		00		ISSUED FOR CONSTRUCTION		Sd./	Sd./	Sd./	DRWN अंकित	Sd./ DEEPAK	SUBMITTED प्रस्तुत PRABHAT ASHAI	Sd./ अनुमोदित RAJEEV KUMAR	RECOMMENDED अनुमोदित RAJEEV KUMAR	DEM / HM		APPROVED अनुमोदित S. CHANDHUR					
DATE		NO		REVISION OR ISSUES		BY	CH.	APP	DATE दिनांक		MAY 2025		DRG. NO. रेखांक	NHDB 4CC4 41 DD 1004 01							
DESIGN MEMO NO. डिजाइन मेमो संख्या																					