



DRG. NO. NHDB-4CC4-41-DD-1015-00

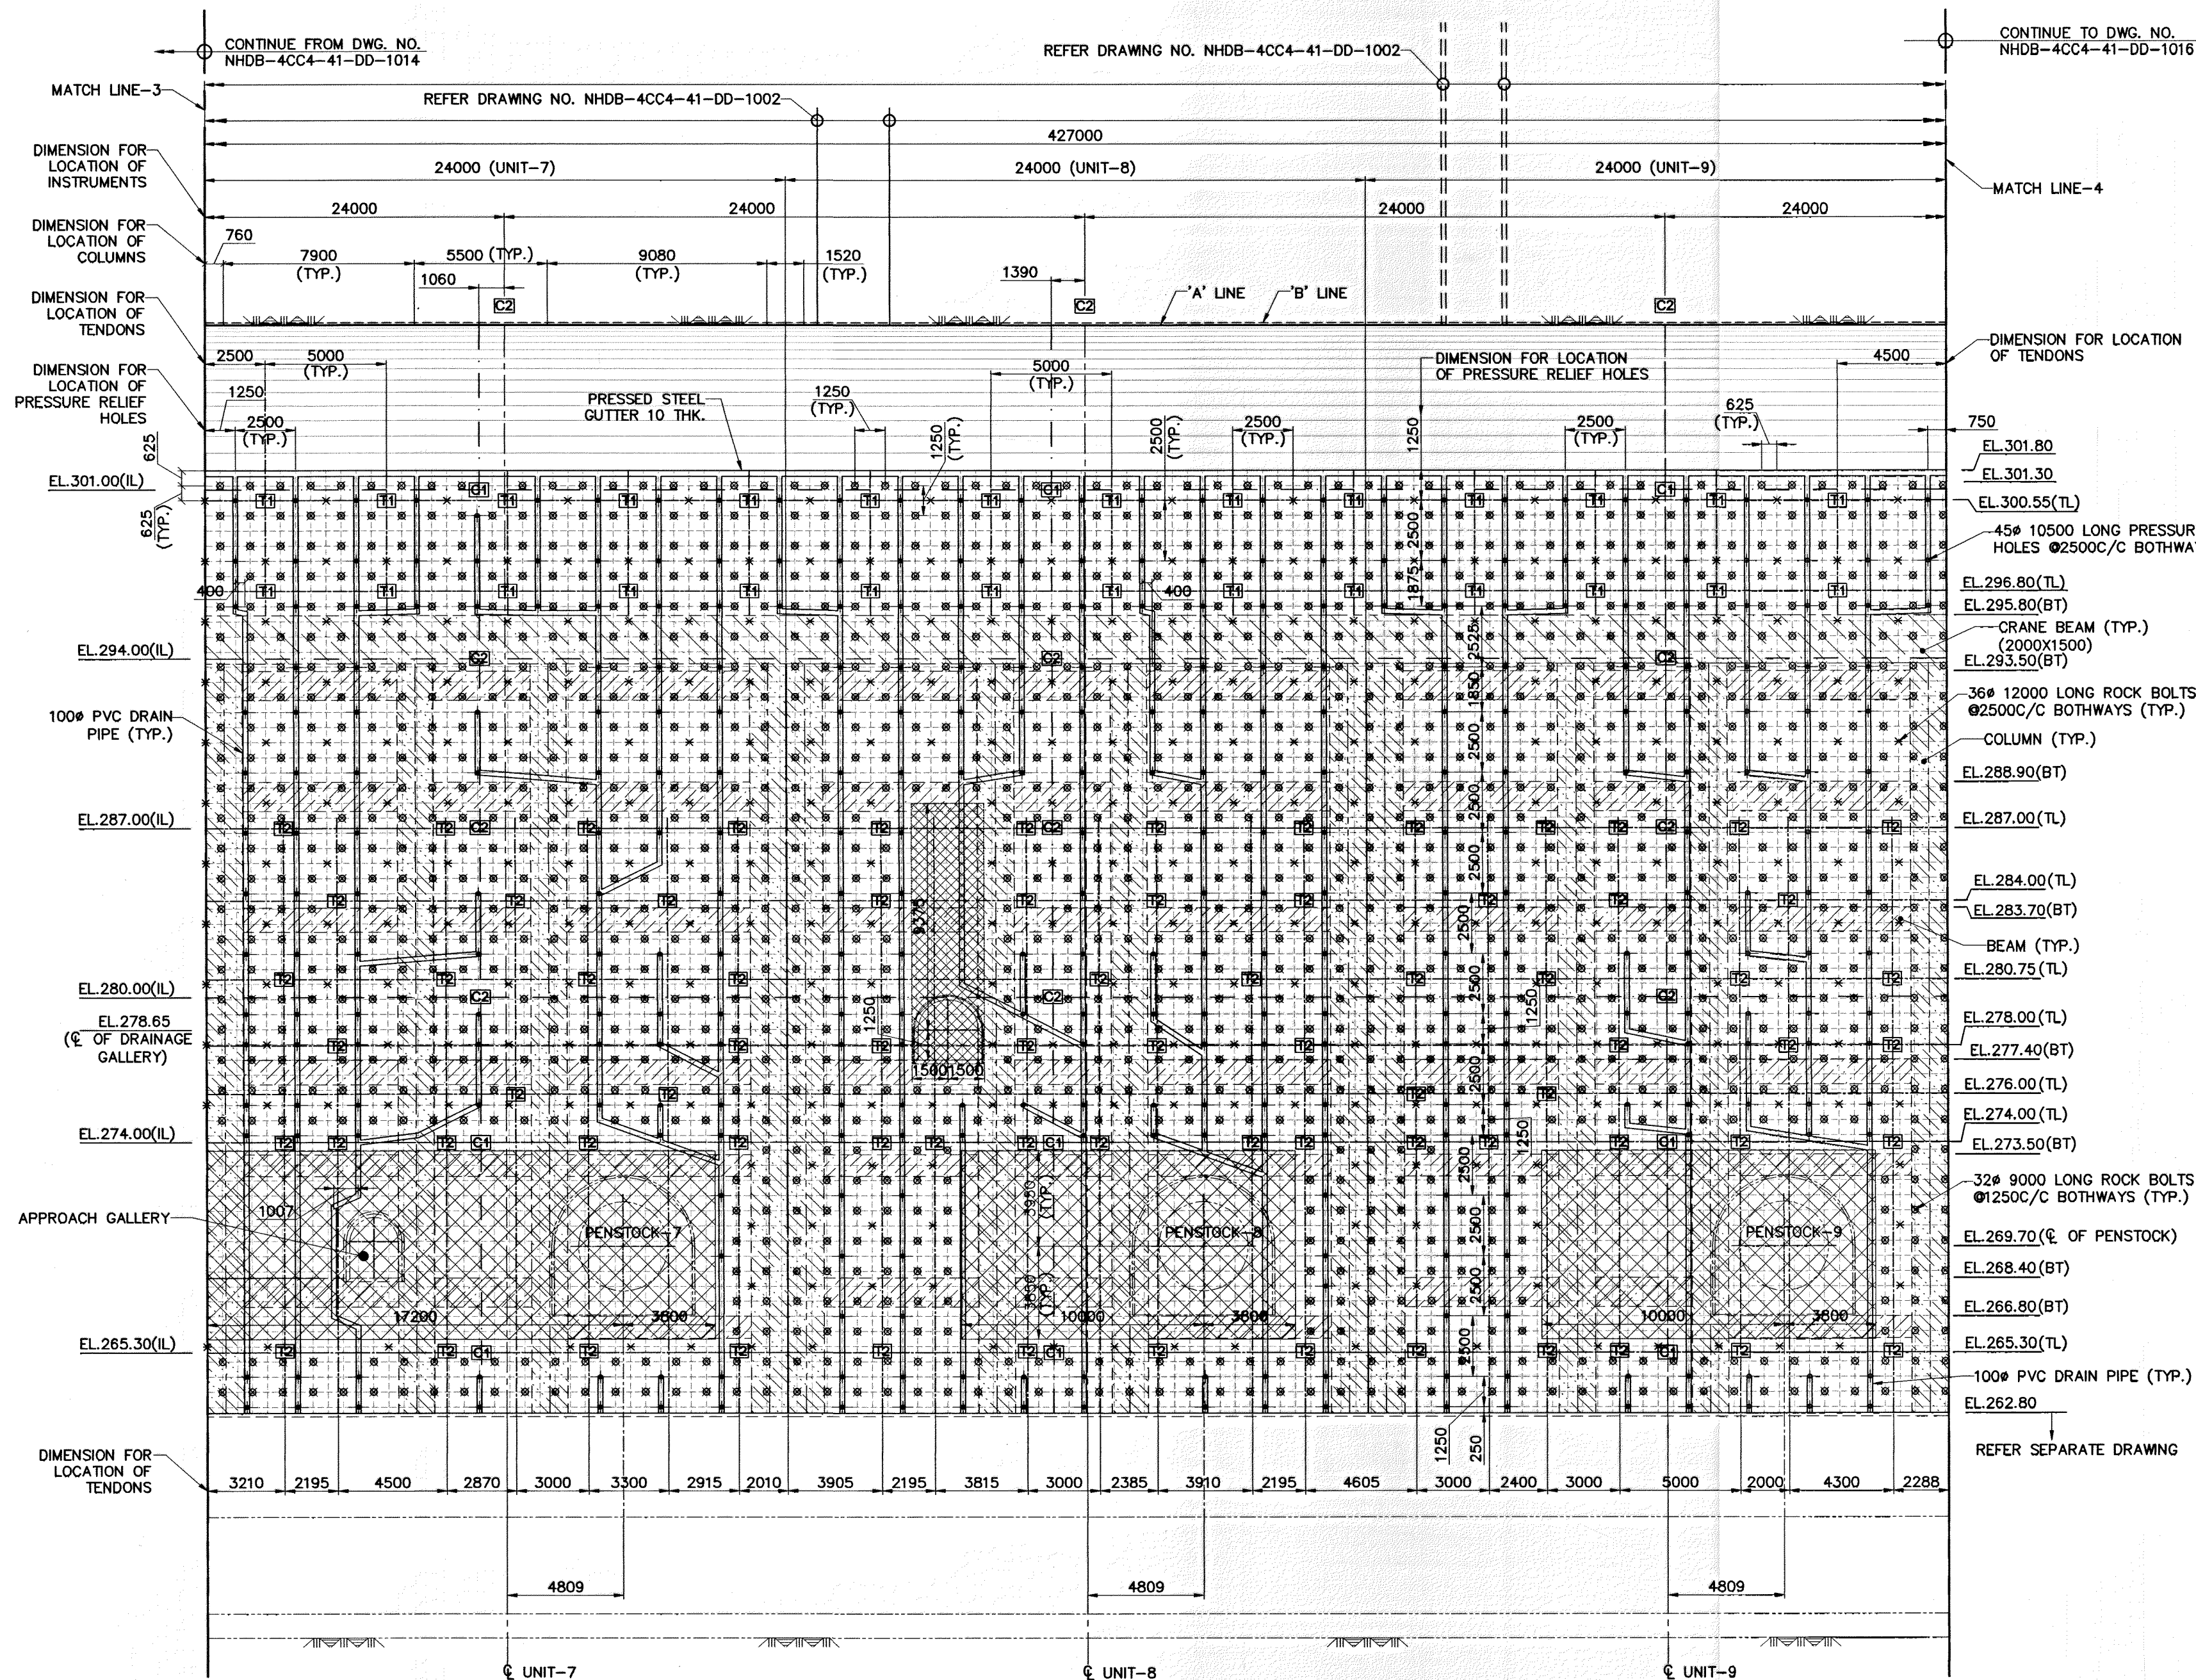

- NOTES:**
- सभी माप मिलीमीटर में तथा ऊंचाई मीटर में दिए गए हैं।
ALL DIMENSIONS ARE IN MILLIMETRE AND ELEVATIONS ARE IN METRE.
 - FOR OTHER NOTES REFER DRAWING NO. NHDB-4CC4-41-DD-1012.
 - THIS DRAWING SHALL BE READ IN CONJUNCTION WITH RELEVANT JUNCTION EXCAVATION DRAWING OF MAT-2/BUS DUCTS/GALLERIES/PENSTOCKS/DRAFT TUBE MANIFOLDS WITH POWER HOUSE WALL.

- LEGENDS:-**
- × 36# 12000 LONG ROCK BOLTS
 - ⊗ 32# 9000 LONG ROCK BOLTS
 - T1 (TYPE-1)-1200KN GUARANTEED ULTIMATE TENSILE STRENGTH (GUTS), LOCK OFF LOAD SHALL BE 60% OF GUTS, TOTAL LENGTH=30M.
 - T2 (TYPE-2)-1200KN GUARANTEED ULTIMATE TENSILE STRENGTH (GUTS), LOCK OFF LOAD SHALL BE 60% OF GUTS, TOTAL LENGTH=36.75M.
 - 45# 10500 LONG PRESSURE RELIEF HOLE
 - × CONVERGENCE MEASUREMENT (OPTICAL TARGETS)
 - ⊕ LOAD CELL (30T CAPACITY)
 - # MULTIPLE POINT BORE HOLE EXTENSOMETER (5M, 10M, 15M) (3 POINTS)
 - ## MULTIPLE POINT BORE HOLE EXTENSOMETER (4M, 7M, 10M, 13M, 16M, 19M) (6 POINT)
 - C1 × # ⊕ (COMBINATION OF INSTRUMENTS-1)
 - C2 × # ⊕ (COMBINATION OF INSTRUMENTS-2)
 - BT BEAM TOP LEVEL
 - TL TENDONS LEVEL
 - IL INSTRUMENTATION LEVEL
 - ⊠ ROCK SUPPORTS AND PRESSURE RELIEF HOLES IN MARKED ZONE SHALL BE INSTALLED AS PER RELEVANT JUNCTION DRAWINGS OF INTERFACING STRUCTURE.

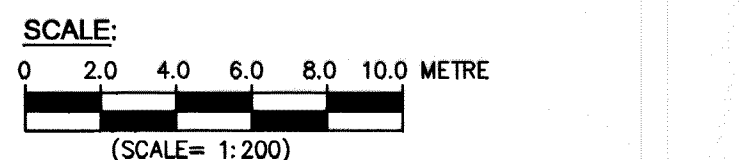

एन एच पी सी लिमिटेड NHPC Limited (A GOVT. OF INDIA ENTERPRISE)	
दिवंग बहुउद्देशीय परियोजना DIBANG MULTIPURPOSE PROJECT	
POWER HOUSE ROCK SUPPORTS, CABLE TENDONS, PRESSURE RELIEF HOLES AND INSTRUMENTATION (EL.301.30 M TO EL.262.80 M / EL.264.90 M) TYPICAL ARRANGEMENT WALL ELEVATION (SHEET 4 OF 14)	
28.01.2026	00
DATE	NO.
ISSUED FOR CONSTRUCTION	
BY	CH. APP.
REVISION OR ISSUES	
DESIGN MEMO NO. 1	
DATE	NO.
JAN 2026	00
DRG. NO.	
NHDB	4CC4 41 DD 1015 00