


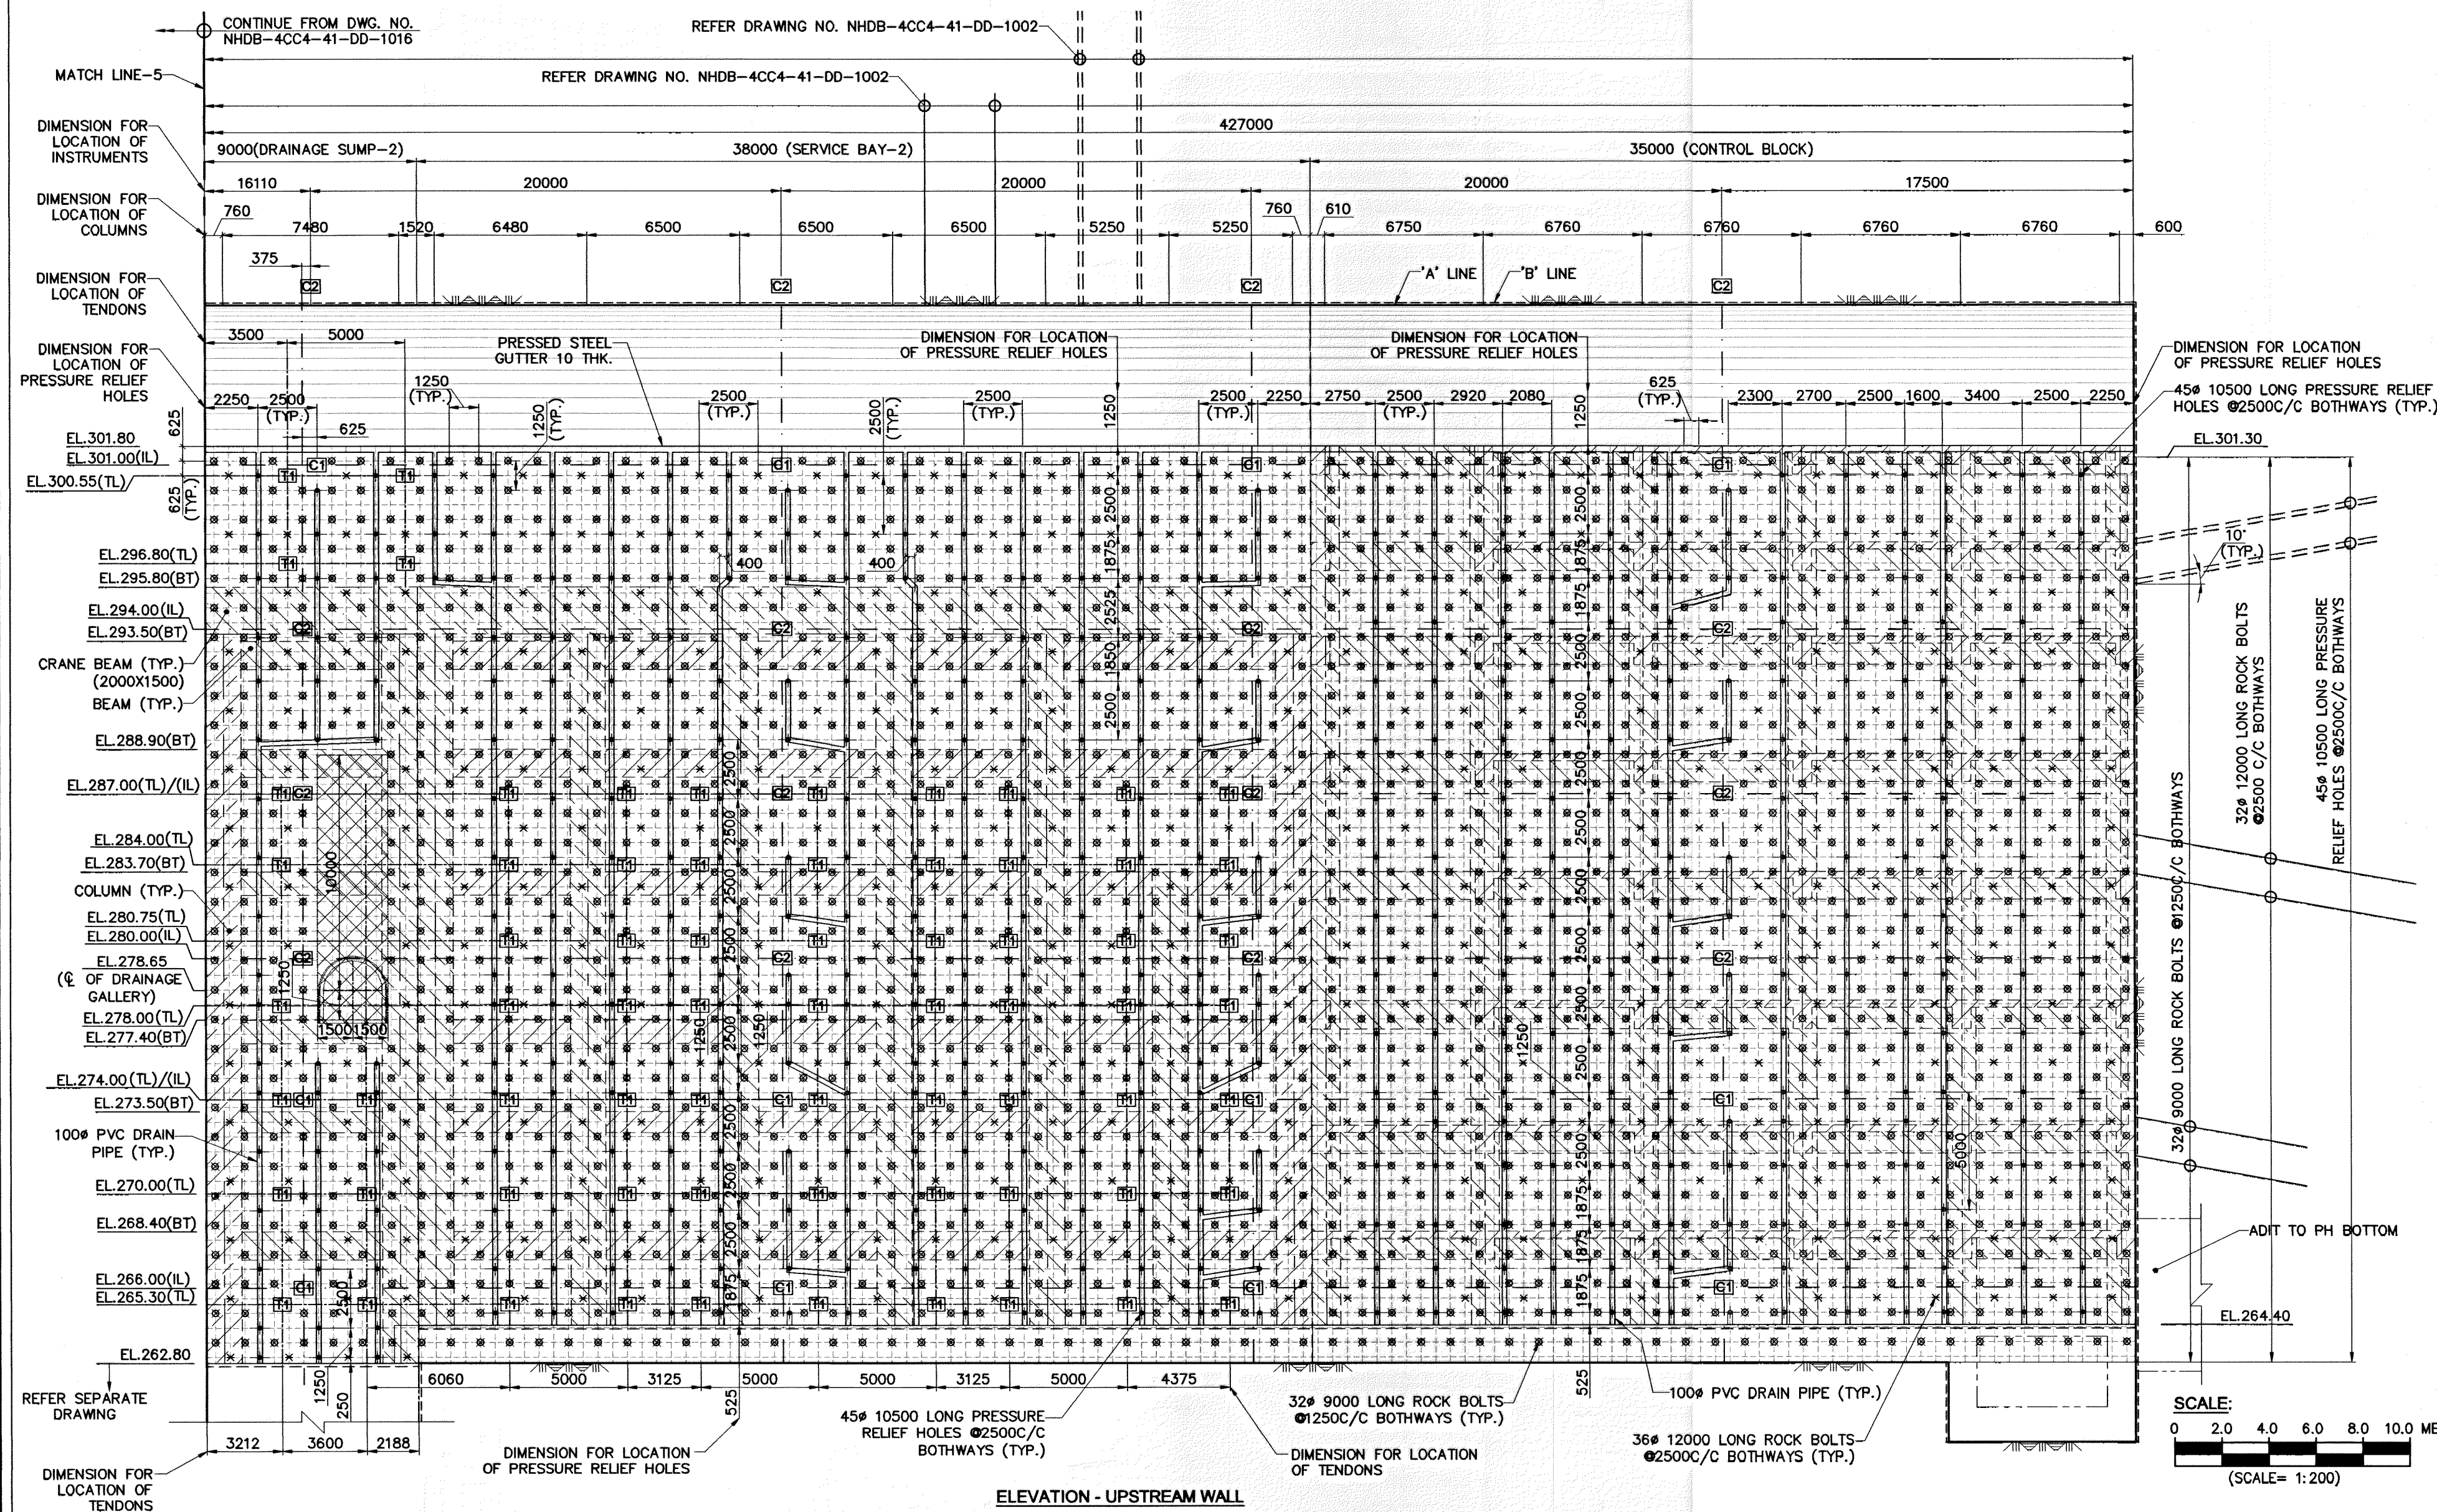

LEGENDS:-

- ✖ 36Ø 12000 LONG ROCK BOLTS
- ✖ 32Ø 9000 LONG ROCK BOLTS
- Ⓜ (TYPE-1)-1200KN GUARANTEED ULTIMATE TENSILE STRENGTH (GUTS), LOCK OFF LOAD SHALL BE 60% OF GUTS, TOTAL LENGTH=30M.
- ⊕ 45Ø 10500 LONG PRESSURE RELIEF HOLE
- ✖ CONVERGENCE MEASUREMENT (OPTICAL TARGETS)
- Ⓢ LOAD CELL (30T CAPACITY)
- Ⓜ MULTIPLE POINT BORE HOLE EXTENSOMETER (5M, 10M, 15M) (3 POINTS)

- ☐ MULTIPLE POINT BORE HOLE EXTENSOMETER (4M, 7M, 10M, 13M, 16M, 19M) (6 POINT)
☒ ☐ ☐ (COMBINATION OF INSTRUMENTS-1)
☒ ☐ ☐ (COMBINATION OF INSTRUMENTS-2)
 BT BEAM TOP LEVEL
 TL TENDONS LEVEL
 IL INSTRUMENTATION LEVEL
☒ ROCK SUPPORTS AND PRESSURE RELIEF HOLES IN MARKED ZONE SHALL BE INSTALLED
 AS PER RELEVANT JUNCTION DRAWINGS OF INTERFACING STRUCTURE.

NOTES:

1. सभी माप मिलीमीटर में तथा ऊंचाई मीटर में दिए गए हैं ।
ALL DIMENSIONS ARE IN MILLIMETRE AND ELEVATIONS ARE IN METRE.
2. FOR OTHER NOTES REFER DRAWING NO. NHDB-4CC4-41-DD-1012.
3. THIS DRAWING SHALL BE READ IN CONJUNCTION WITH RELEVANT JUNCTION EXCAVATION DRAWING OF MAT-2/BUS DUCTS/GALLERIES/PENSTOCKS/DRAFT TUBE MANIFOLDS WITH POWER HOUSE WALL.

										(EL.301.30 M TO EL.262.80 M / EL.264.90 M)											
										TYPICAL ARRANGEMENT											
										WALL ELEVATION (SHEET 6 OF 14)											
28.01.2026		00		ISSUED FOR CONSTRUCTION				BY. CH. APP		DRAWN अक्षर		SEAL अक्षर		SUBMITTED अक्षर PRABHAT ASWAL		RECOMMENDED अक्षर अशोक कुमार		DESHMUKH		APPROVED अशोक कुमार	
DATE		NO.		REVISION OR ISSUES				BY. CH. APP		DRAWN		SEAL		SUBMITTED		RECOMMENDED		DESHMUKH		APPROVED	
DESIGN MEMO NO.-										DATE		JAN 2026		DRG. NO.		NHDB		4CC4		41 DD 1017 00	
डिजाइन मेमो संख्या										अक्षर		अक्षर		अक्षर		अक्षर		अक्षर		अक्षर	