


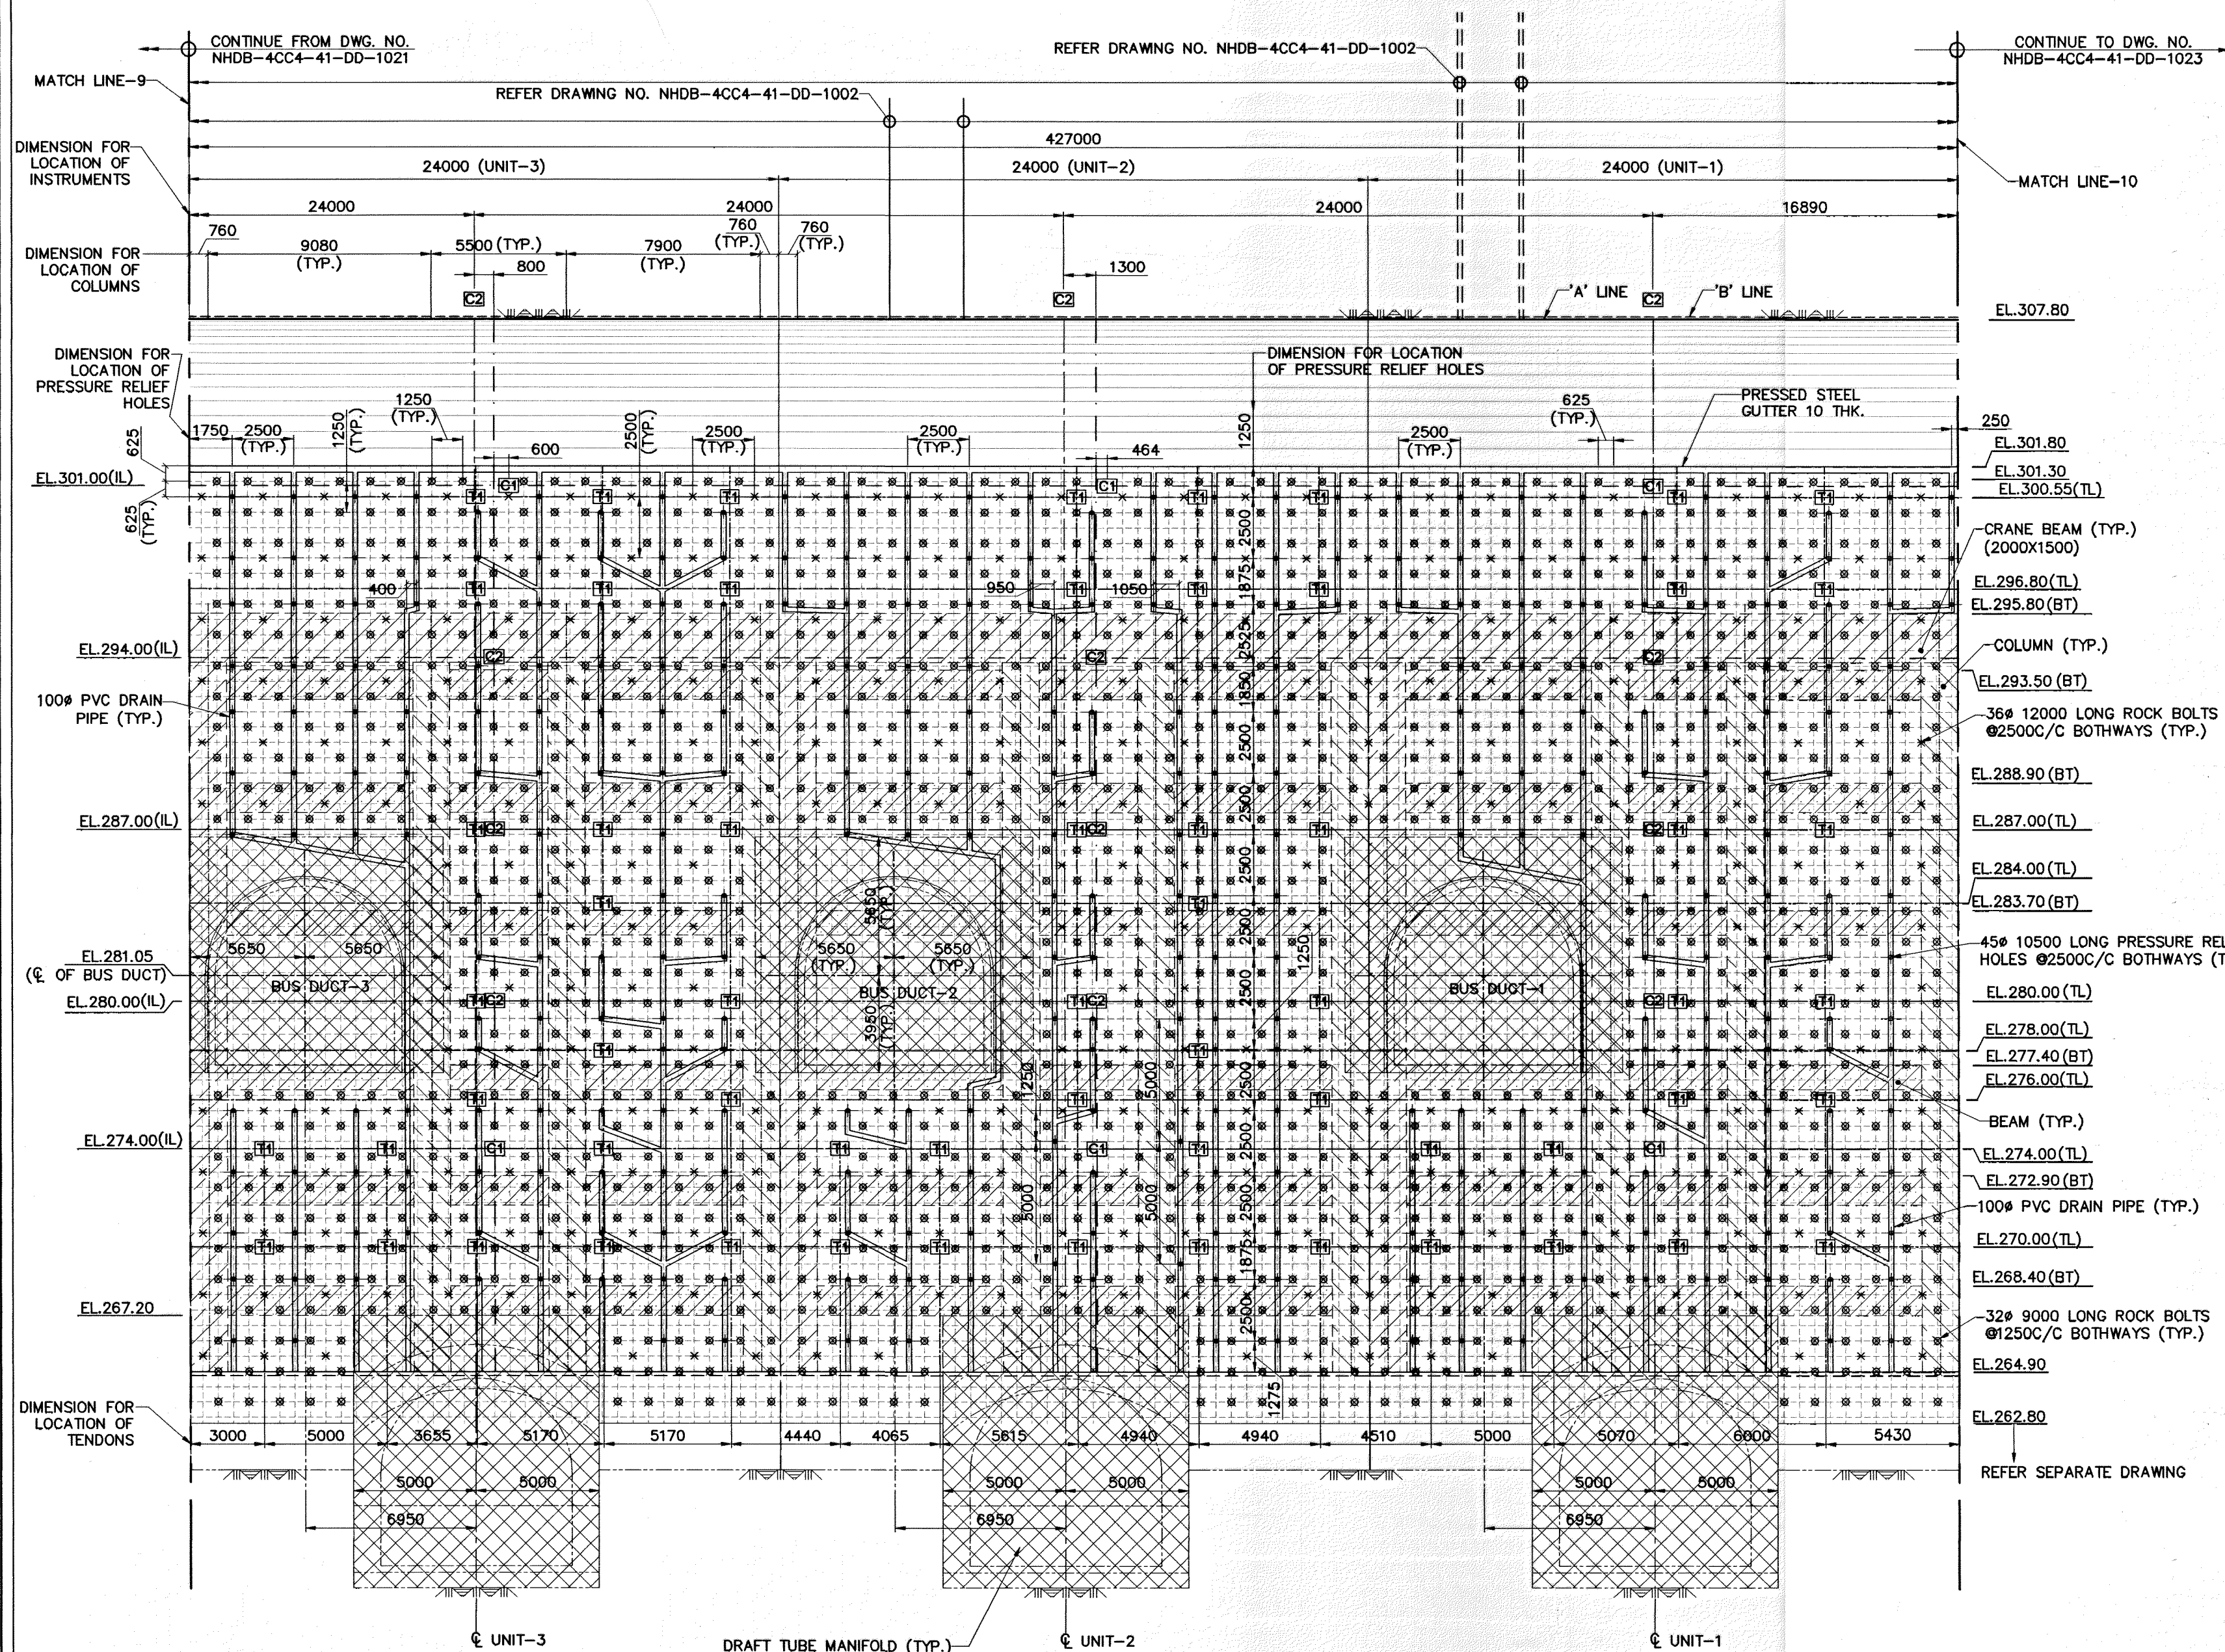


NOTES:

1. सभी माप मिलीमीटर में तथा ऊंचाई मीटर में दिए गए हैं ।
ALL DIMENSIONS ARE IN MILLIMETRE AND ELEVATIONS ARE IN METRE.
2. FOR OTHER NOTES REFER DRAWING NO.
NHD-B-44C-41-DD-1012.
3. THIS DRAWING SHALL BE READ IN CONJUNCTION WITH RELEVANT JUNCTION EXCAVATION DRAWING OF MAT-2/BUS DUCTS/GALLERIES/PENSTOCKS/DRAFT TUBE MANIFOLDS WITH POWER HOUSE WALL.

LEGENDS:-

- ✱ 36# 12000 LONG ROCK BOLTS
- ✱ 32# 9000 LONG ROCK BOLTS
- ④ (TYPE-1)-1200KN GUARANTEED ULTIMATE TENSILE STRENGTH (GUTS), LOCK OFF LOAD SHALL BE 60% OF GUTS, TOTAL LENGTH=30M.
- ④ 45# 10500 LONG PRESSURE RELIEF HOLE
- ✱ CONVERGENCE MEASUREMENT (OPTICAL TARGETS)
- ④ LOAD CELL (30T CAPACITY)
- ✱ MULTIPLE POINT BORE HOLE EXTENSOMETER (5M, 10M, 15M) (3 POINTS)
- ✱ MULTIPLE POINT BORE HOLE EXTENSOMETER (4M, 7M, 10M, 13M, 16M, 19M) (6 POINT)
- ④ ④ ✱ (COMBINATION OF INSTRUMENTS-1)
- ④ ④ ✱ (COMBINATION OF INSTRUMENTS-2)
- BT BEAM TOP LEVEL
- TL TENDONS LEVEL
- IL INSTRUMENTATION LEVEL
- ✱ ROCK SUPPORTS AND PRESSURE RELIEF HOLES IN MARKED ZONE SHALL BE INSTALLED AS PER RELEVANT JUNCTION DRAWINGS OF INTERFACING STRUCTURE.

SCALE:

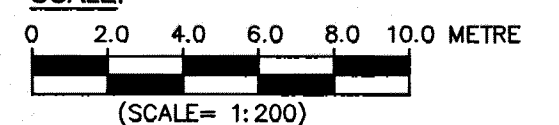

 A Navratna Company	एन एच पी सी लिमिटेड (एक सरकारी एवं नगरपाल जका) NHPC Limited (A GOVT. OF INDIA NAVRATNA ENTERPRISE)
लिबांग बहुउद्देशीय परियोजना DIBANG MULTIPURPOSE PROJECT	
POWER HOUSE ROCK SUPPORTS, CABLE TENDONS, PRESSURE RELIEF HOLES AND INSTRUMENTATION (EL.301.30 M TO EL.262.80 M / EL.264.90 M) TYPICAL ARRANGEMENT WALL ELEVATION	
(SHEET 11 OF 14)	

DRAWN ड्राइंग विनय कुमार	SUBMITTED प्रस्तुत प्रभात अश्वल	RECOMMENDED अनुमोदित प्रदीप कुमार	DEMON प्रदर्शन प्रदीप कुमार	APPROVED अनुमोदित प्रदीप कुमार
DATE दिनांक JAN 2026	DRG. NO. ड्राइंग संख्या NHDB	4CC4	41	DD
				1022
				00

										(EL.301.30 M TO EL.262.80 M / EL.264.90 M)									
										TYPICAL ARRANGEMENT									
										WALL ELEVATION									
										(SHEET 11 OF 14)									
28.01.2026	00	ISSUED FOR CONSTRUCTION				BY:	CH. APP.	DRAWN अशोक VINAY KUMAR		SUBMITTED प्रमोद PRAMAT ASHVAL		RECOMMENDED अशोक RAMESH KUMAR		DESHM		APPROVED अनुमोदित		COUNTERY	
DATE	NO.	REVISION OR ISSUES				BY:	CH. APP.	DATE दिनांक	JAN 2026	DRG. NO. ड्राइंग संख्या	NHDB	4CC4	41	DD	1022	00			
DESIGN MEMO NO.- डिजाइन मेमो संख्या																			