




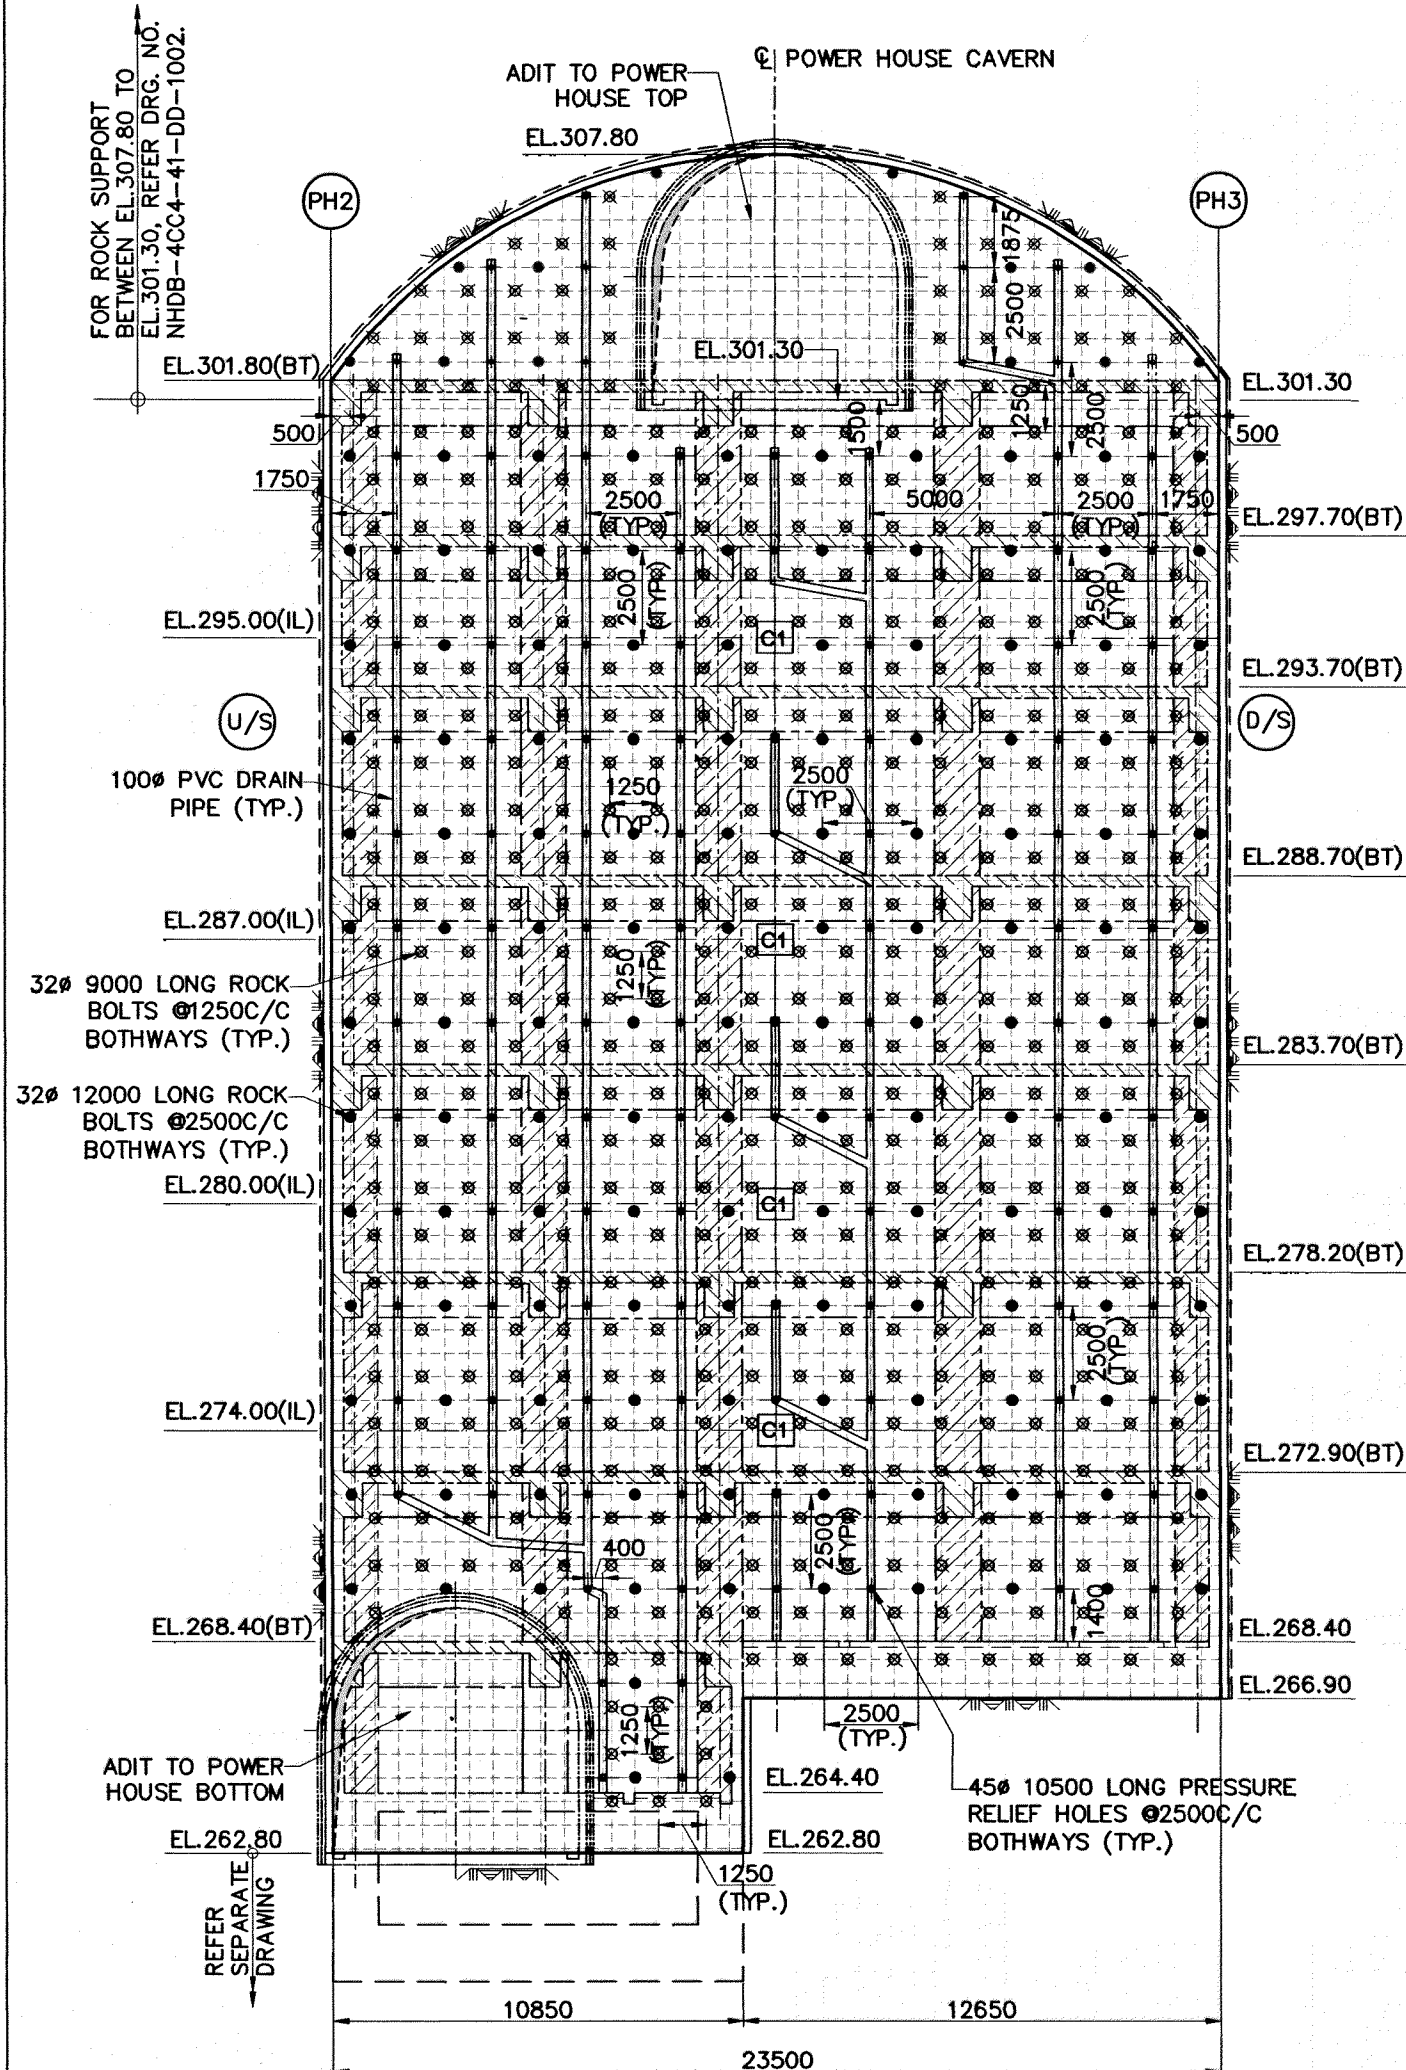

TYPICAL CROSS SECTION-END WALL 
(CONTROL BLOCK SIDE)

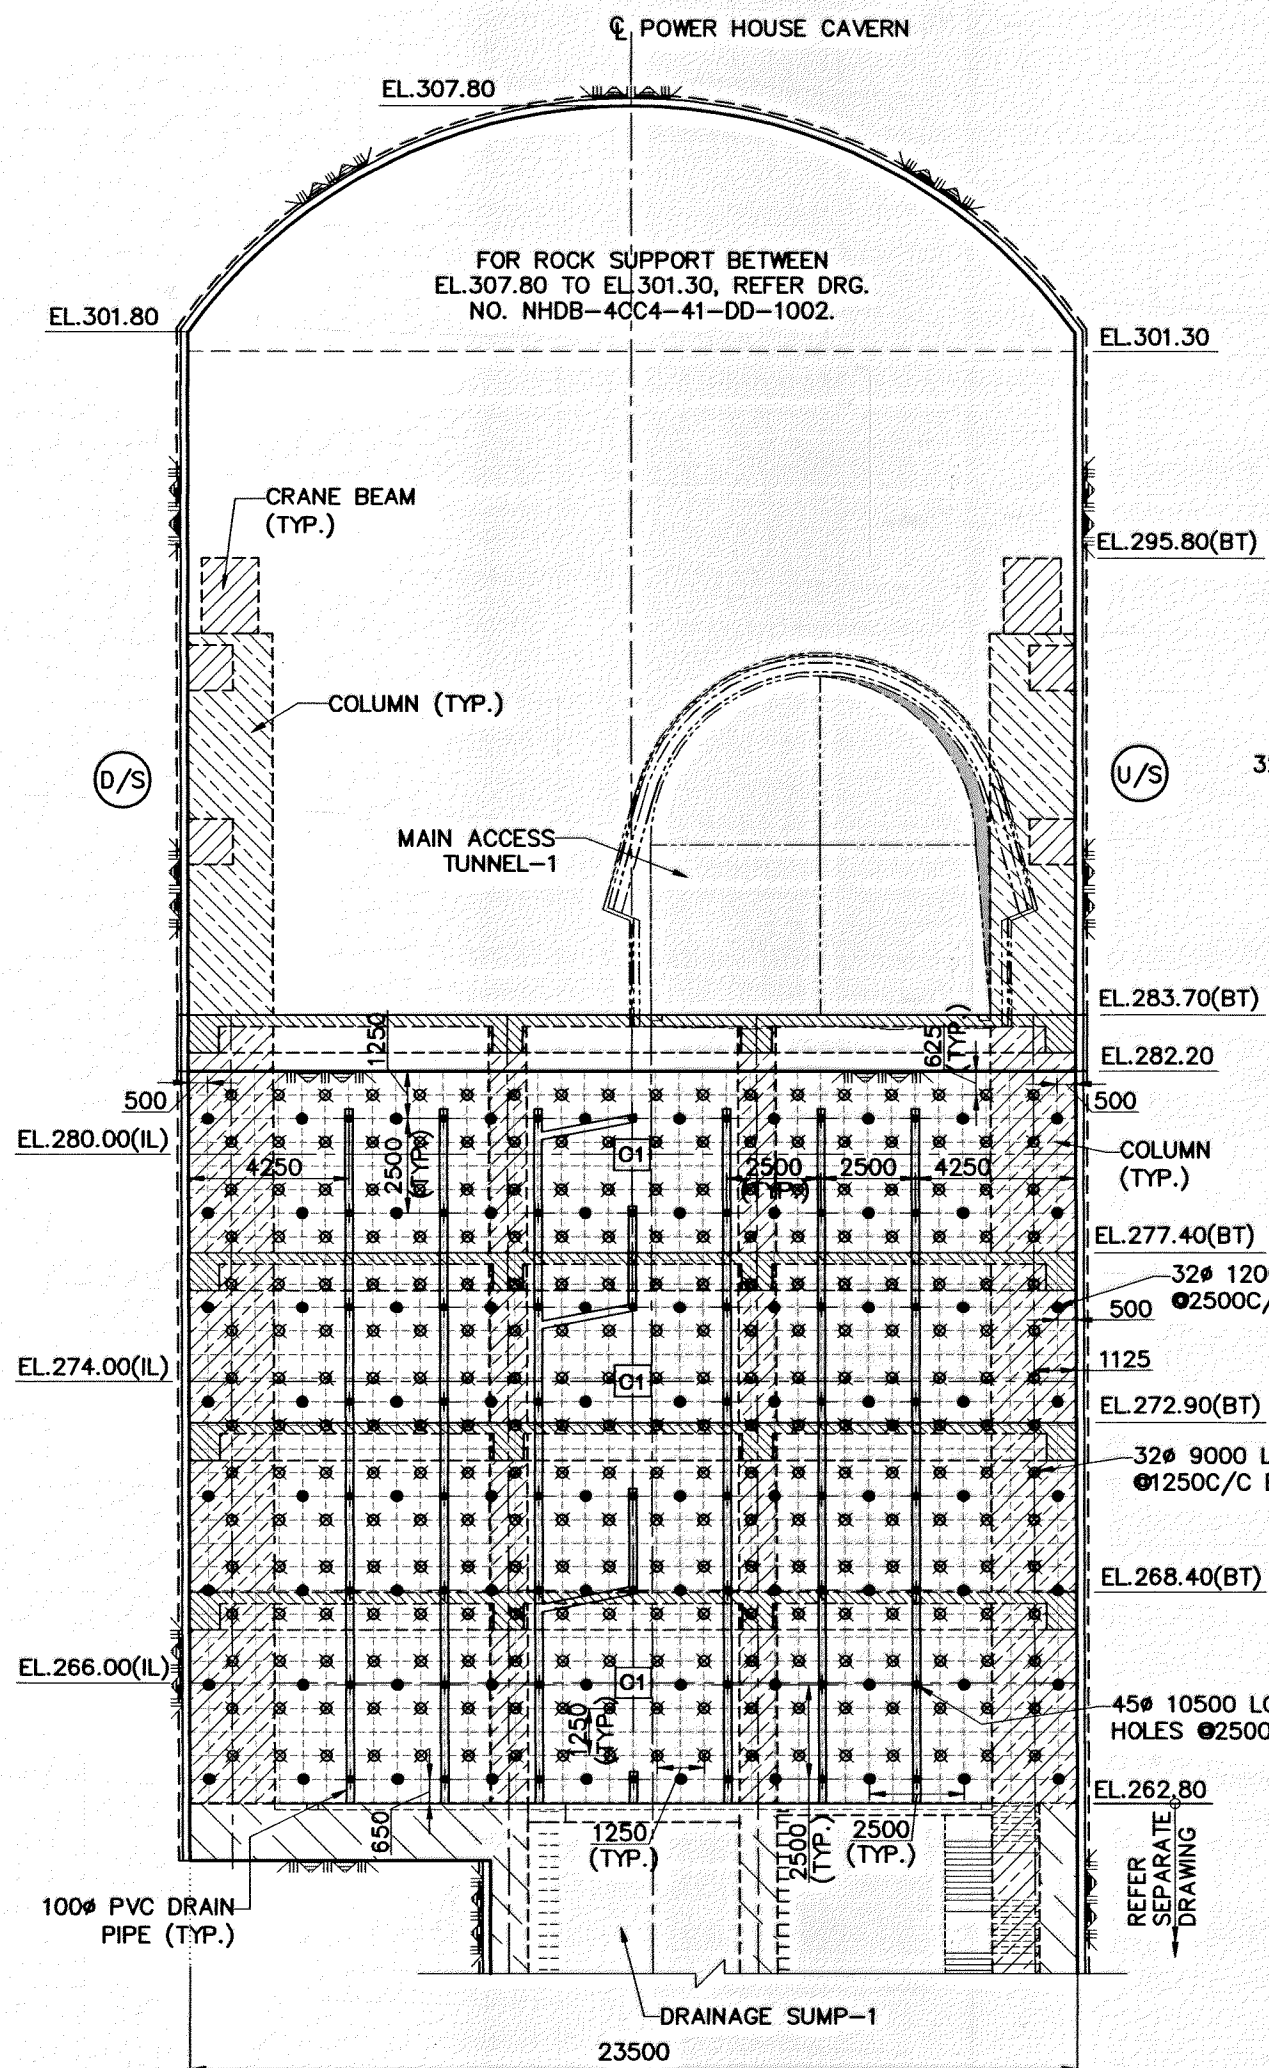

TYPICAL CROSS SECTION-END WALL 
SERVICE BAY-1 (DRAINAGE SUMP-1 SIDE)

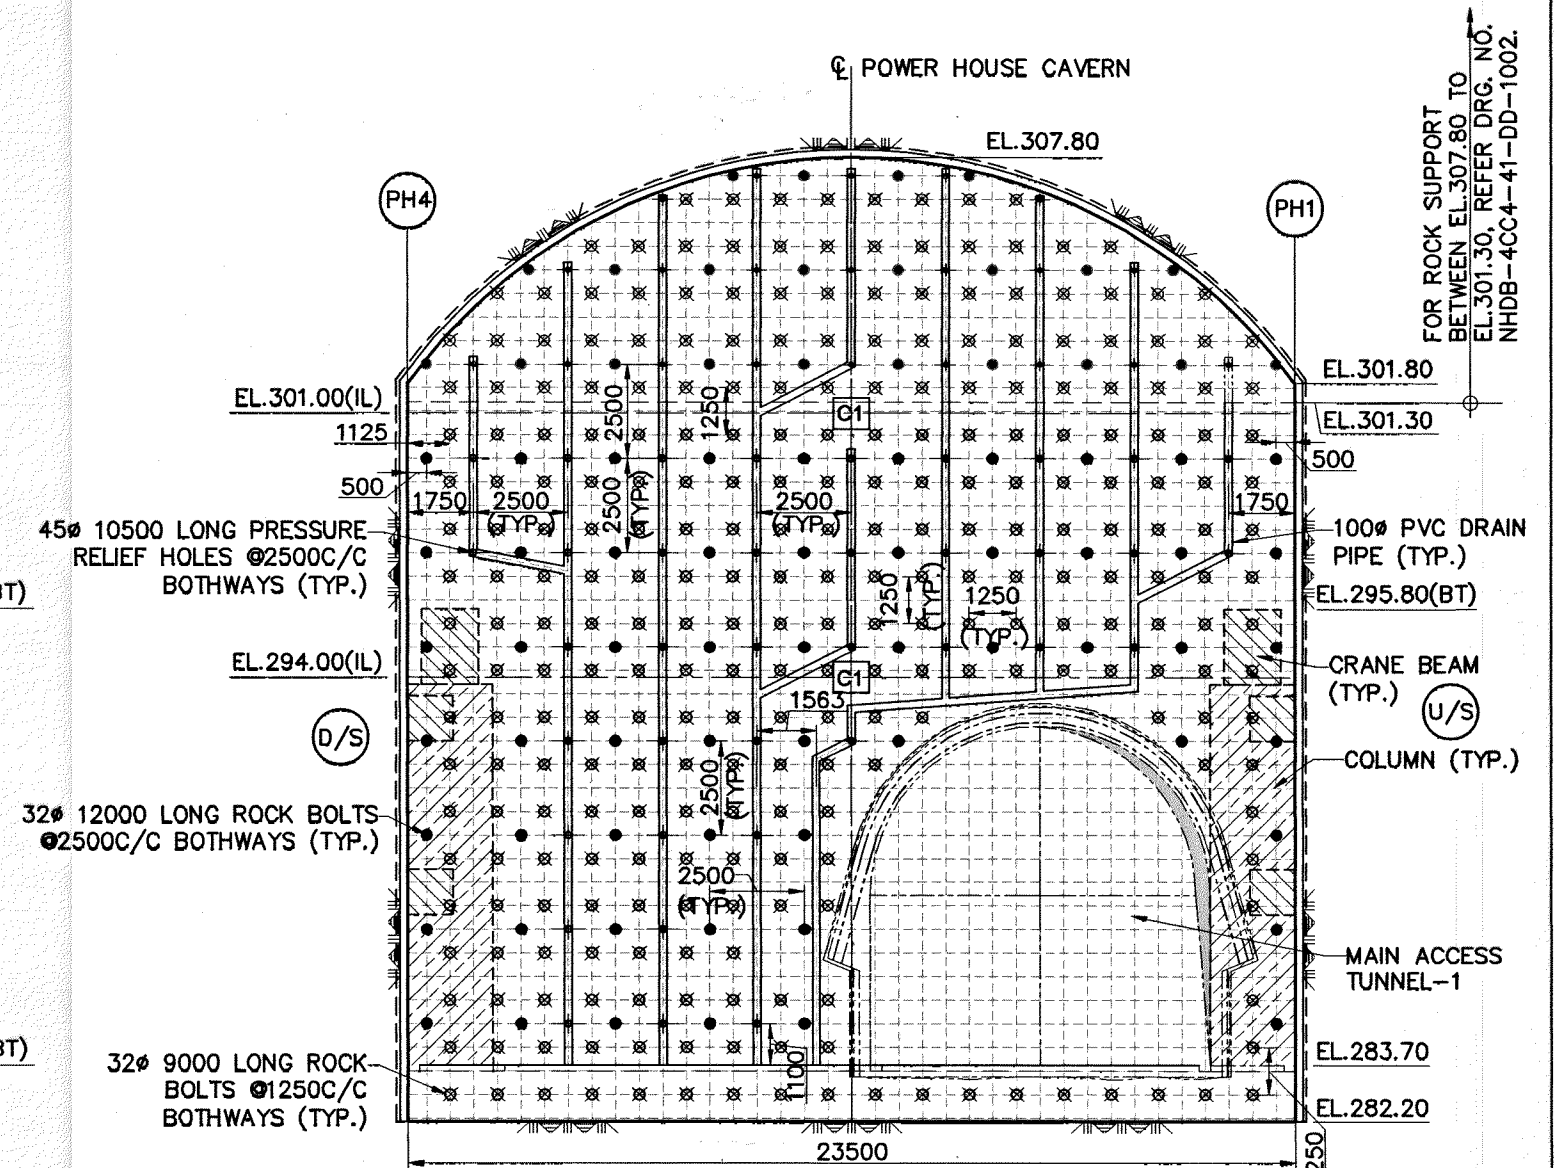

TYPICAL CROSS SECTION-END WALL

SERVICE BAY-1 (MAT-1 SIDE)

A



NOTES:-

1. सभी माप मिलीमीटर में तथा ऊंचाई मीटर में दिए गए हैं ।।
ALL DIMENSIONS ARE IN MILLIMETRE AND ELEVATIONS ARE IN METRE.
2. FOR OTHER NOTES REFER DRAWING NO. NHDB-4CC4-41-DD-1012.
3. THIS DRAWING SHALL BE READ IN CONJUNCTION WITH RELEVANT JUNCTION EXCAVATION DRAWING OF MAT-2/BUS DUCTS/GALLERIES/PENSTOCKS/DRAFT TUBE MANIFOLDS WITH POWER HOUSE WALL.

LEGENDS:-

- 32# 12000 LONG ROCK BOLTS
- ✕ 32# 9000 LONG ROCK BOLTS
- ✕ 45# 10500 LONG PRESSURE RELIEF HOLE
- ✕ CONVERGENCE MEASUREMENT (OPTICAL TARGETS)
- LOAD CELL (30T CAPACITY)
- ## MULTIPLE POINT BORE HOLE EXTENSOMETER
(5M, 10M, 15M) (3 POINTS)
- [C1] ✕ ● (COMBINATION OF INSTRUMENTS-1)
- BT BEAM TOP LEVEL
- IL INSTRUMENTATION LEVEL
- (U/S) UPSTREAM SIDE
- (D/S) DOWNSTREAM SIDE

SCALE:

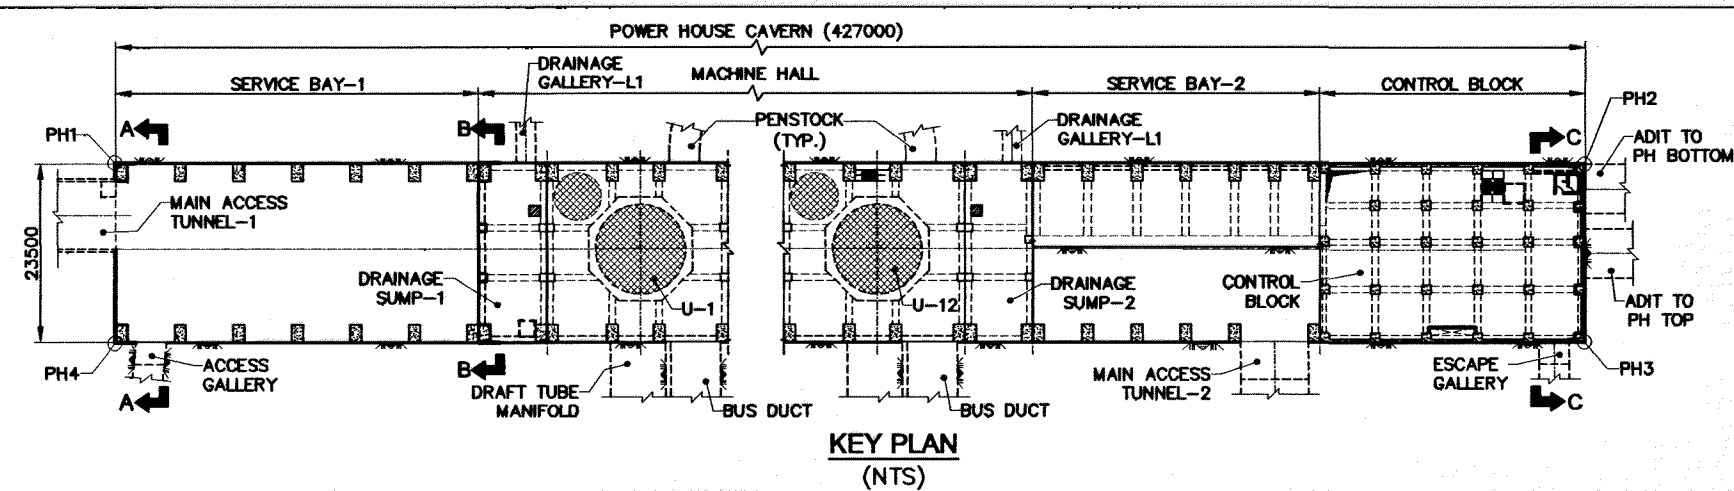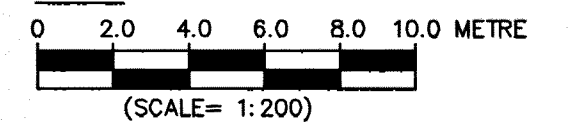

						RACKS/OFF-GRIDS, CABLE RETRACTIONS, PRESSURE RELIEF HOLES AND INSTRUMENTATION (EL.301.30 M TO EL.262.80 M / EL.264.90 M) TYPICAL ARRANGEMENT WALL ELEVATION (SHEET 13 OF 14)									
28.01.2026	00	ISSUED FOR CONSTRUCTION	BY	CH.	APP.	DRAWN अशोक ASHOK KUMAR		SUBMITTED प्रशान्त PRASHANT ASHNA	RECOMMENDED अनुमोदित ANUJ KUMAR		DEMARR		APPROVED अनुमोदित ANUJ KUMAR		
DATE	NO.	REVISION OR ISSUES	BY.	CH.	APP.										
DESIGN MEMO NO.- डिजाइन मेमो संख्या						DATE दिनांक	JAN. 2026	DRG. NO. ड्रॉइंग संख्या	NHDB	4CC4	41	DD	1024 00		