
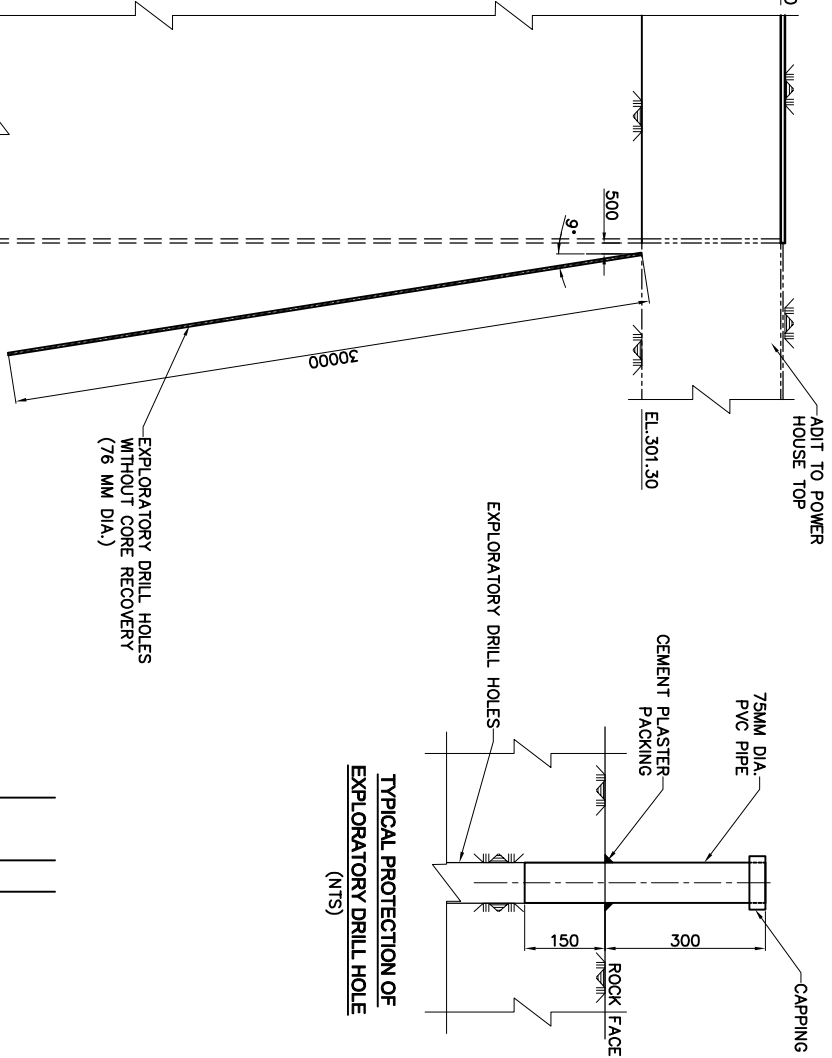
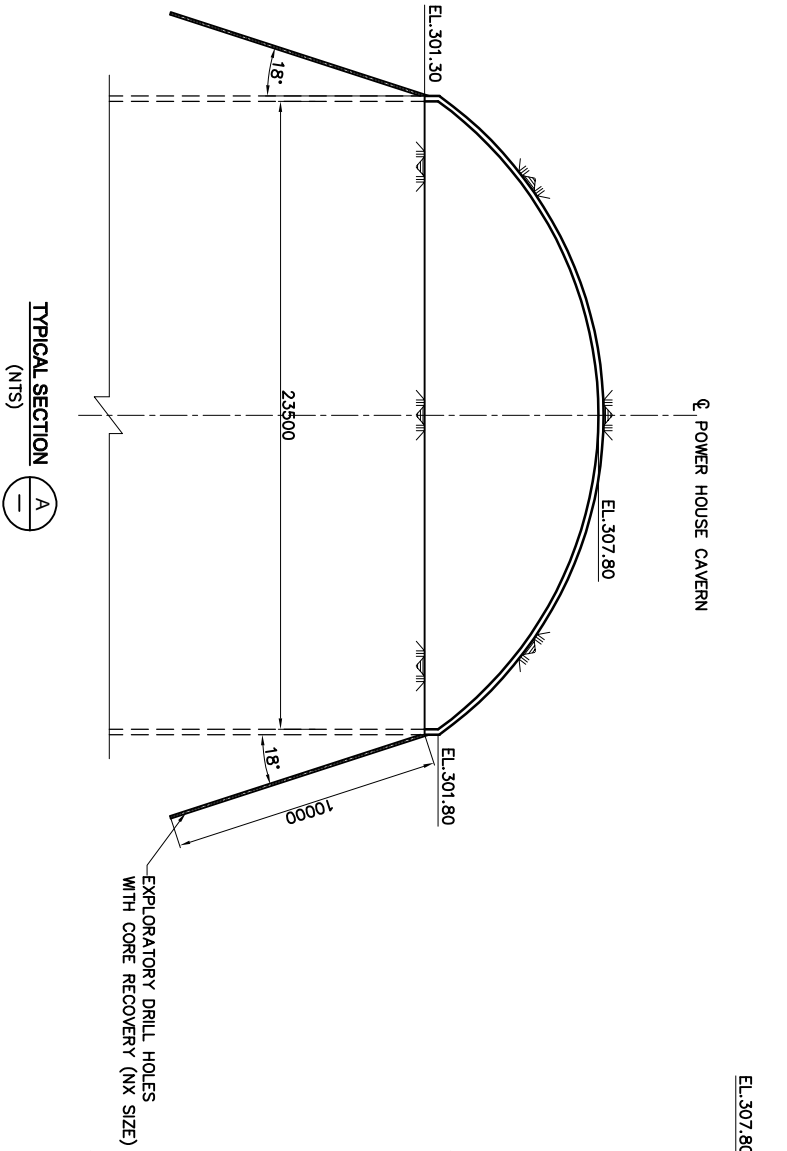
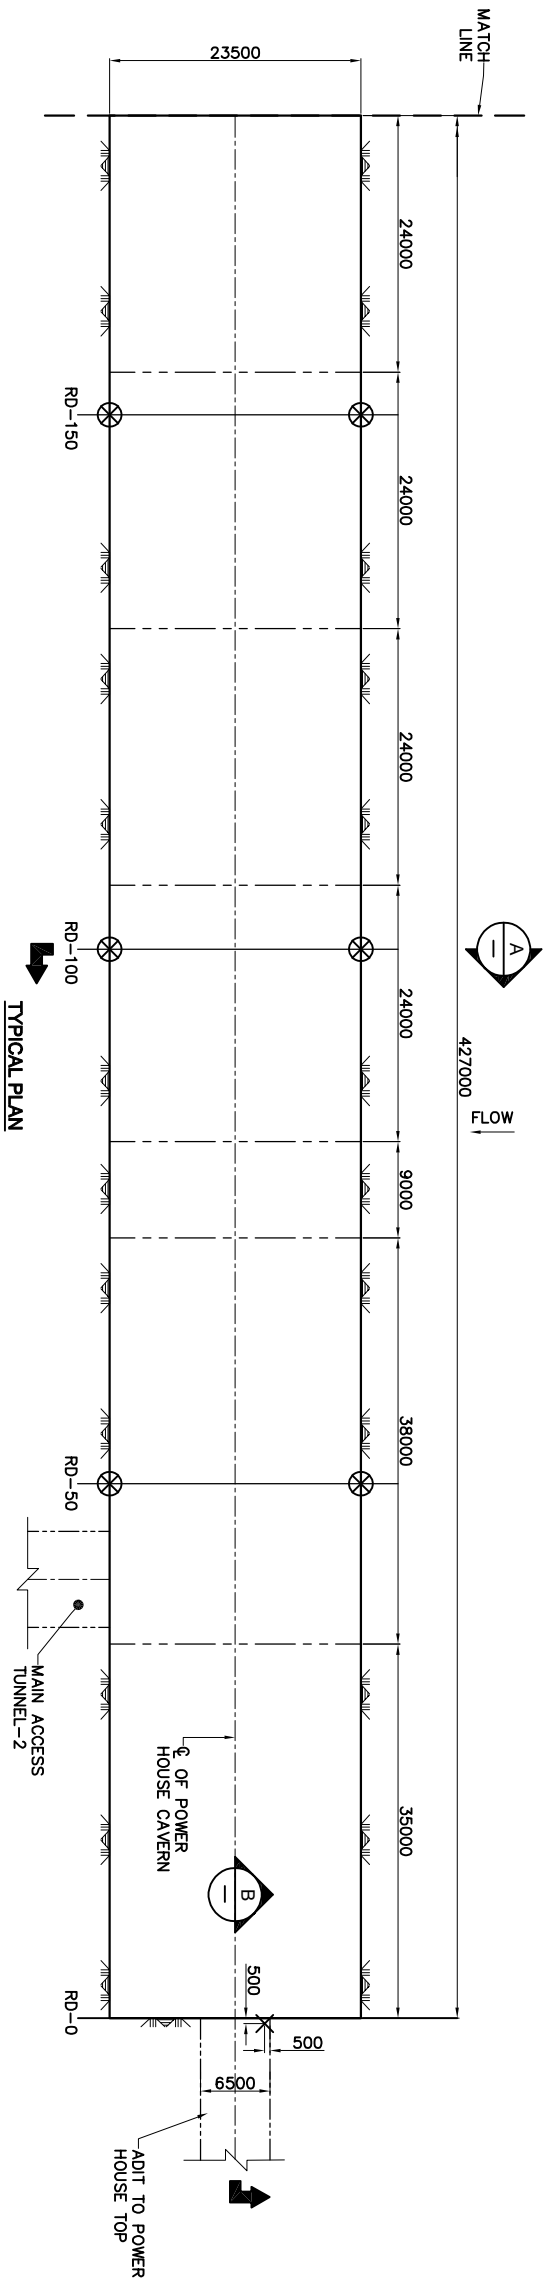
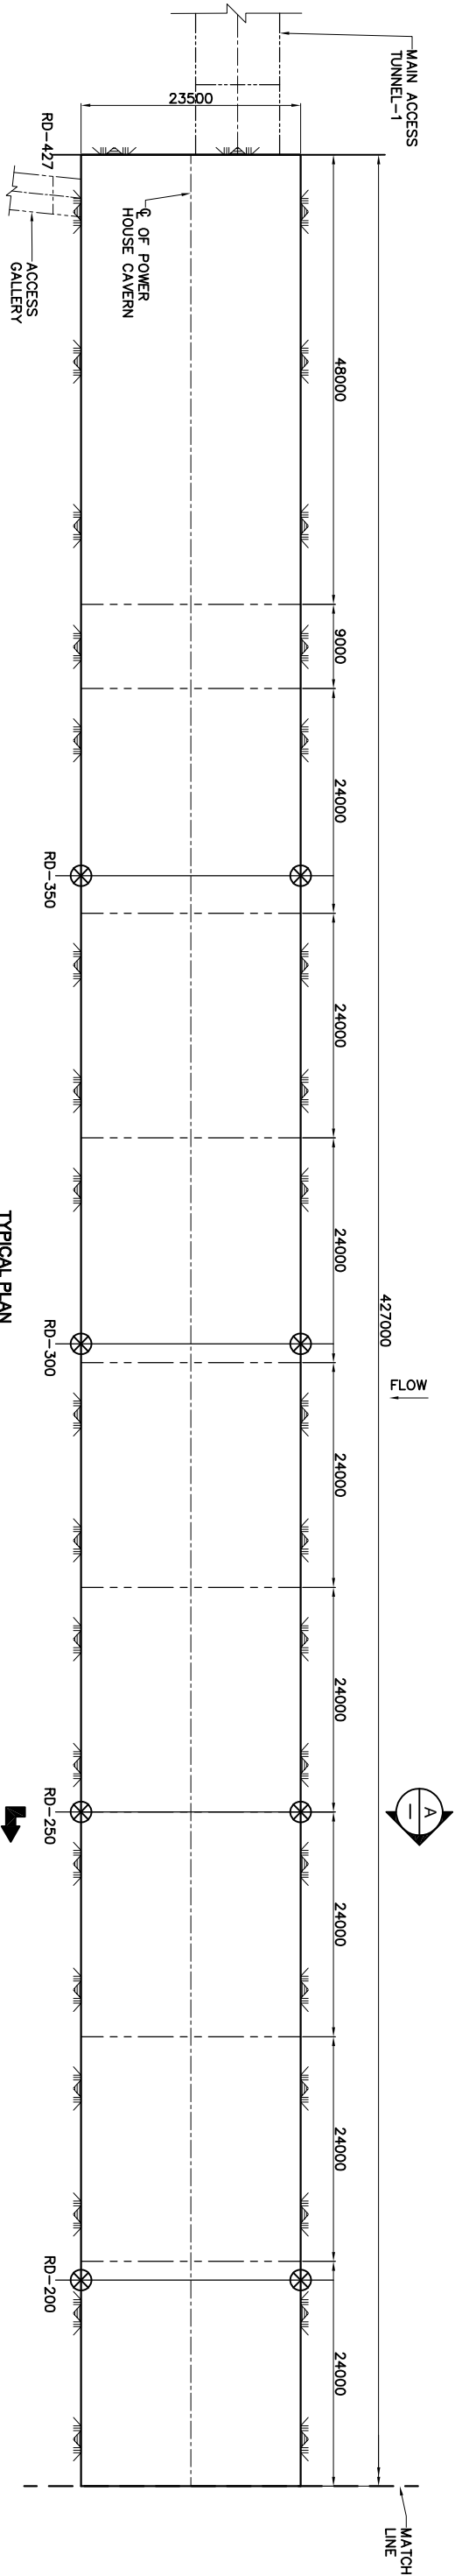


NOTES:

- ALL DIMENSIONS ARE IN MILLIMETRE AND ELEVATIONS ARE IN METRE.
- THIS DRAWING IS PREPARED BASED ON 3D GEOLOGICAL LOG OF POWER HOUSE UPPER PILOT TUNNEL AND IN CONSULTATION WITH GEOLOGY DIVISION.
- EXPLORATORY DRILLING HOLES WITH/WITHOUT CORE RECOVERY SHALL CONFORM TO SECTION B.7 OF TECHNICAL SPECIFICATIONS.
- SUBMITTAL FOR EXPLORATORY DRILL HOLE WITH CORE RECOVERY SHALL BE AS PER CLAUSE 7.2.1 (5) & (7) OF SECTION B.7 OF TECHNICAL SPECIFICATIONS.
- THE CONTRACTOR SHALL COLLECT THE CORES AND THE CORRECT BY PERMANENTLY LABELED WOODEN BLOCKS RECORDING THE MEASURED DISTANCES IN THE HOLE. NO BOX SHALL CONTAIN CORES FROM MORE THAN ONE HOLE. DESIGNATION MARKS, HOLE NUMBERS AND DEPTH VALUES SHALL BE INSCRIBED IN THE BOXES, THE COVER SECURELY FASTENED TO THE CORE BOXES, AND THE BOXES DELIVERED AT AN AREA NEAR THE SITE AS DESIGNATED BY THE ENGINEER-IN-CHARGE.
- THE CONTRACTOR SHALL GIVE THE NECESSARY ASSISTANCE AND FACILITIES TO PERFORM IN SITU TESTS OR EXAMINATION USING BORE HOLE CAMERA OR A GEOPHYSICAL TESTS IN THE SELECTED EXPLORATORY HOLES IF REQUIRED BY ENGINEER-IN-CHARGE.
- DRILL HOLE MAY BE USED FOR DIFFERENT STUDY SO DRILL HOLE SHALL BE PROTECTED FROM DAMAGE.
- THE PVC PIPE SHALL CONFORM TO SECTION B-16 OF TECHNICAL SPECIFICATION.

LEGENDS:-

SL. NO.	DESCRIPTION	SYMBOL	TOTAL DEPTH (m)
1.	EXPLORATORY DRILL HOLES WITH CORE RECOVERY (NX SIZE)		14 NOS.X10 = 140 M
2.	EXPLORATORY DRILL HOLES WITHOUT CORE RECOVERY		30 M

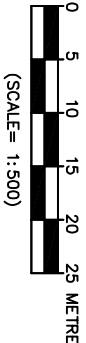

00-05-2026	00	ISSUED FOR CONSTRUCTION			
DATE	NO.	REVISION OR ISSUES	BY:	CH. APP.	

एन एच पी सी लिमिटेड NHPC A FINANCIAL COMPANY		एन एच पी सी लिमिटेड ONE HOUSE IN ONE SCHEMATIC NHPC Limited A GOVT. OF INDIA UNDERTAKING ENTERPRISE			
दिबांग बहुउद्देशीय परियोजना DIBANG MULTIPURPOSE PROJECT					
POWER HOUSE CAVERN EXPLORATORY DRILL HOLES LOCATION (SCHEMATIC)					
PROJ. NO.	SUBMITTED	RECOMMENDED	DESIGNED		APPROVED
DATE	DR. NO.	DR. NO.	DR. NO.		DR. NO.
MAY, 2026	NHDB	ACQ4	41	DD	7002
					00