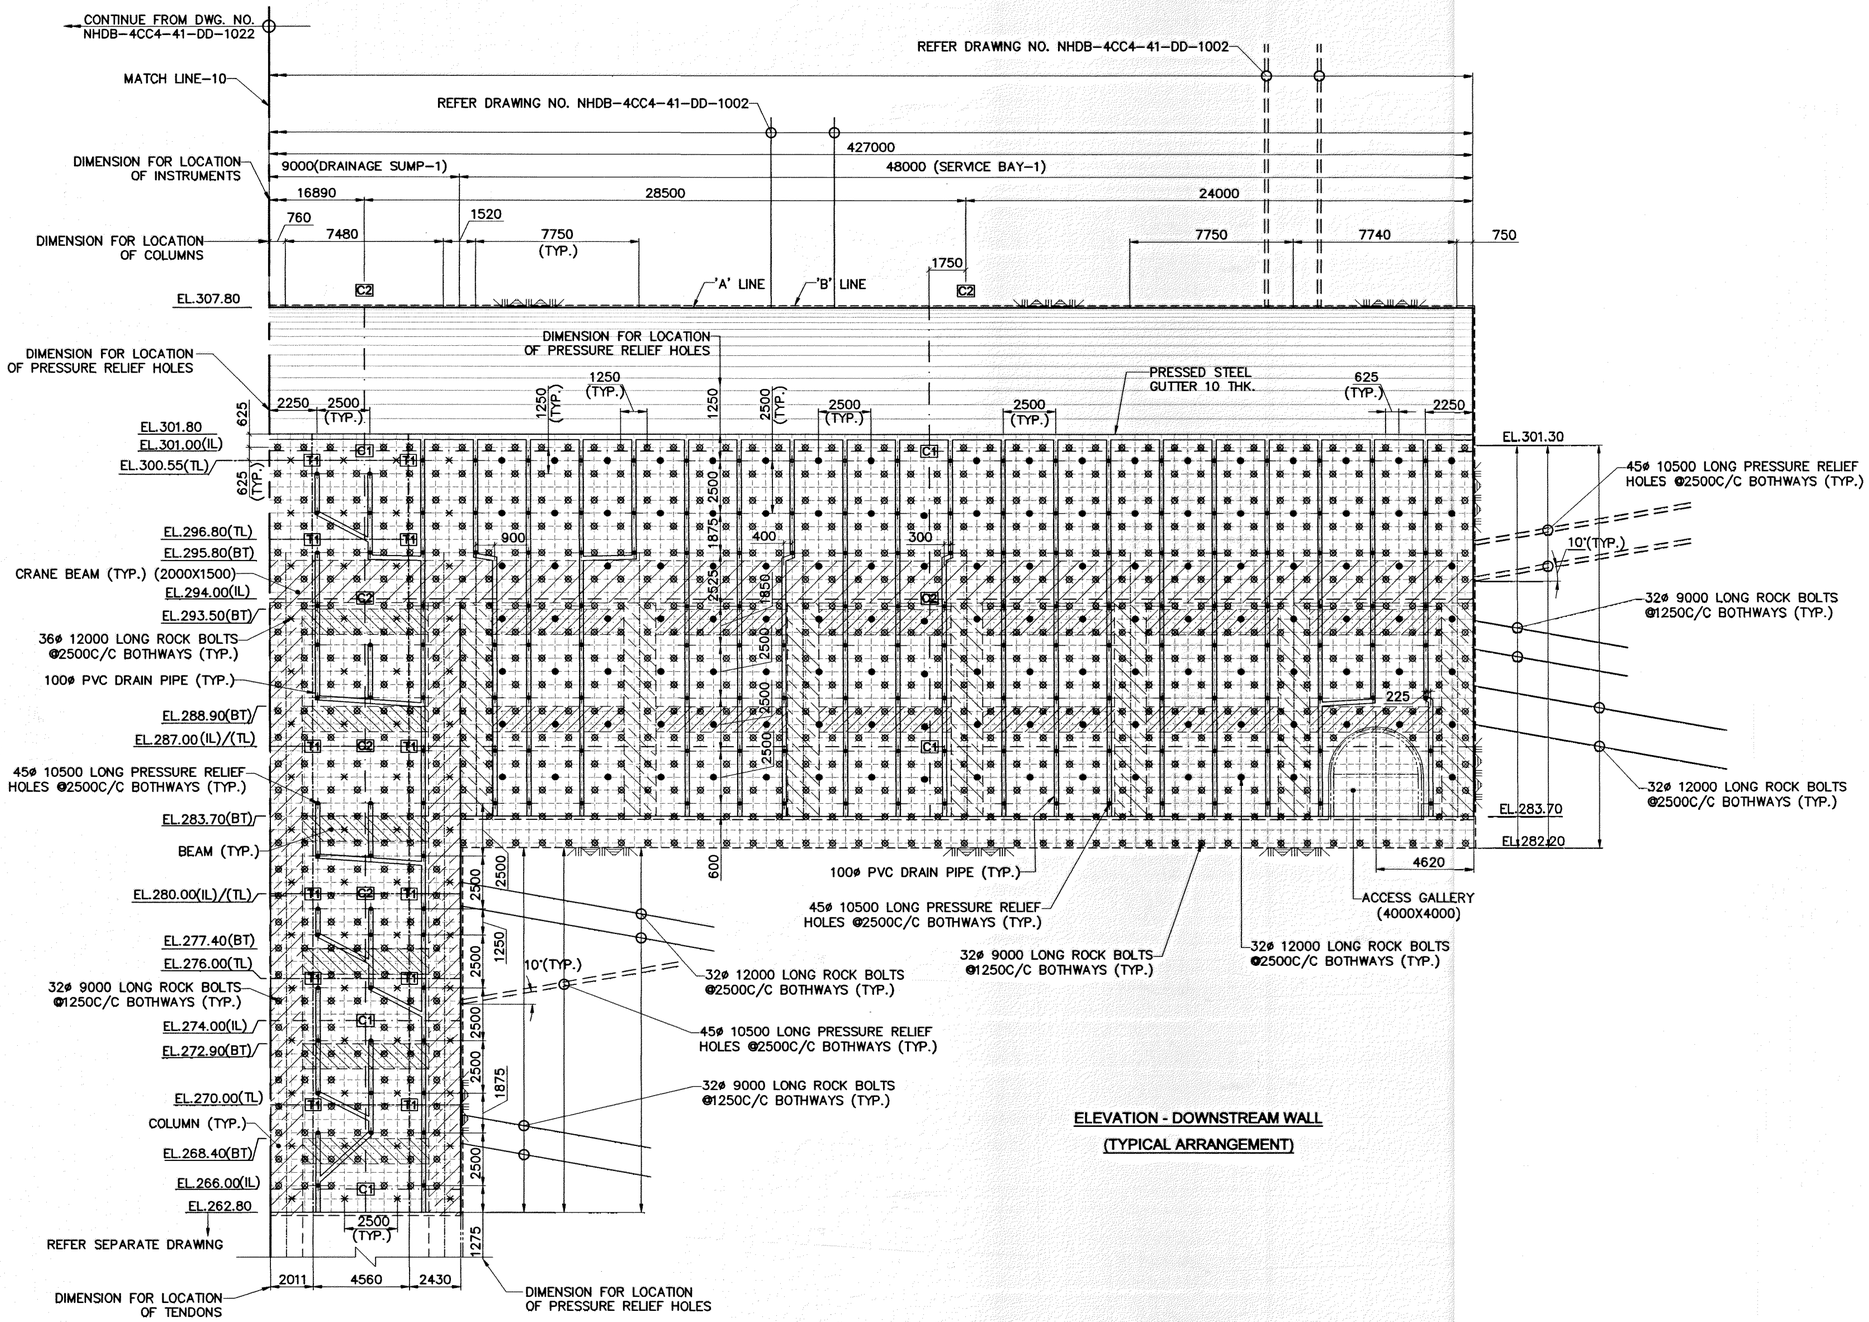


ELEVATION - DOWNSTREAM WALL

(TYPICAL ARRANGEMENT)

NOTES:

1. सभी माप मिलीमीटर में तथा ऊंचाई मीटर में दिए गए हैं ।
 ALL DIMENSIONS ARE IN MILLIMETRE AND ELEVATIONS ARE IN METRE.
2. FOR OTHER NOTES REFER DRAWING NO. NHDB-4CC4-41-DD-1012.
3. THIS DRAWING SHALL BE READ IN CONJUNCTION WITH RELEVANT JUNCTION EXCAVATION DRAWING OF MAT-2/BUS DUCTS/GALLERIES/PENSTOCKS/DRAFT TUBE MANIFOLDS WITH POWER HOUSE WALL.

LEGENDS:-

- ⊠ 36ø 12000 LONG ROCK BOLTS
- ● 32ø 12000 LONG ROCK BOLTS
- ⊠ 32ø 9000 LONG ROCK BOLTS
- T1 (TYPE-1)-1200KN GUARANTEED ULTIMATE TENSILE STRENGTH (GUTS),LOCK OFF LOAD SHALL BE 60% OF GUTS, TOTAL LENGTH=30M.
- ⊕ 45ø 10500 LONG PRESSURE RELIEF HOLE
- × CONVERGENCE MEASURMENT (OPTICAL TARGETS)
- LOAD CELL (30T CAPACITY)
- MULTIPLE POINT BORE HOLE EXTENSOMETER (5M, 10M, 15M) (3 POINTS)
- MULTIPLE POINT BORE HOLE EXTENSOMETER (4M, 7M, 10M, 13M, 16M, 19M) (6 POINT)
- C1 × # (COMBINATION OF INSTRUMENTS-1)
- C2 × (COMBINATION OF INSTRUMENTS-2)

BT BEAM TOP LEVEL
TL TENDONS LEVEL
IL INSTRUMENTATION LEVEL

SCALE:

0 2.0 4.0 6.0 8.0 10.0 METRE

(SCALE= 1:200)

28.01.2026	00	ISSUED FOR CONSTRUCTION			
DATE	NO.	REVISION OR ISSUES	BY.	CH.	APP.

DESIGN MEMO NO.:- डिज़ाइन मेमो संख्या

एनएचपीसी NHPC A Navratna Company

एन एच पी सी लिमिटेड
(भारत सरकार का एक नवरत्न उद्यम)
NHPC Limited
(A GOVT. OF INDIA NAVRATNA ENTERPRISE)

दिबांग बहुउद्देशीय परियोजना
DIBANG MULTIPURPOSE PROJECT

POWER HOUSE
ROCK SUPPORTS, CABLE TENDONS,
PRESSURE RELIEF HOLES AND INSTRUMENTATION
(EL.301.30 M TO EL.262.80 M / EL.264.90 M)
TYPICAL ARRANGEMENT
WALL ELEVATION (SHEET 12 OF 14)

DRAWN अंकित	SUBMITTED प्रस्तुत	RECOMMENDED अनुशंसित		APPROVED अनुमोदित
VINAY KUMAR	PRABHAT ASWAL	NISHI JOSHI RAJEEV KUMAR	DEWM	S. CHOWDHURY

DATE दिनांक	DRG. NO.					
JAN 2026	NHDB	4CC4	41	DD	1023	00

DRG. NO. NHDB-4CC4-41-DD-1023-00

IMS/DED/F-02 REV. NO. : 03 EFF. DATE 21.07.2016