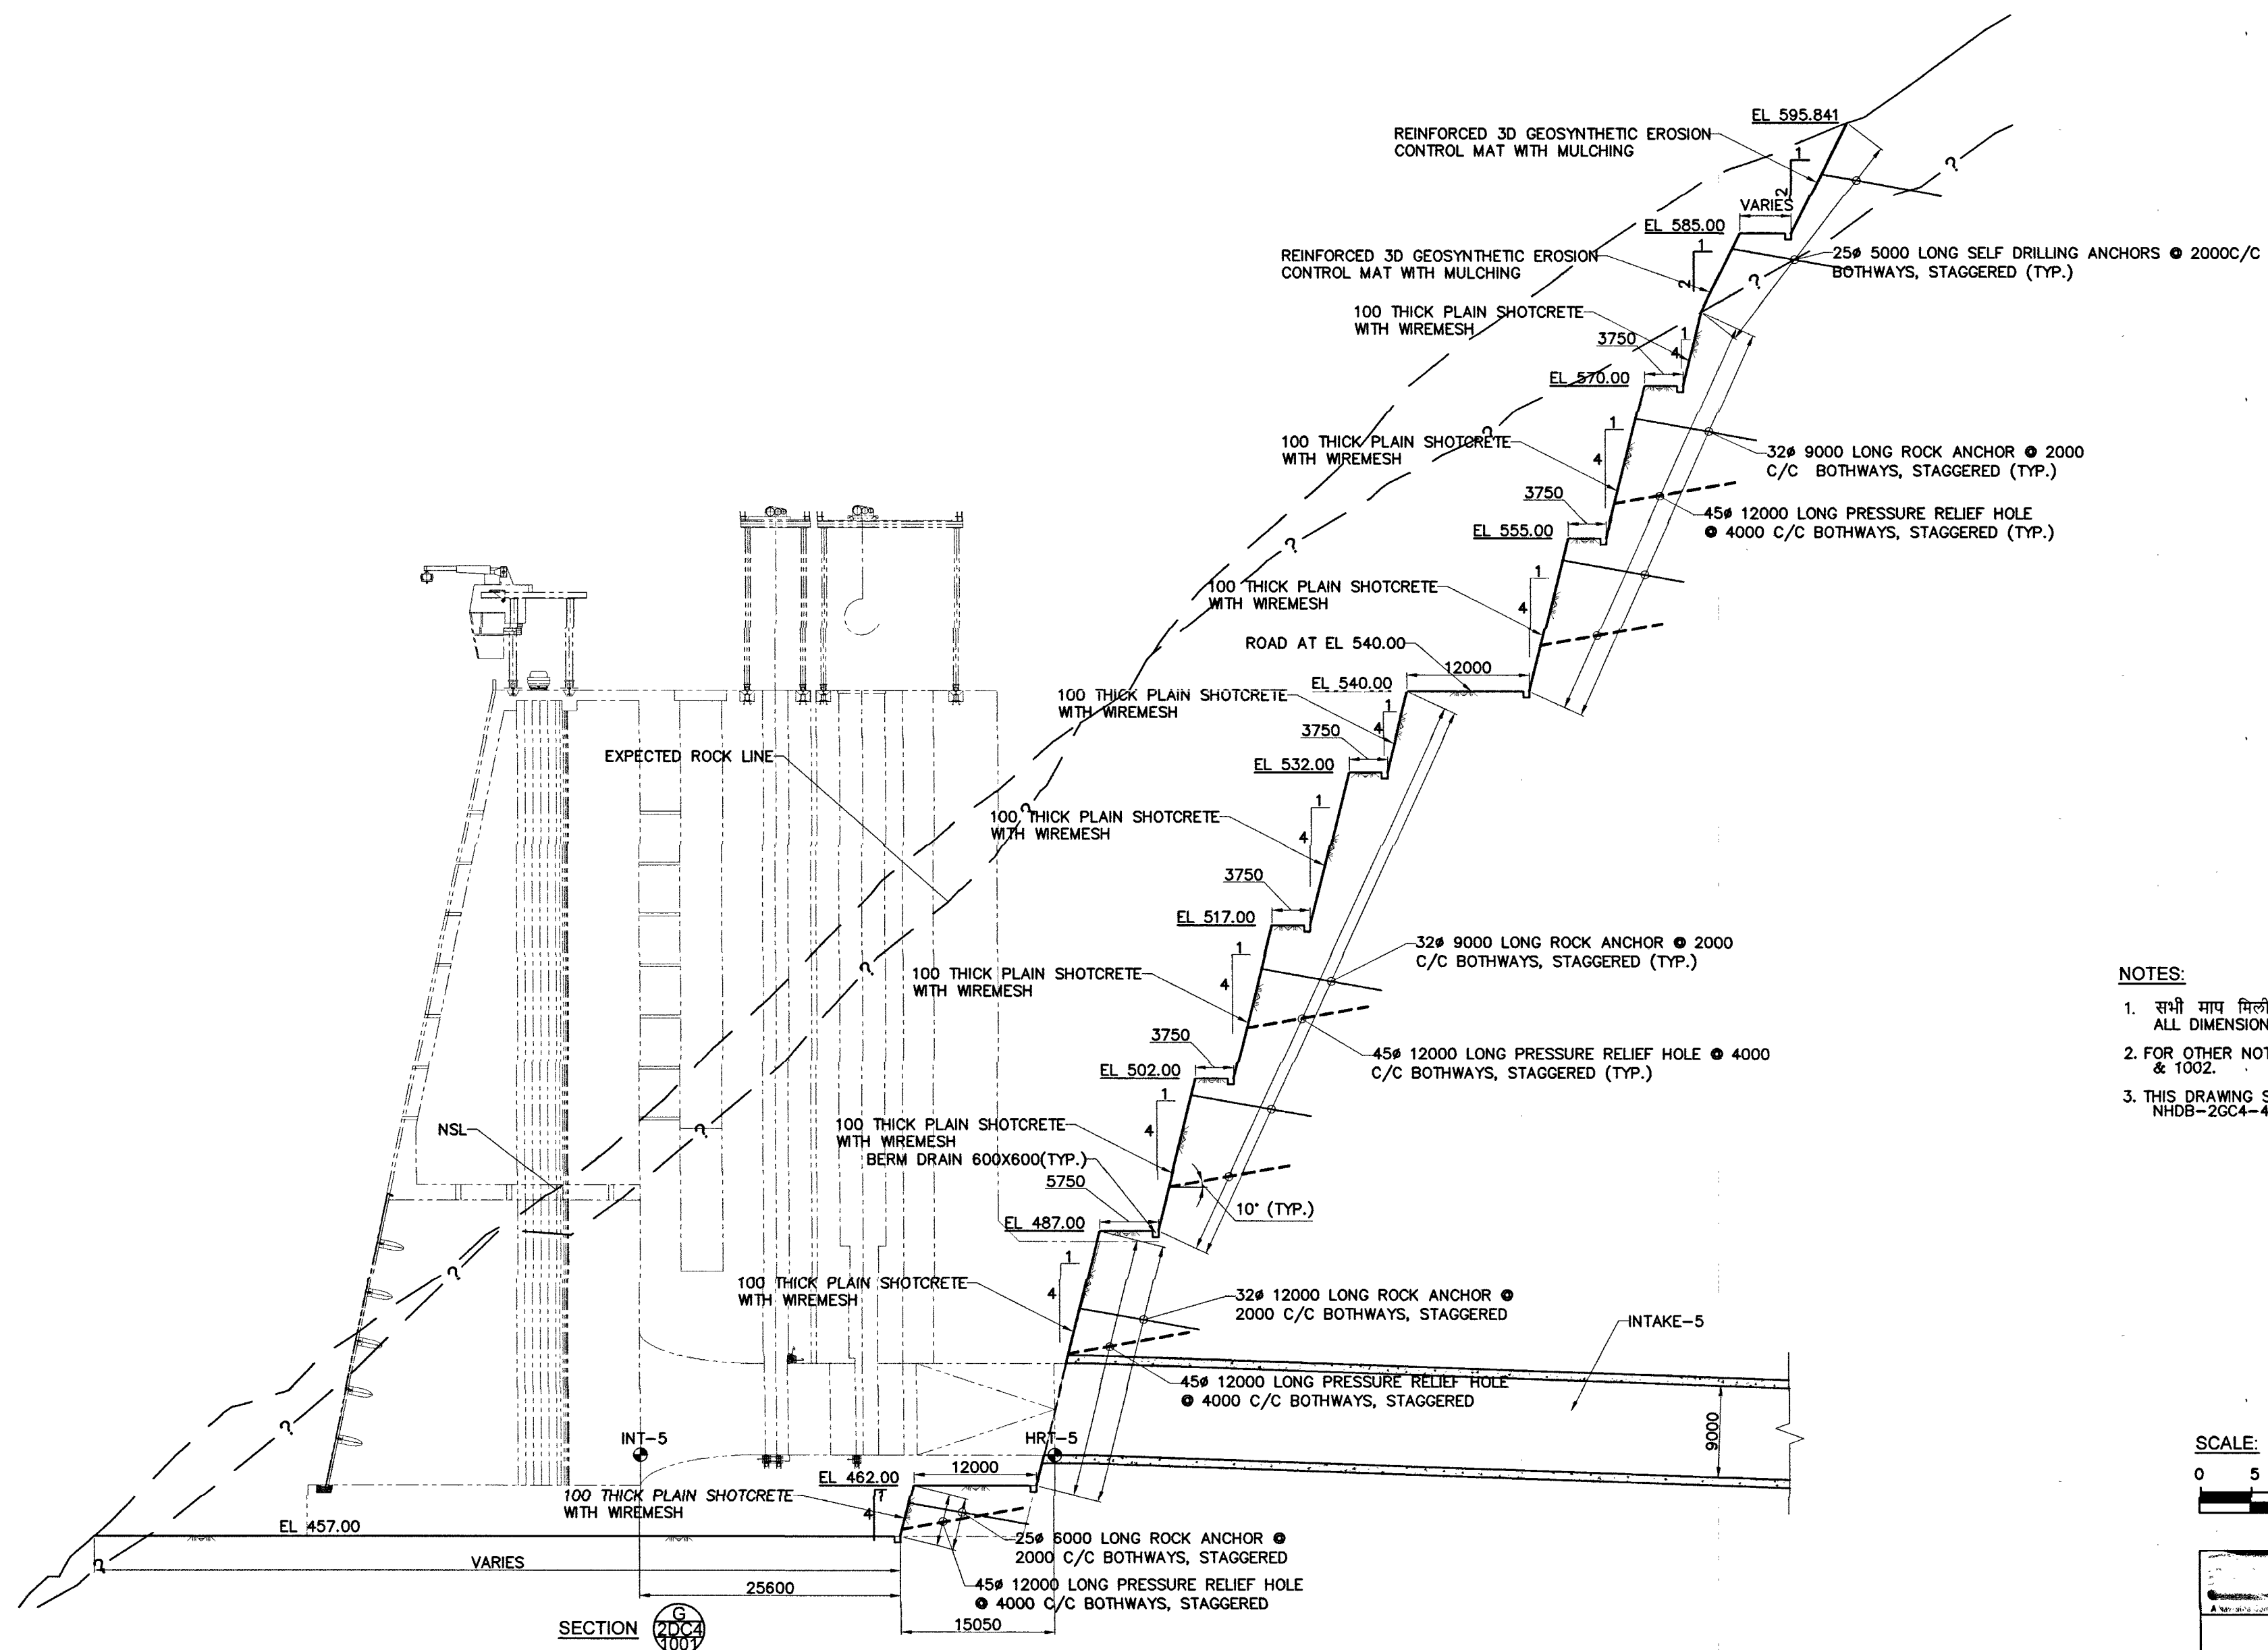
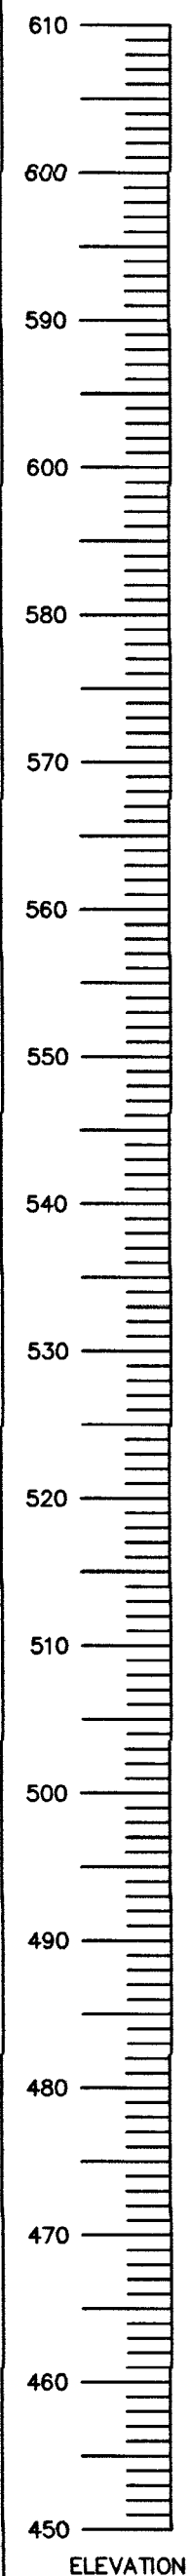
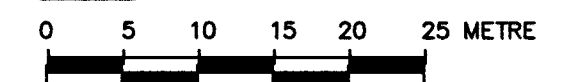


**NOTES:**

- सभी माप मिलीमीटर में तथा ऊंचाई मीटर में दिए गए हैं।
ALL DIMENSIONS ARE IN MILLIMETRES AND ELEVATIONS IN METRES.
- FOR OTHER NOTES REFER DRAWING NO. NHDB-2GC4-41-DD-1001 & 1002.
- THIS DRAWING SHALL BE READ IN CONJUNCTION WITH DRAWING NO. NHDB-2GC4-41-DD-1001 TO 1008 & 1009 TO 1013.

SCALE:

एन एच पी सी लिमिटेड (भारत सरकार का एक नवेली उद्यम) NHPC Limited (A GOVT. OF INDIA ENTERPRISE)	
दिबांग बहुउद्देशीय परियोजना DIBANG MULTIPURPOSE PROJECT	
POWER INTAKE EXCAVATION AND ROCK SUPPORT SECTIONS	
SHEET 08 OF 13	
DATE 07.03.25	NO. 1008
REVISION OR ISSUES 1.	BY CH. APT.
DATE MAR 2025	DRG. NO. NHDB 2GC4 41 DD 1008
DESIGN MEMO NO. दिबांग मगो संरक्षा	APPROVED अनुमोदन