


INKJET 75 MIC D/M BH. NO. TP-15100/2 PRINT ON THIS SIDE

DRG. NO. NHDB-2GC4-41-DD-1010-00

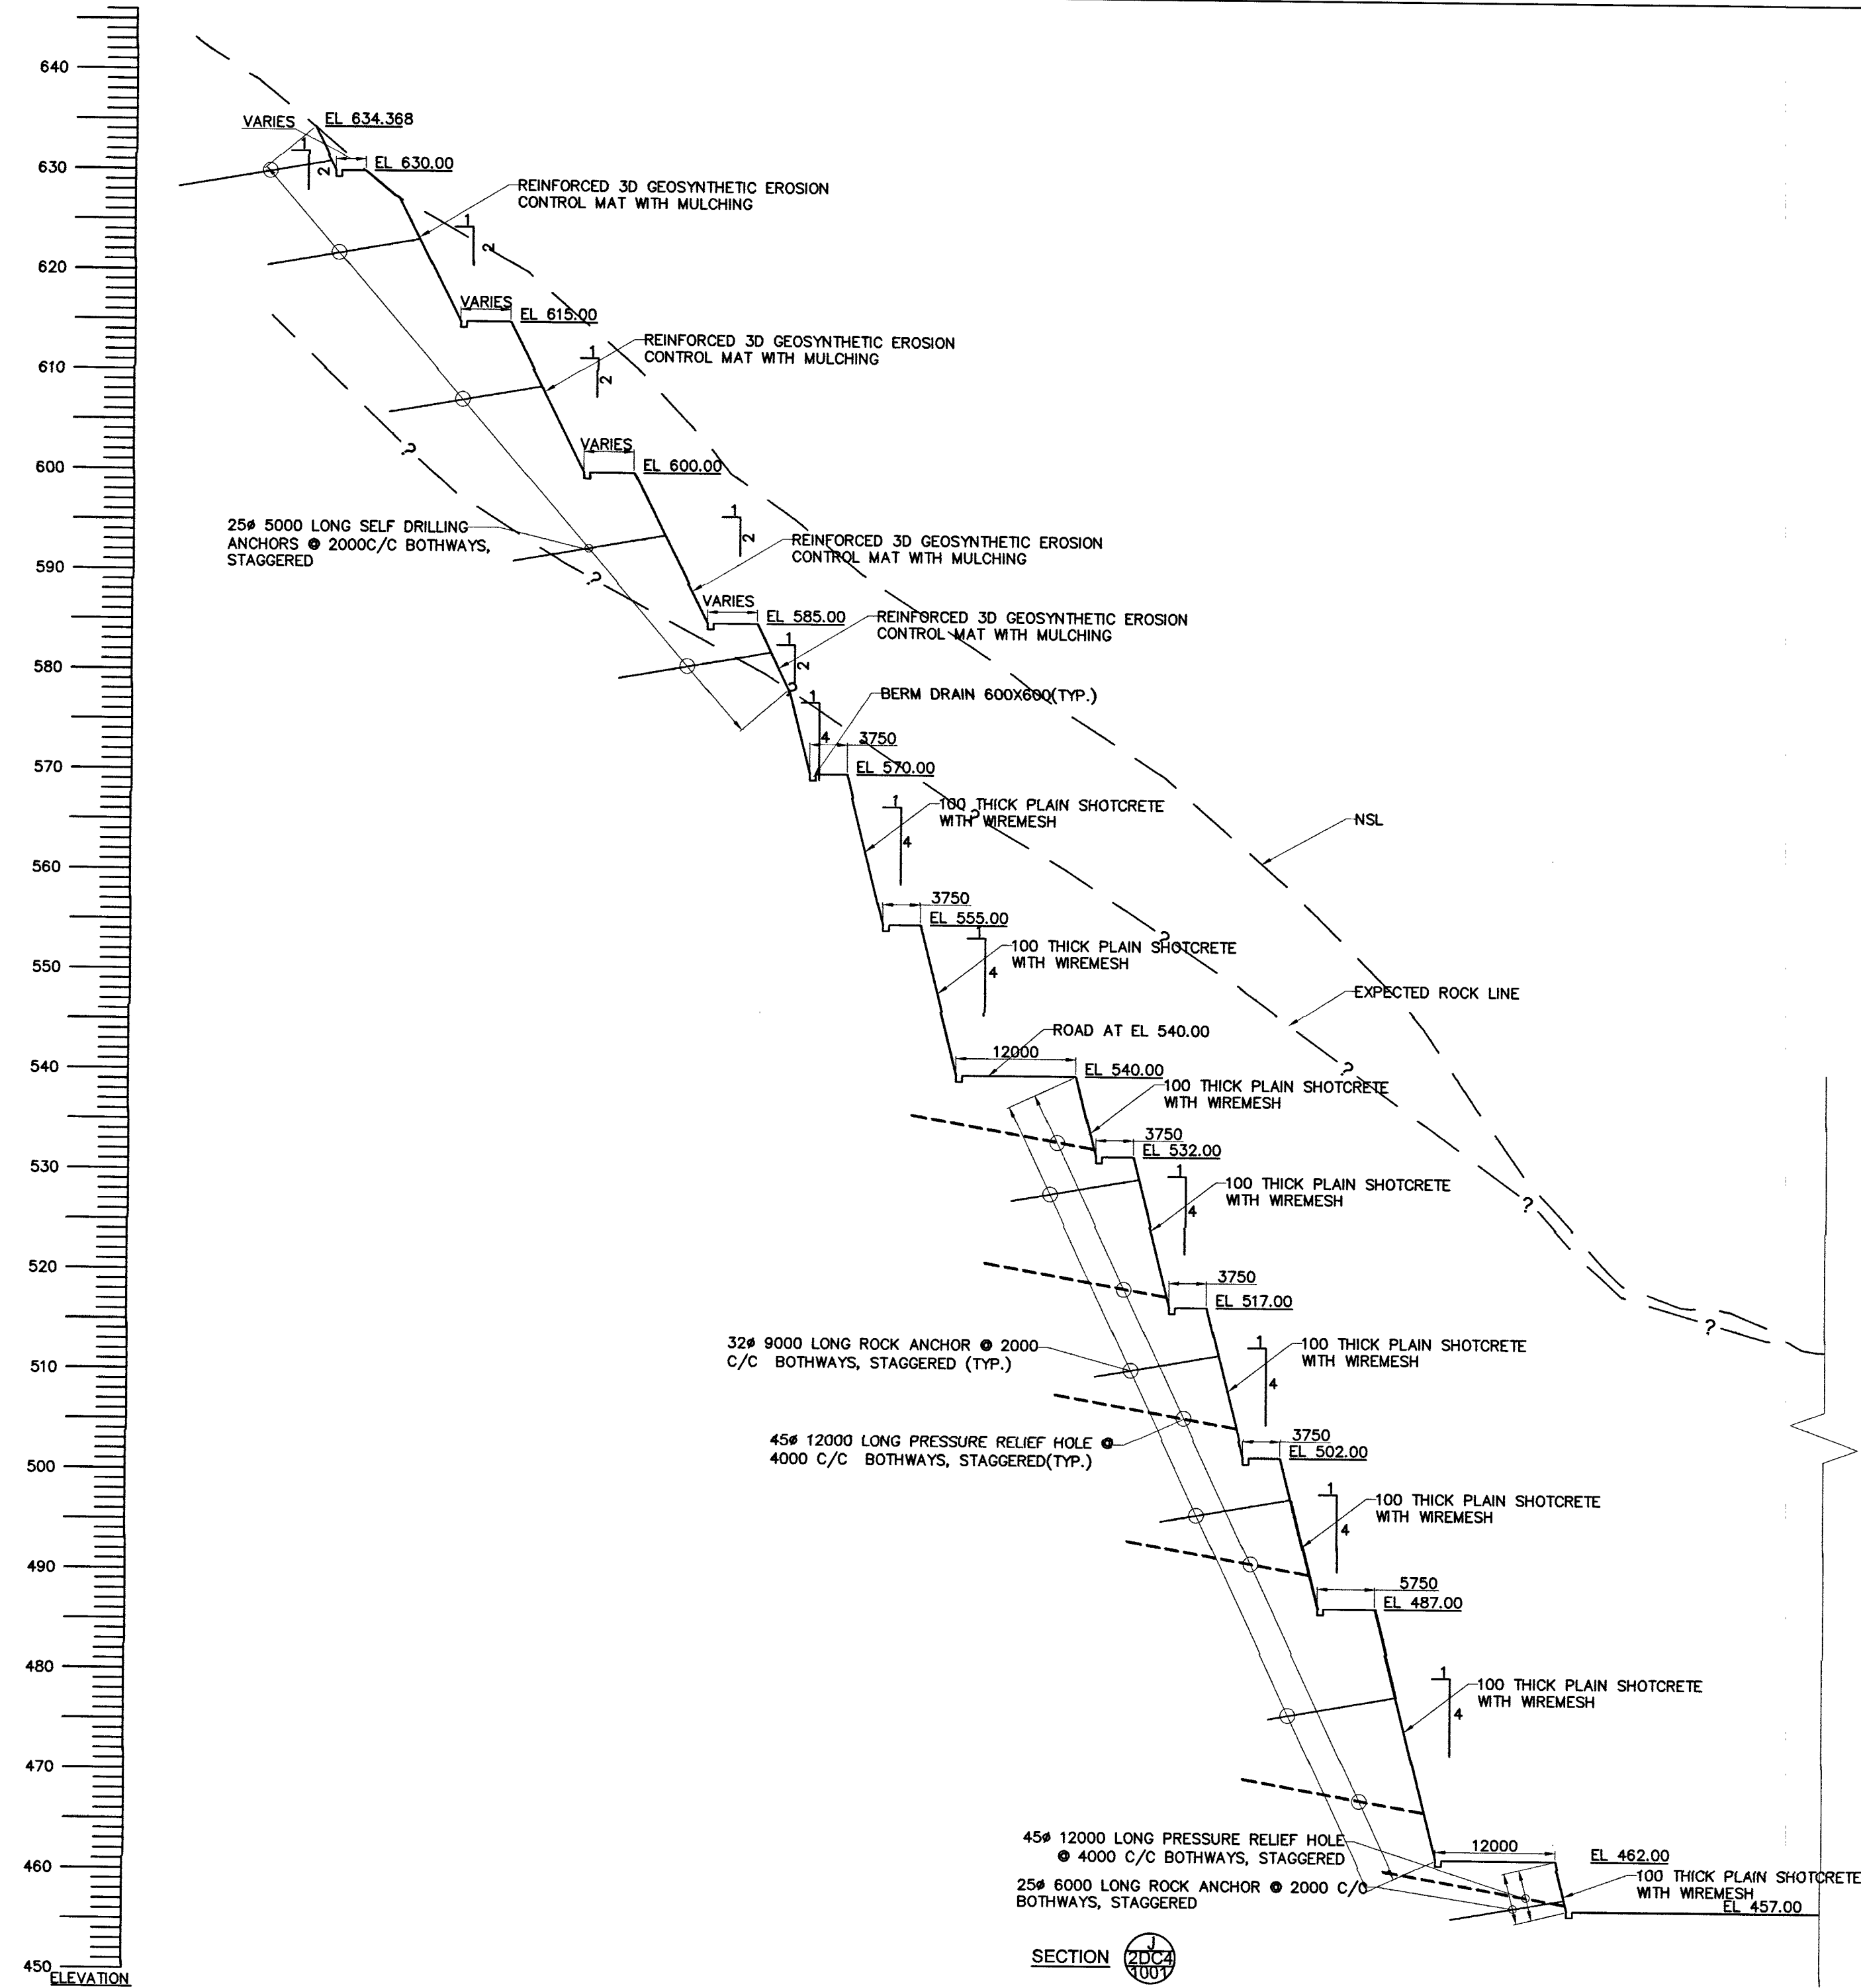

- NOTES:**
- सभी माप मिलीमीटर में तथा ऊंचाई मीटर में दिए गए हैं।
ALL DIMENSIONS ARE IN MILLIMETRES AND ELEVATIONS IN METRES.
 - FOR OTHER NOTES REFER DRAWING NO. NHDB-2GC4-41-DD-1001 & 1002
 - THIS DRAWING SHALL BE READ IN CONJUNCTION WITH DRAWING NO. NHDB-2GC4-41-DD-1001 TO 1009 & 1011 TO 1013.



एन एच पी सी लिमिटेड (भारत सरकार का एक नगरपालिका उद्योग) NHPC Limited (A GOVT. OF INDIA NAVRATNA ENTERPRISE)	
दिवांग बहुउद्देशीय परियोजना DIBANG MULTIPURPOSE PROJECT	
POWER INTAKE EXCAVATION AND ROCK SUPPORT SECTIONS	
SHEET 10 OF 13	
DATE 07.03.25	REVISION OR ISSUES
BY CH. APP.	BY CH. APP.
DATE 07.03.25	DRG. NO. NHDB 2GC4 41 DD 1010 00
RECOMMENDED	APPROVED