



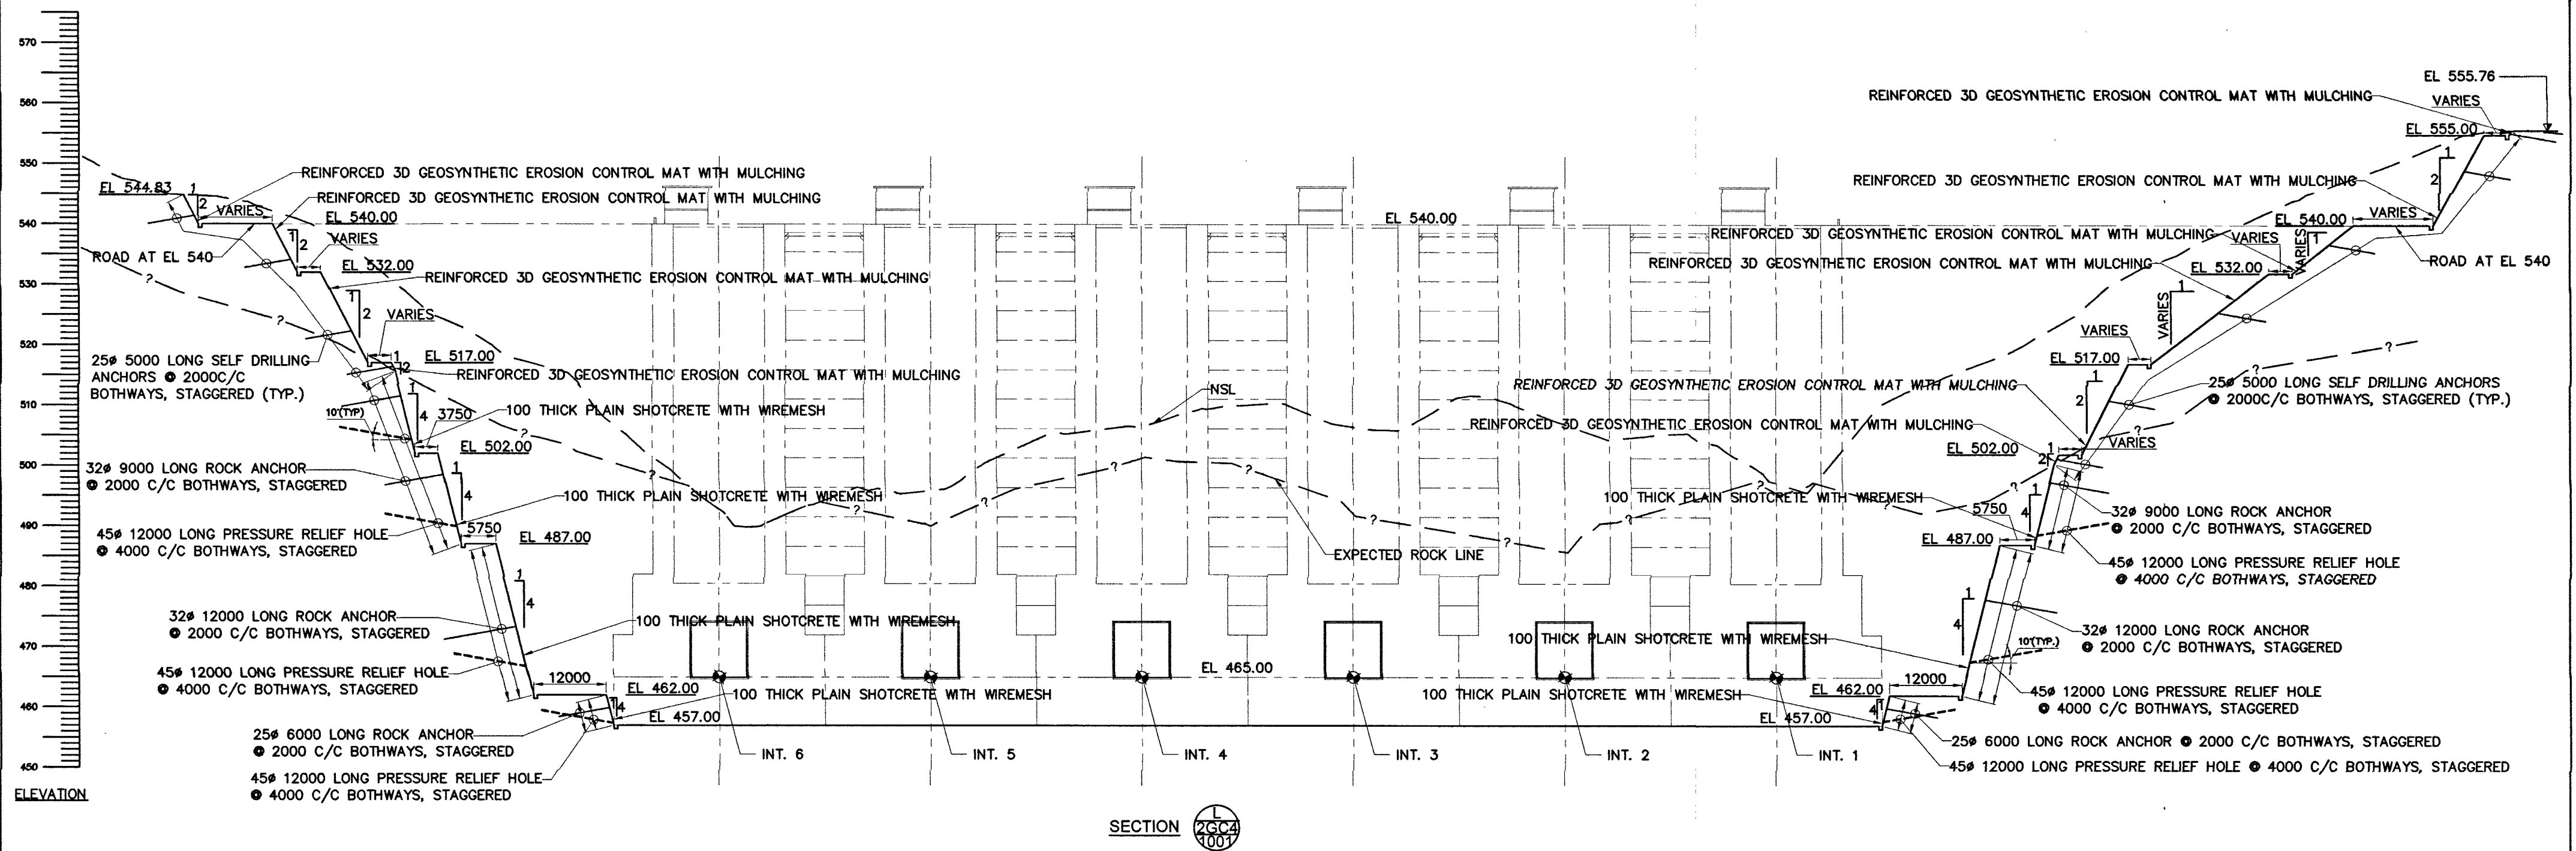

NOTES:

- सभी माप मिलीमीटर में तथा ऊँचाई मीटर में लिए गए हैं।
ALL DIMENSIONS ARE IN MILLIMETRES AND ELEVATIONS IN METRES.
- FOR OTHER NOTES REFER DRAWING NO. NHDB-2GC4-41-DD-1001 & 1002.
- THIS DRAWING SHALL BE READ IN CONJUNCTION WITH DRAWING NO. NHDB-2GC4-41-DD-1001 TO 1010 & 1011,1013.

SCALE:

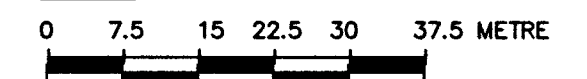

एन एच पी सी लिमिटेड (भारत सरकार का एक स्वतंत्र अंग) NHPC Limited (A GOVT. OF INDIA NAVRATNA ENTERPRISE)	
दिबांग बहुउद्देशीय परियोजना DIBANG MULTIPURPOSE PROJECT	
POWER INTAKE EXCAVATION AND ROCK SUPPORT SECTIONS	
SHEET 12 OF 13	
07.03.25 00	ISSUED FOR CONSTRUCTION
DATE NO.	REVISION OR ISSUES
DESIGN MEMO NO.	BY CH. APPR.
डिजाइन मेमो संख्या	डिजाइन संख्या
DATE	DRG. NO.
MAR 2025	NHDB 2GC4 41 DD 1012 00
डिजाइन संख्या	डिजाइन संख्या