



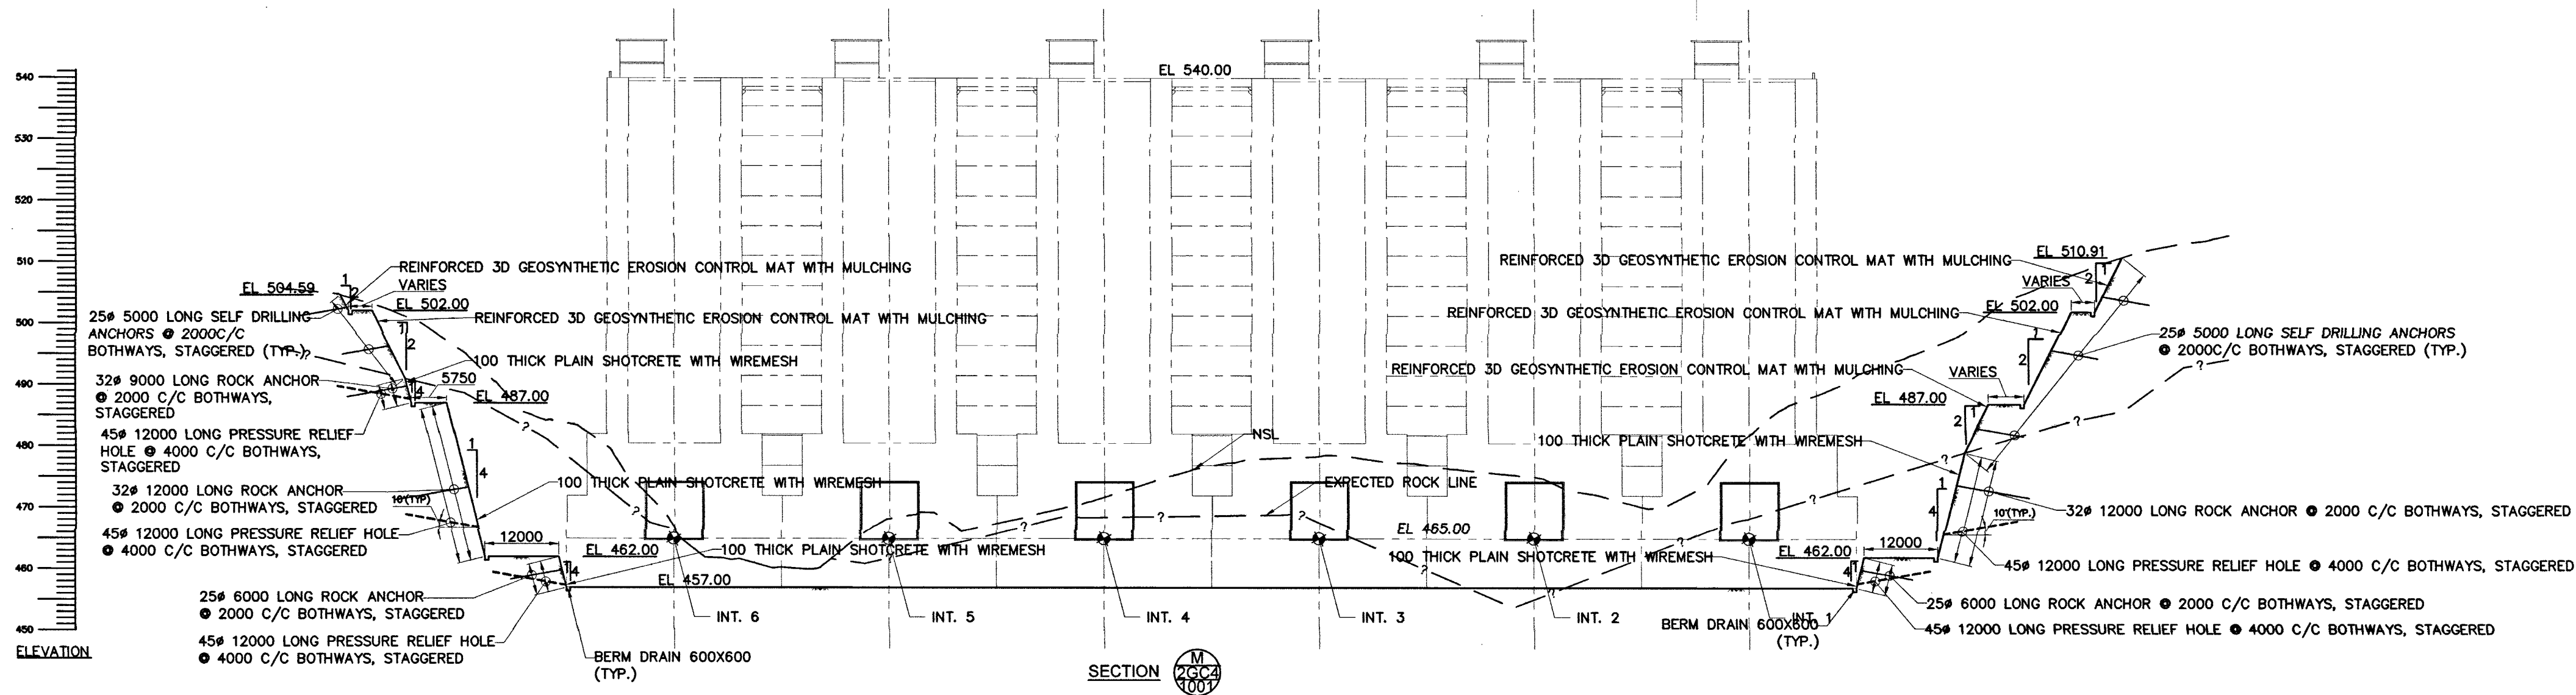

NOTES:

1. सभी माप मिलीमीटर में तथा ऊंचाई मीटर में दिए गए हैं।
ALL DIMENSIONS ARE IN MILLIMETRES AND ELEVATIONS IN METRES.
2. FOR OTHER NOTES REFER DRAWING NO. NHDB-2GC4-41-DD-1001 & 1002.
3. THIS DRAWING SHALL BE READ IN CONJUNCTION WITH DRAWING NO. NHDB-2GC4-41-DD-1001 TO 1012.

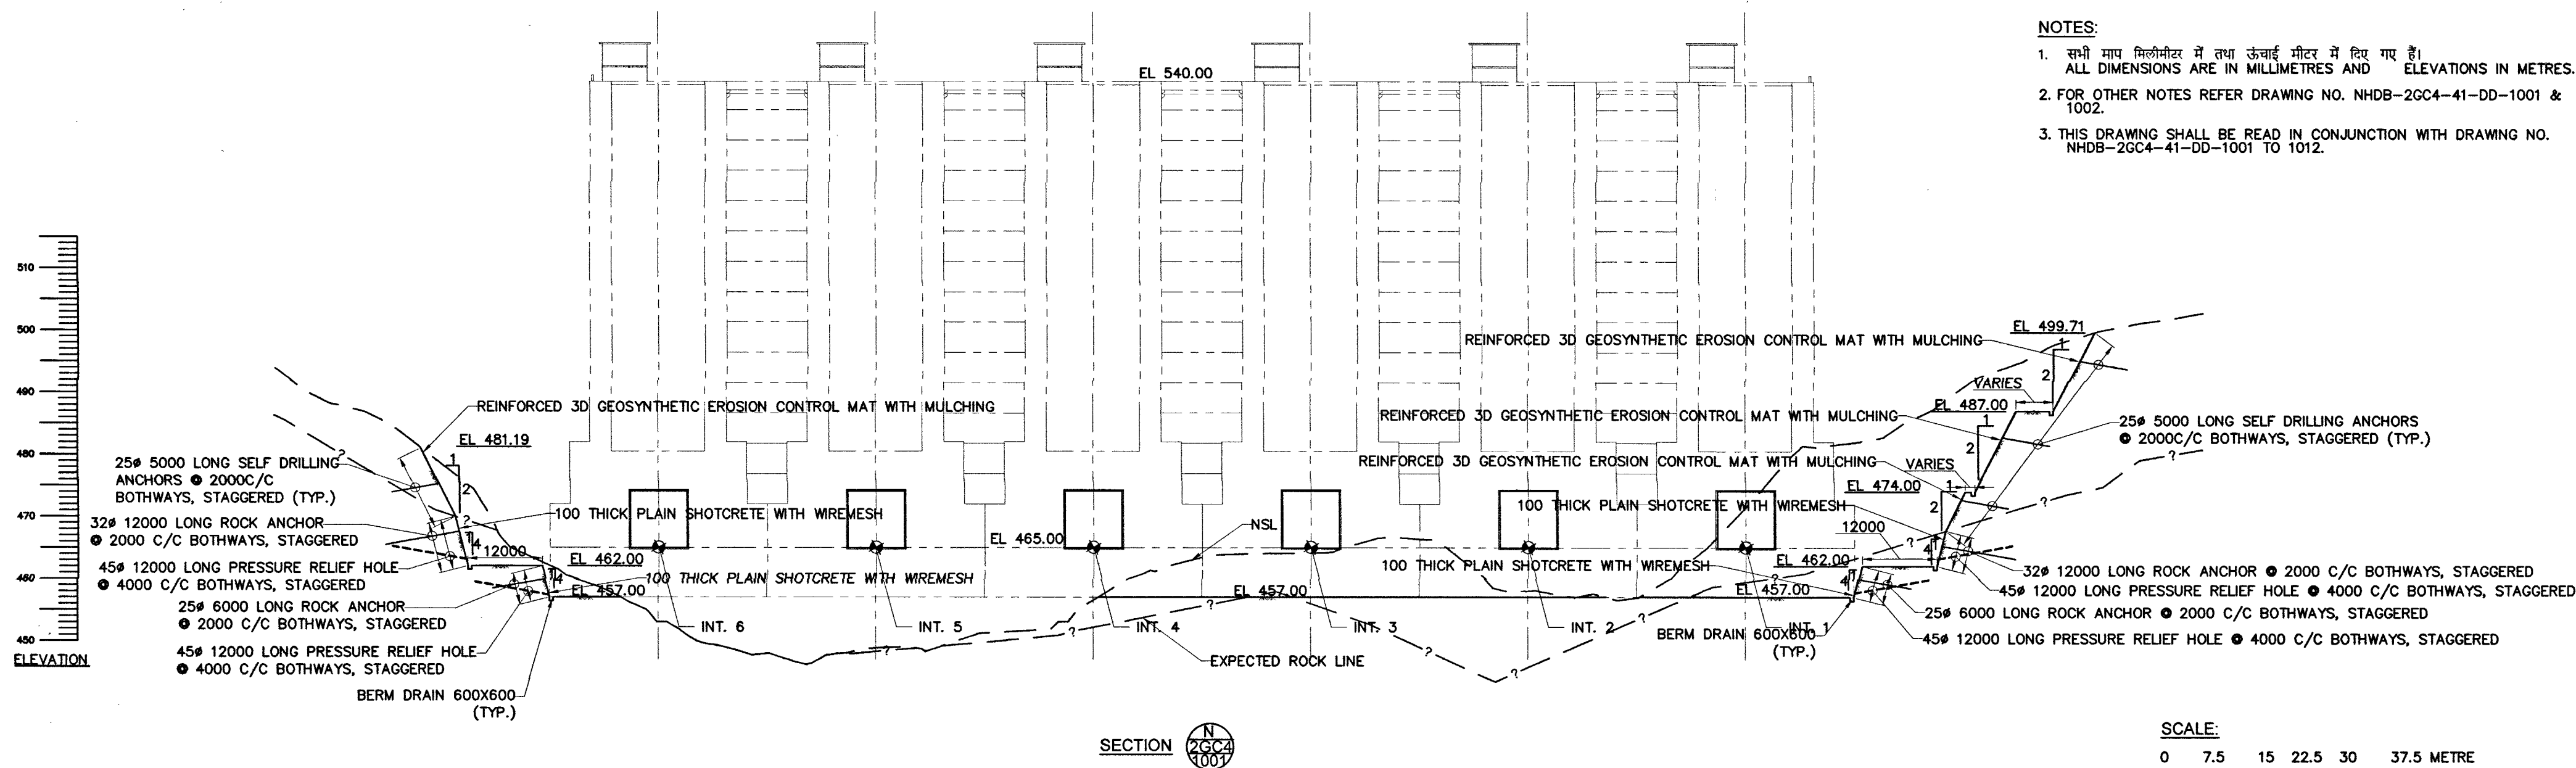

SCALE:

0 7.5 15 22.5 30 37.5 METRE

	एन एच पी सी लिमिटेड (भारत सरकार का एक निर्यात अंगण) NHPC Limited (A GOVT. OF INDIA NATIVATA ENTERPRISE)						
दिबांग बहुउद्देशीय परियोजना DIBANG MULTIPURPOSE PROJECT							
POWER INTAKE EXCAVATION AND ROCK SUPPORT SECTIONS							
SHEET 13 OF 13							
DRAWN अंकित	SUBMITTED उत्सुग	RECOMMENDED अनुमोदित	APPROVED अनुमोदन	अधिकारी अधिकारी			
DATE दिनांक	MAR 2025	DRG. NO. ड्रॉग नंबरा	NHDB	2GC4 41	DD	1013	00