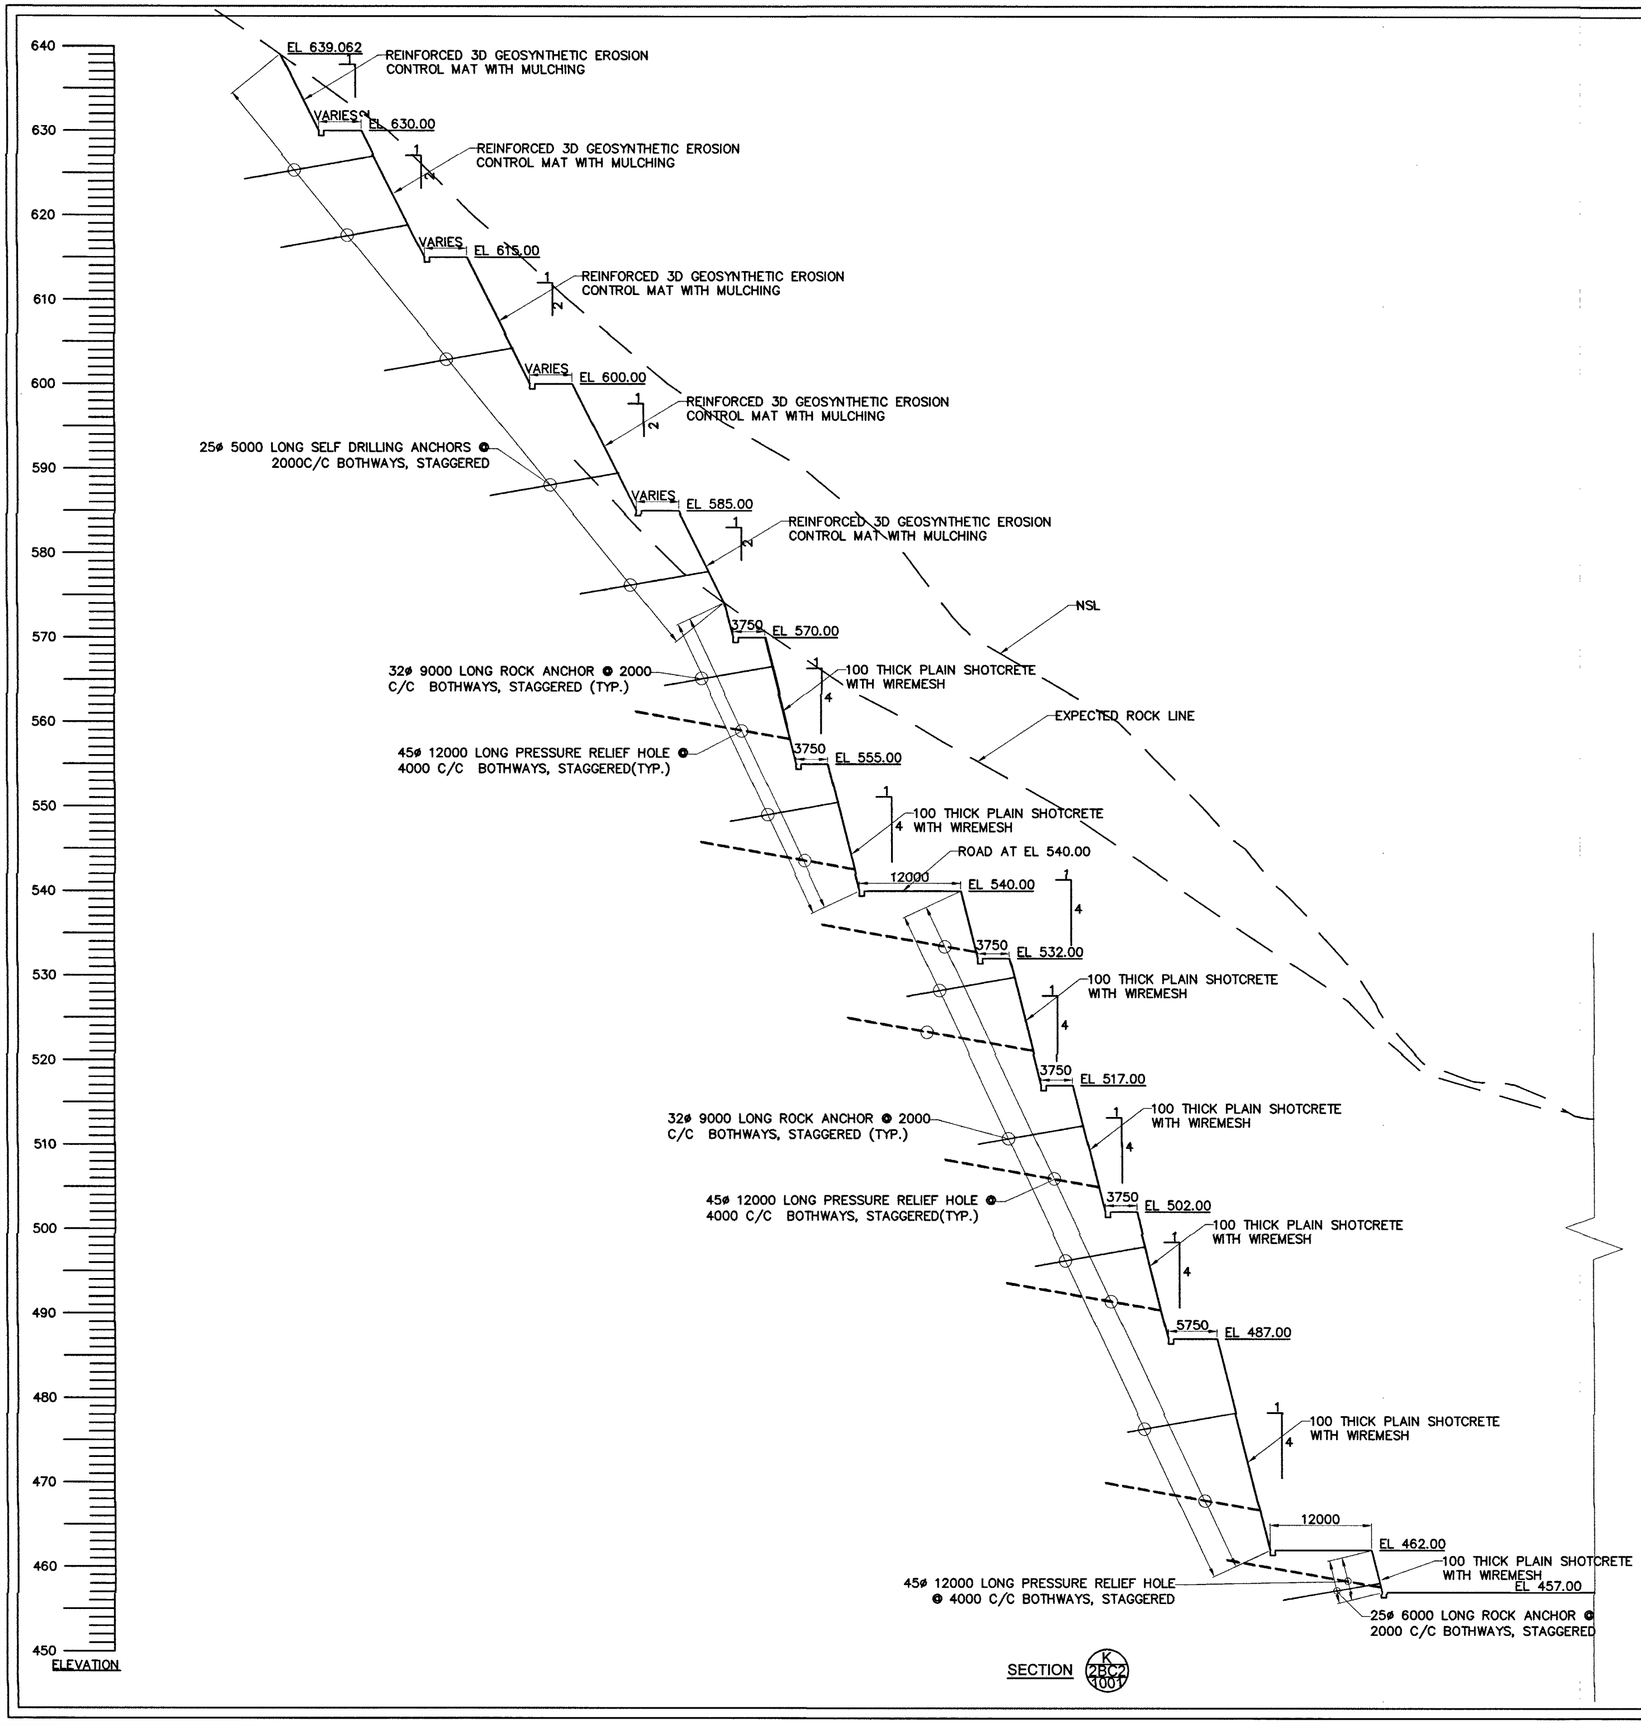


SECTION K 2BC2 1001

NOTES:

1. सभी माप मिलीमीटर में तथा ऊंचाई मीटर में दिए गए हैं।
 ALL DIMENSIONS ARE IN MILLIMETRES AND ELEVATIONS IN METRES.
2. FOR OTHER NOTES REFER DRAWING NO. NHDB–2GC4–41–DD–1001 & 1002
3. THIS DRAWING SHALL BE READ IN CONJUNCTION WITH DRAWING NO. NHDB–2GC4–41–DD–1001 TO 1010 & 1012, 1013.

SCALE:

0 5000 5 10 15 20 25 METRE

एन एच पी सी लिमिटेड
(भारत सरकार का एक नवरत्न उद्यम)
NHPC Limited
(A GOVT. OF INDIA NAVRATNA ENTERPRISE)

दिबांग बहुउद्देशीय परियोजना
DIBANG MULTIPURPOSE PROJECT

POWER INTAKE
EXCAVATION AND ROCK SUPPORT
SECTIONS

SHEET 11 OF 13

DATE	NO.	REVISION OR ISSUES	BY	CH	APP
07.03.25					

DESIGN MEMO NO. डिजाइन मेमो संख्या

DRAWN अंकित	SUBMITTED प्रस्तुत	RECOMMENDED अनुशंसित	APPROVED अनुमोदित
ASHISHEK YADAV	ASHISH RAO	SAURABH SINGH	S CHAUDHARY

DATE दिनांक	DRG. NO. ड्रेग संख्या					
MAR 2025	NHDB	2GC4	41	DD	1011	00

DRG. NO. NHDB-2GC4-41-DD-1011-00