




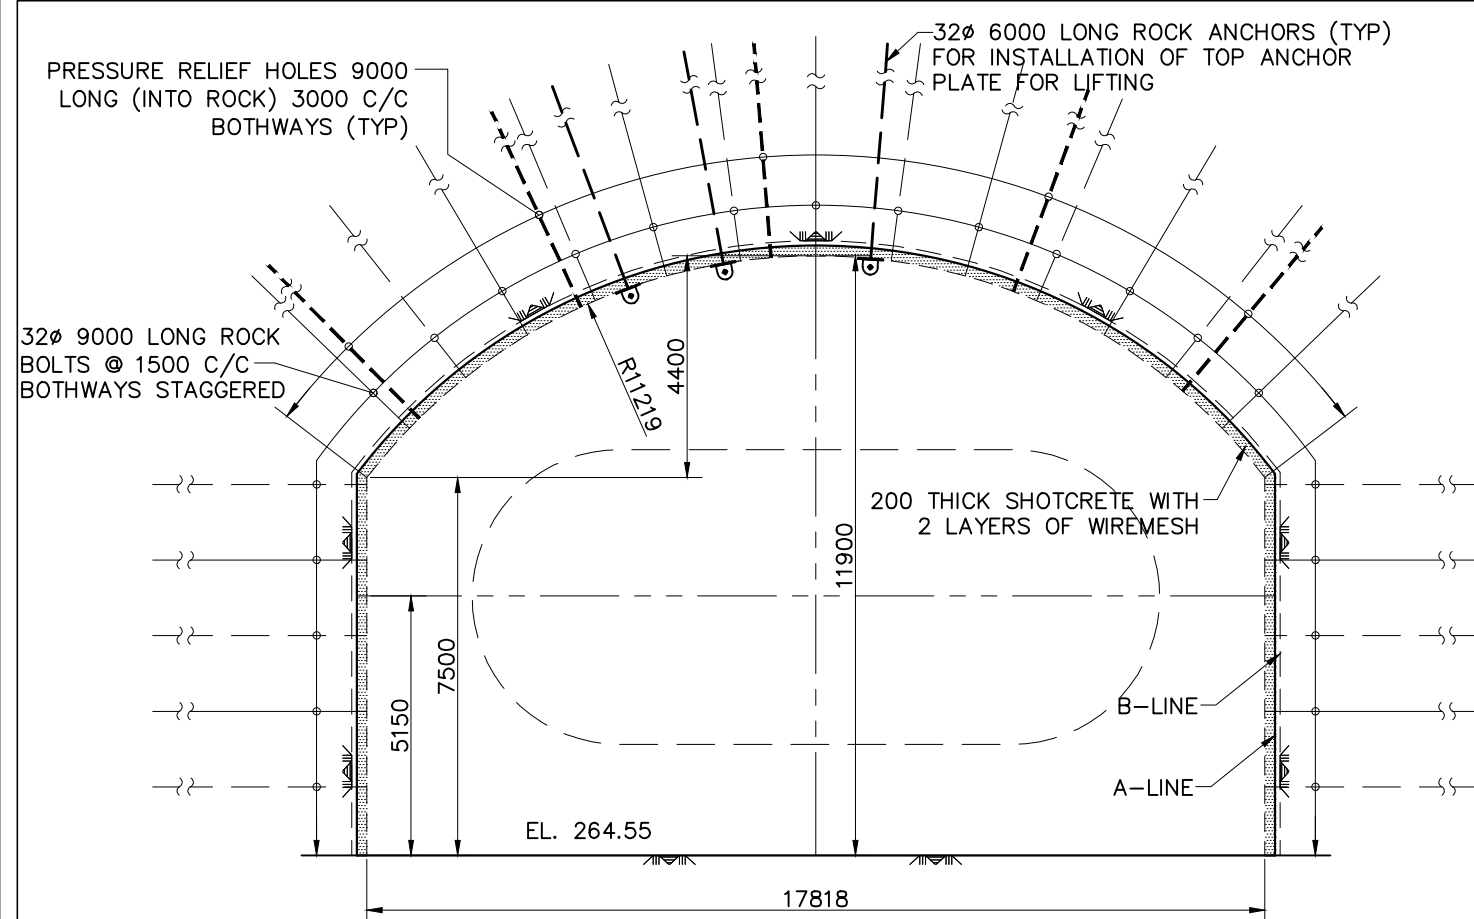


SECTION 

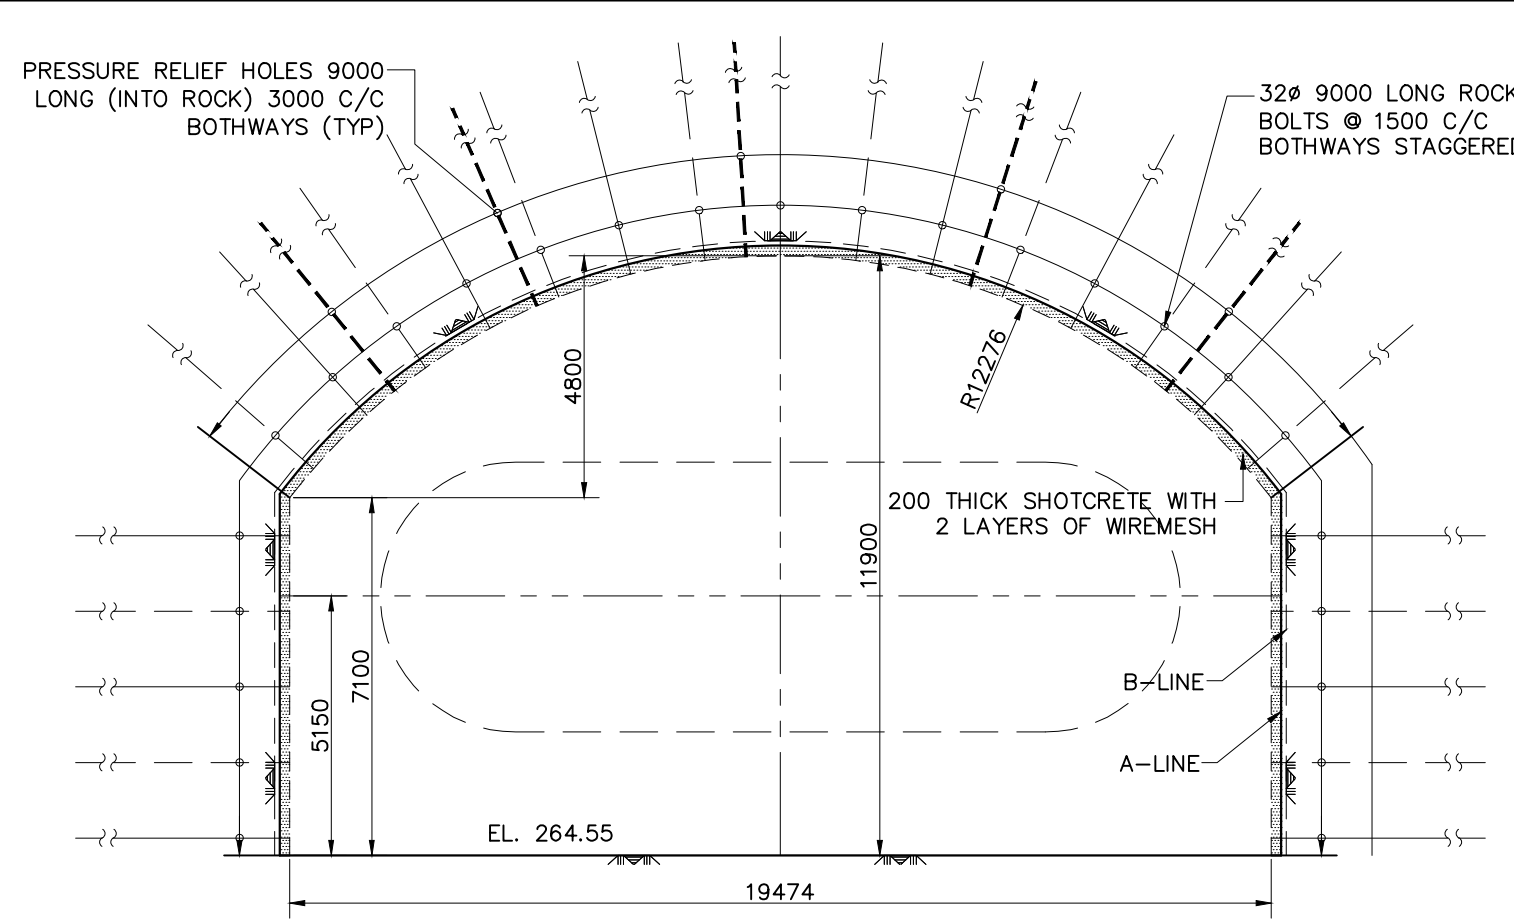


SECTION 

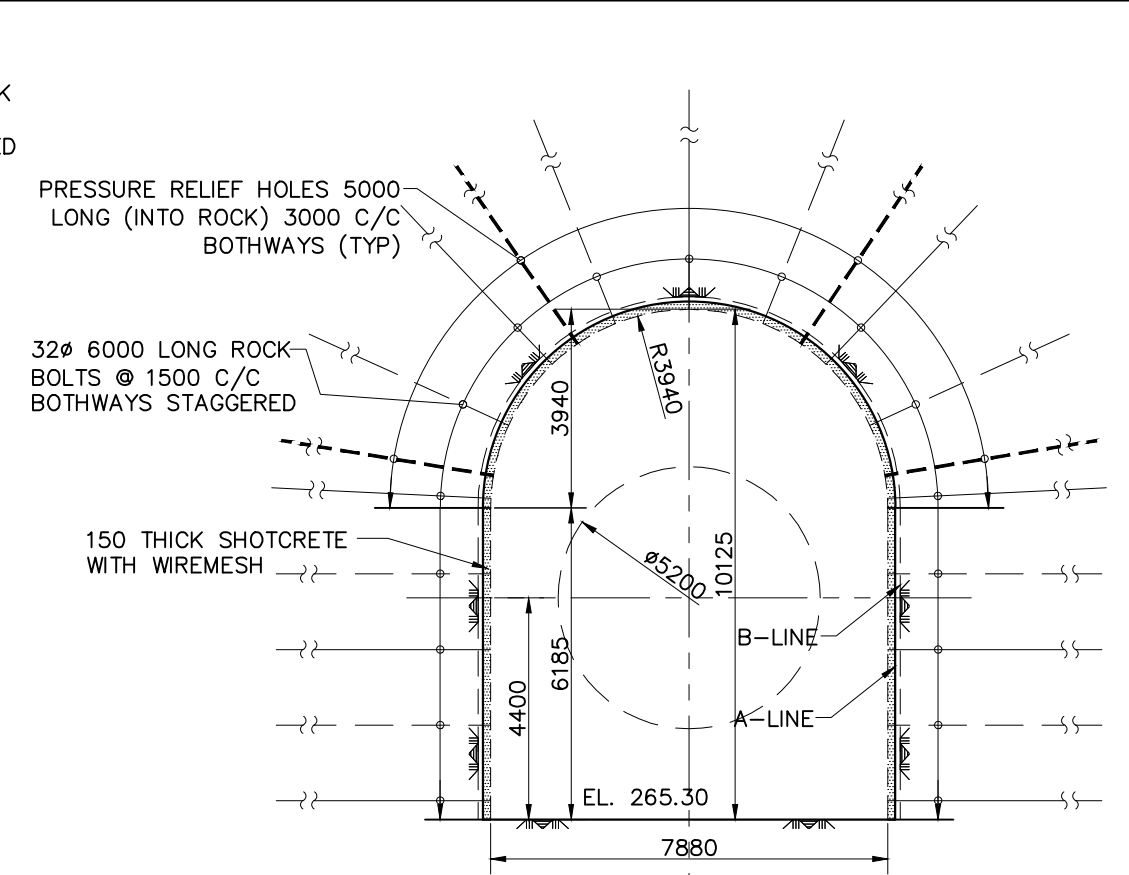


SECTION 

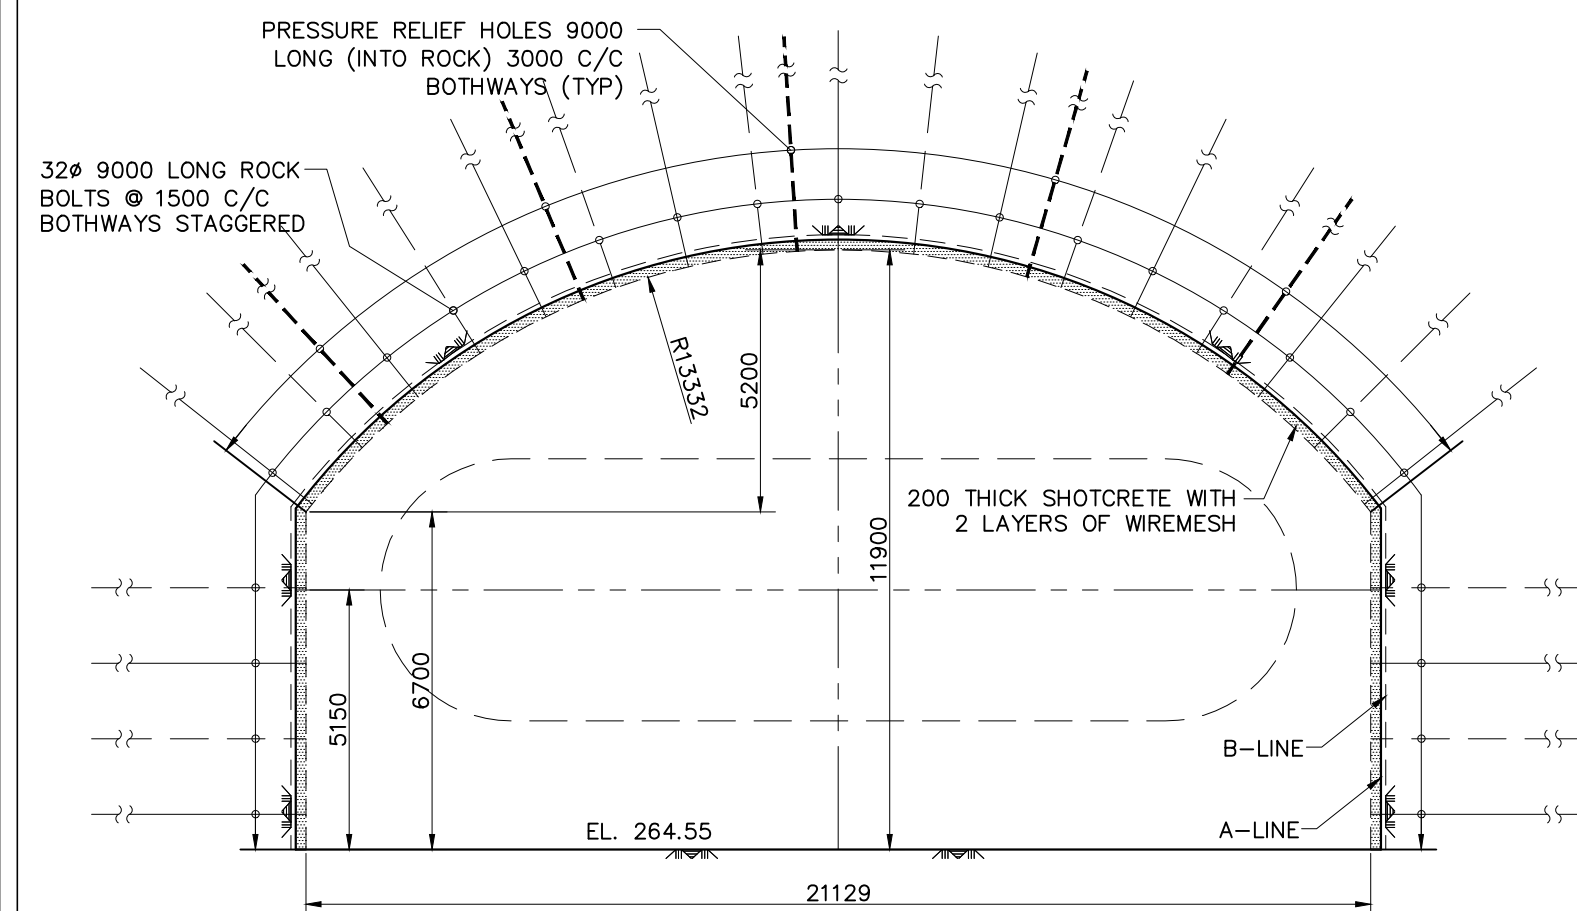


SECTION 

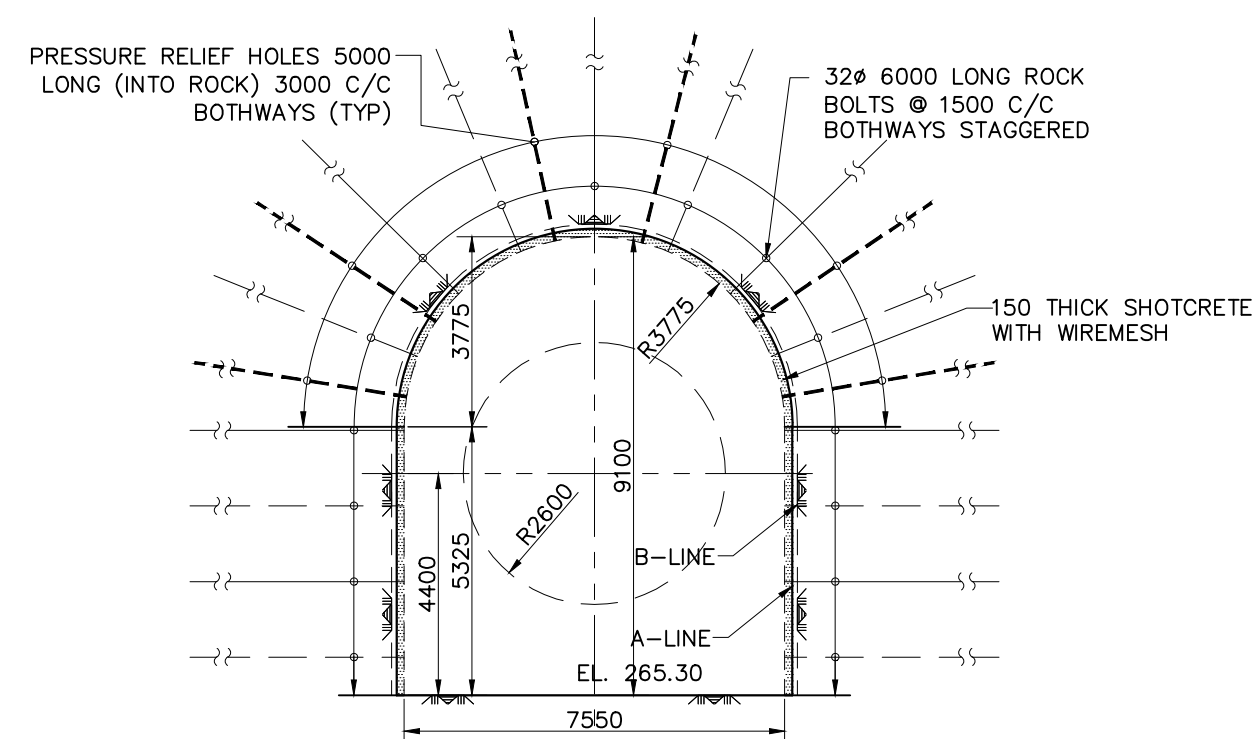


SECTION 

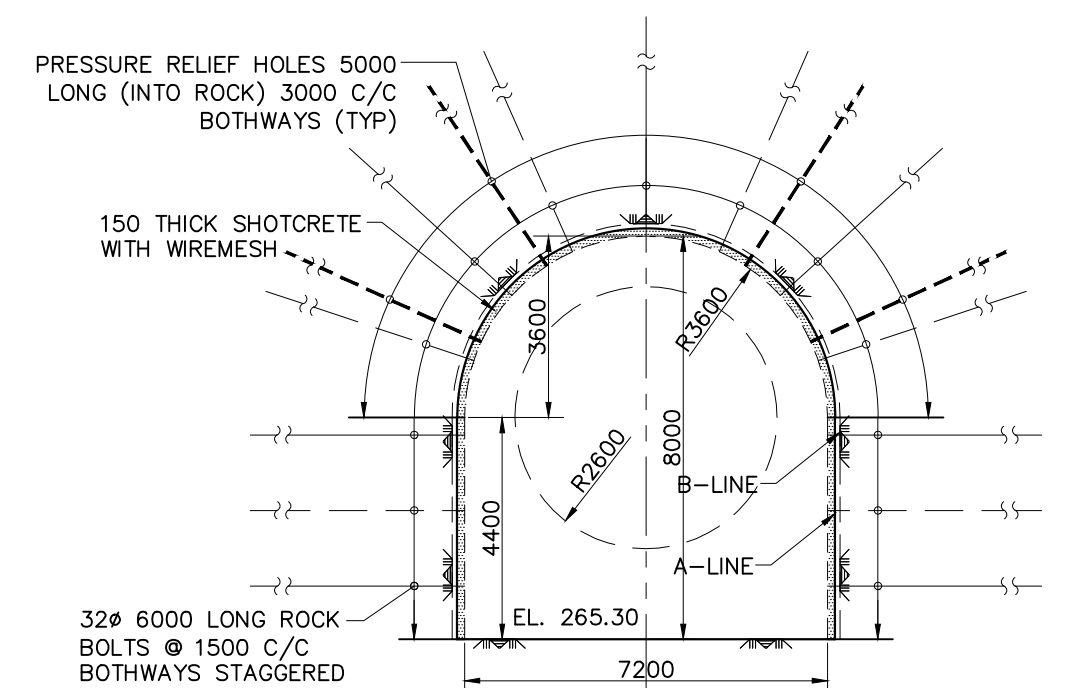

SECTION 

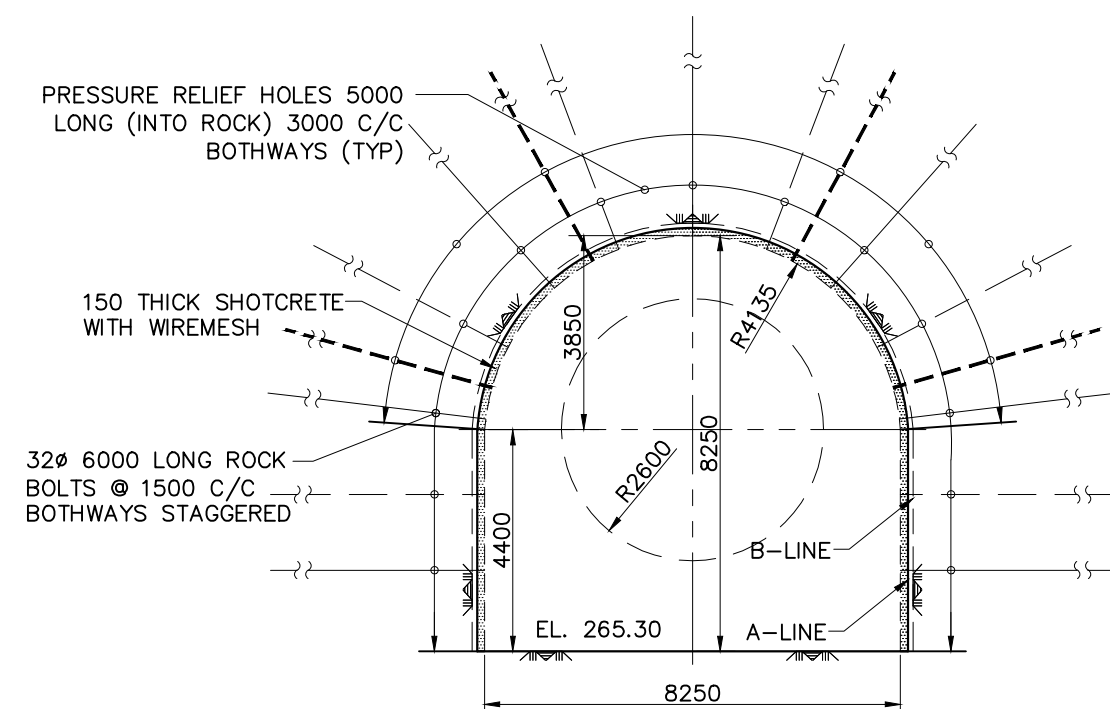

SECTION 

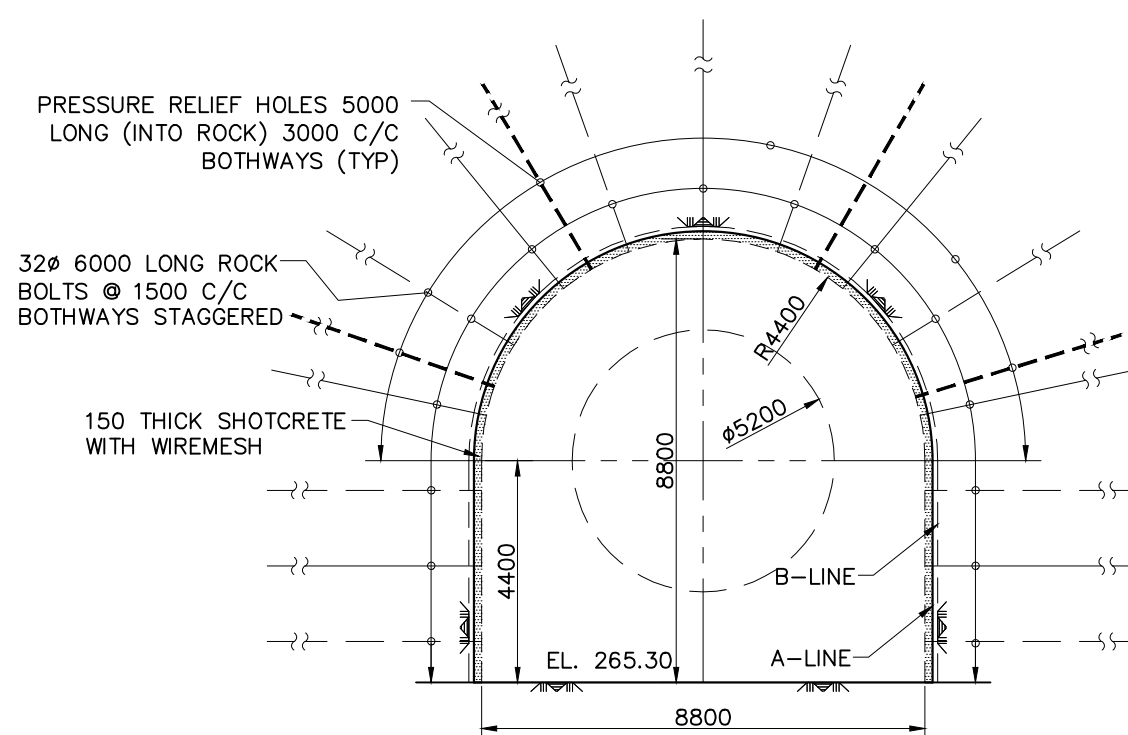

SECTION 

NOTES:-

1. सभी माप मिलीमीटर में तथा ऊंचाई मीटर में दिए गए हैं।
ALL DIMENSIONS ARE IN MILLIMETERS AND LEVELS IN METERS.
2. FOR OTHER NOTES REFER DRAWING NO.
NHDB-3KC4-41-DD-1006.
3. THIS DRAWING SHALL BE READ IN CONJUNCTION
WITH DRAWING NO. NHDB-3KC4-41-DD-1006 &
1007.
4. THIS DRAWING SUPERCEDES DRAWING NO.
NHDB-3KC4-41-DD-1004 & 1005

SCALE:

0 1.5 3.0 4.5 6.0 7.5 METRE



एन.एच.पी.सी.
NHPC
A Navratna Company

एन एच पी सी लिमिटेड
(भारत सरकार का उद्यम)
NHPC Limited
(A GOVT. OF INDIA ENTERPRISE)

दिवंग बहुउद्देशीय परियोजना
DIBANG MULTIPURPOSE PROJECT

PRESSURE SHAFT
 LOWER HORIZONTAL PRESSURE SHAFT AND PENSTOCK
 EXCAVATION AND ROCK SUPPORT DETAILS
 SECTIONS

(SHEET 3 OF 3)

20.02.2026		00	ISSUED FOR CONSTRUCTION				(SHEET 3 OF 3)						
DATE	NO.	REVISION OR ISSUES		BY	CH	APP	DRAWN अर्पित	SUBMITTED DC DWIVEDI	APPROVED प्रमोद ASHISH RAO	RECOMMENDED अशोक SURAISH SINGH		APPROVED अशोक SURAISH SINGH	
DESIGN MEMO NO. विज्ञापन मेमो संख्या						DATE दिनांक	FEB 2026	DRG. NO. ड्रॉग संख्या	NHDB	3KC4	41	DD 1008	00