
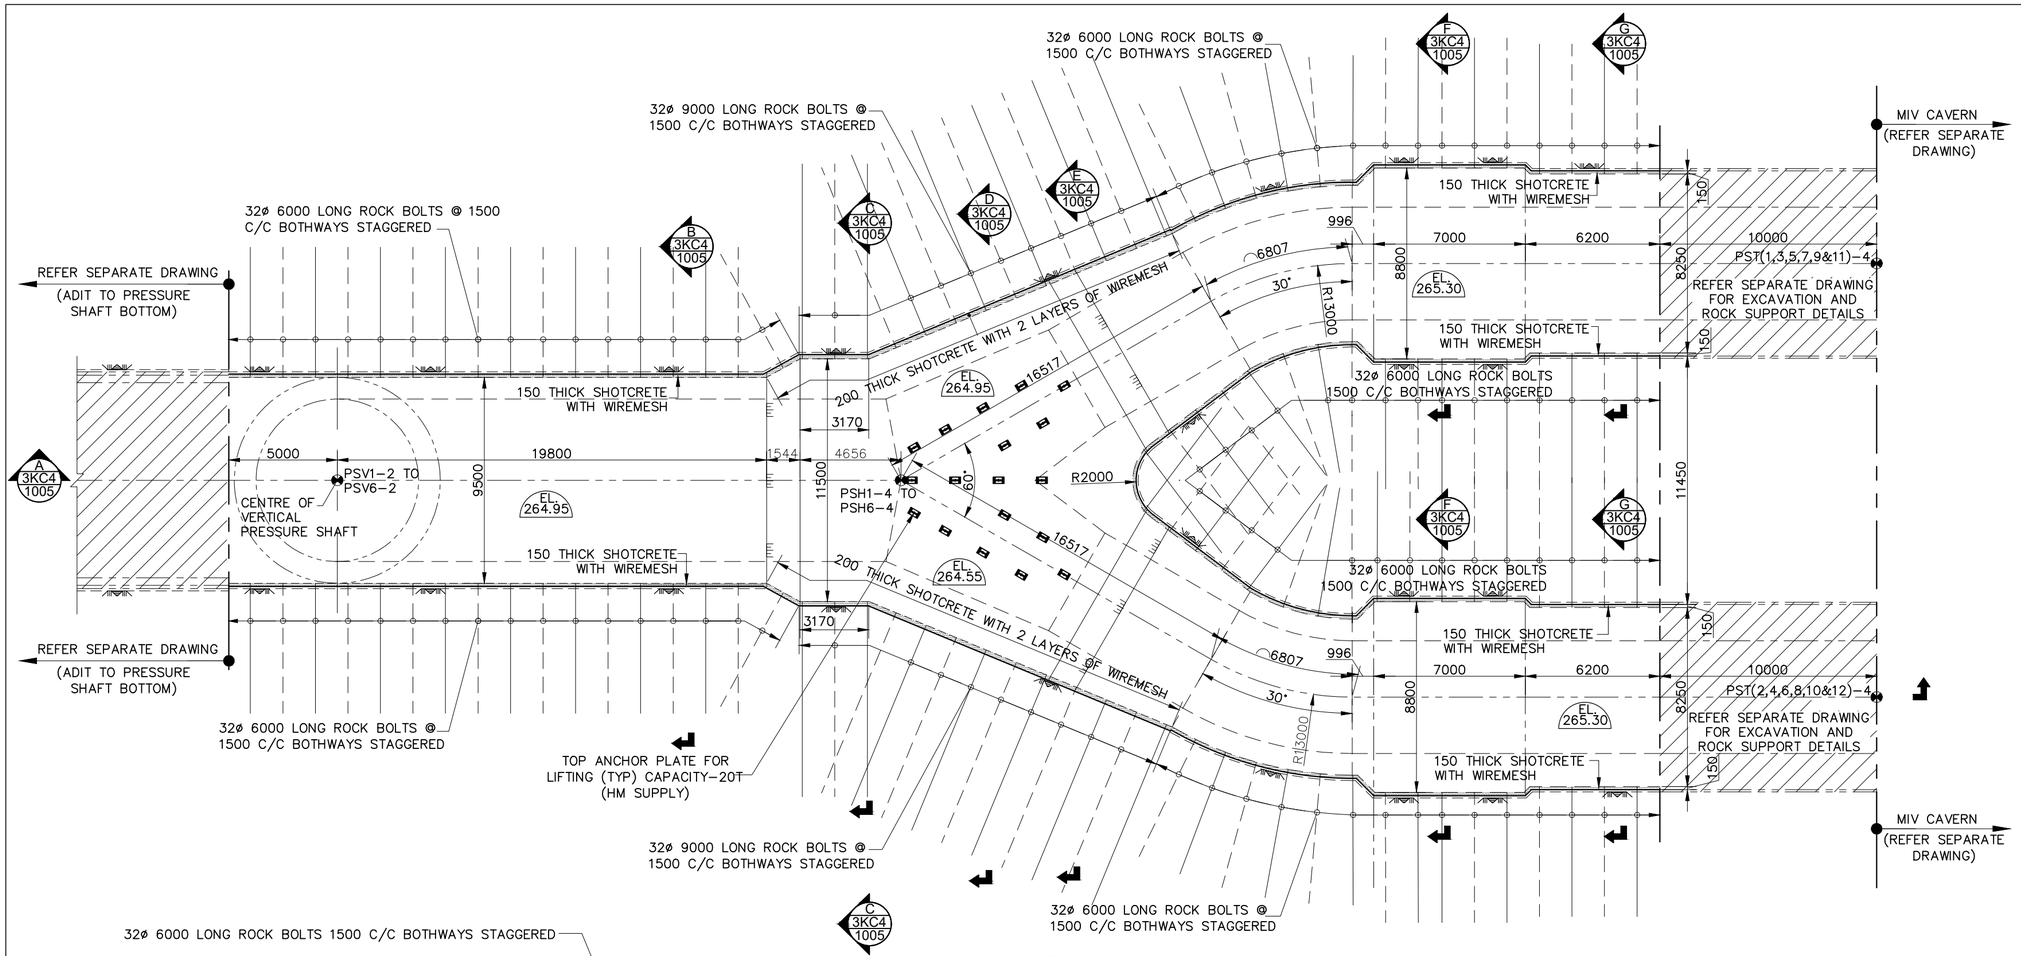


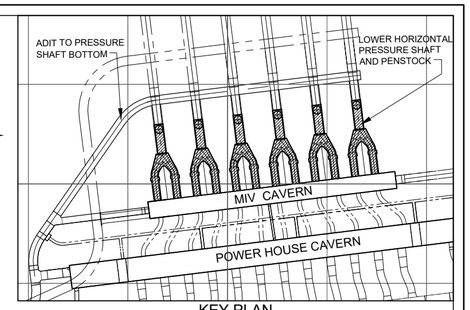

KEY PLAN
(NTS)

NOTES:-

1. सभी माप मिलीमीटर में तथा ऊंचाई मीटर में दिए गए हैं। ALL DIMENSIONS ARE IN MILLIMETERS AND LEVELS IN METERS.
2. THE DEFINITION OF 'A' & 'B' LINE AND VARIOUS CLASSES OF EXCAVATION SHOWN SHALL BE AS PER SECTION B.3 OF TECHNICAL SPECIFICATION.
3. MINOR MODIFICATION IN THE LENGTH, ORIENTATION, PATTERN AND LOCATION OF ROCK ANCHORS MAY BE DONE TO SUIT THE SITE CONDITIONS WITH THE APPROVAL OF ENGINEER-IN-CHARGE.
4. ROCK ANCHORS/BOLTS SHOWN IN THE DRAWING SHALL BE CONFORMING TO SECTION B.4 OF TECHNICAL SPECIFICATION.
5. THE REQUIREMENT FOR 45 MM DIAMETER PRESSURE RELIEF HOLES WITH 36 MM DIAMETER PERFORATED PVC PIPES, AS SHOWN IN THE DRAWING, MAY BE MODIFIED BY THE ENGINEER-IN-CHARGE TO SUIT THE SITE CONDITIONS. THE PRESSURE-RELIEF HOLES SHALL BE PROVIDED IN ACCORDANCE WITH SECTION B.7 OF THE TECHNICAL SPECIFICATION. FURTHER, THE PVC PIPES USED FOR THE PRESSURE RELIEF HOLES SHALL BE INTERCONNECTED THROUGHOUT THE LOWER HORIZONTAL PRESSURE SHAFT AND PENSTOCK UPTO THE MIV CAVERN USING 100 MM SOLID PVC PIPES.
6. SHOTCRETE SHOWN ON DRAWING SHALL BE APPLIED AS SPECIFIED IN SECTION B.5 OF TECHNICAL SPECIFICATION. THE THICKNESS OF SHOTCRETE AND LAYERS OF WIREMESH MAY BE MODIFIED TO SUIT SITE CONDITIONS WITH THE APPROVAL OF ENGINEER-IN-CHARGE.
7. UNDERGROUND EXCAVATION INCLUDING PROTECTION OF TUNNEL INVERT SHALL BE CONFIRMING TO SECTION B.3 OF TECHNICAL SPECIFICATION.
8. IF ADDITIONAL ROCK SUPPORT MEASURES ARE REQUIRED BASED ON THE SITE SPECIFIC CONDITIONS THEN REFER DRG. NO. NHDB-4BC4-41-DD-1007 AS DIRECTED BY ENGINEER-IN-CHARGE.
9. THE EXCAVATION PROFILE SHALL CHANGE IN SECTIONS WHERE RIBS/LG ARE REQUIRED TO SUPPORT THE EXCAVATED PROFILE. SEPARATE DRAWING SHALL BE ISSUED IN THIS RESPECT.
10. THE TOP ANCHOR PLATE FOR LIFTING CAPACITY 20T AS SHOWN IN THE DRAWING SHALL BE SUPPLIED BY HM CONTRACTOR AND INSTALLED BY CIVIL CONTRACTOR USING ROCK ANCHOR. THE LOCATION SHOWN IN DRAWING ARE TENTATIVE AND MAY CHANGE AS PER SITE REQUIREMENT.
11. THIS DRAWING SHALL BE READ IN CONJUNCTION WITH DRAWING NO. NHDB-3KC4-41-DD-1005.

SCALE:
0 2 4 6 8 10 METRE

REFERENCE DRAWINGS:
NHDB-3KC4-41-DD-003 TO 008

DATE	NO.	REVISION OR ISSUES	BY	CH.	APP
06.02.2026	00	ISSUED FOR CONSTRUCTION			

DESIGN MEMO NO. डिजाइन मेमो संख्या

एन एच पी सी लिमिटेड (भारत सरकार का उद्यम)
NHPC Limited (A GOVT. OF INDIA ENTERPRISE)
A Navratna Company

दिबांग बहुउद्देशीय परियोजना
DIBANG MULTIPURPOSE PROJECT

PRESSURE SHAFT
LOWER HORIZONTAL PRESSURE SHAFT AND PENSTOCK
EXCAVATION AND ROCK SUPPORT DETAILS
TYPICAL PLAN AND SECTION
(SHEET 1 OF 2)

DRAWN अंकित	SUBMITTED प्रस्तुत	RECOMMENDED अनुशंसित		APPROVED अनुमोदन
DC DWIVEDI	ASHISH RAO	SAURABH SINGH		SANKHADIP CHOWDHURY

DATE दिनांक	DRG. NO. ड्रेग संख्या					
FEB 2026	NHDB	3KC4	41	DD	1004	00

DRG. NO. NHDB-3KC4-41-DD-1004-00