

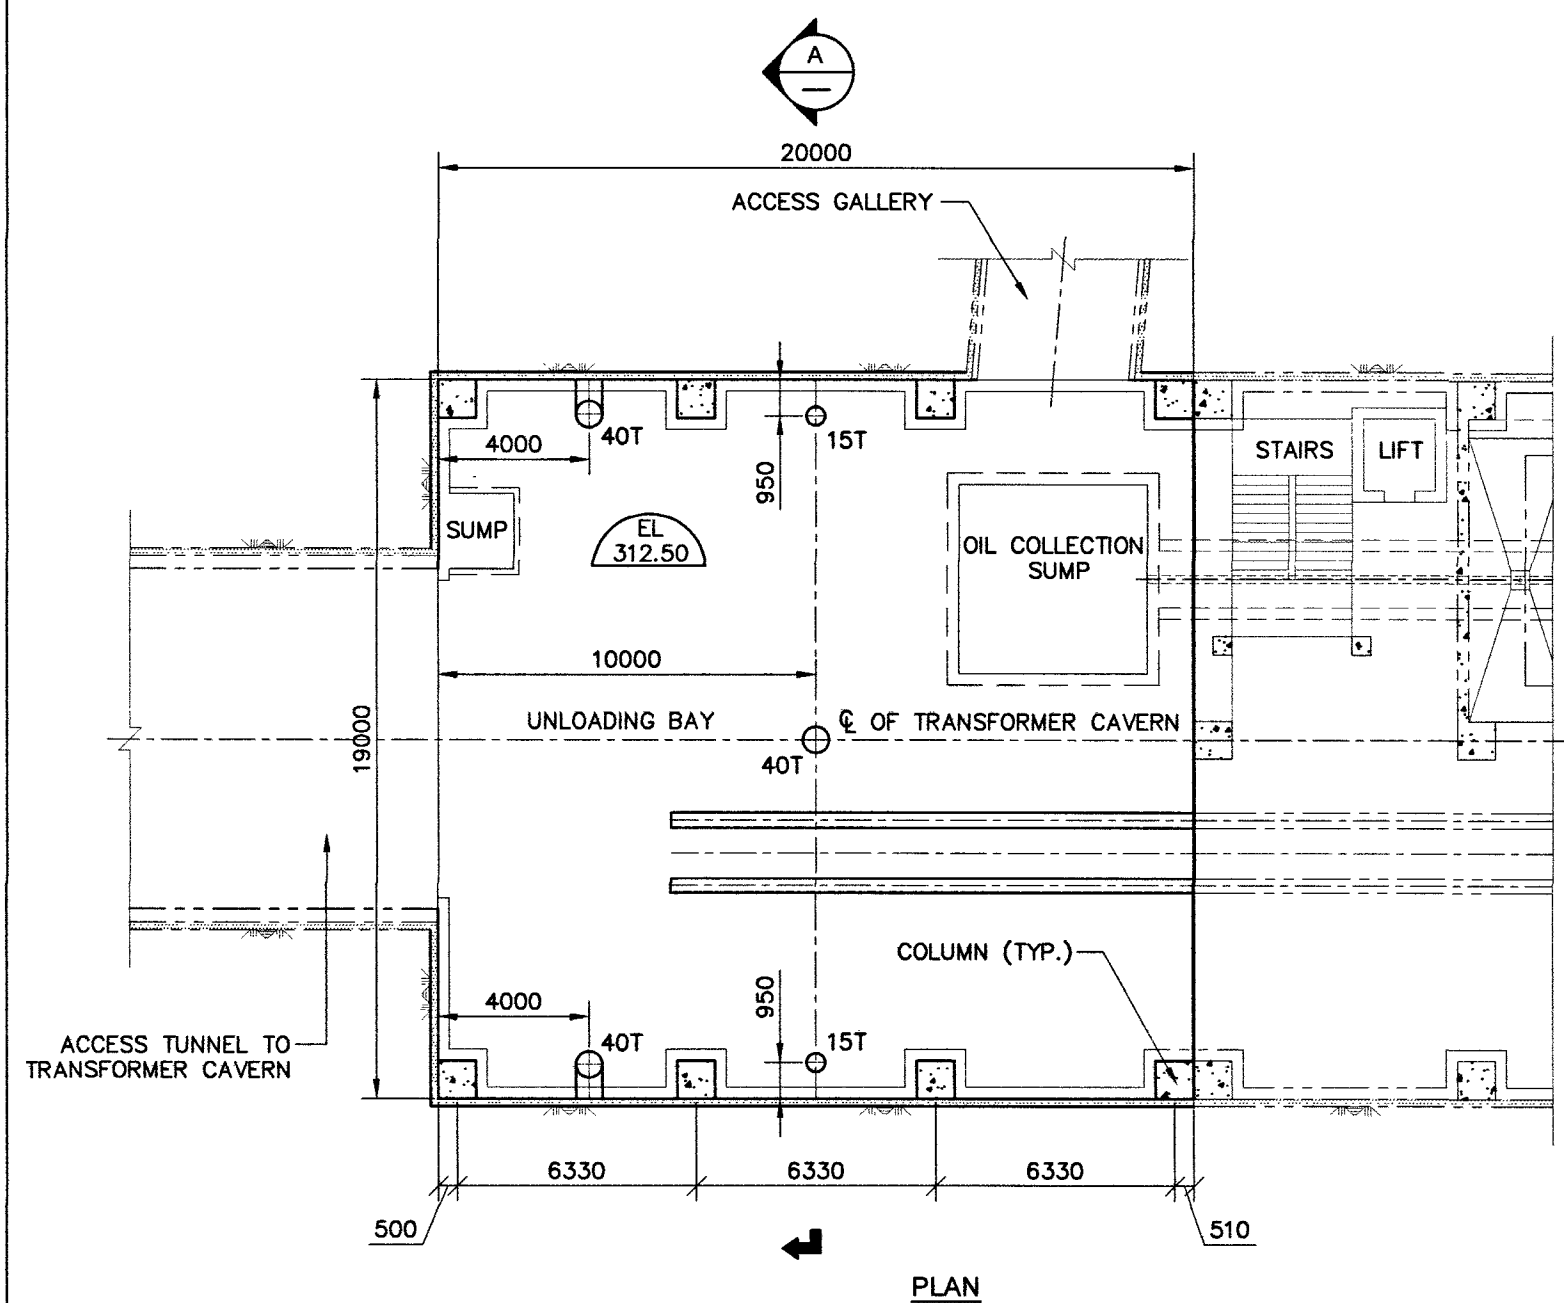
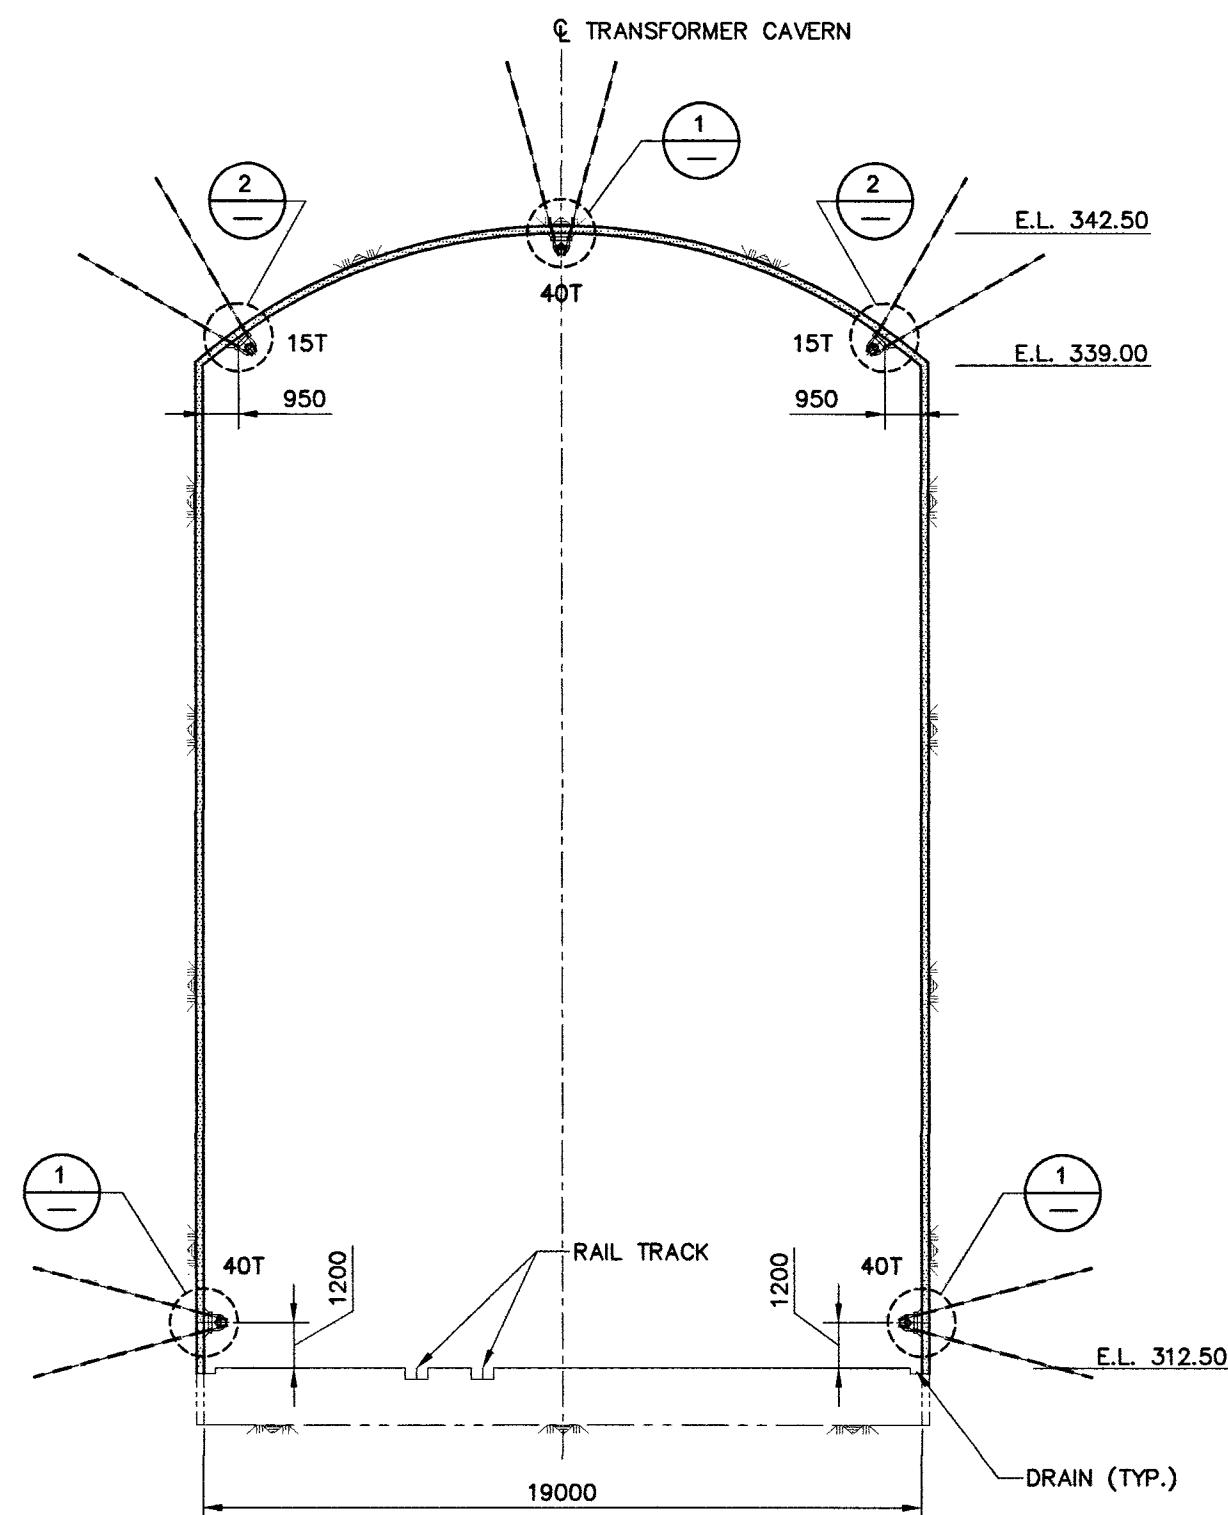


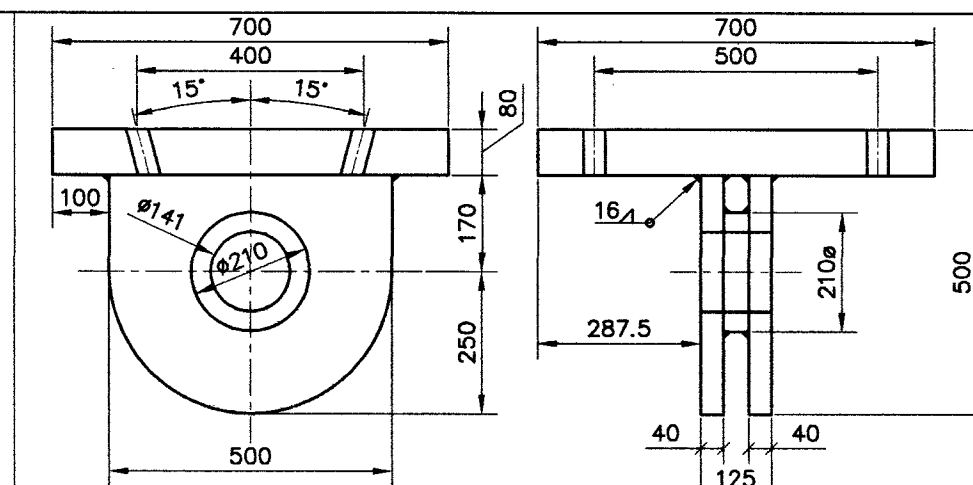


PLAN

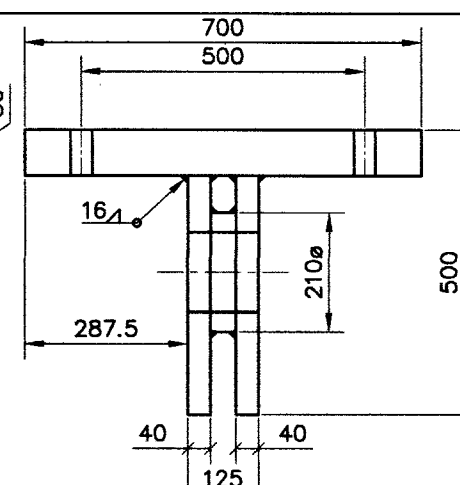

SECTION



ELEVATION

SIDE VIEW

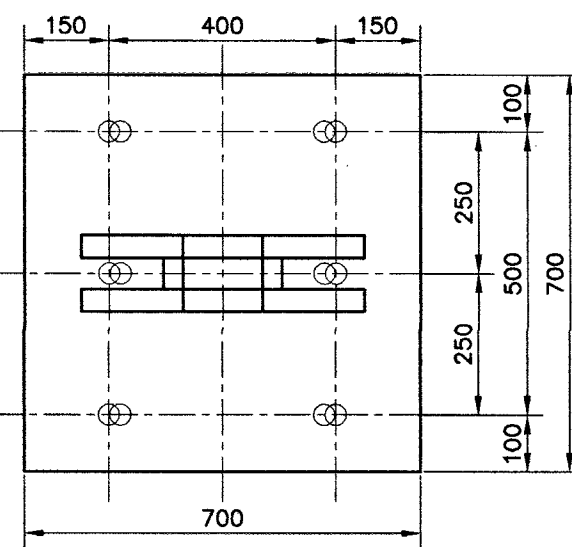


PLAN

HOOK CAPACITY - 40T (QTY-3NOS.)
(NTS)

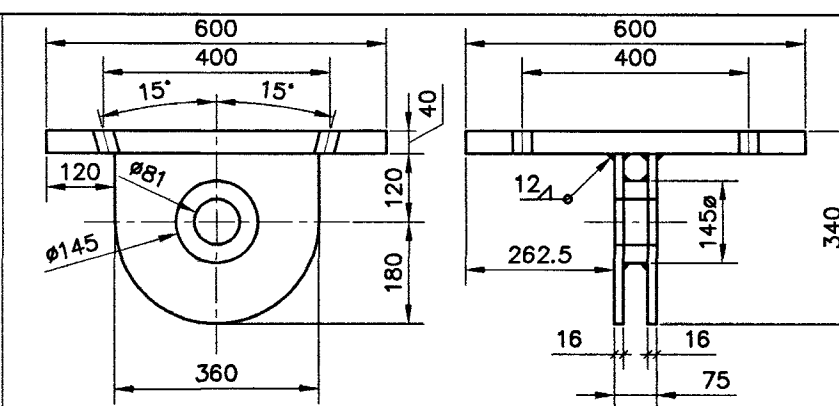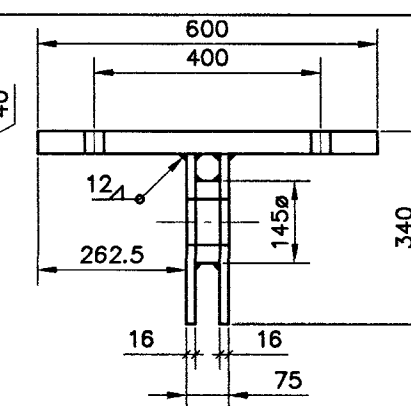
ELEVATION

SIDE VIEW

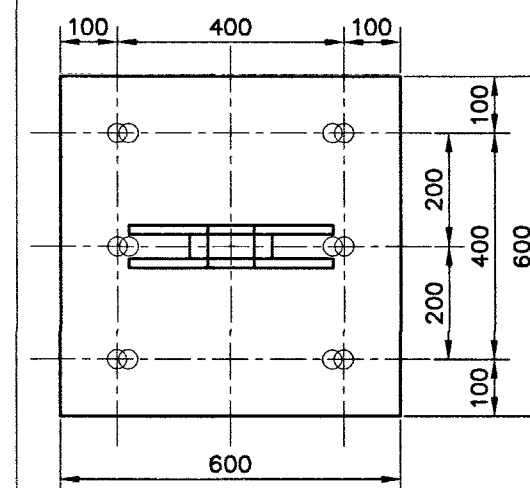


PLAN


HOOK CAPACITY - 15T (QTY-2NOS.)
(NTS)

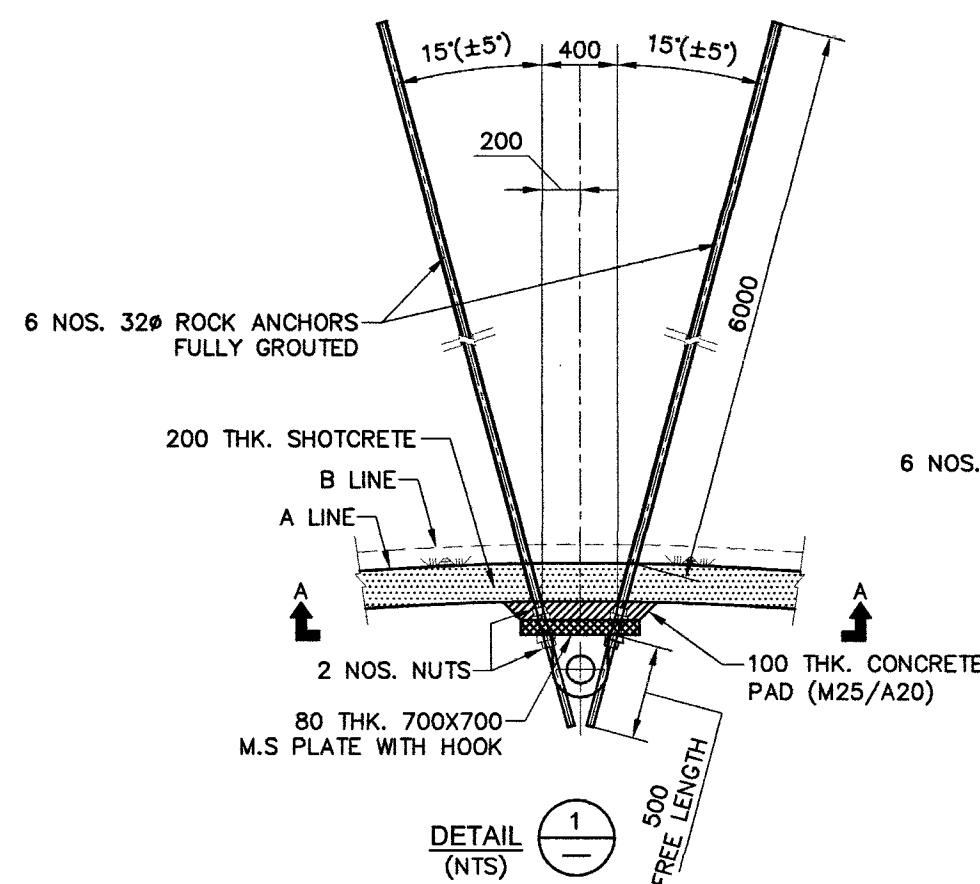


DETAIL (NTS) 

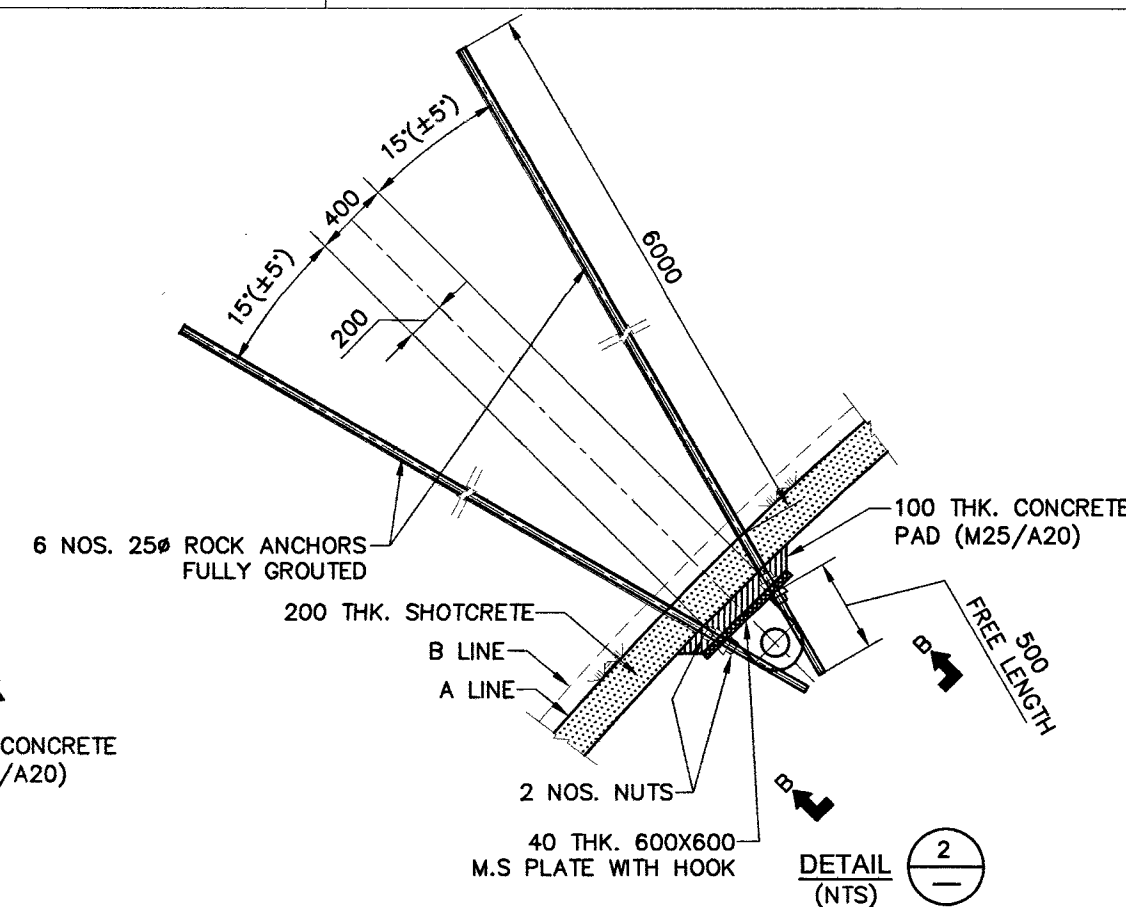

DETAIL (NTS) 

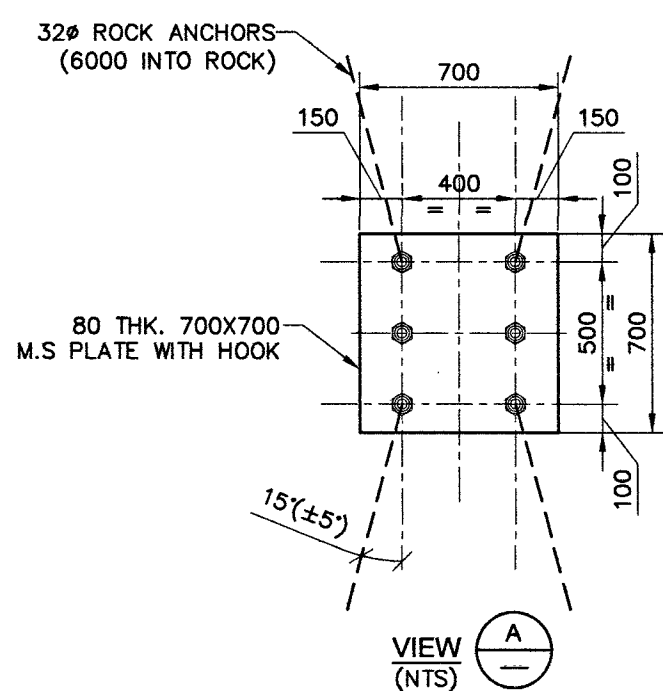

VIEW
(NTS) 

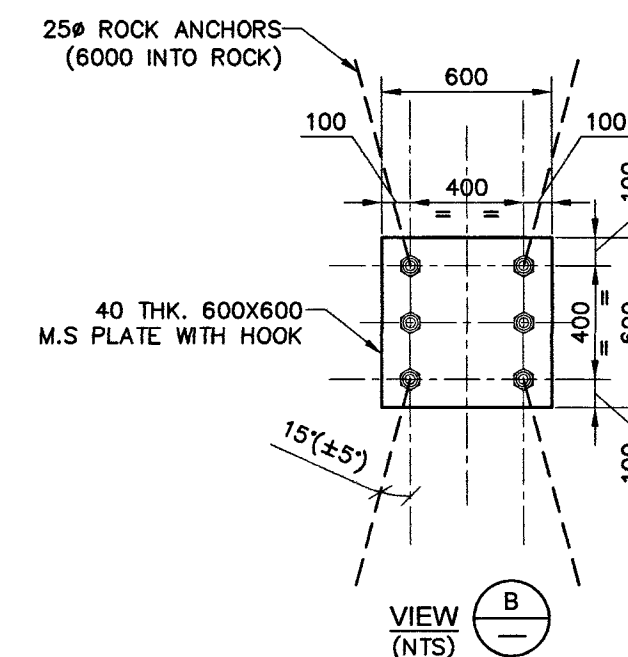

VIEW
(NTS) 

NOTES: –

1. सभी माप मिलीमीटर में तथा ऊंचाई मीटर में दिए गए हैं।
ALL DIMENSIONS ARE IN MILLIMETERS AND LEVELS IN METERS.
2. THIS DRAWING HAS BEEN DEVELOPED BASED UPON E&M DRG. NO.-PE-DC-507-501-A001C.
3. ROCK ANCHORS, THEIR INSTALLATION, TENSIONING AND TESTING SHALL CONFORM TO SECTION B.4 OF TECHNICAL SPECIFICATION.
4. THE ROCK ANCHORS SHALL BE OF HIGH YIELD STRENGTH STEEL CONFORMING TO IS:1786. THE ANCHORAGE FOR THE FULLY GROUTED ROCK ANCHORS SHALL BE OF RESIN TYPE.
5. EACH ROCK ANCHORS SHALL BE PROVIDED WITH AT LEAST 2 NOS. NUTS AND MINIMUM FREE LENGTH OF 500MM WITH THREADING.
6. IF NECESSARY THE FREE LENGTH OF ROCK ANCHORS SHALL BE CUT OR BENT FOR PROPER PLACING OF ERECTION HOOK PLATE ASSEMBLY.
7. THE EFFECTIVENESS OF EACH 32 ϕ ANCHORS & 25 ϕ ANCHORS SHALL BE CHECKED FOR A LOAD OF 12T & 5T RESPECTIVELY BY CARRYING OUT PULL OUT TESTS BEFORE INSTALLING ERECTION HOOKS ASSEMBLY AND SUBJECTING IT TO THE FINAL LOADING.
8. THE CONCRETING SHALL BE DONE AS PER SECTION B.9 OF TECHNICAL SPECIFICATIONS.
9. DESIGN OF ERECTION HOOK IS IN E&M SCOPE. SUPPLY, FABRICATION & INSTALLATION OF ALL ERECTION HOOKS TO BE DONE BY CIVIL CONTRACTOR IN CLOSE COORDINATION WITH E&M CONTRACTOR.

REFERENCE DRAWINGS:-

1. NHDB-4GC4-41-DD-1003.
2. NHDB-4GC4-41-DD-1005 & 1006.
3. E&M DRG. NO.-PE-DC-507-501-A001C.

SCALE:

0 2.0 4.0 6.0 8.0 10.0 METRE

एन एच पी सी लिमिटेड (भारत सरकार का उद्यम) NHPC Limited (A GOVT. OF INDIA ENTERPRISE)							
दिवंग बहुउद्देशीय परियोजना DIBANG MULTIPURPOSE PROJECT							
TRANSFORMER CAVERN UNLOADING BAY ERECTION HOOKS FOR EOT CRANE ANCHORAGE DETAILS							
DRAWN  डीपक	SUBMITTED  प्रभुत प्रभात अस्वाल	RECOMMENDED  रश्मि रक्षक कुमार	DESIGNED  डिजाइनर	APPROVED  अनुमोदित			
DATE OCT 2025	DRG. NO. उद्देश संख्या	NHDB	4GC4	41	DD	1008	00