

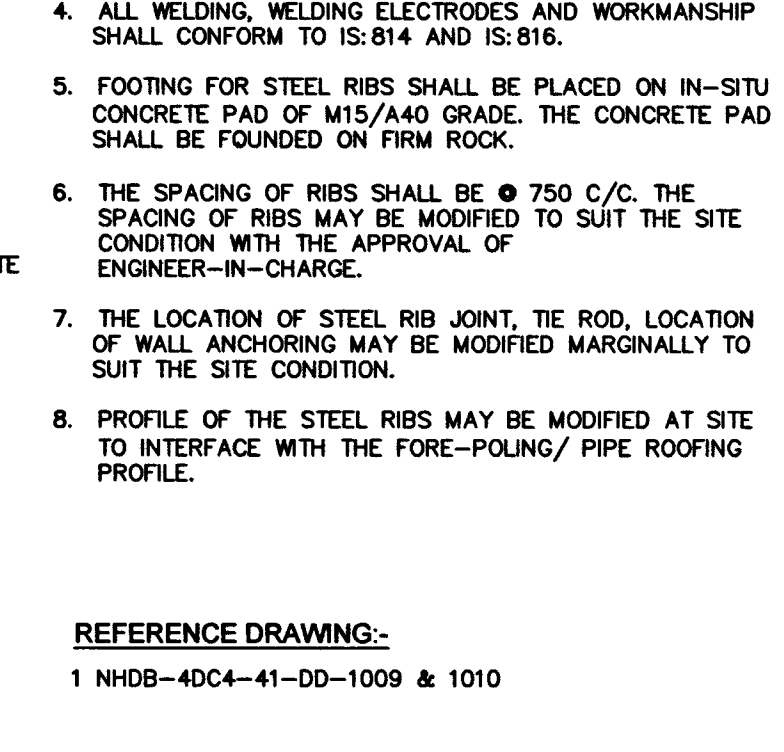
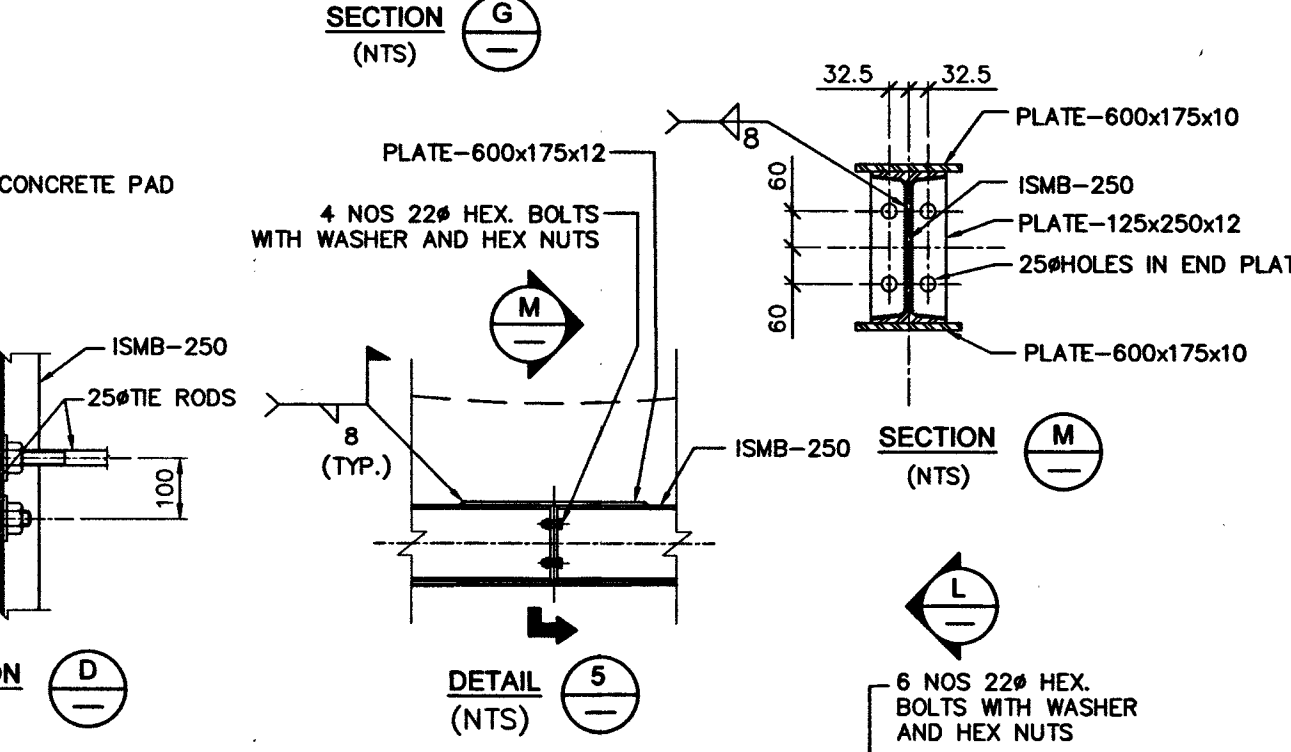
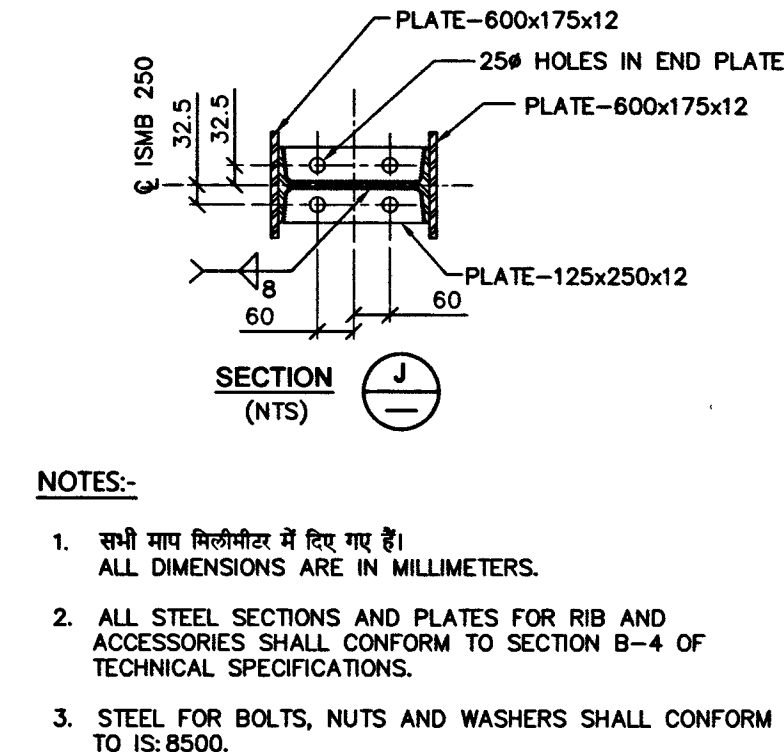
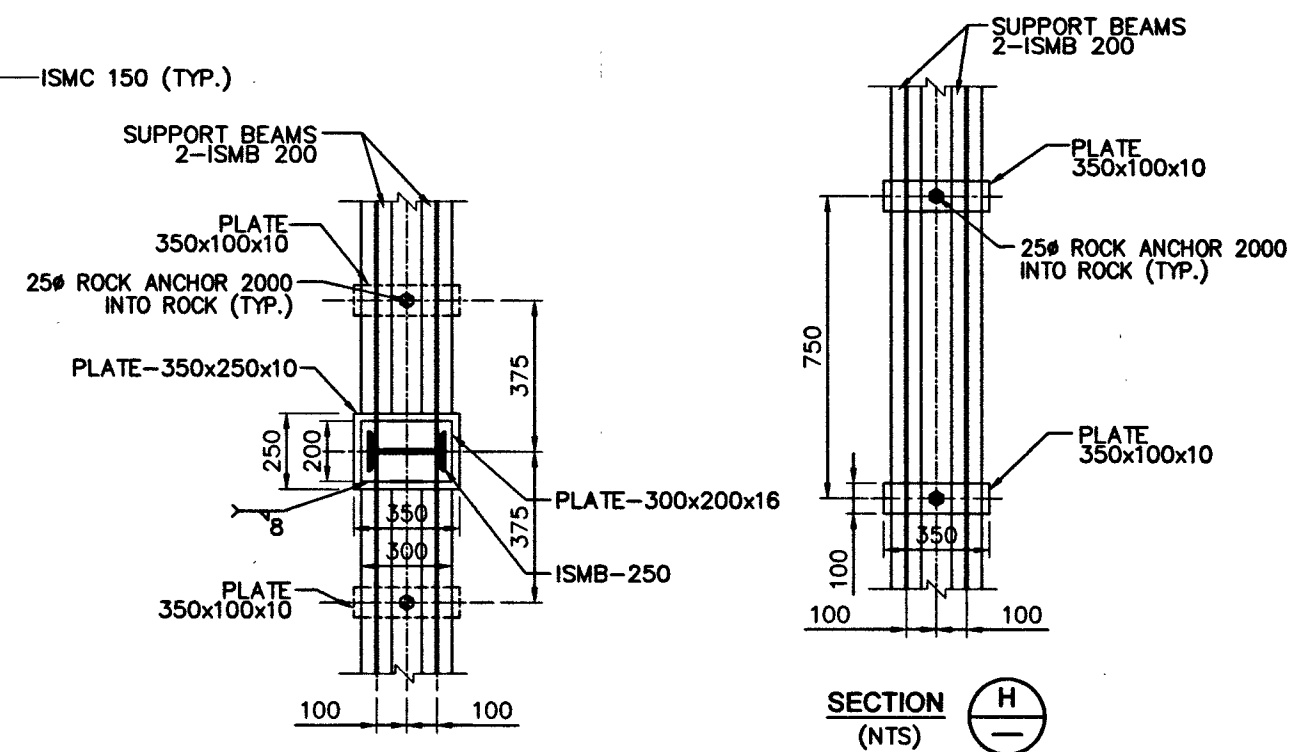
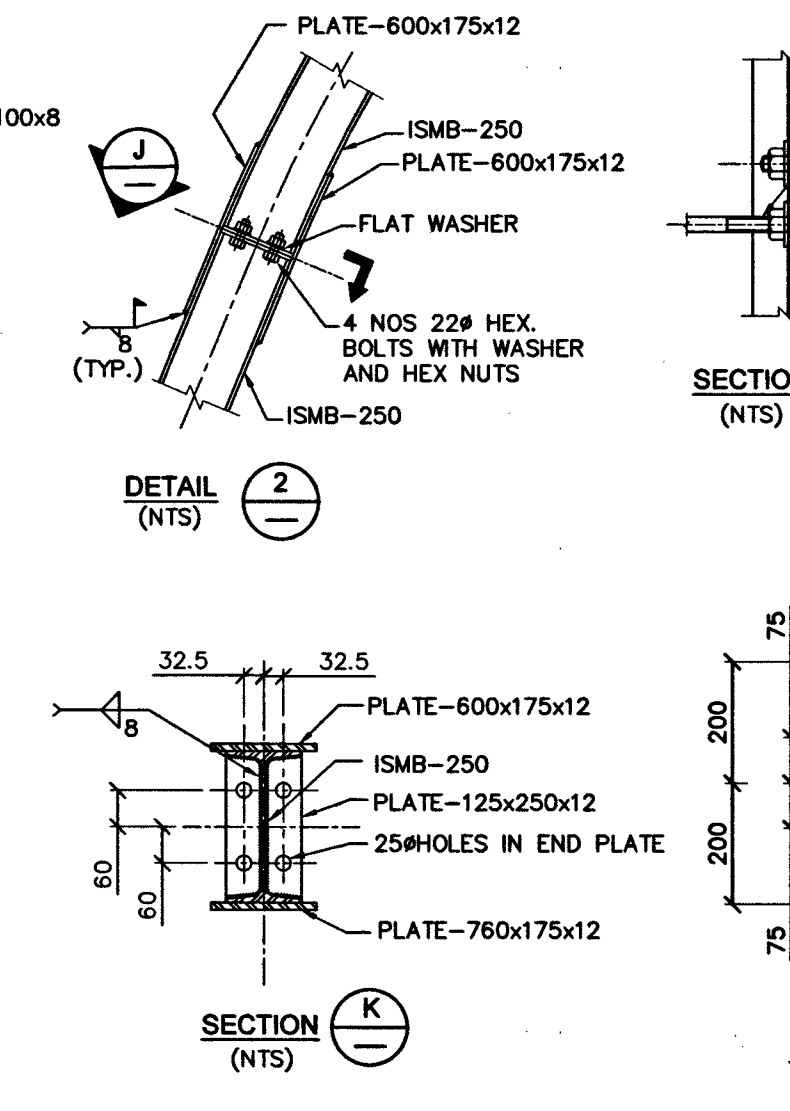
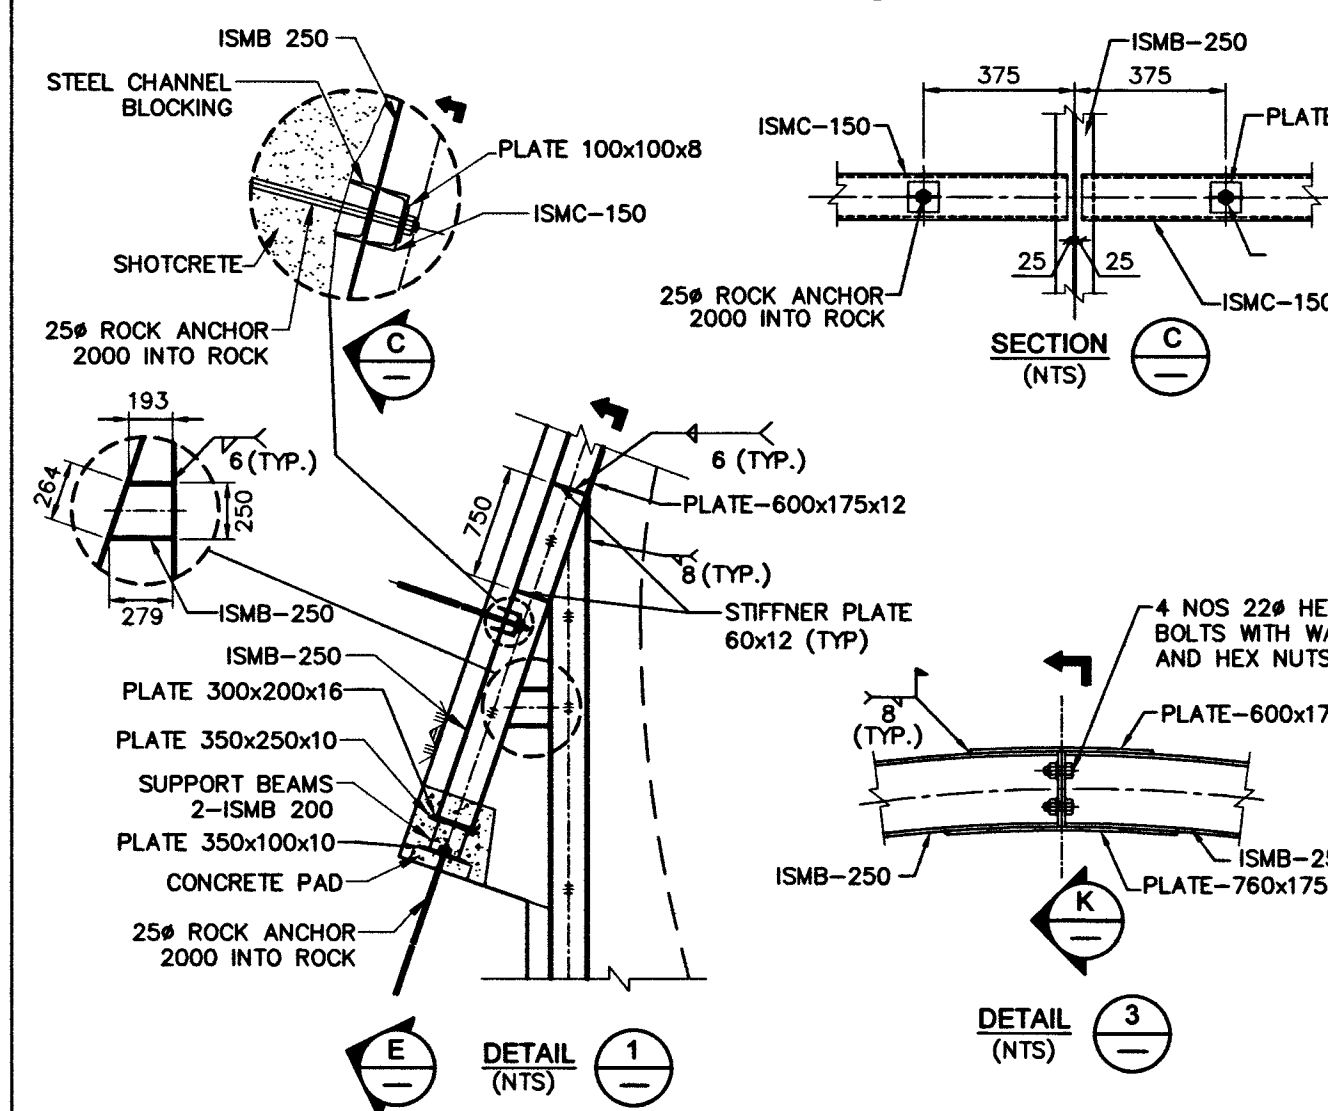
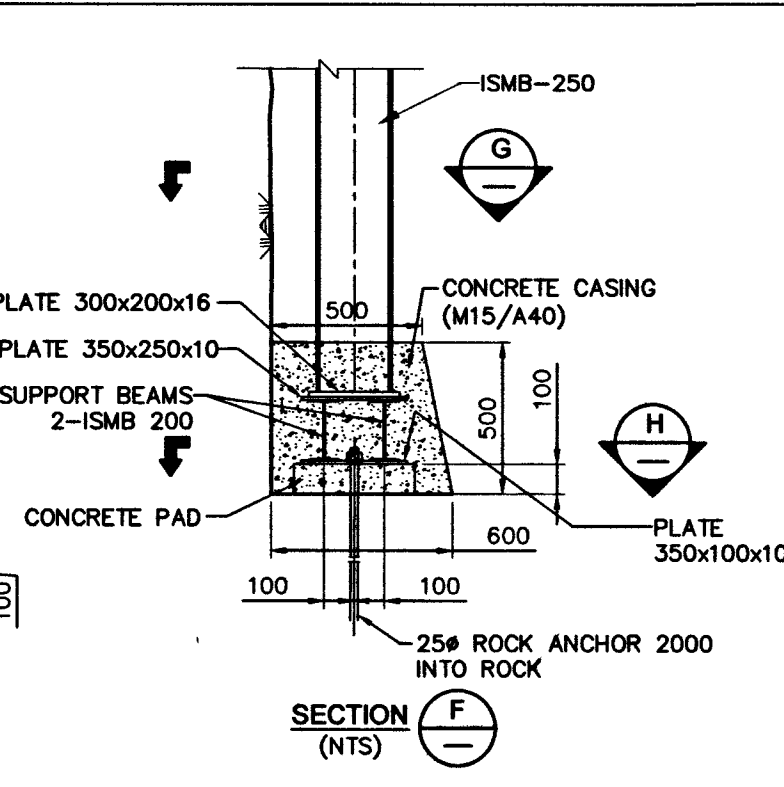
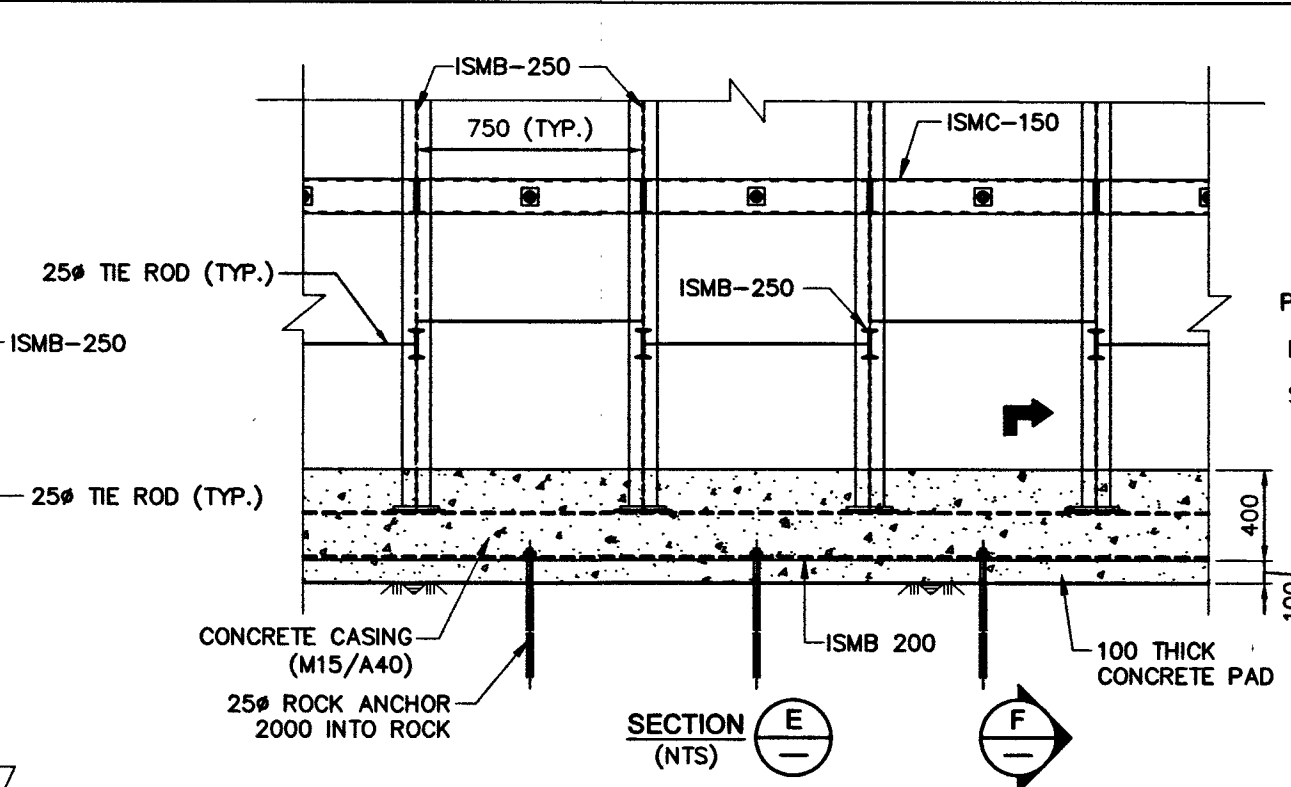
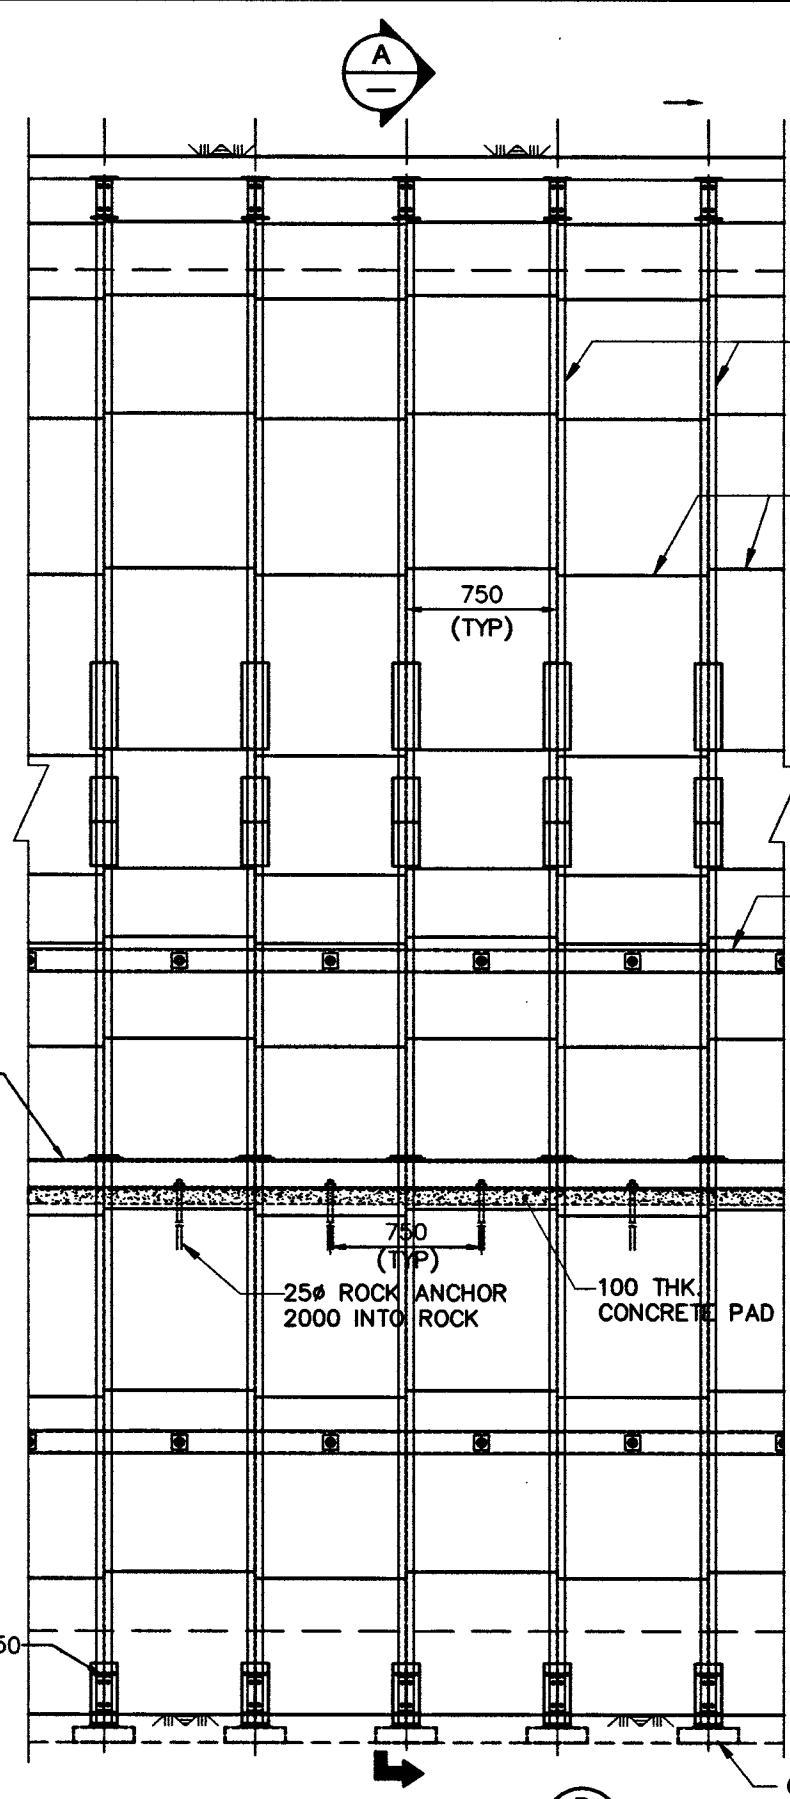


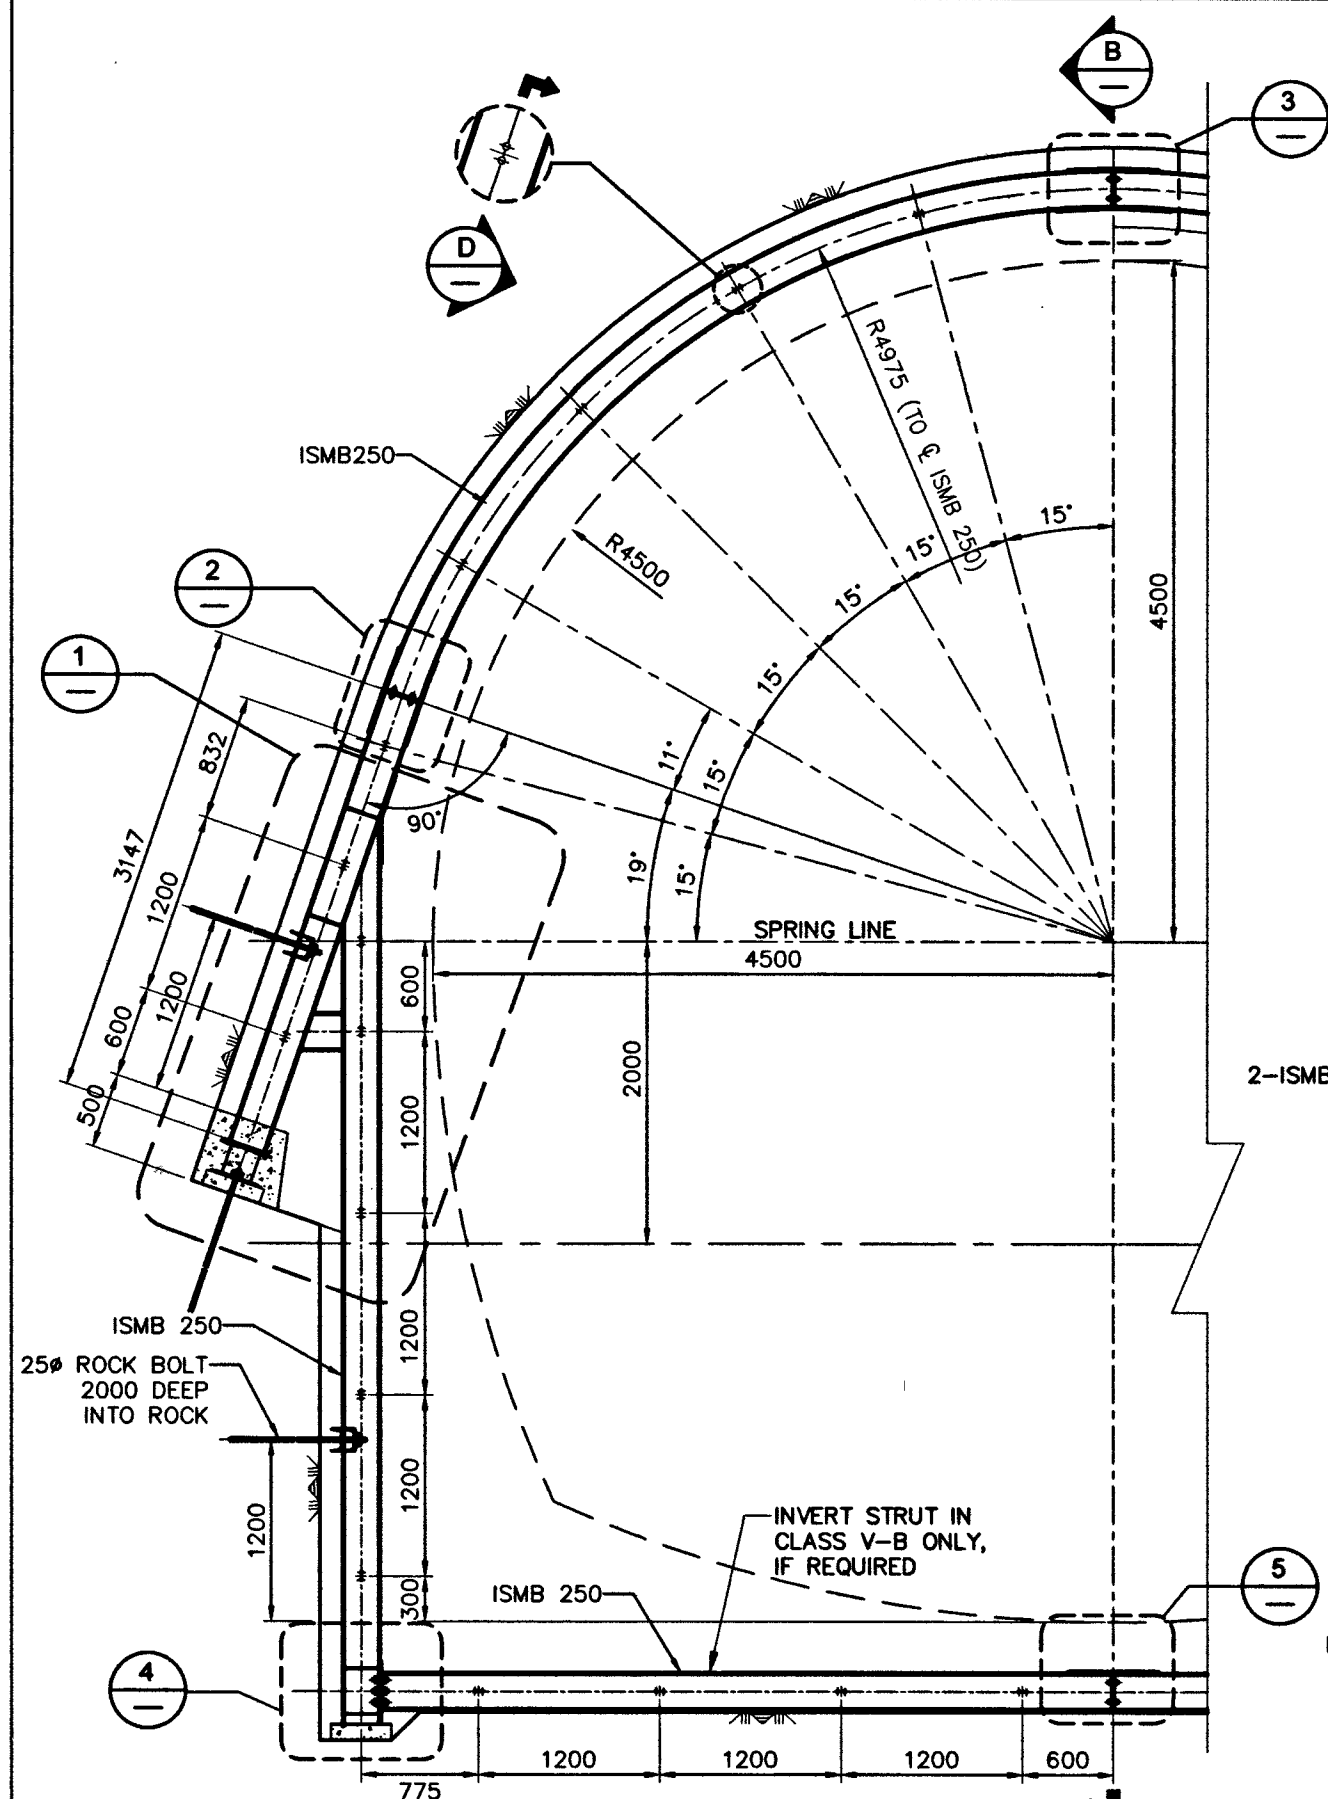

- NOTES:-**
- सभी माप मिलीमीटर में दिए गए हैं।
ALL DIMENSIONS ARE IN MILLIMETERS.
 - ALL STEEL SECTIONS AND PLATES FOR RIB AND ACCESSORIES SHALL CONFORM TO SECTION B-4 OF TECHNICAL SPECIFICATIONS.
 - STEEL FOR BOLTS, NUTS AND WASHERS SHALL CONFORM TO IS: 8500.
 - ALL WELDING, WELDING ELECTRODES AND WORKMANSHIP SHALL CONFORM TO IS: 814 AND IS: 816.
 - FOOTING FOR STEEL RIBS SHALL BE PLACED ON IN-SITU CONCRETE PAD OF M15/A40 GRADE. THE CONCRETE PAD SHALL BE FOUNDED ON FIRM ROCK.
 - THE SPACING OF RIBS SHALL BE @ 750 C/C. THE SPACING OF RIBS MAY BE MODIFIED TO SUIT THE SITE CONDITION WITH THE APPROVAL OF ENGINEER-IN-CHARGE.
 - THE LOCATION OF STEEL RIB JOINT, TIE ROD, LOCATION OF WALL ANCHORING MAY BE MODIFIED MARGINALLY TO SUIT THE SITE CONDITION.
 - PROFILE OF THE STEEL RIBS MAY BE MODIFIED AT SITE TO INTERFACE WITH THE FORE-POLING/ PIPE ROOFING PROFILE.

REFERENCE DRAWING:-
1 NHDB-4DC4-41-DD-1009 & 1010

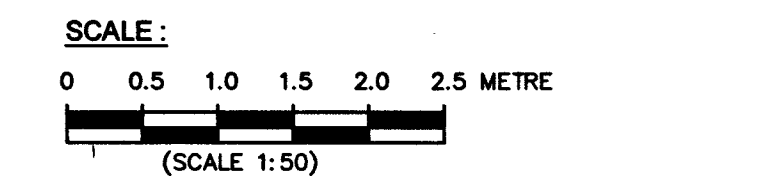

एन एच पी सी लिमिटेड NHPC Limited (A GOVT. OF INDIA ENTERPRISE) दिबांग बहुउद्देशीय परियोजना DIBANG MULTIPURPOSE PROJECT TAIL RACE TUNNEL STEEL RIBS DETAILS CLASS - VA & VB		26.09.25 00 DATE NO. ISSUED FOR CONSTRUCTION 26.09.25 00 DATE NO. REVISION OR ISSUES 26.09.25 00 DATE NO. BY CH. AS	26.09.25 00 DATE NO. SUBMITTED 26.09.25 00 DATE NO. RECOMMENDED 26.09.25 00 DATE NO. APPROVED
DRG. NO. NHDB-4DC4-41-DD-1011-00		26.09.25 00 DATE NO. ISSUED FOR CONSTRUCTION	26.09.25 00 DATE NO. SUBMITTED