

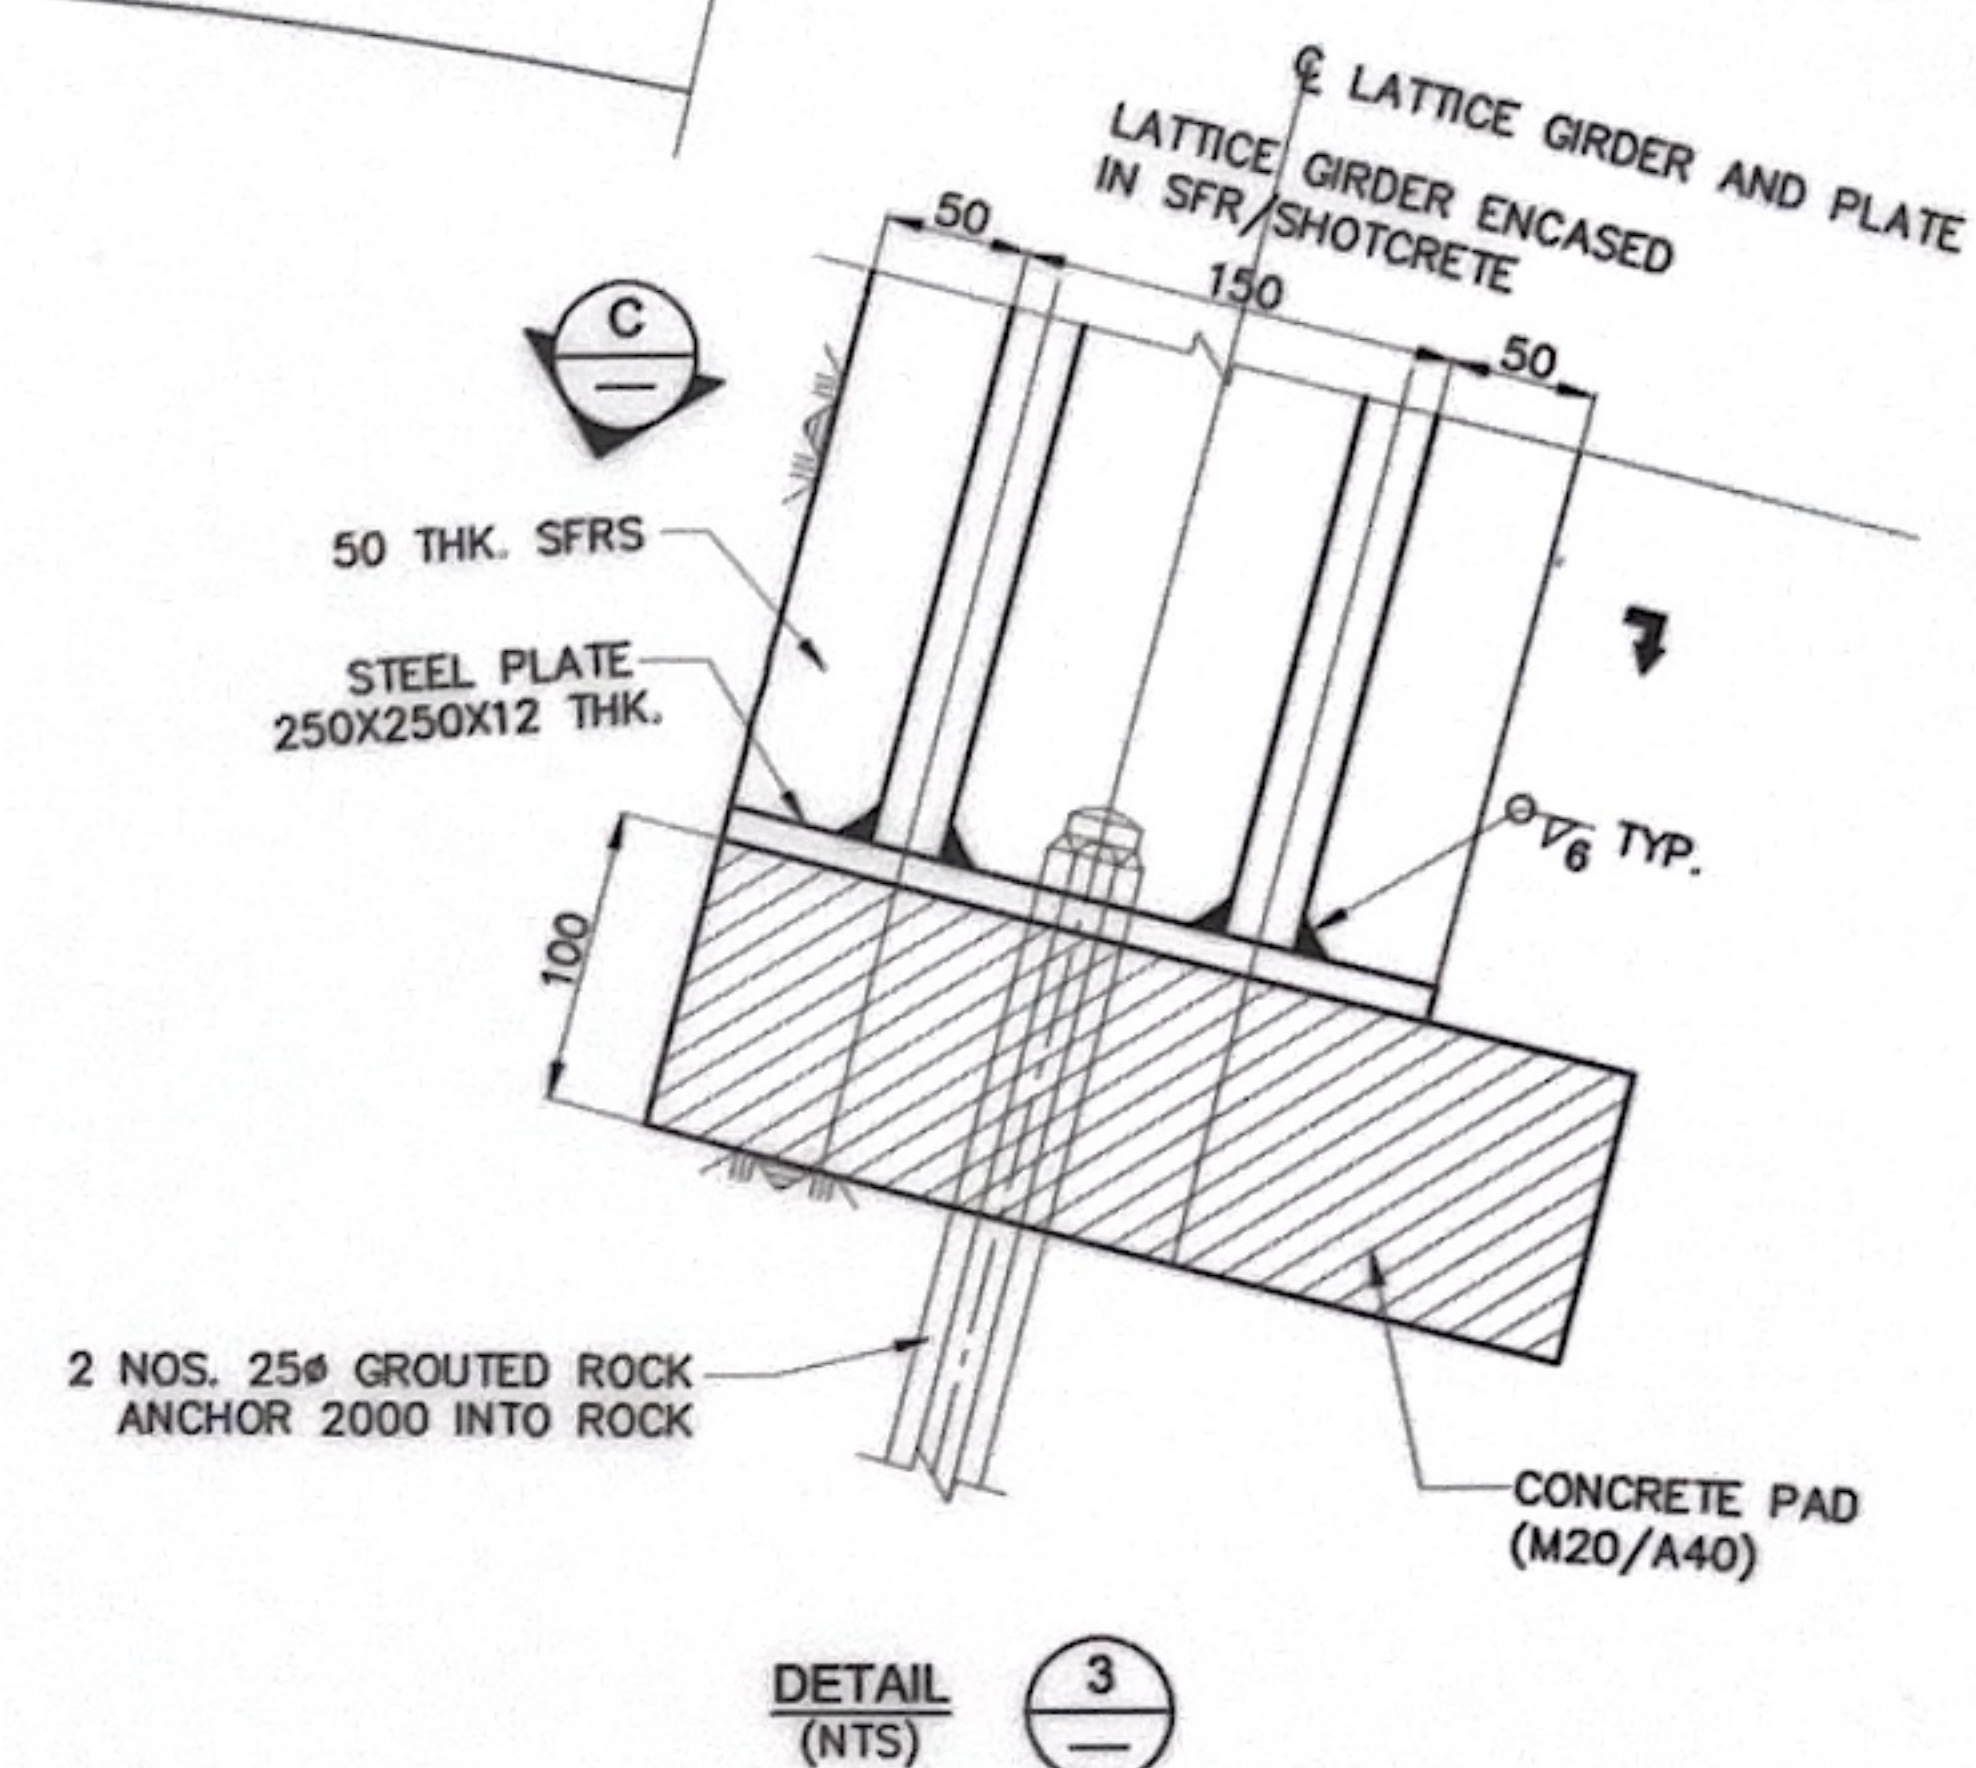
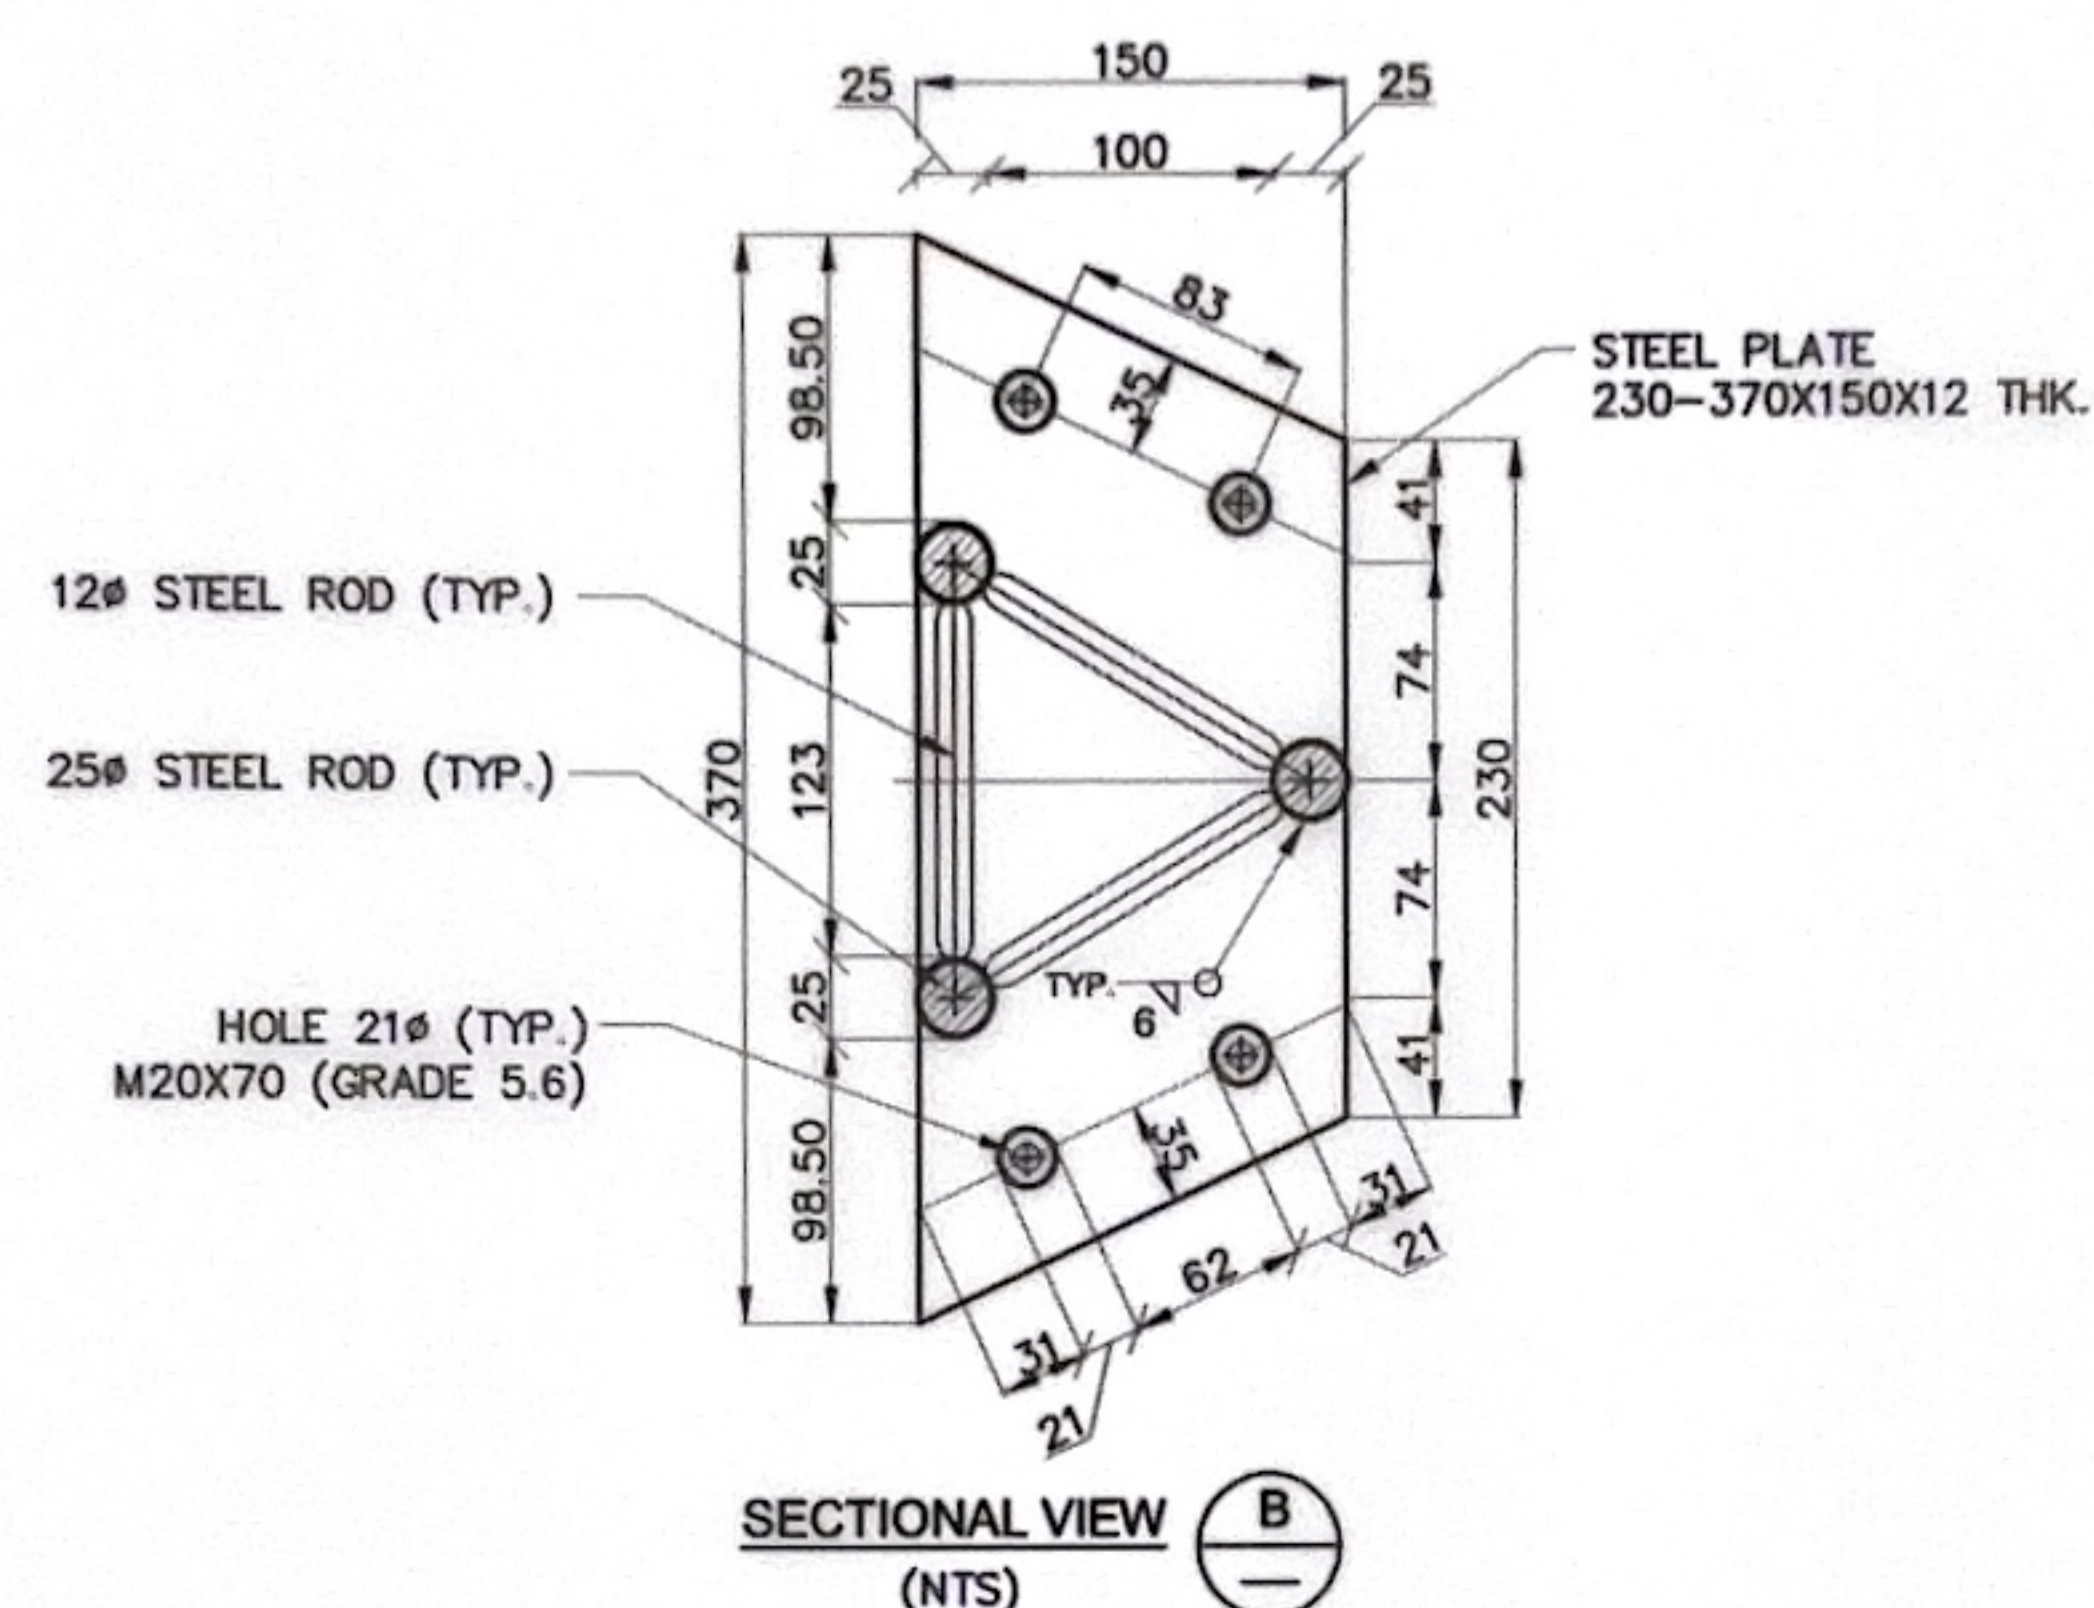
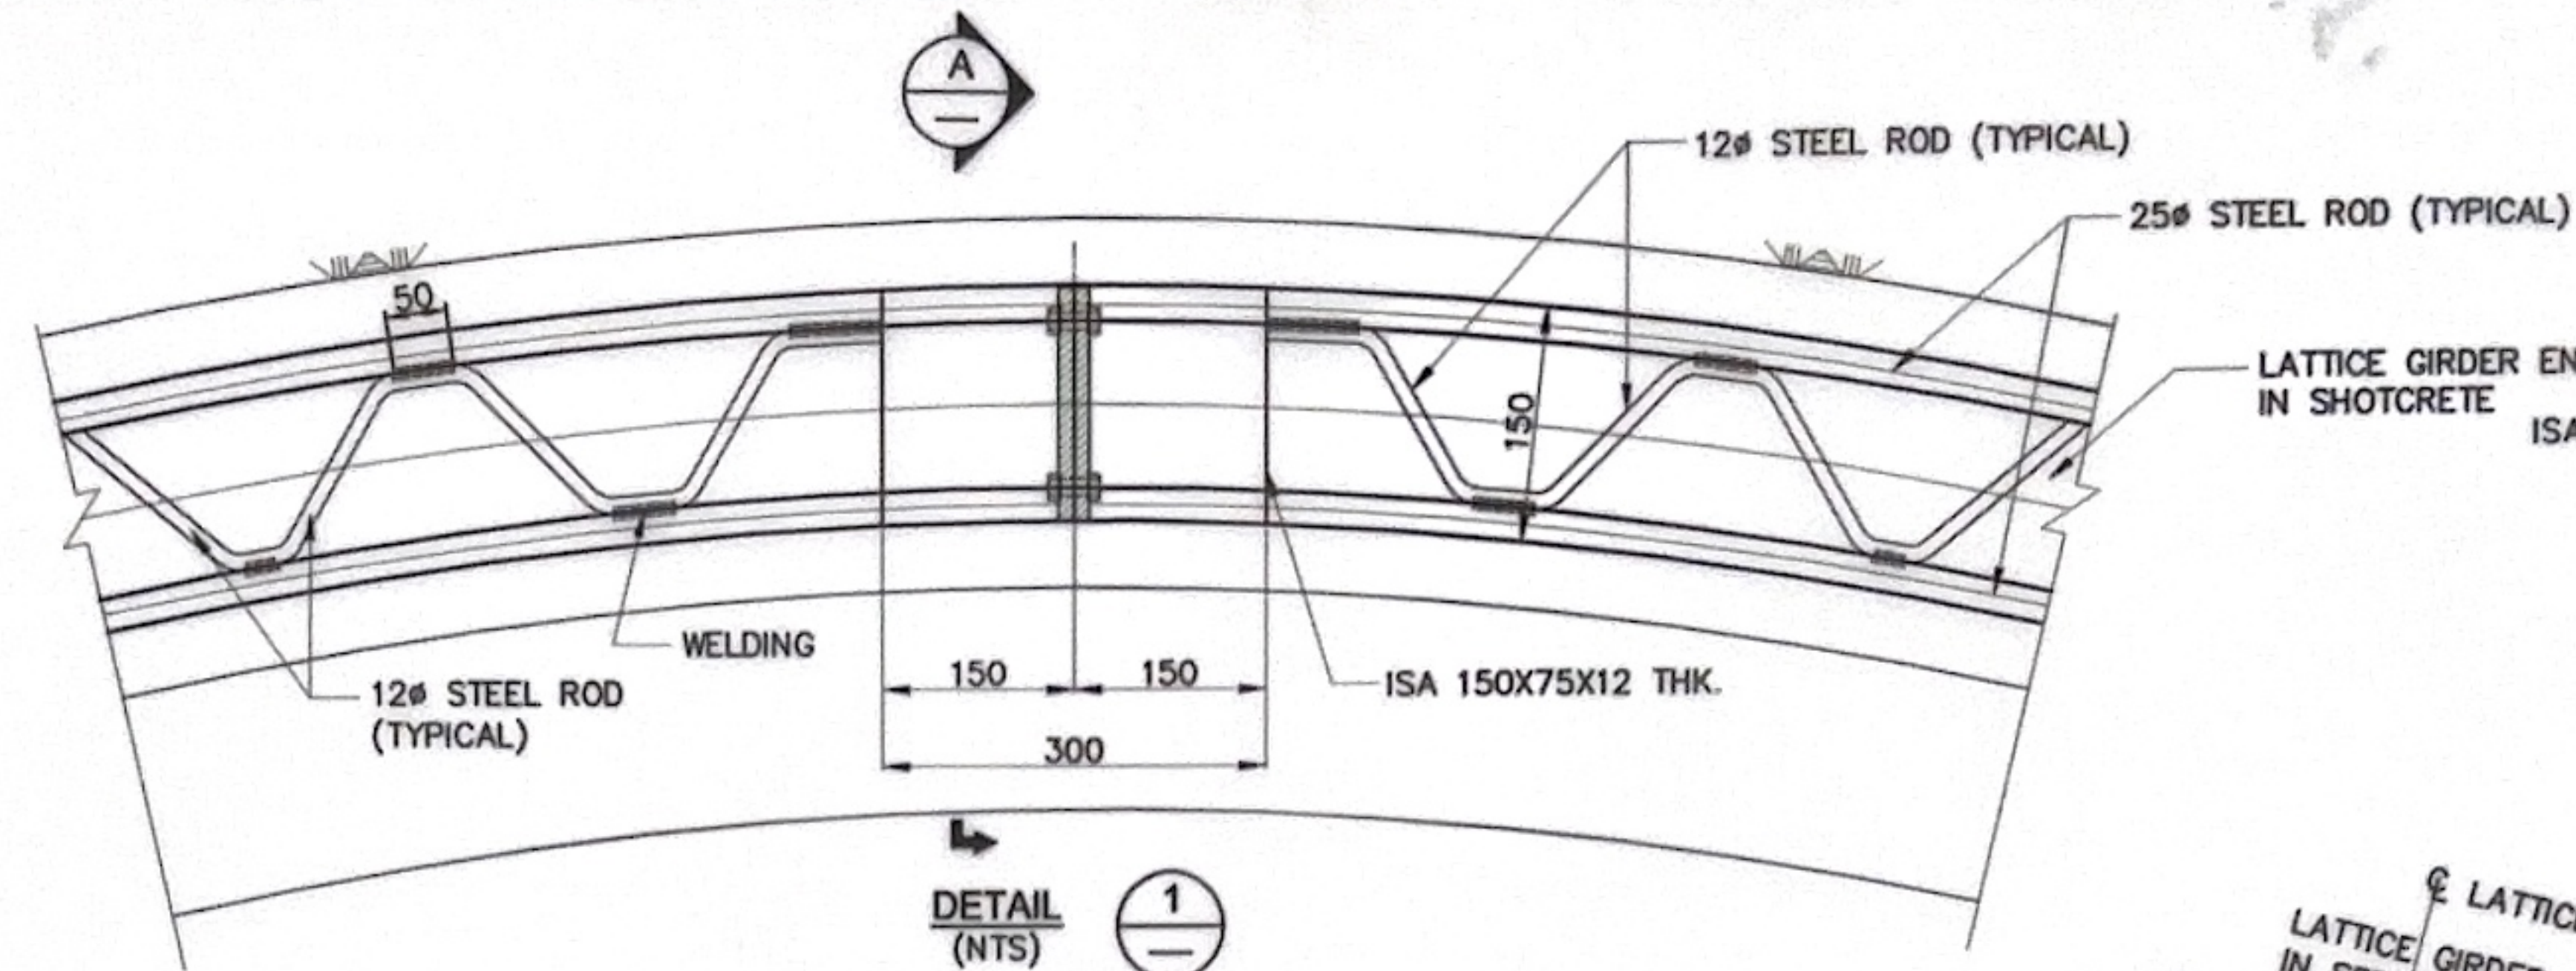
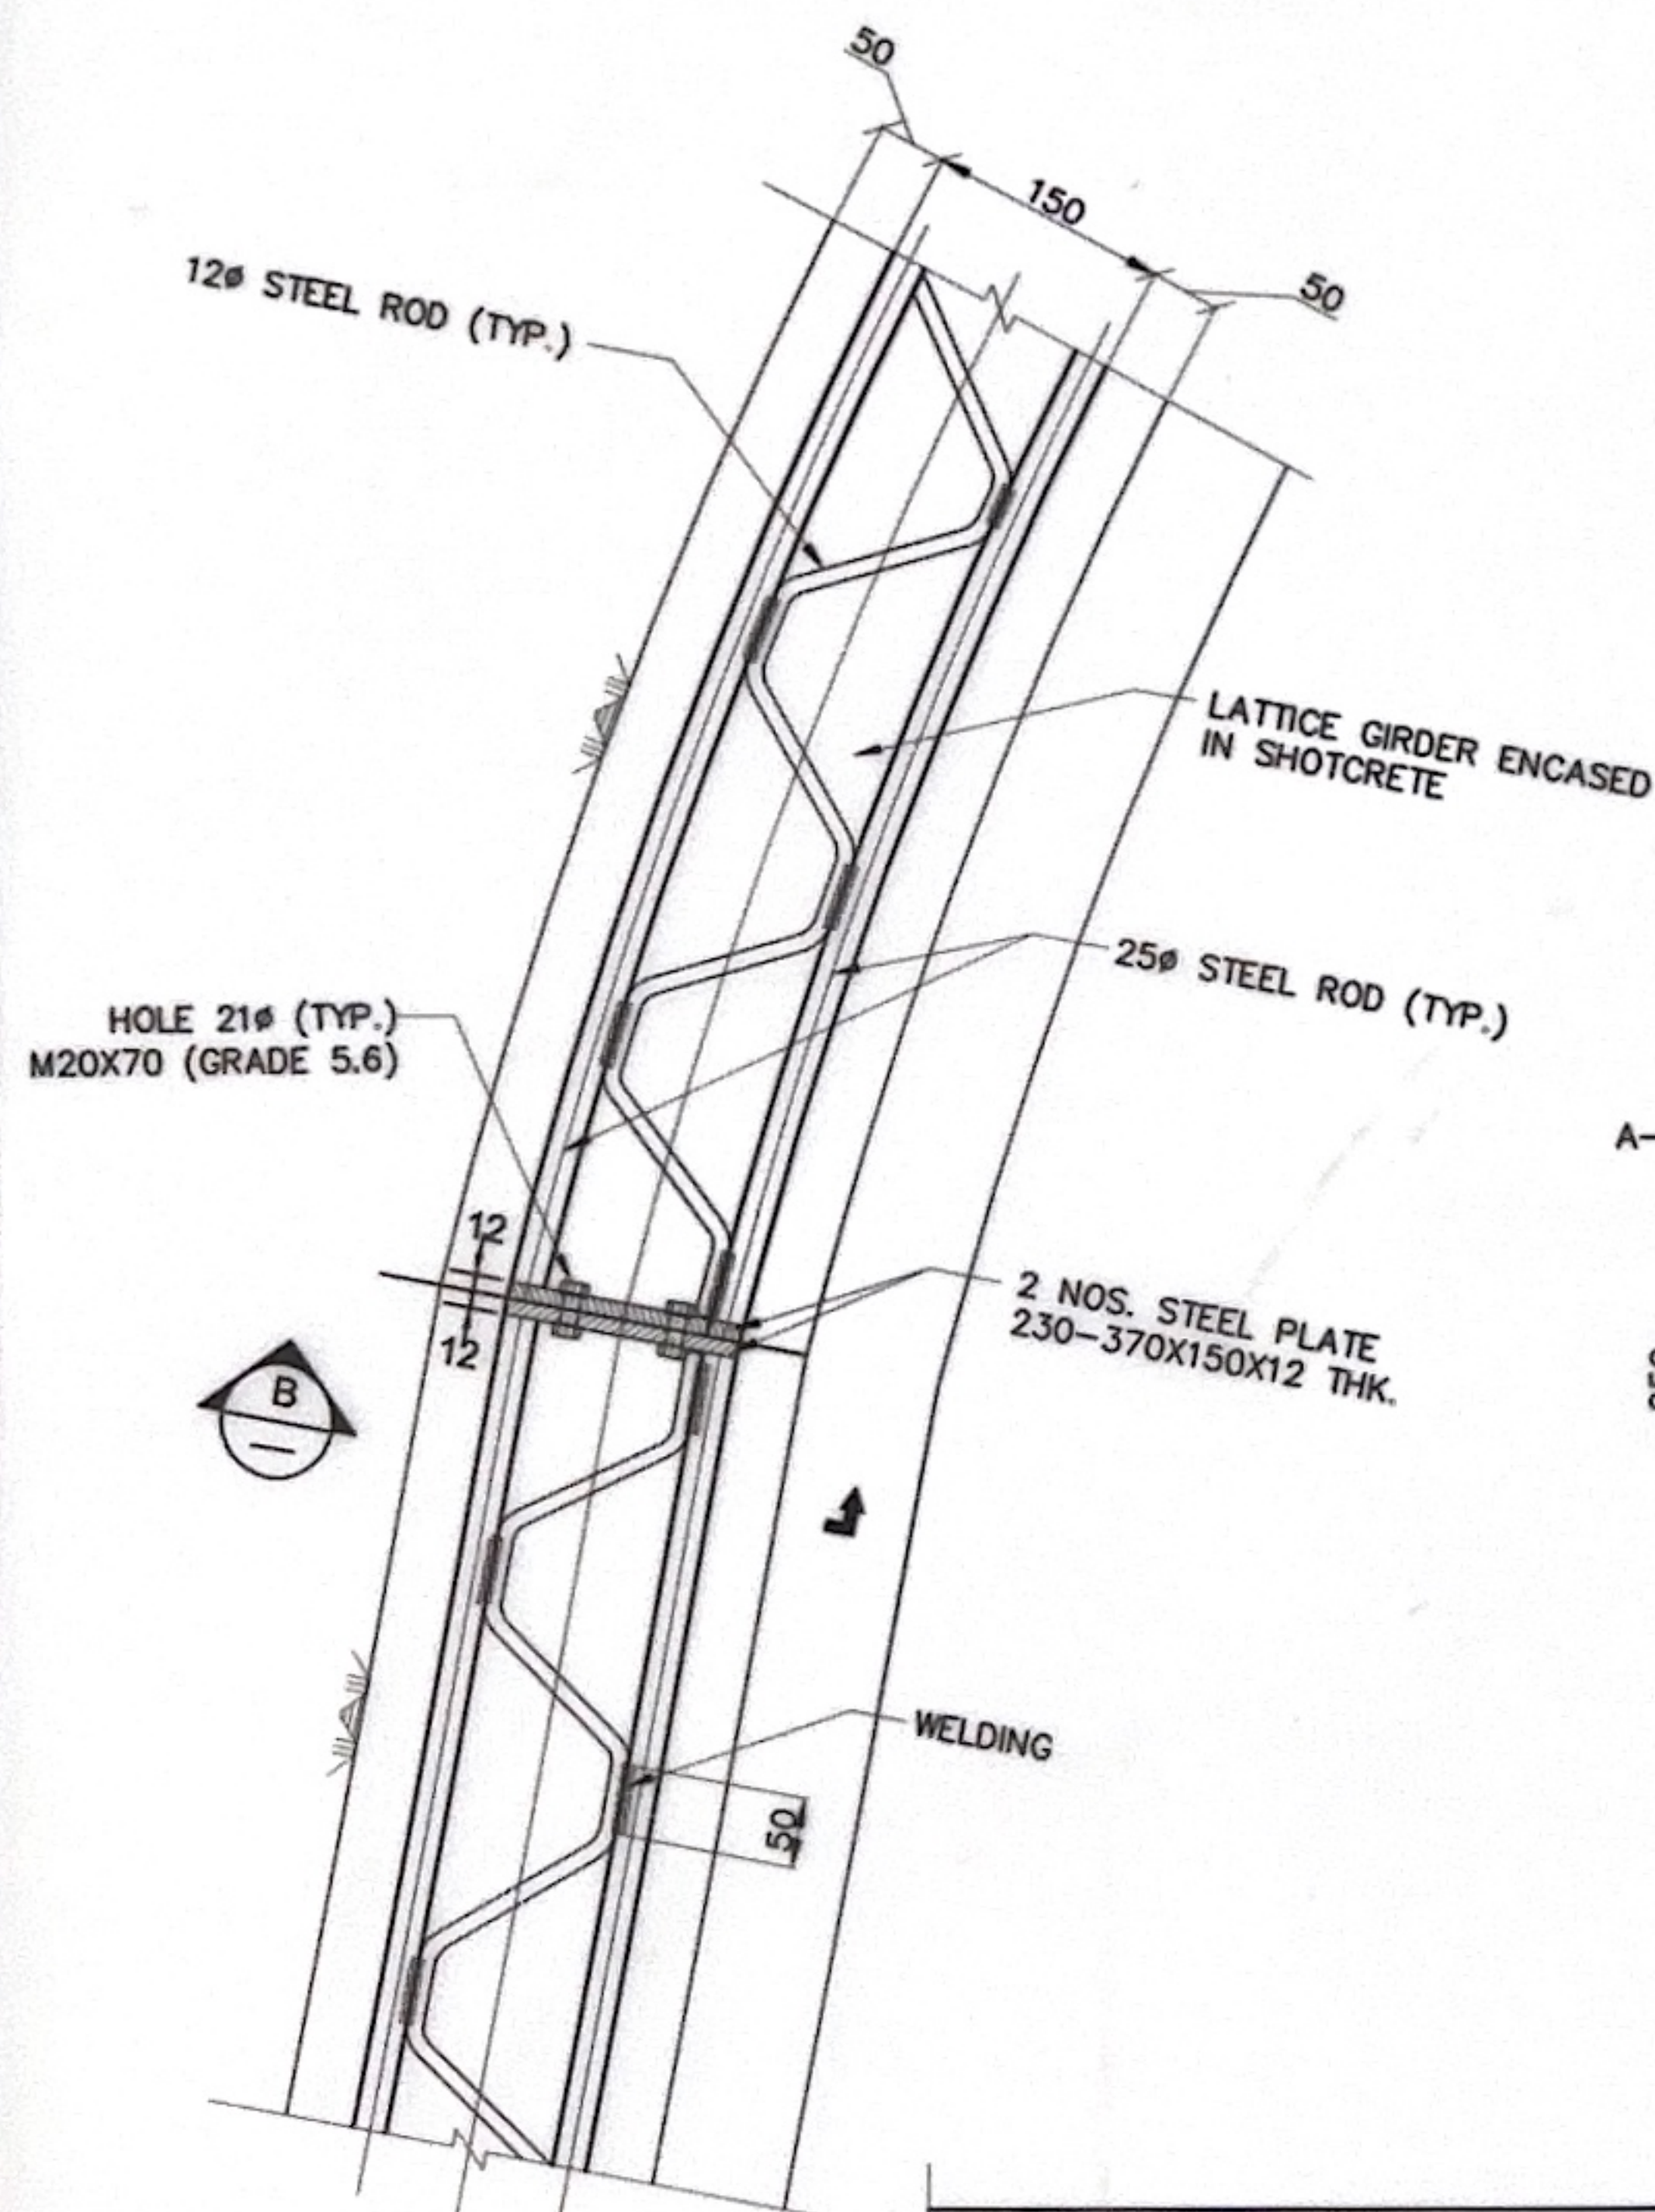




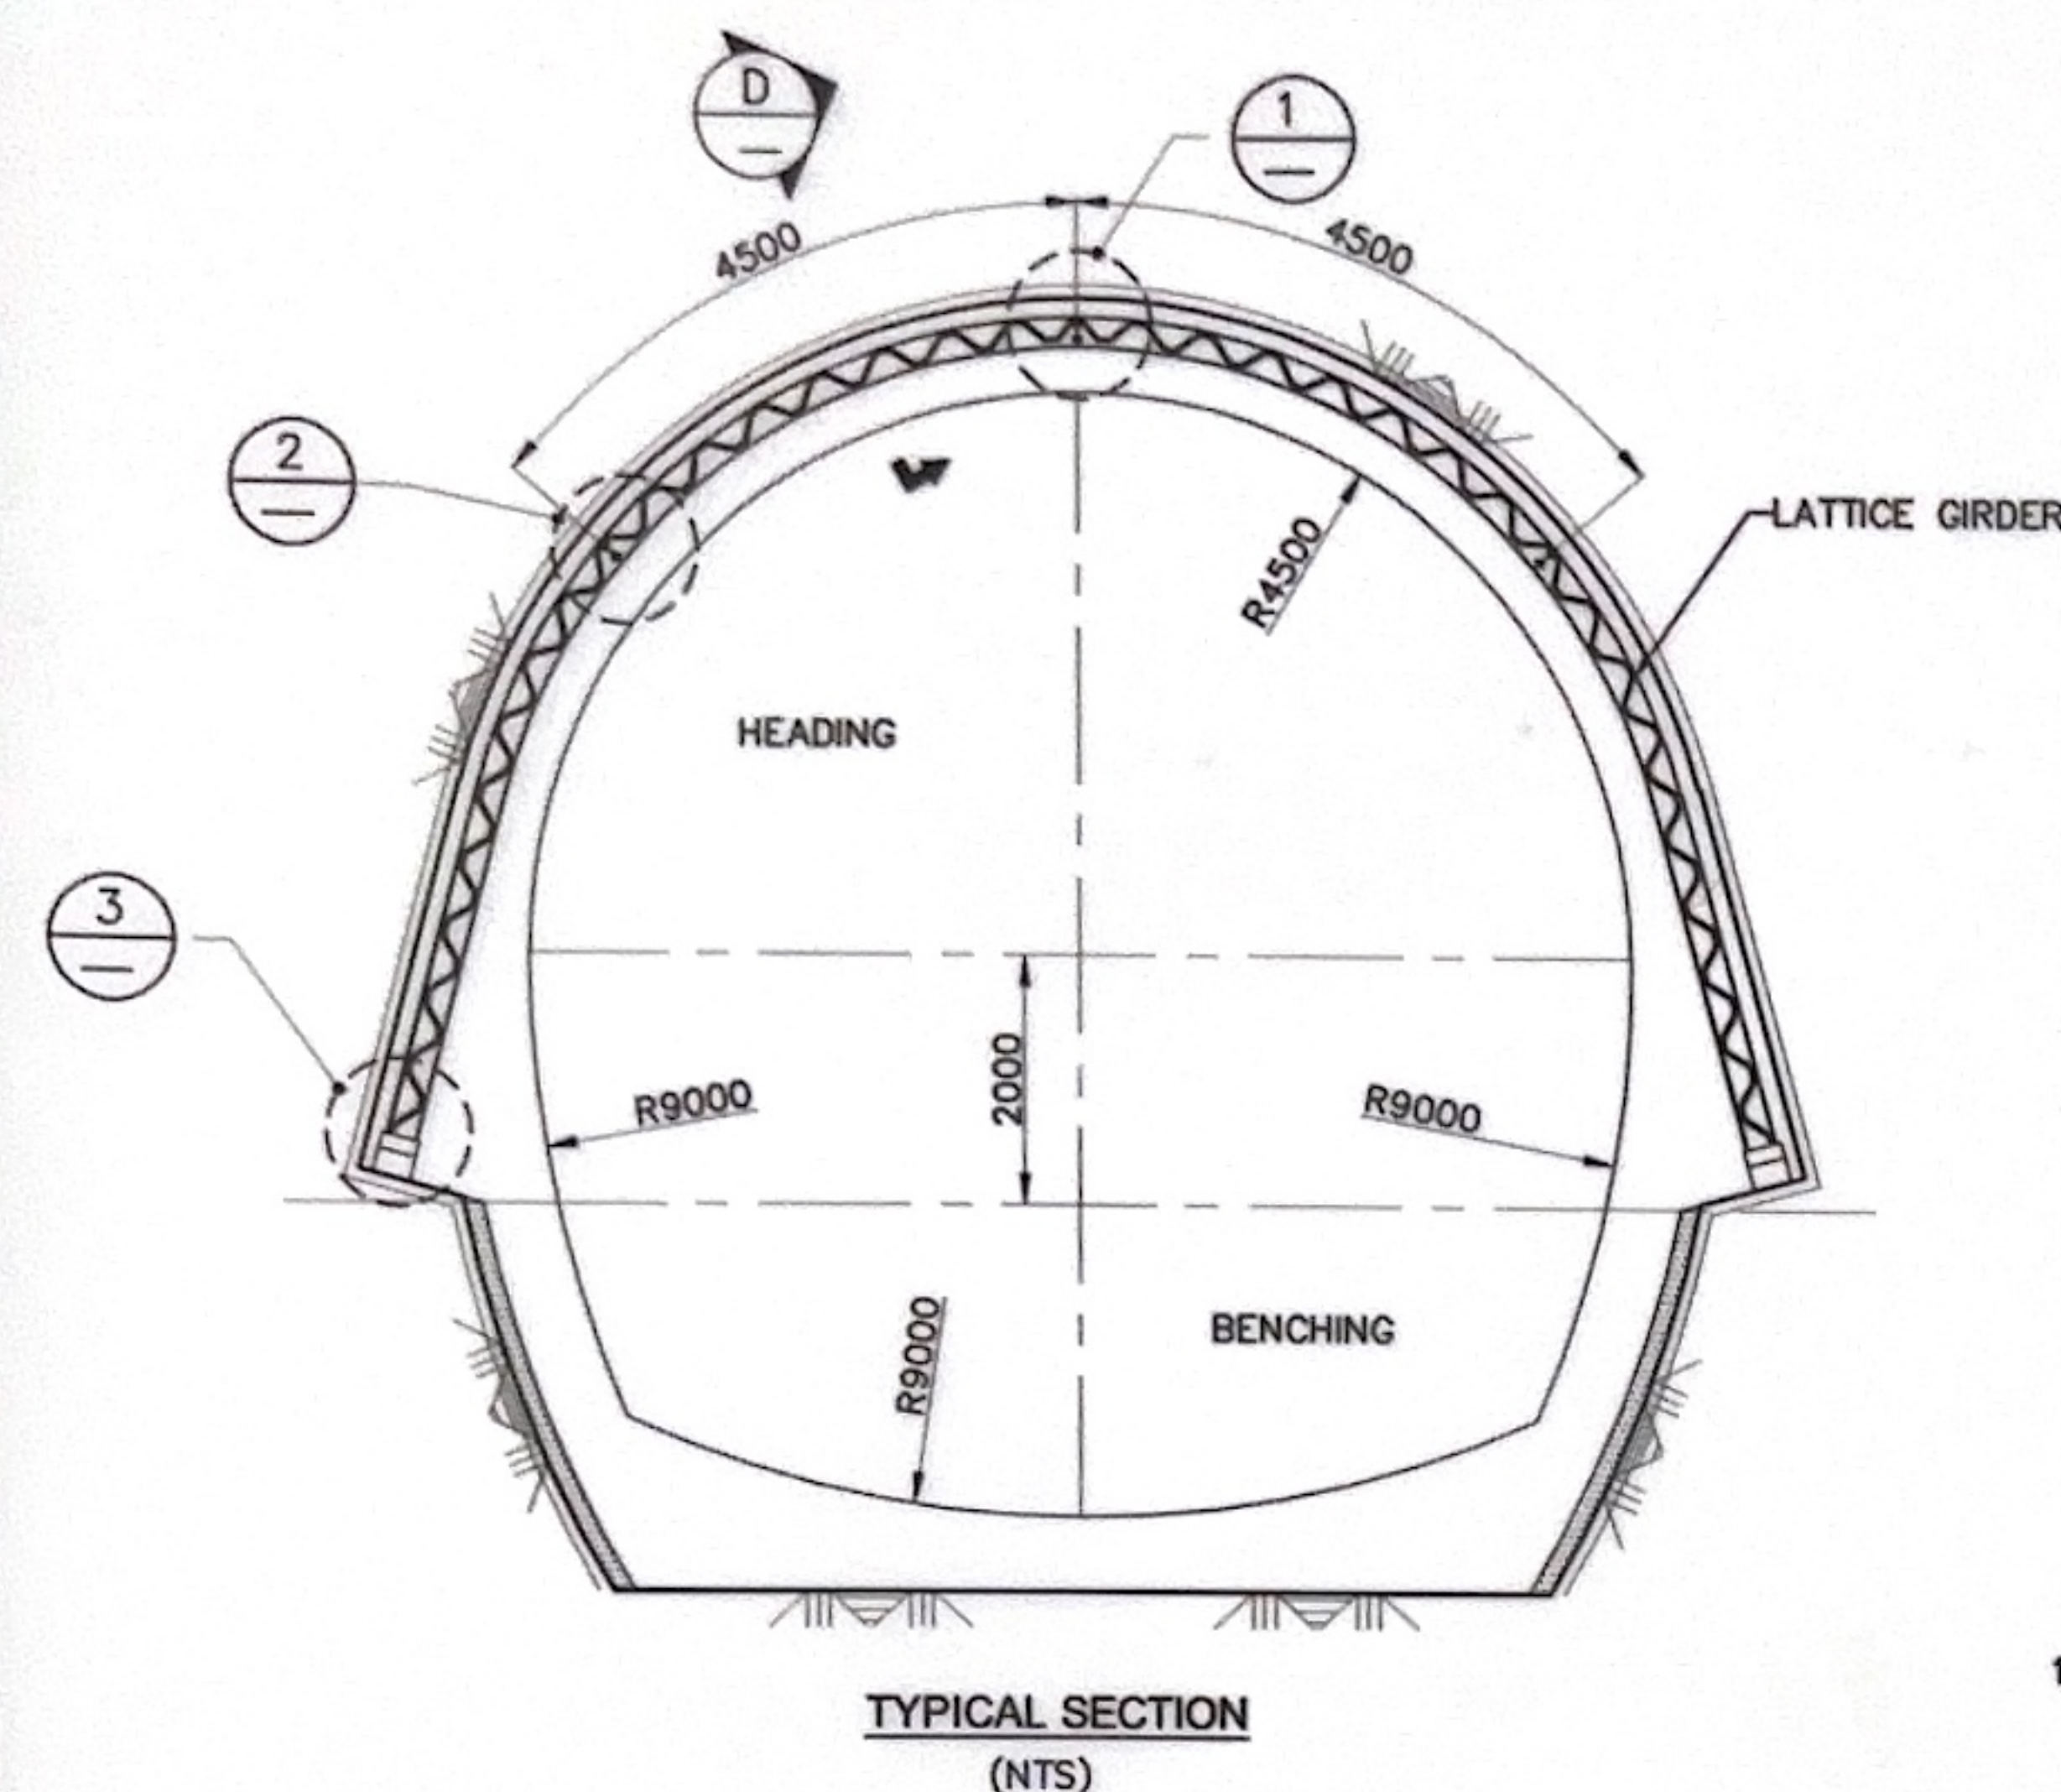


SECTIONAL VIEW A (NTS)



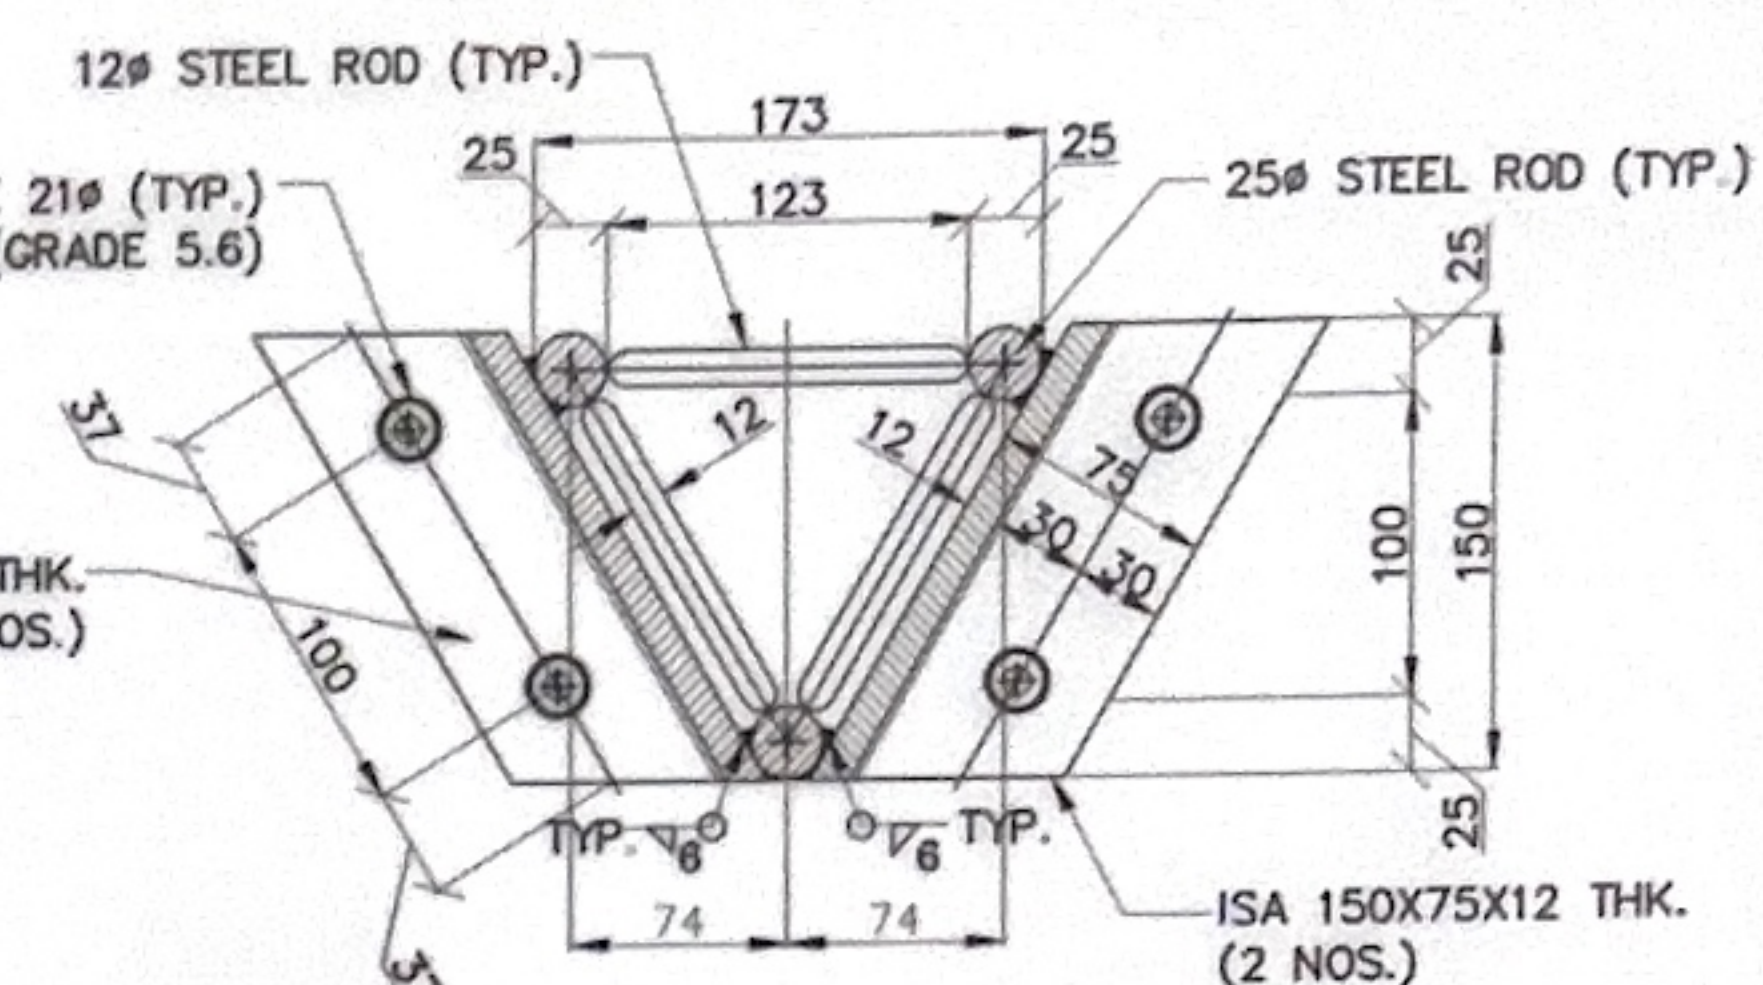


NOTES

1. सभी माप मिलीमीटर में मीटर में दिए गए हैं।
ALL DIMENSIONS ARE IN MILLIMETERS.
2. STEEL RIBS MAY BE PROVIDED WITH LATTICE GIRDER AS PER SITE SPECIFIC CONDITIONS WITH THE APPROVAL OF ENGINEER-IN-CHARGE.
3. LATTICE GIRDER SHOWN IN THE DRAWING SHALL BE CONFORMING TO SECTION B.4 OF TECHNICAL SPECIFICATION.
4. THIS ARRANGEMENT OF LATTICE GIRDER SHALL BE USED IN HEADING ZONE FOR ROCK CLASS IV AND CLASS V-A & V-B WITH THE APPROVAL OF ENGINEER-IN-CHARGE.
5. LATTICE GIRDER SHALL CONSIST OF 3 NOS. 25 MM DIA. REINFORCEMENT BARS FORMING TRIANGLE AS SHOWN IN THE DRAWING, LACED TOGETHER BY 10 MM DIA. REINFORCEMENT BARS.
6. SPACING OF LATTICE GIRDER SHALL BE 750 C/C IN CLASS IV ROCK AND 500C/C IN CLASS V-A & V-B ROCK. SPACING OF LATTICE GIRDER MAY BE MODIFIED MARGINALLY TO SUIT SITE CONDITIONS WITH THE APPROVAL OF ENGINEER-IN-CHARGE.
7. ALL STEEL SECTIONS, PLATES AND ACCESSORIES SHALL CONFORM TO IS: 2062: 2011.
8. STEEL FOR BOLTS, NUTS AND WASHERS SHALL CONFORM TO IS: 2062: 2011.
9. ALL WELDING, WELDING ELECTRODES AND WORKMANSHIP SHALL CONFORM TO IS: 816 & IS: 814.
10. THE REINFORCEMENT BAR SHALL CONFORM TO IS: 1786.
11. ADDITIONAL BRACINGS MAYBE PROVIDED BETWEEN CONSECUTIVE LATTICE GIRDERS WITH THE APPROVAL OF ENGINEER IN CHARGE AS PER SITE REQUIREMENT.

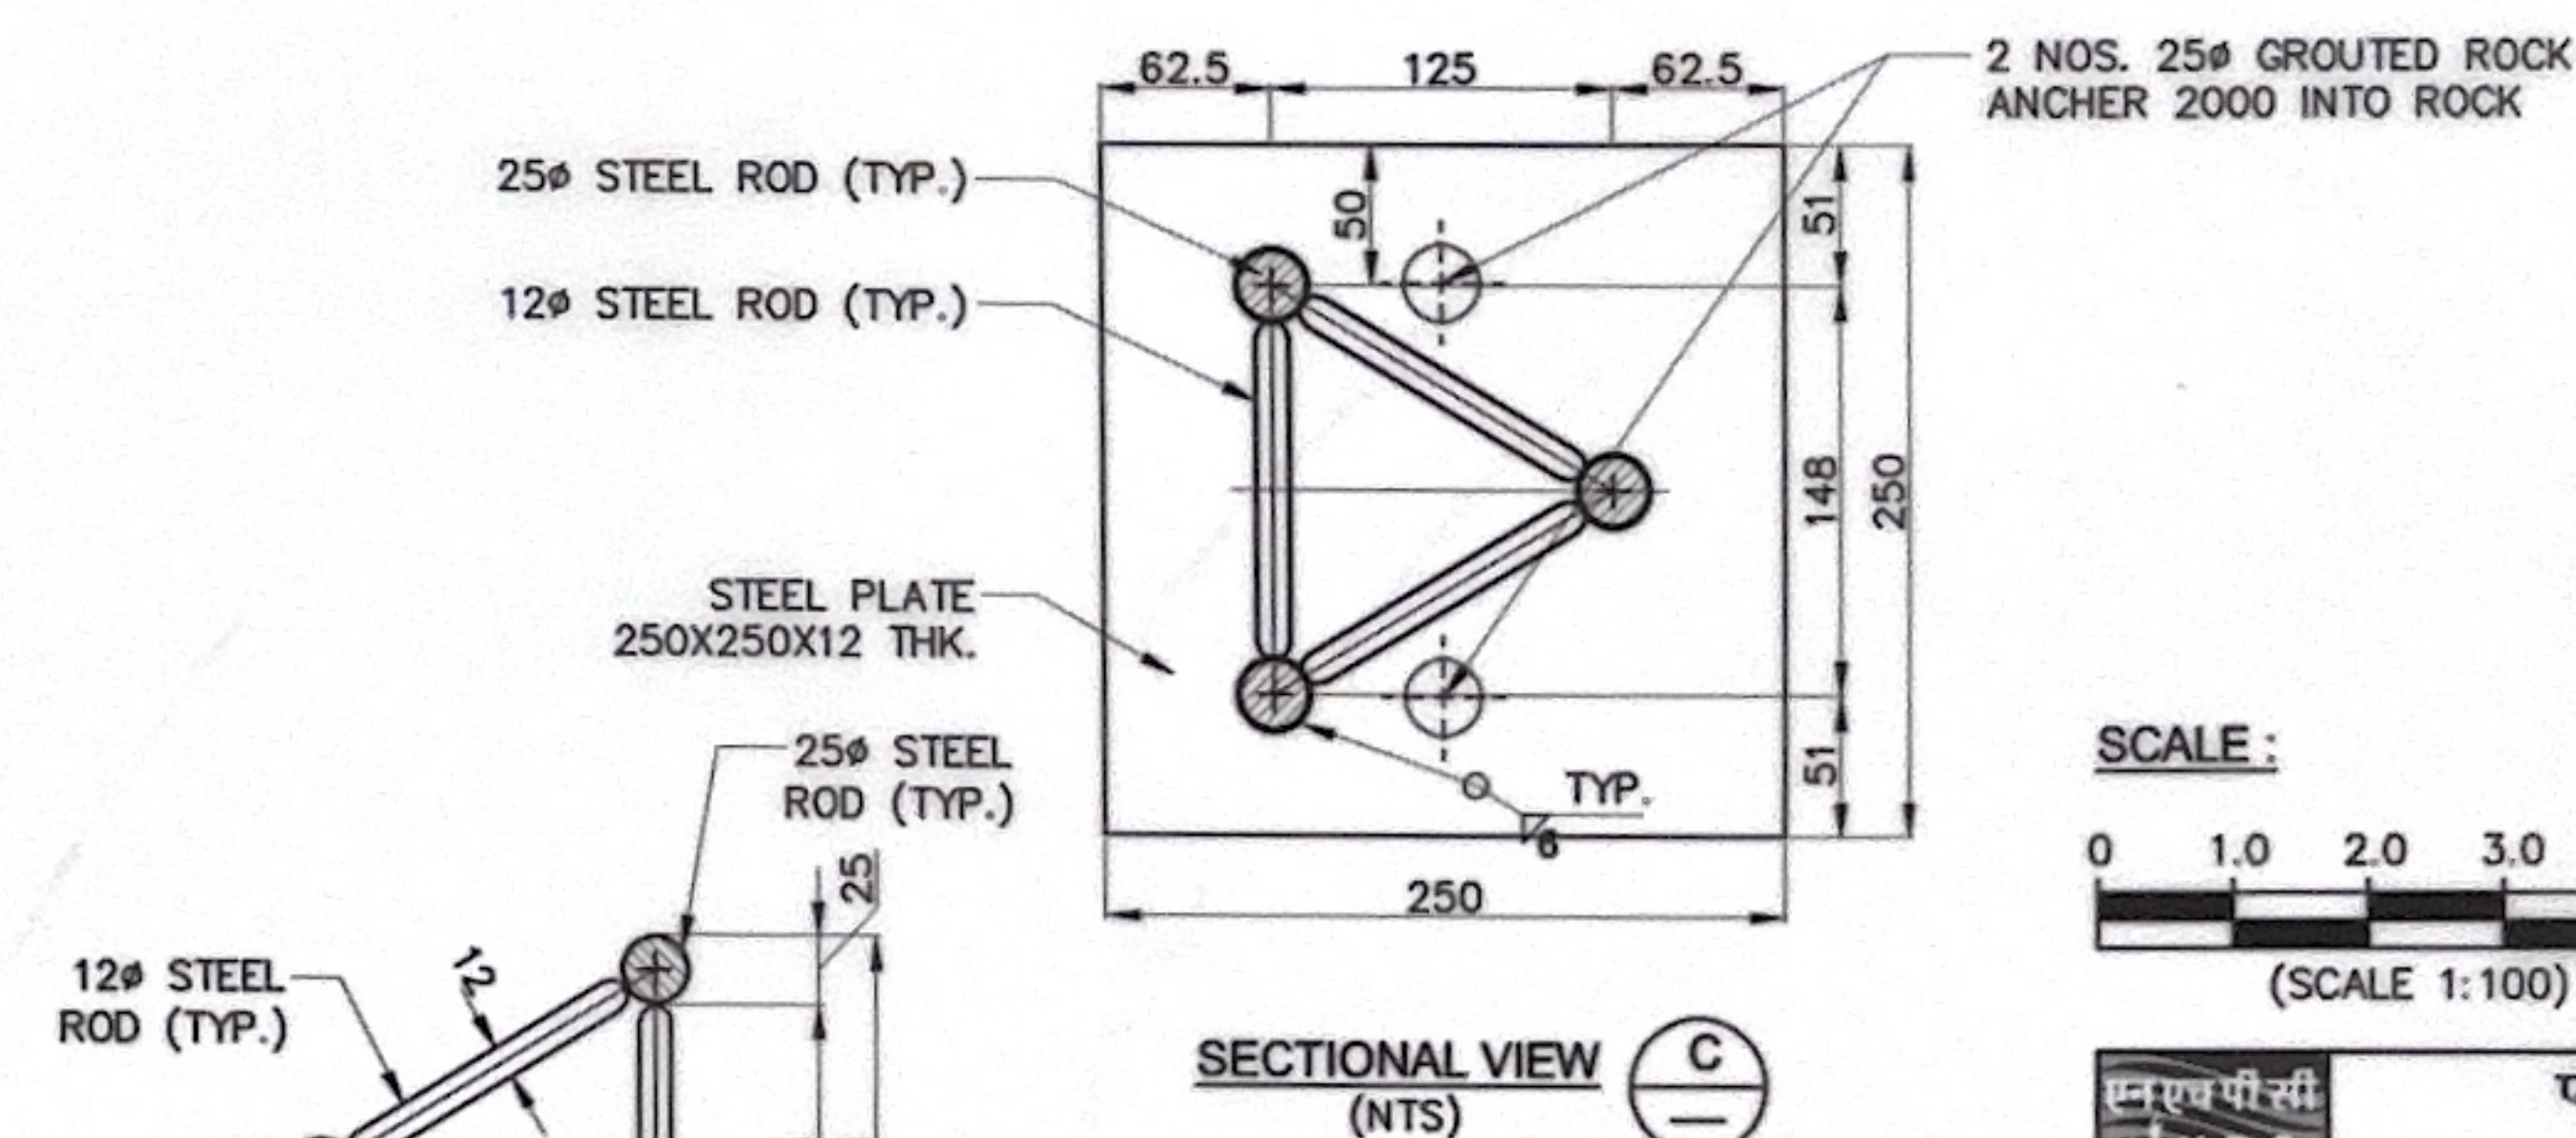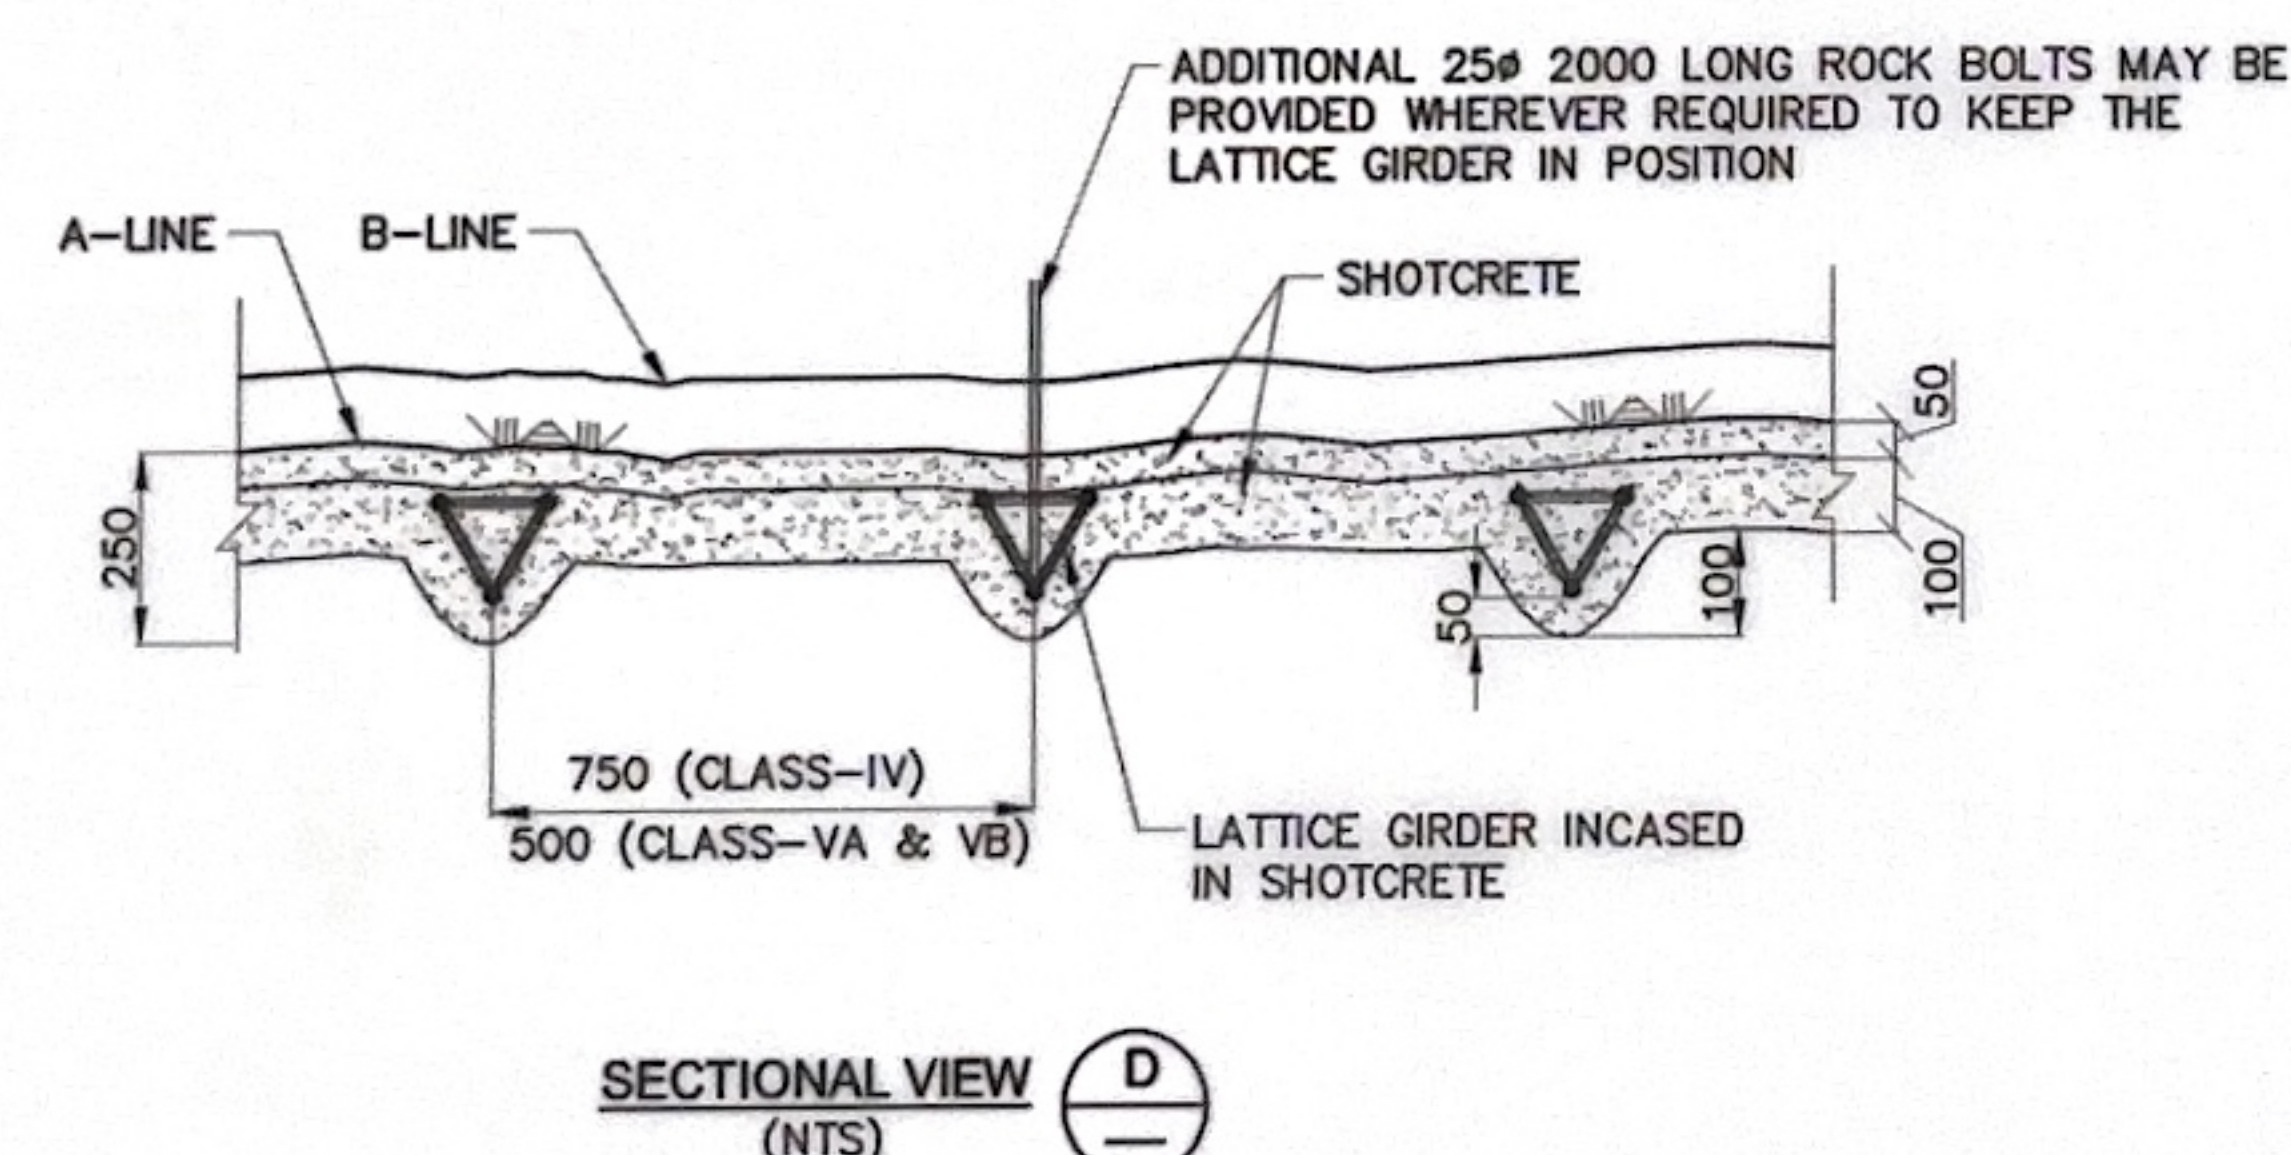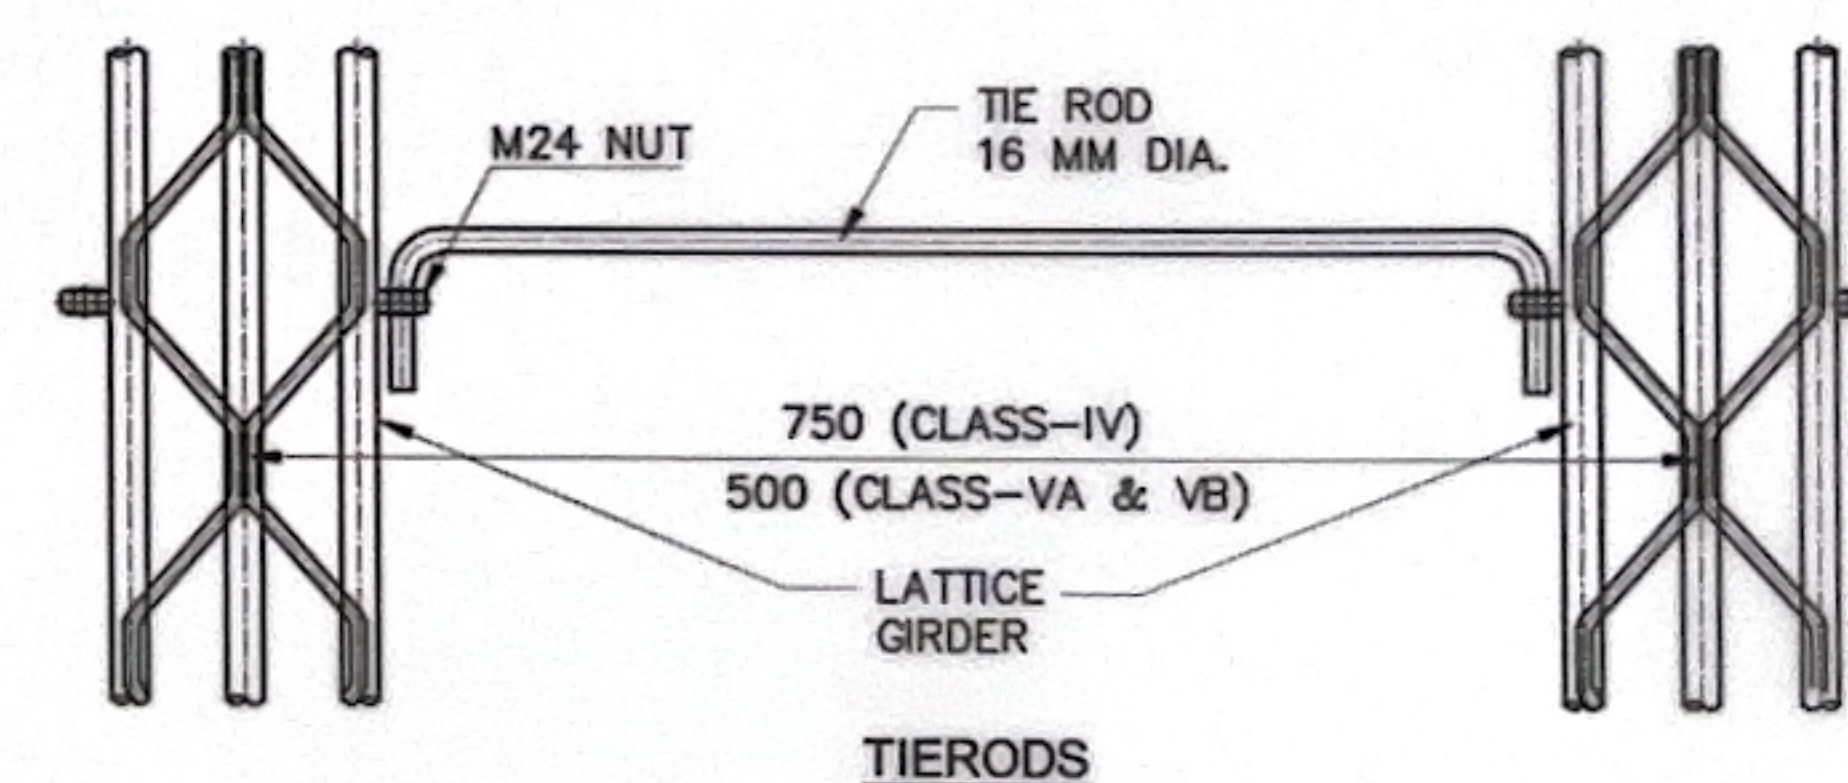

SCALE:

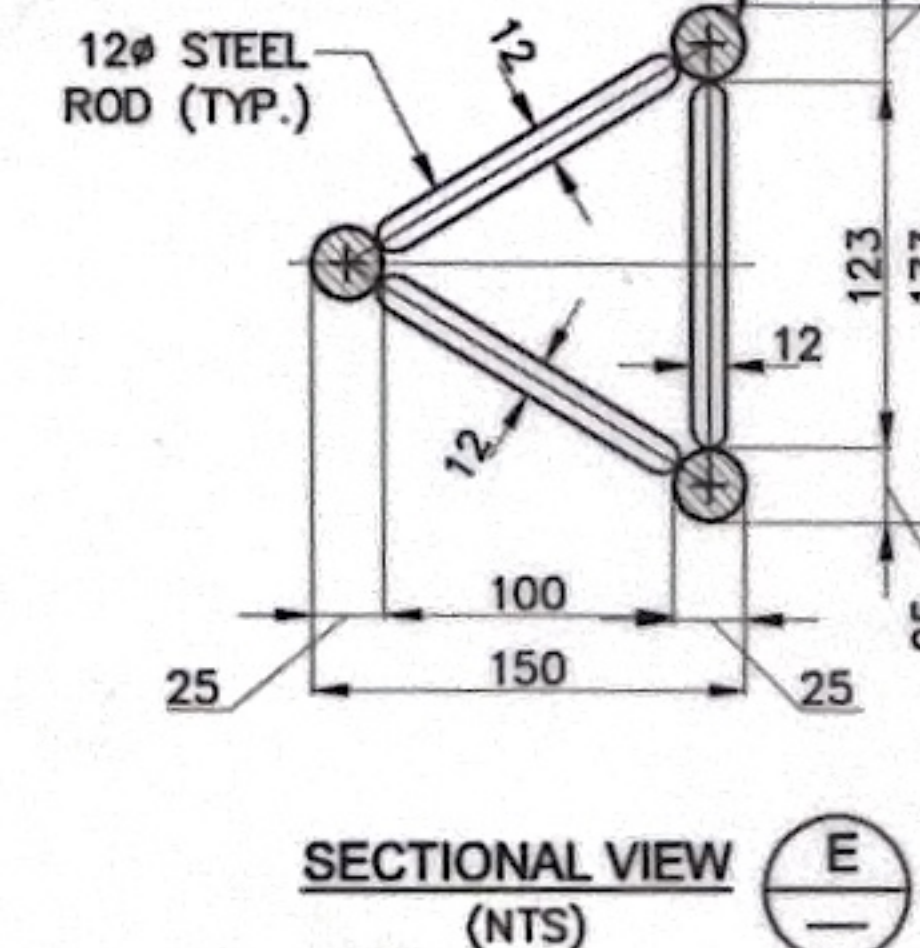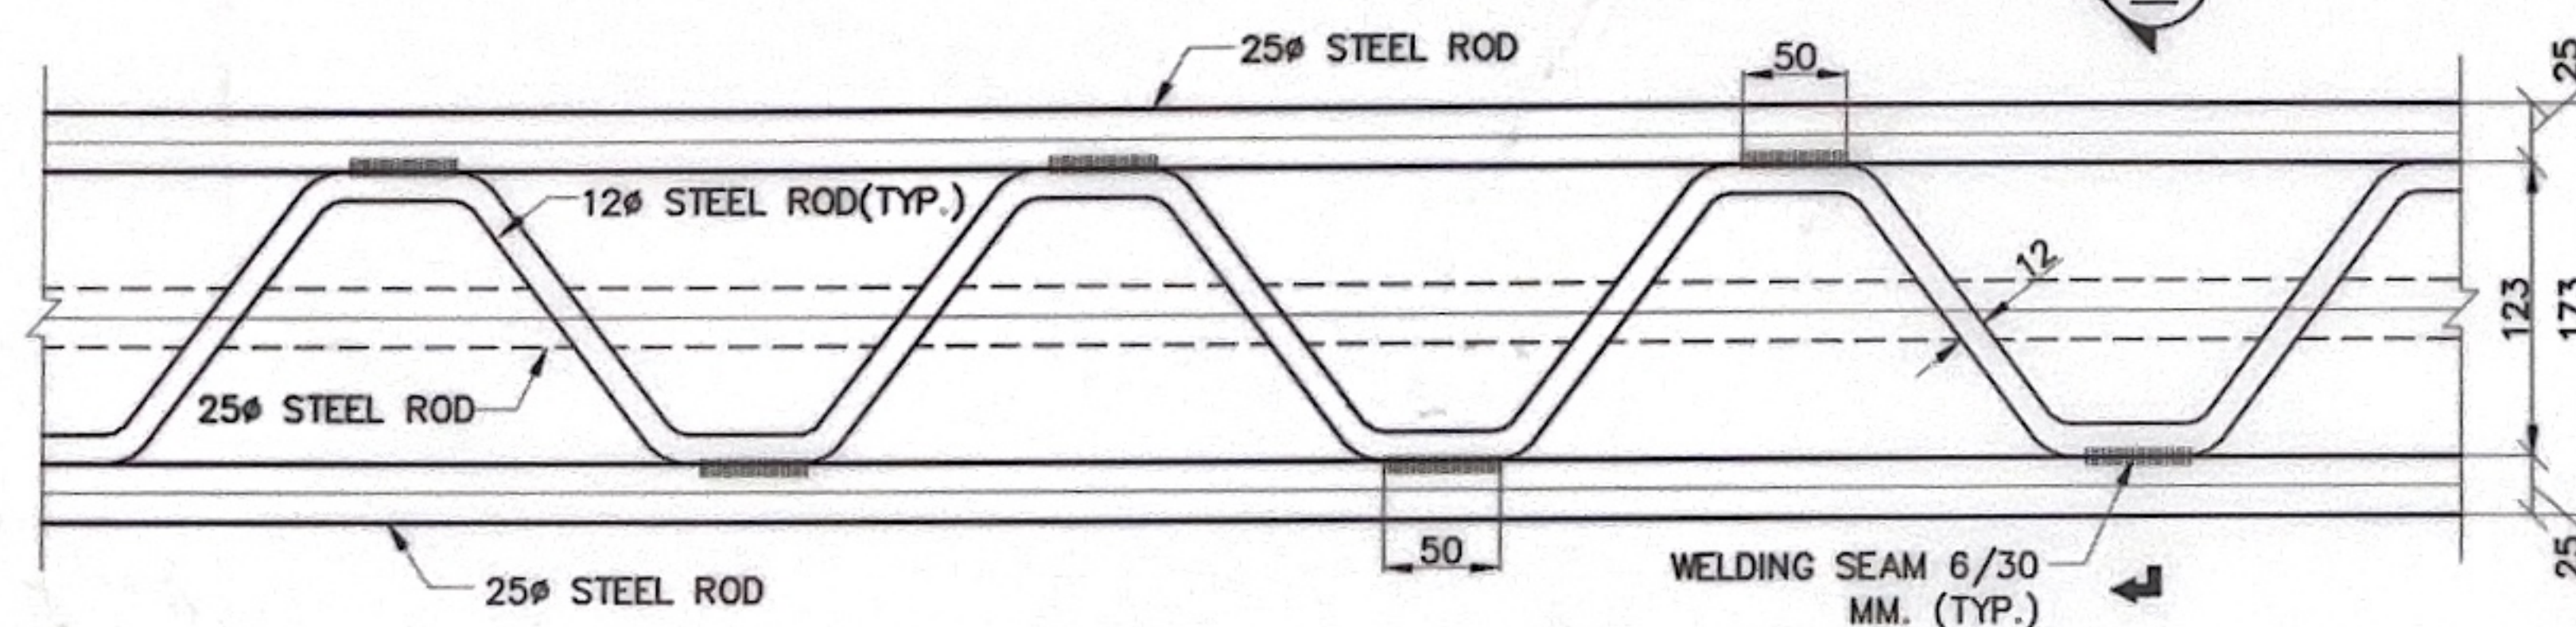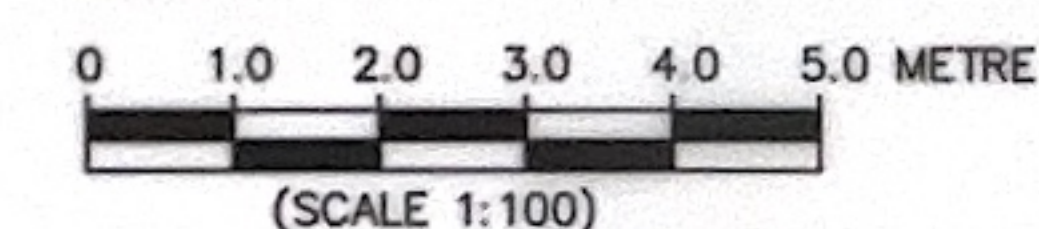

05.03.20	00	ISSUED FOR CONSTRUCTION	DATE	NO.	REVISION OR ISSUES	BY	CH. APP.	DATE	NO.	REVISION OR ISSUES	BY	CH. APP.	DATE	NO.	REVISION OR ISSUES	BY	CH. APP.
एन एच पी सी लिमिटेड
NHPC Limited
(A GOVT. OF INDIA UNDERTAKING)

दिवंग बहुउद्देशीय परियोजना
DIBANG MULTIPURPOSE PROJECT

TAIL RACE TUNNEL
LATTICE GIRDER - HEADING ZONE
DETAILS

DATE: MARCH 2026 DRG. NO.: NHDB 4DC4 41 DD 1012 00